


LEGENDE

- CHÉMINEMENT PMR LARGEUR MINI 120cm  
PENTE MAXI à 4%
- AIRE DE ROTATION PMR
- ESPACE DE MANŒUVRE DEVANT PORTE D'ENTRÉE
- DISTANCE ENTRE PLACE PMR ET ESPACE  
DE MANŒUVRE DEVANT PORTE D'ENTRÉE < A 30m

36 PLACES RÉGLEMENTAIRE SOIT 2 PLACES PMR (5% des places)  
4 PLACES PMR PROJÉTÉES

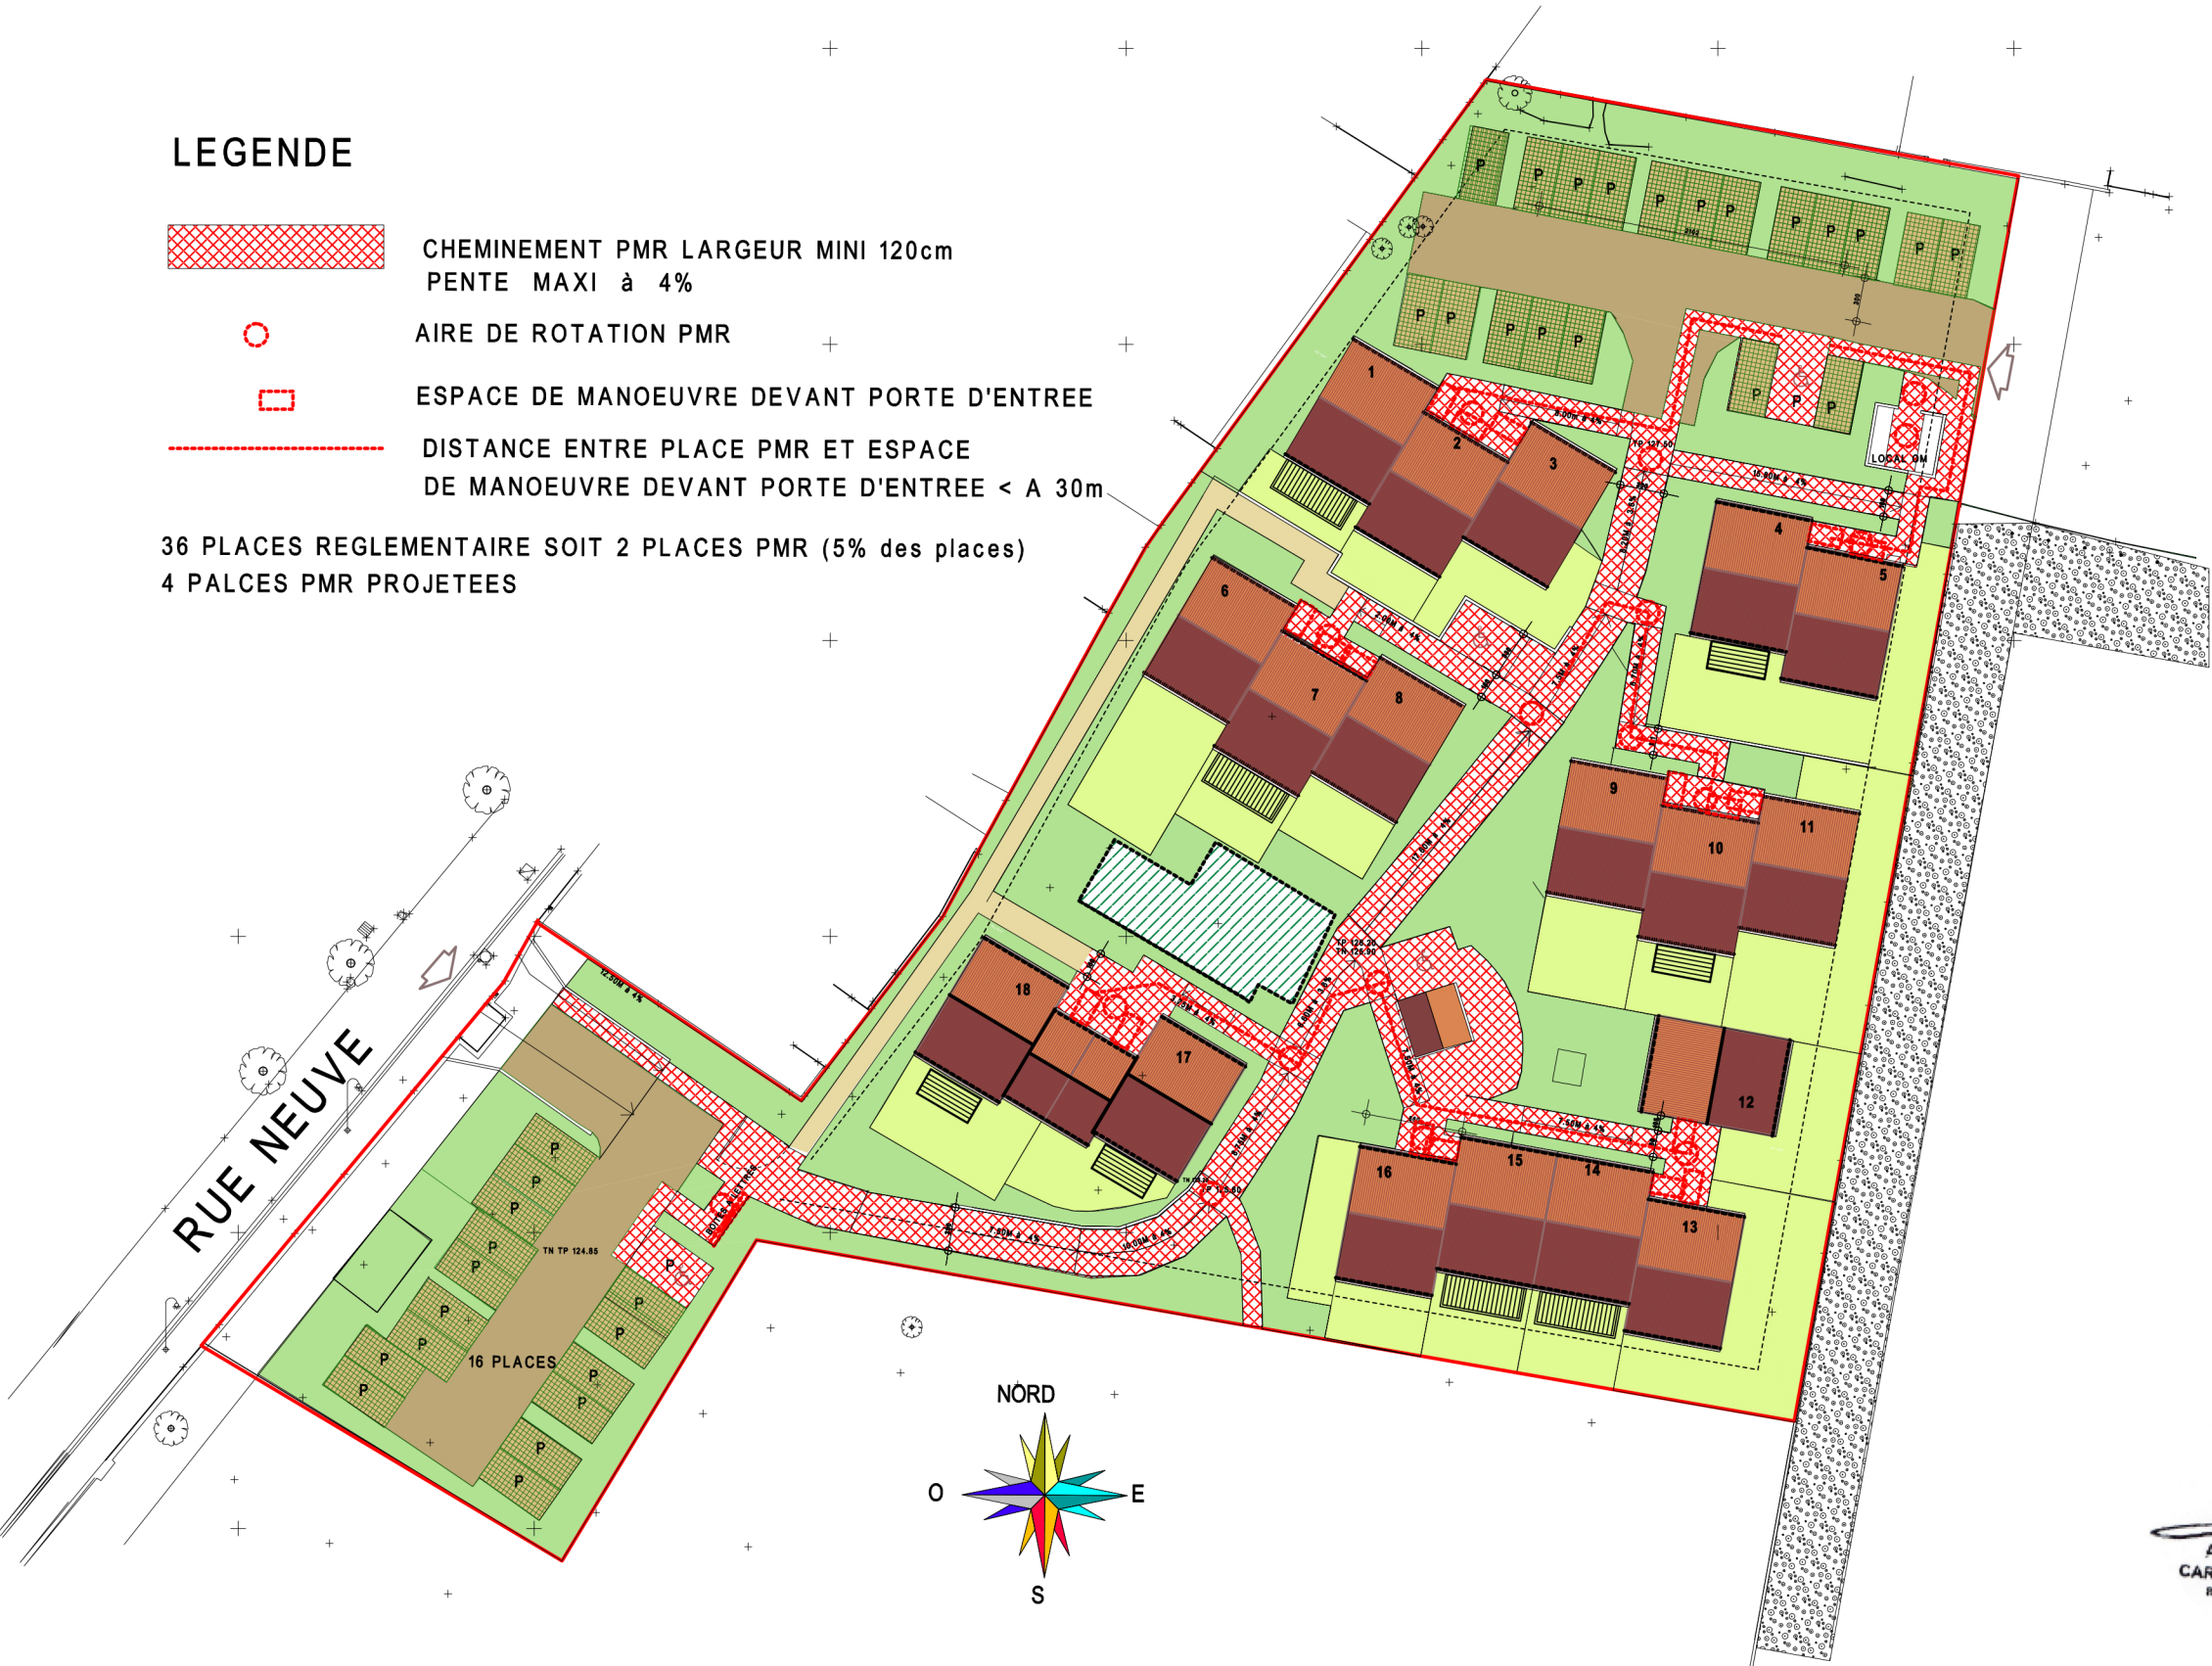

SCCV GRANDE TERRE  
837BIS ALLÉE DE PARIS  
83500 LA SEYNE-SUR-MER  
RCS TOULON 942743709

Anne Catherine  
CARNAZZA-VERNET  
Architecte d.p.l.g.

Michel CHAUVET  
Architecte D.P.L.G.  
40, rue Fargès 13008 MARSEILLE  
04 91 81 39 80  
06 16 17 21 48

ARCHITECTES

M. CHAUVET  
A.C. CARNAZZA  
ARCHITECTES D.P.L.G.  
Entrepreneurs Individuels  
40 Rue FARGES 13008 MARSEILLE  
ml.chauvet@wanadoo.fr  
ac.vernet13@gmail.com

MAÎTRE D'OUVRAGE

SCCV GRANDE TERRE  
(SIRET 942 743 709 R.C.S. Toulon)

DATE 12/06/2025

ÉCHELLE 1/500

OPÉRATION

RUE NEUVE GRAND TERRE  
13930 AUREILLE

TITRE DU PLAN

PLAN PMR

A.P.S.

P.C.

D.C.E.

MARCHES

Annexe  
3a