


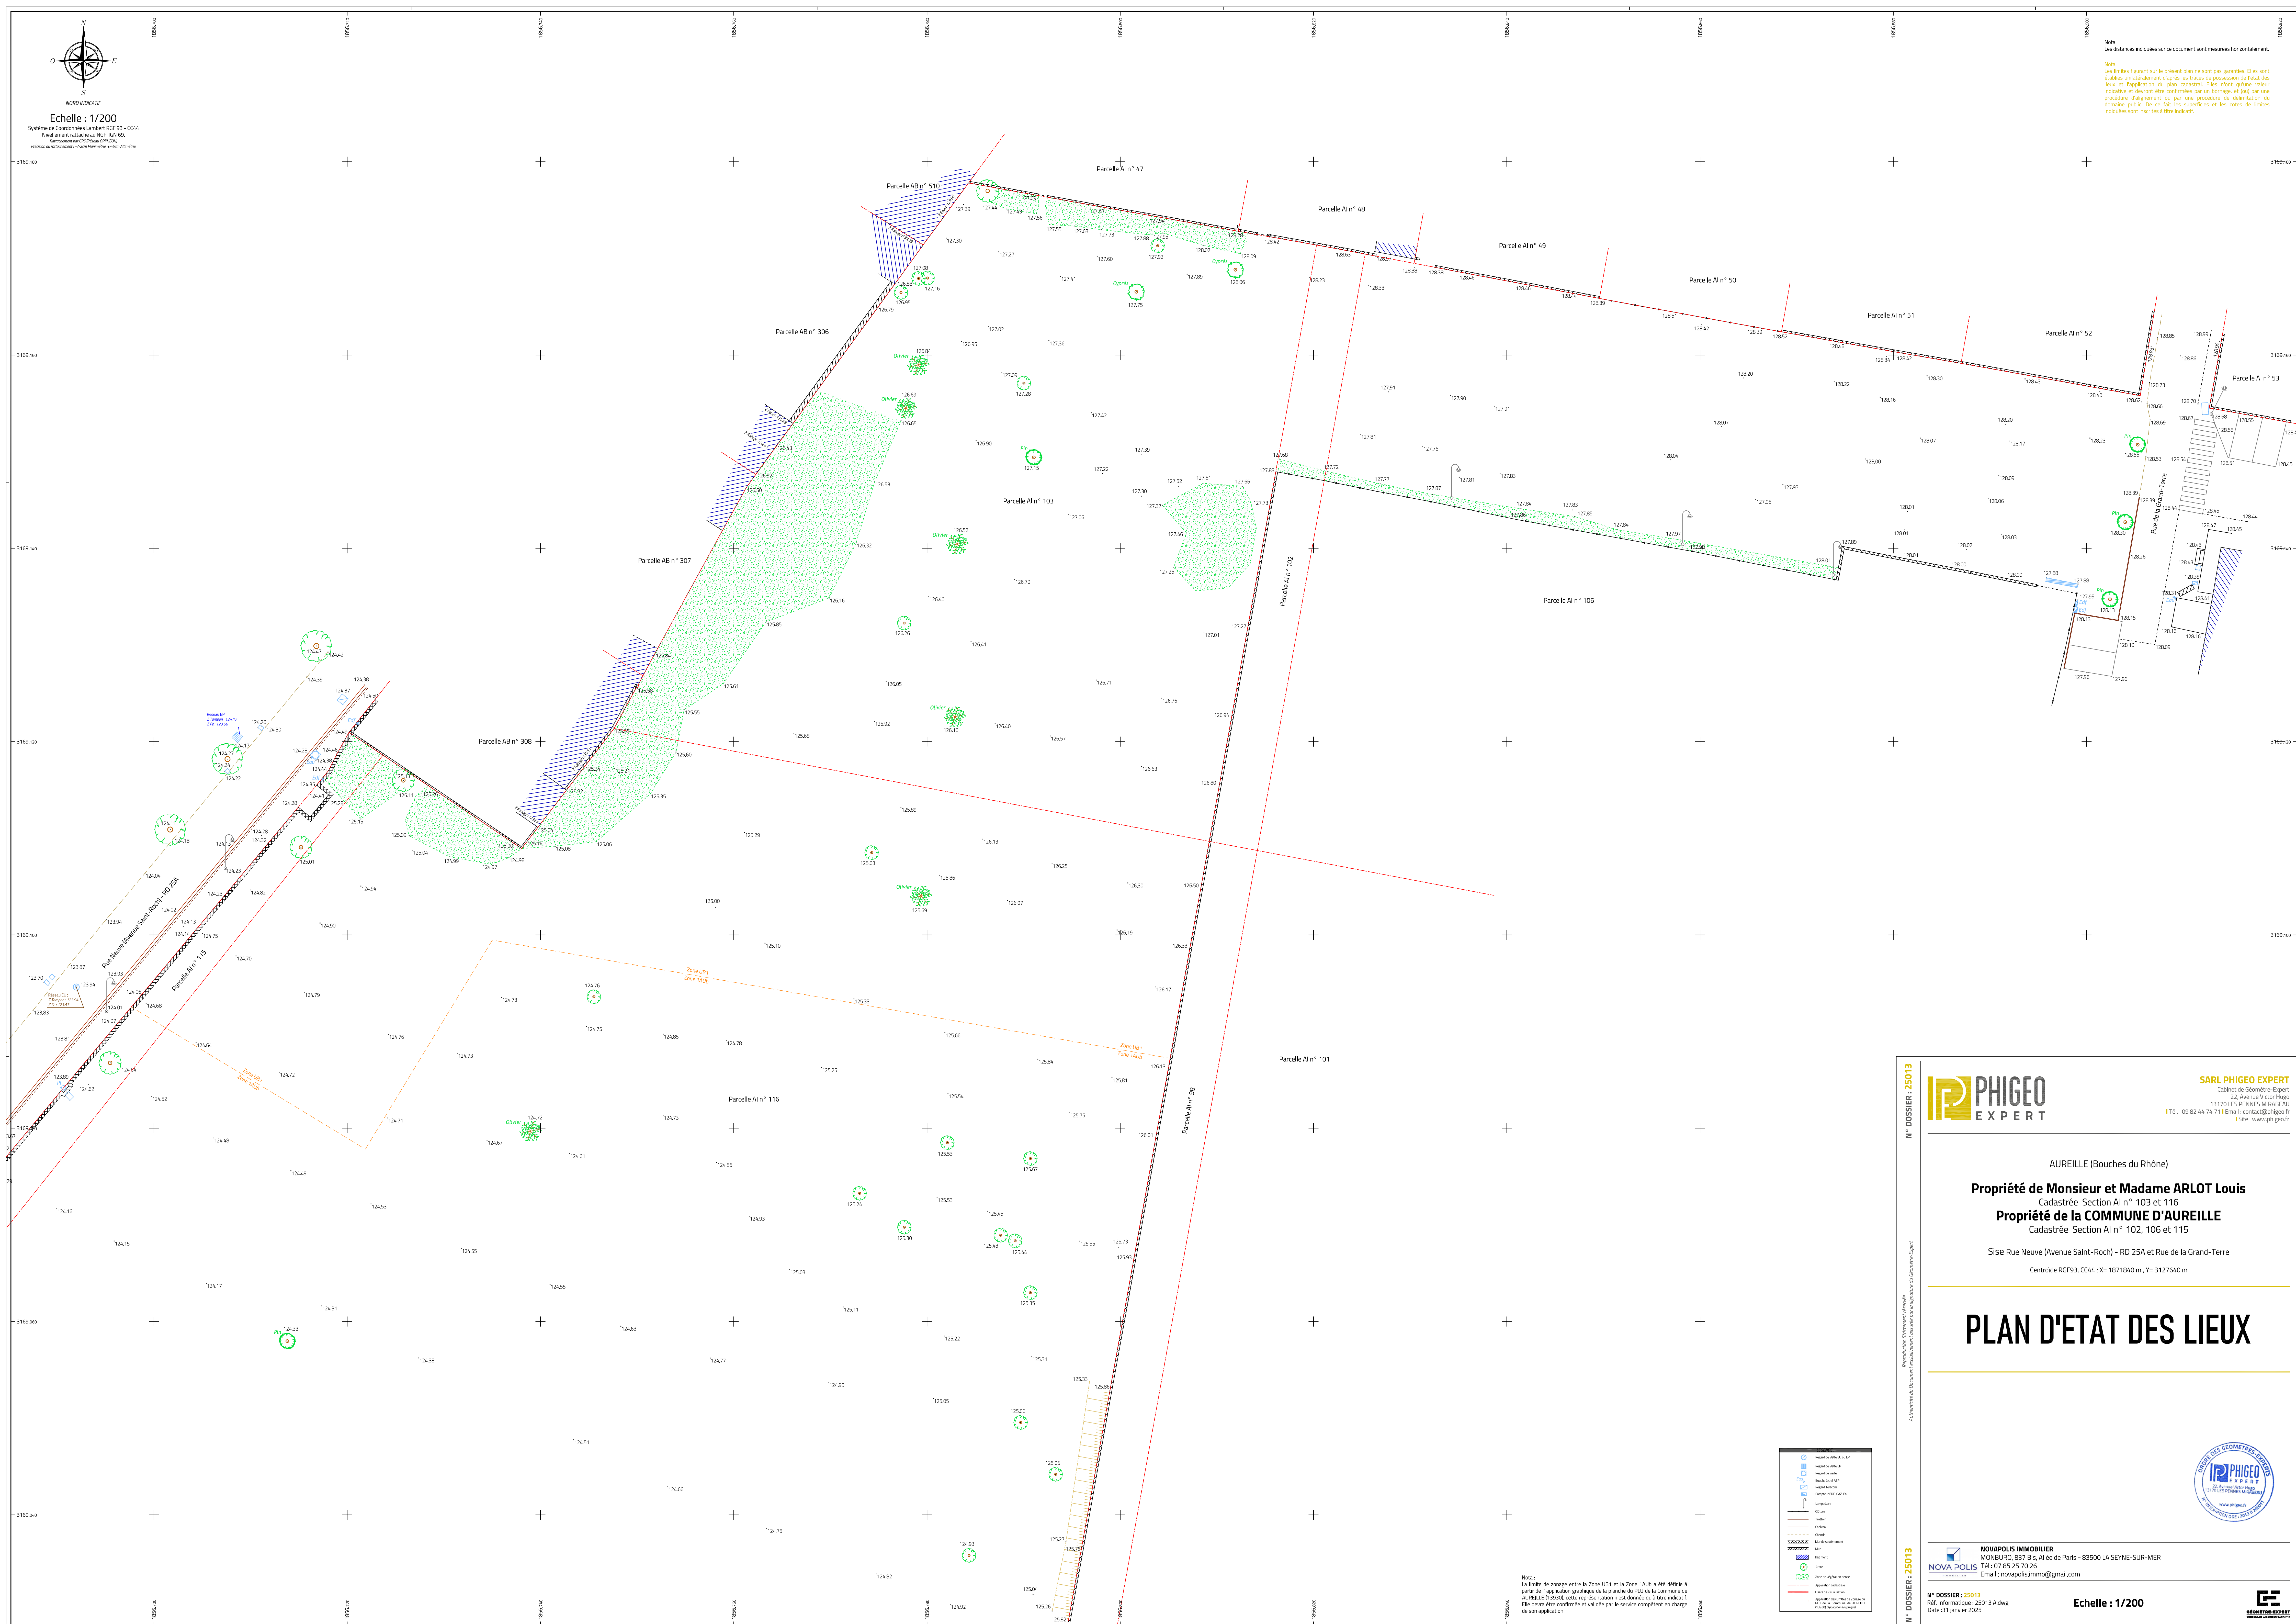

Nota:
Les distances indiquées sur ce document sont mesurées horizontalement.

Nota :
La limite de zonage entre la Zone UB1 et la Zone 1AUb a été définie à partir de l'application graphique de la planche du PLU de la Commune de AUREILLE (13930), cette représentation n'est donnée qu'à titre indicatif. Elle devra être confirmée et validée par le service compétent en charge de son application.

N° DOSSIER: 25013

N° DOSSIER: 25013



SARL PHIGEO EXPERT
Cabinet de Géomètre-Expert
22, Avenue Victor Hugo
13170 LES PENNES MIRABEAU
04 44 74 71 | Email : contact@phigeo.fr
| Site : www.phigeo.fr

AUREILLE (Bouches du Rhône)

Propriété de Monsieur et Madame ARLOT Louis
Cadastrée Section Al n° 103 et 116

Propriété de la COMMUNE D'AUREILLE
Cadastrée Section Al n° 102, 106 et 115

SISE Rue Neuve (Avenue Saint-Roch) - RD 25A et Rue de la Grand-Terre

Centroides RG93, C(C4): Xc= 1871840 m, Yc= 3127640 m

PLAN D'ETAT DES LIEUX

 NOVAPOLIS IMMOBILIER
MONBURE, 837 Bis, Aliée de Paris - 83500 LA SEYNE-SUR-MER
Tél : 07 85 25 70 26
Email : novapolisimmo@gmail.com

N° DOSSIER : 25013
Réf. Informatique : 25013 A.dwg
Date : 31 janvier 2025

Echelle : 1/200

CENTRE-EXPERT