




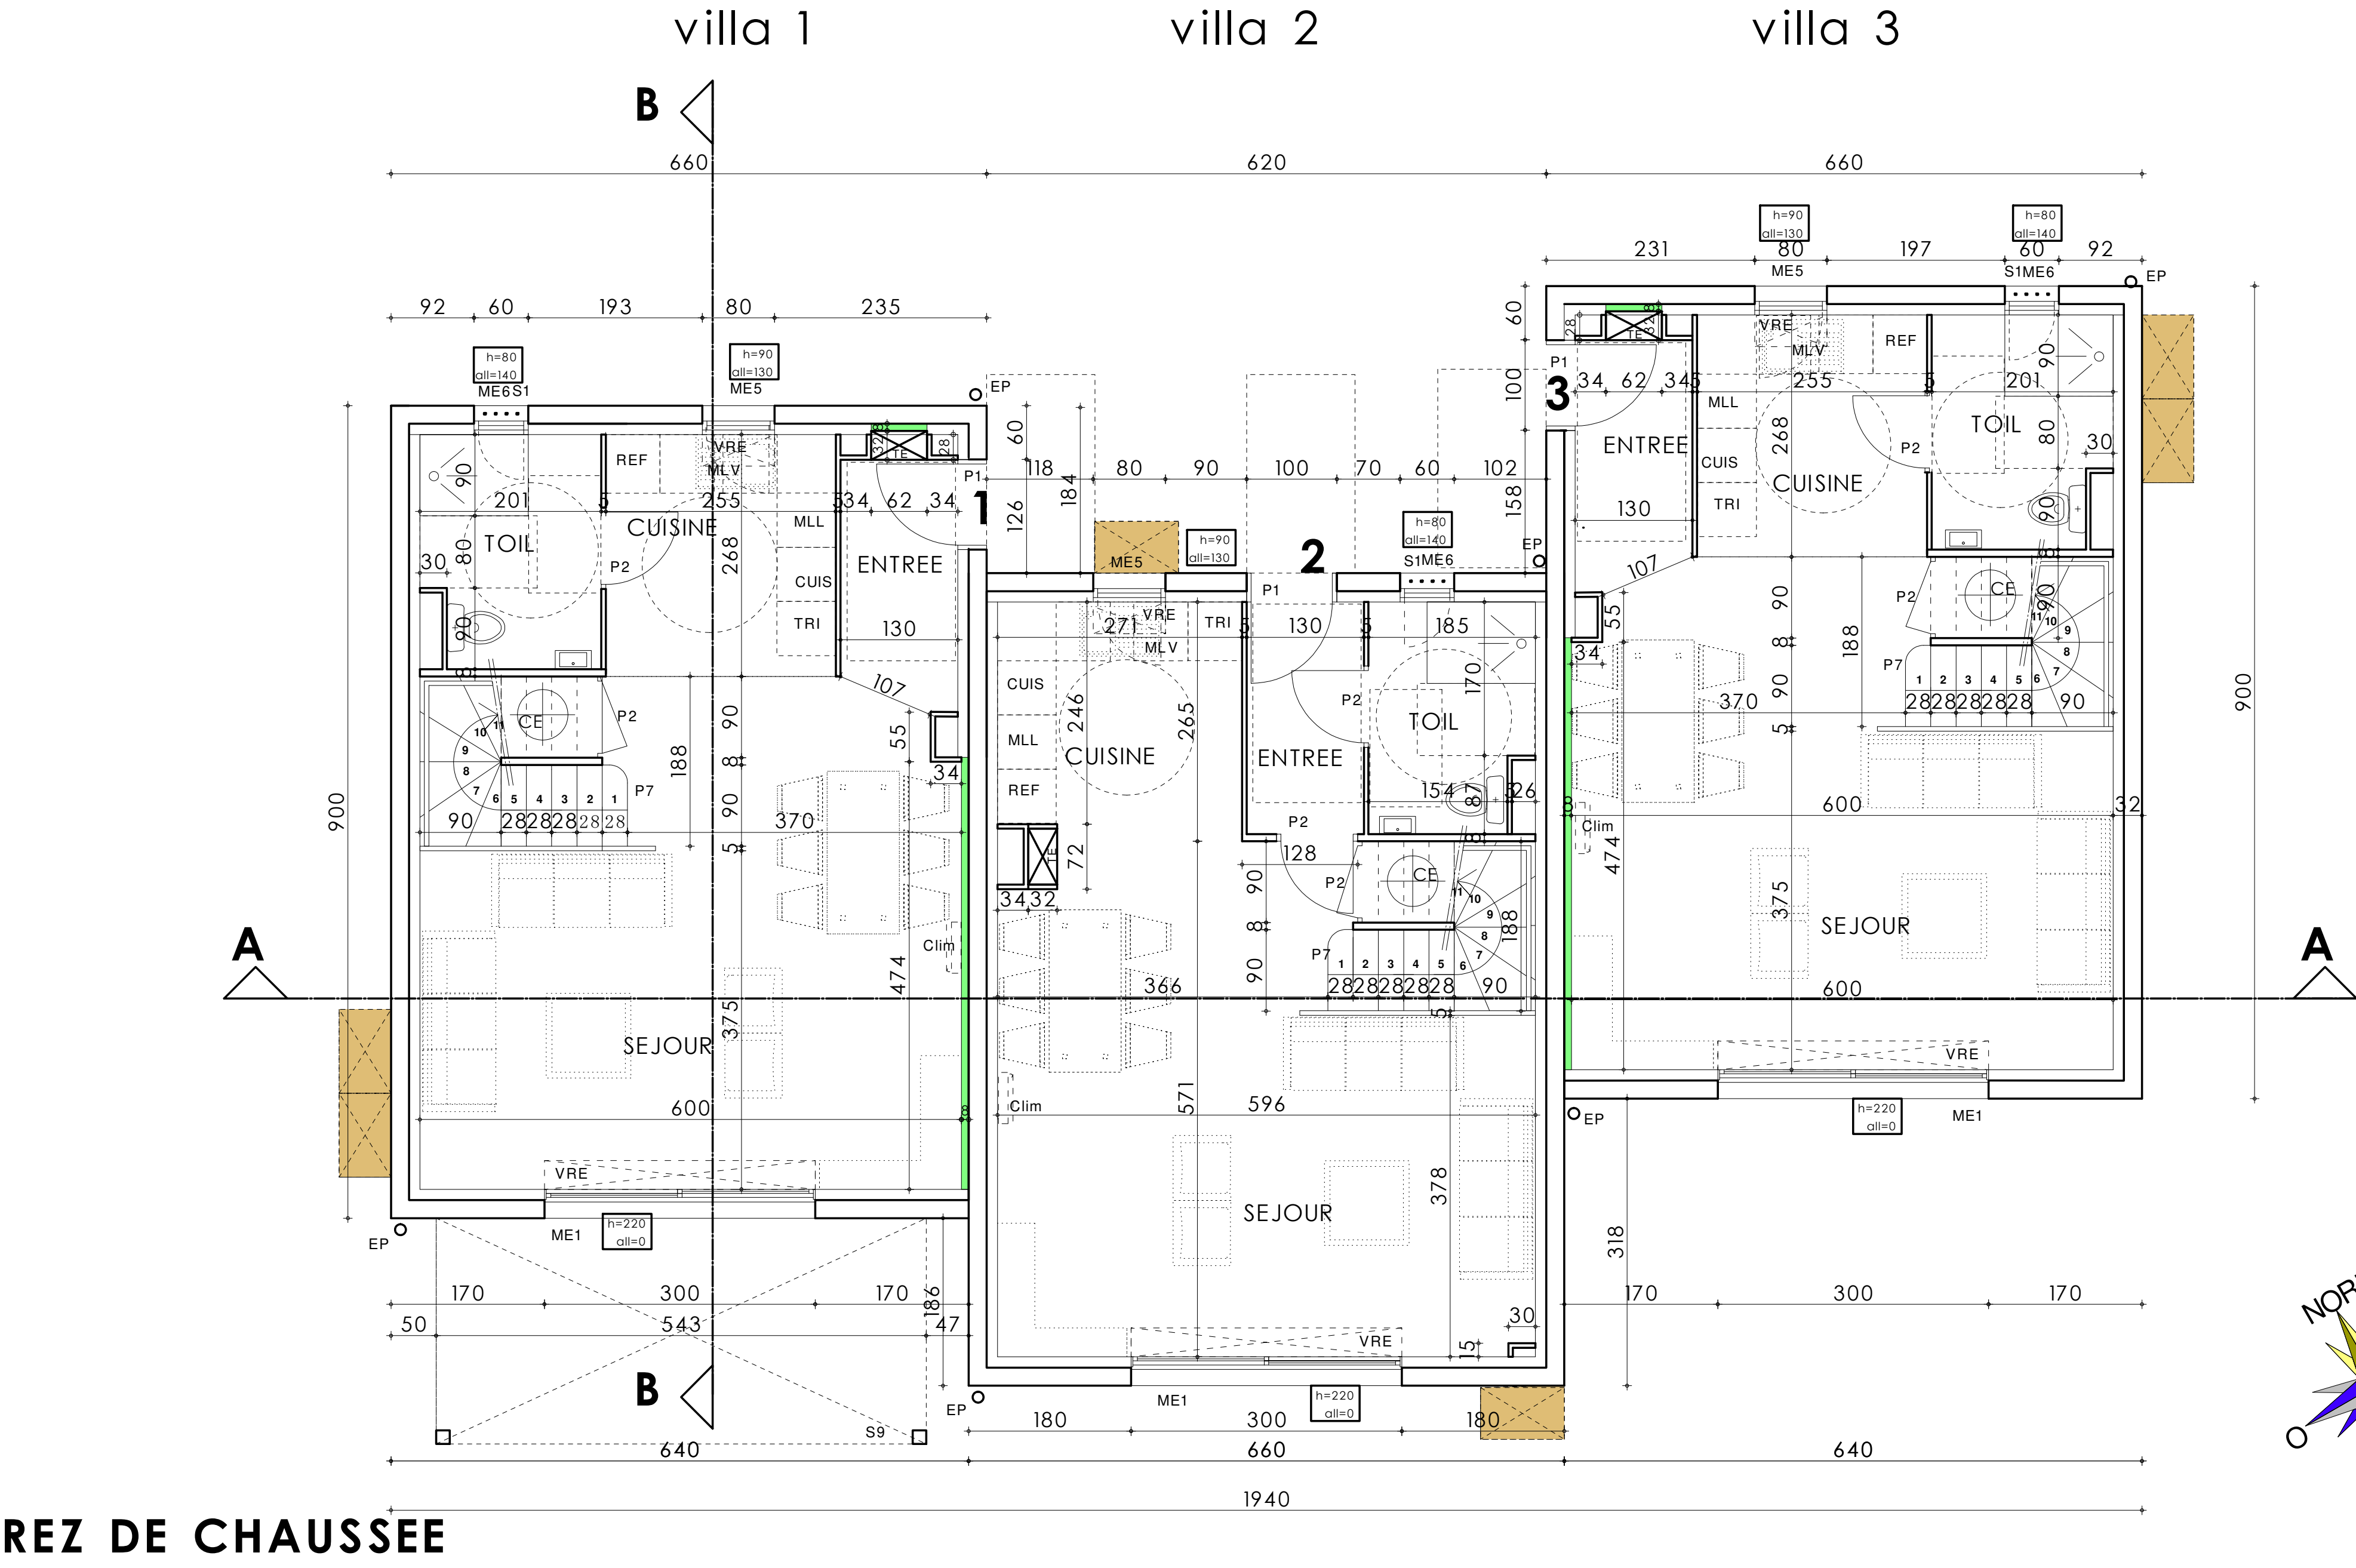


REZ DE CHAUSSEE

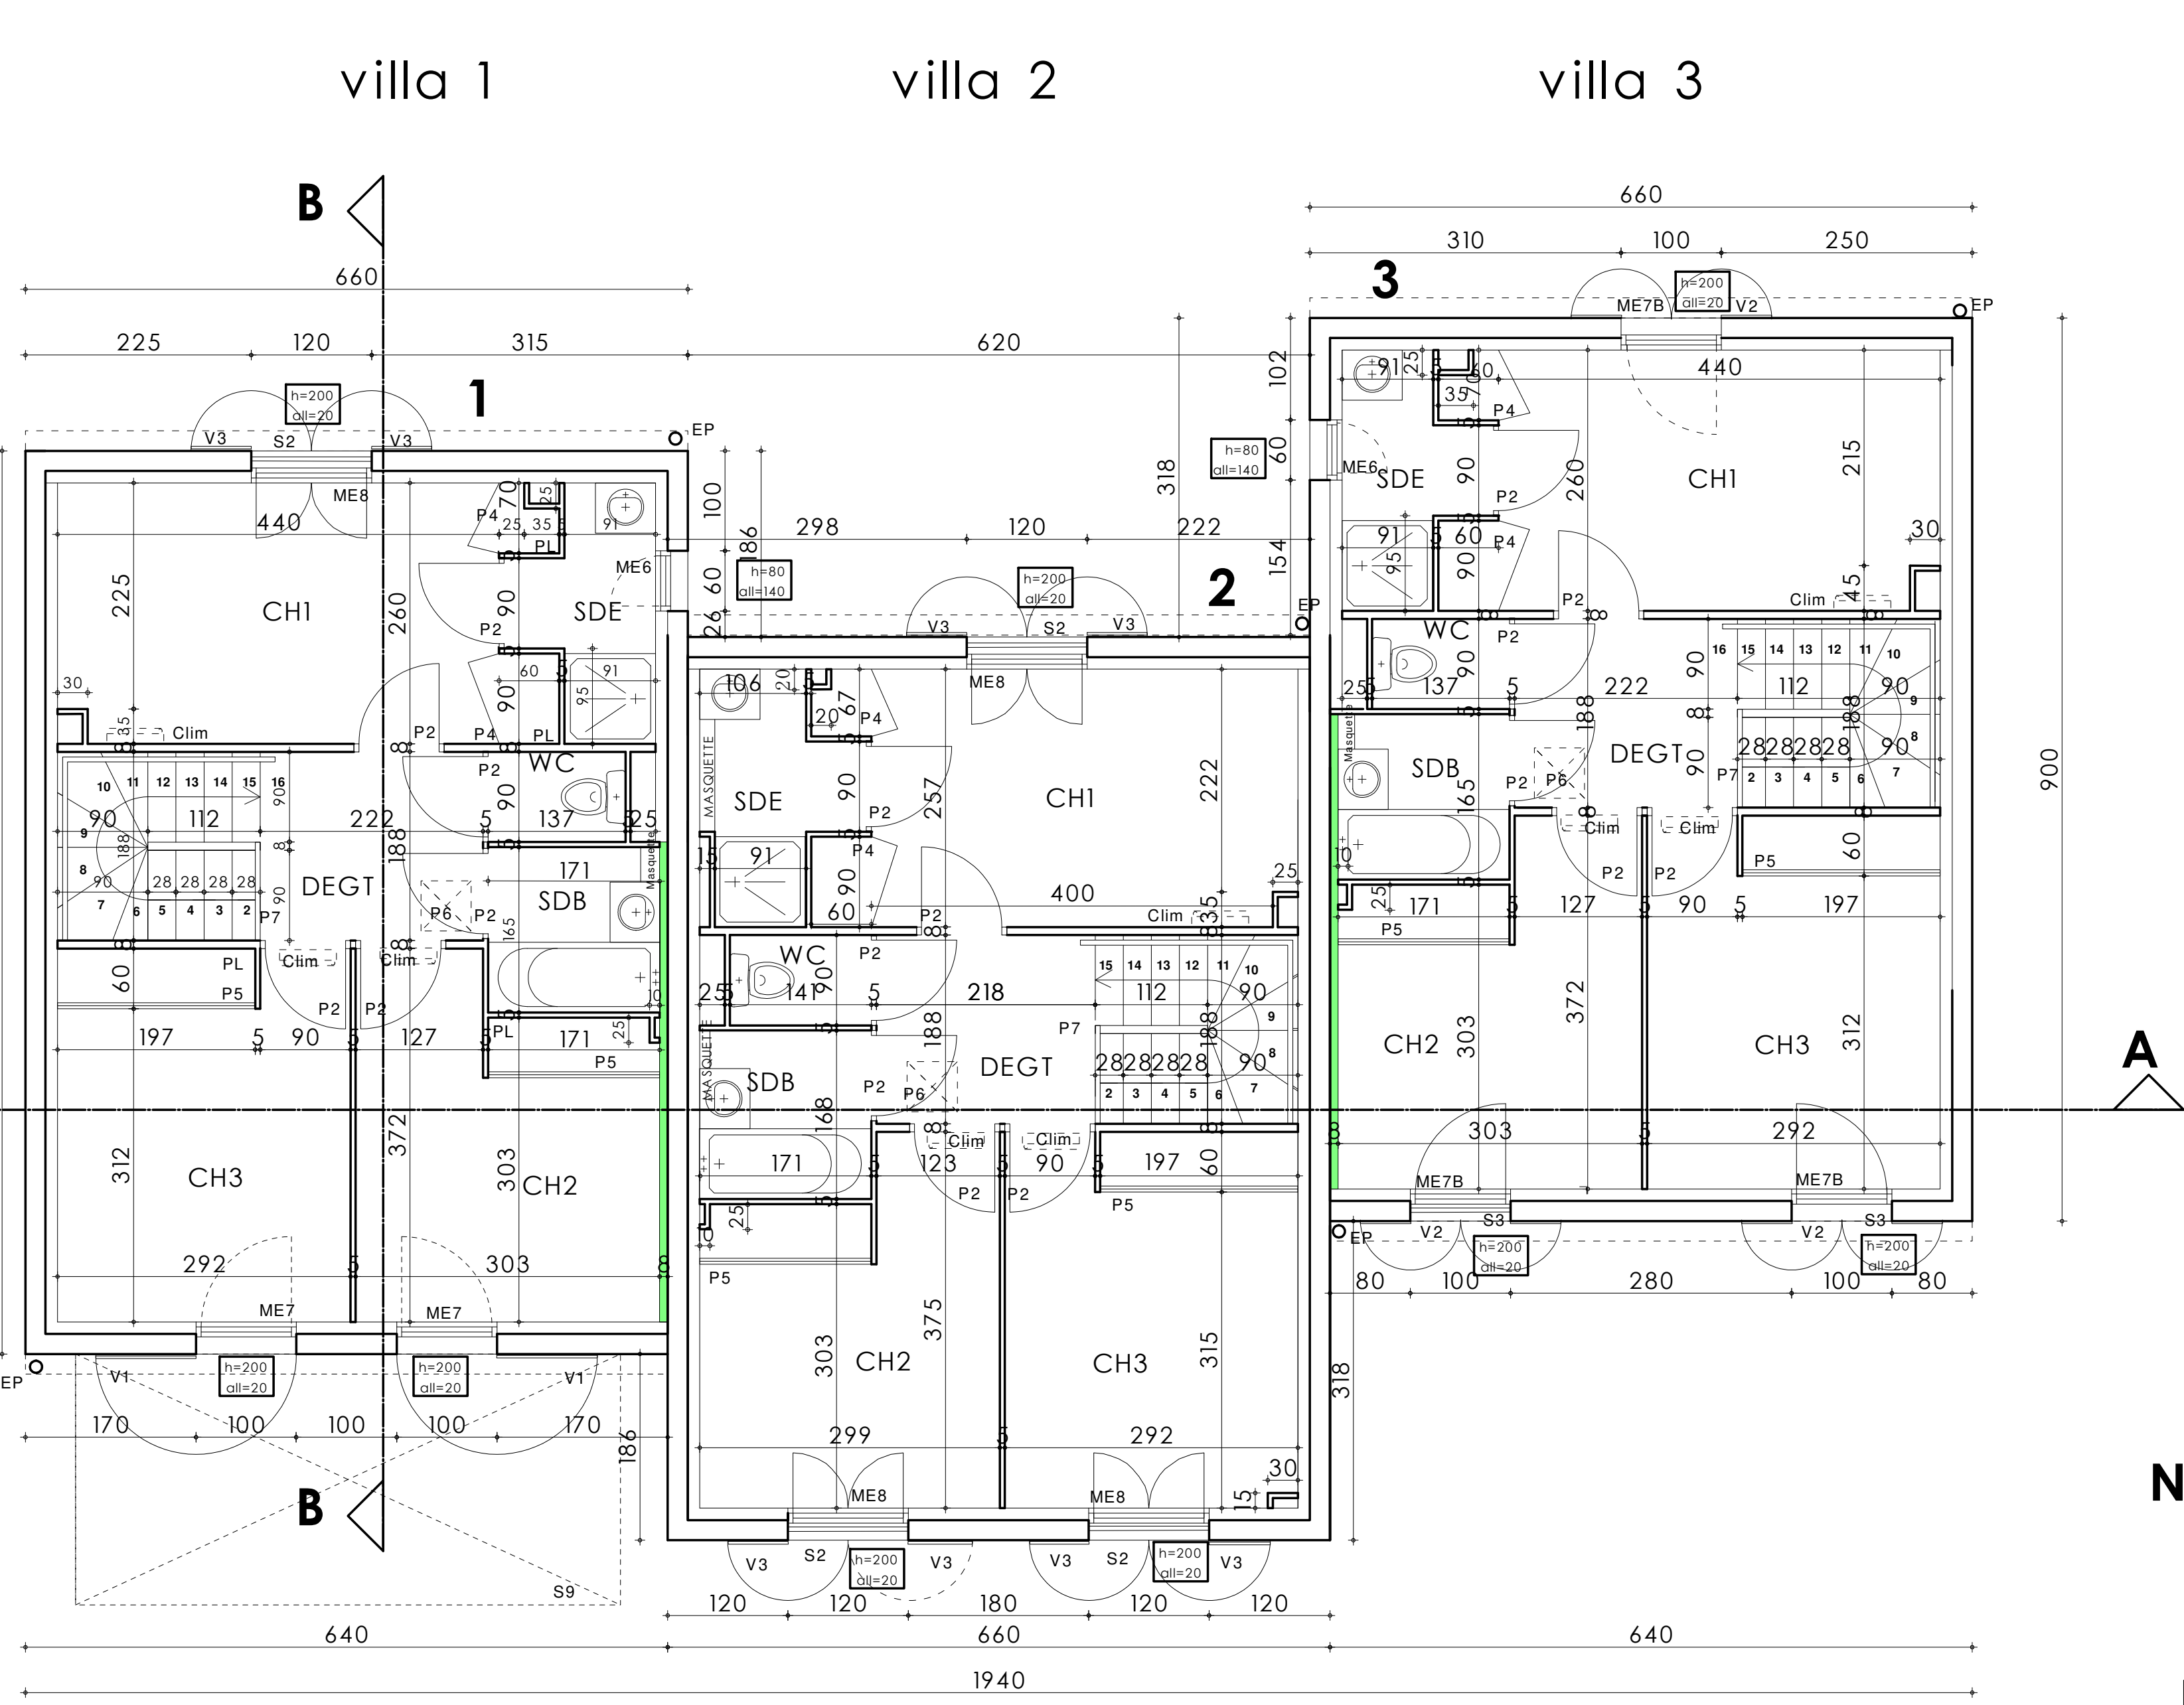

NIVEAU 1





PLAN DE NIVEAU 1/50

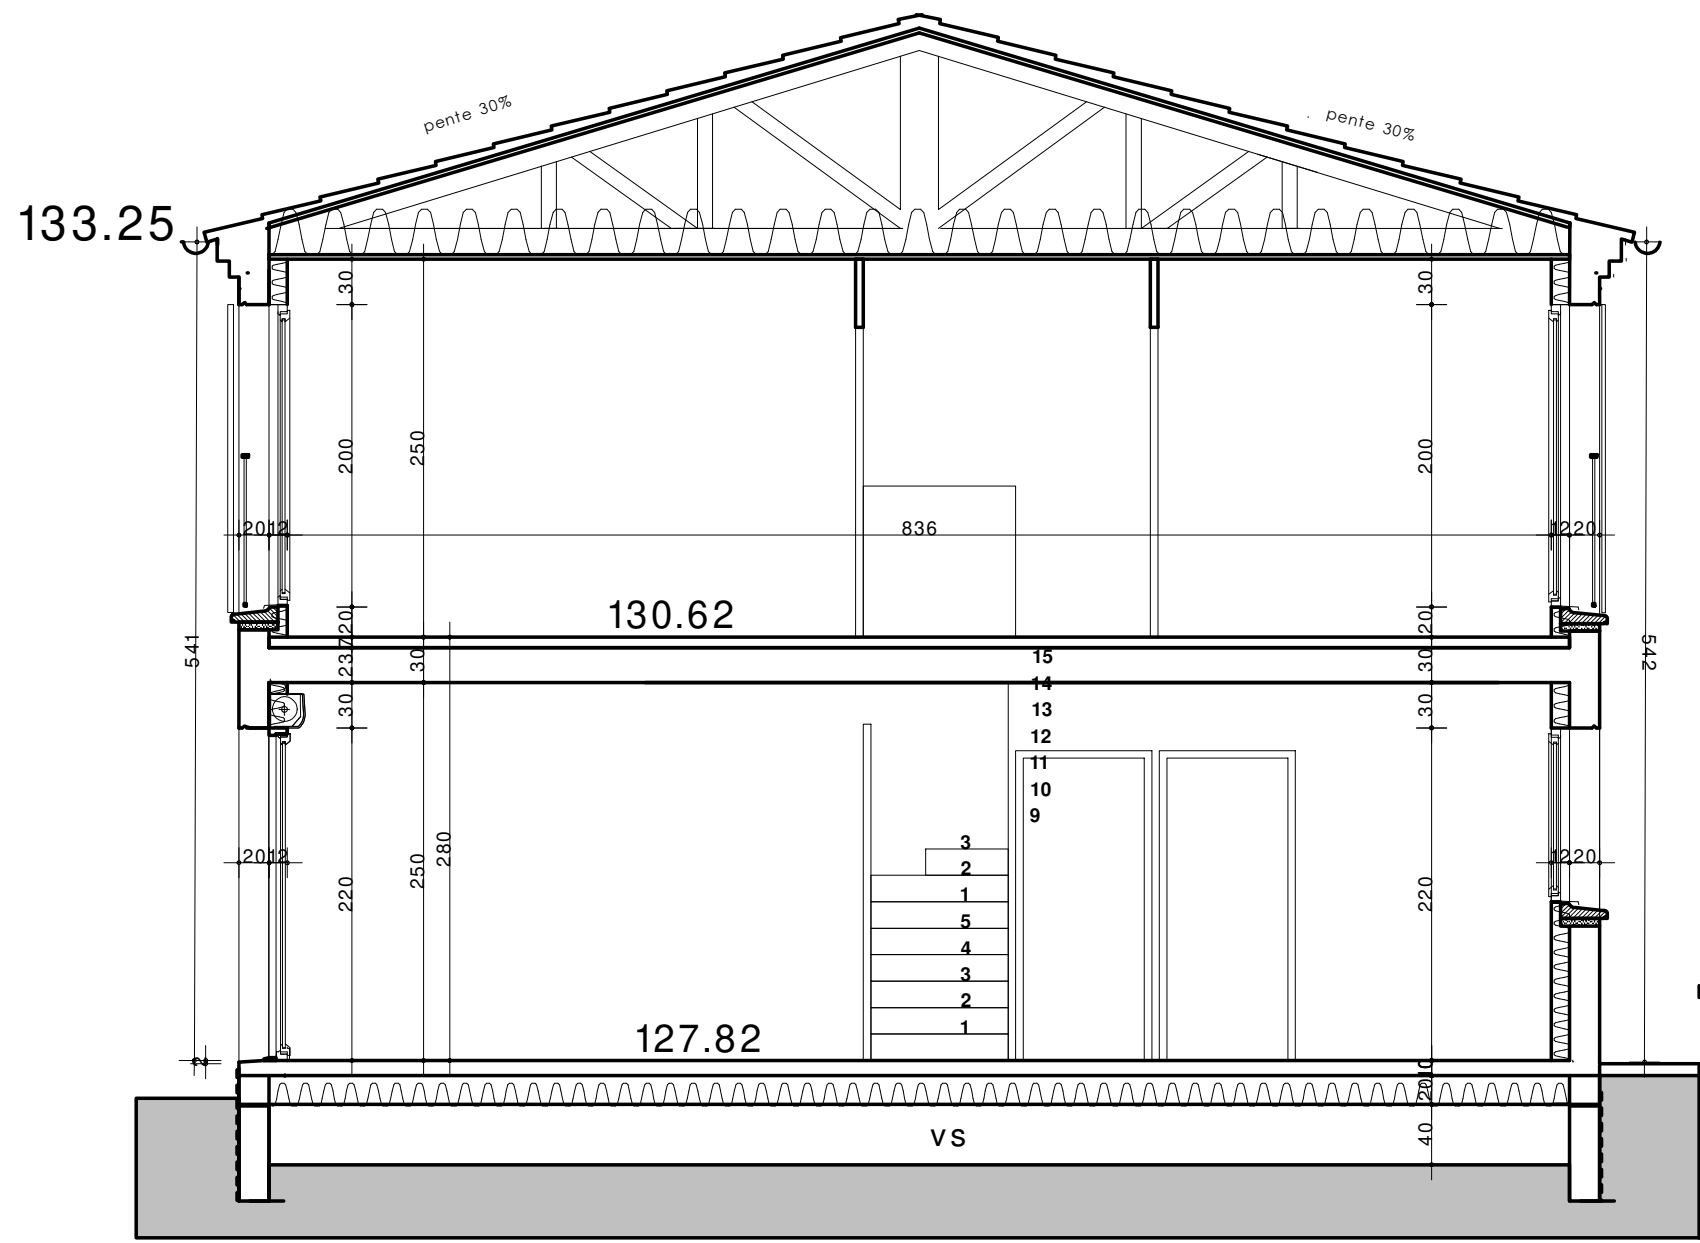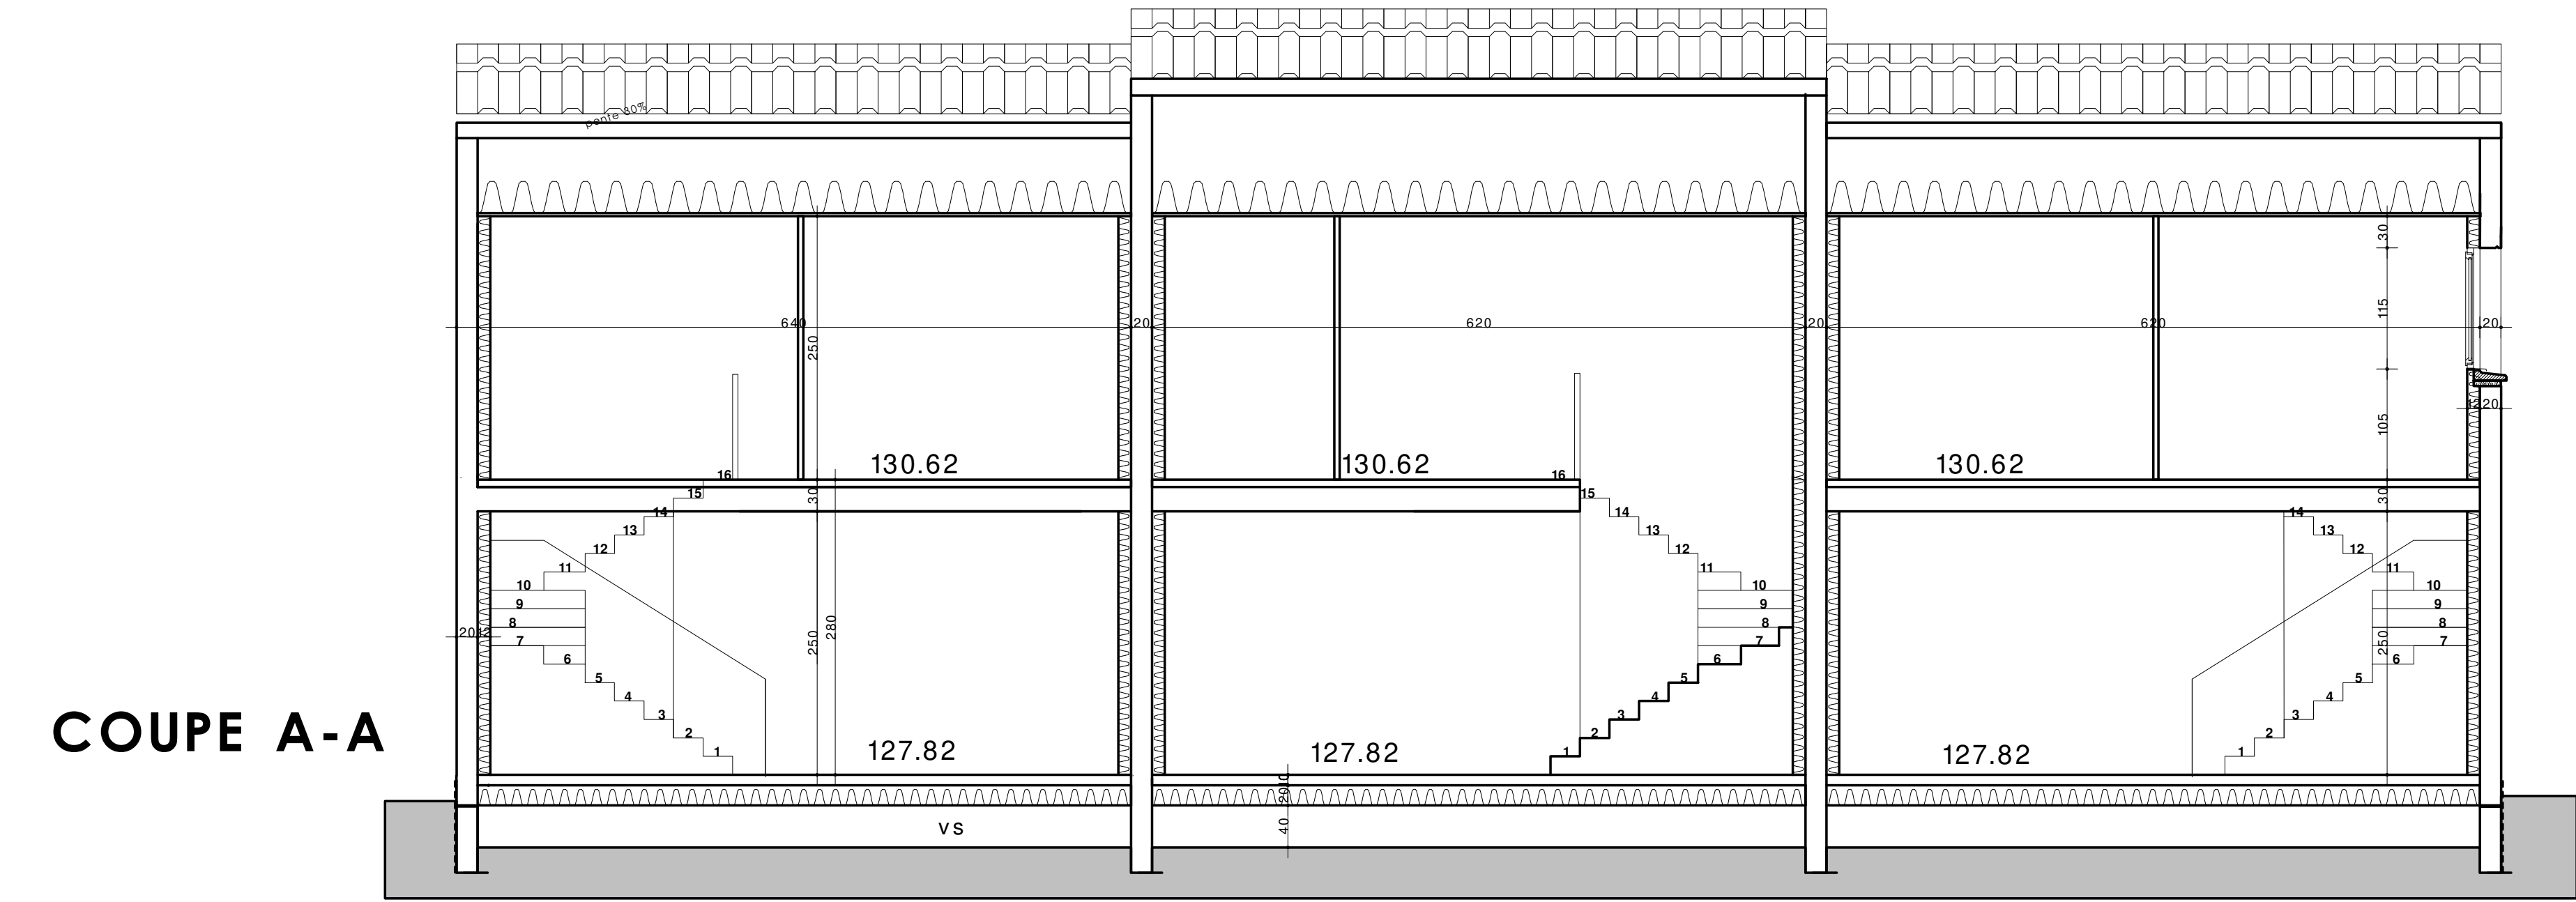

LEGENDE

- Coffre volet roulant
- Faux plafond
- Espace de manoeuvre 220X120 devant la porte d'entrée
- Espace de manoeuvre 80X130 sanitaire
- Aire de rotation PMR
- GTL cf détail technique
- Isolant acoustique
- Cache de l'unité extérieure de climatisation

COUPES 1/50

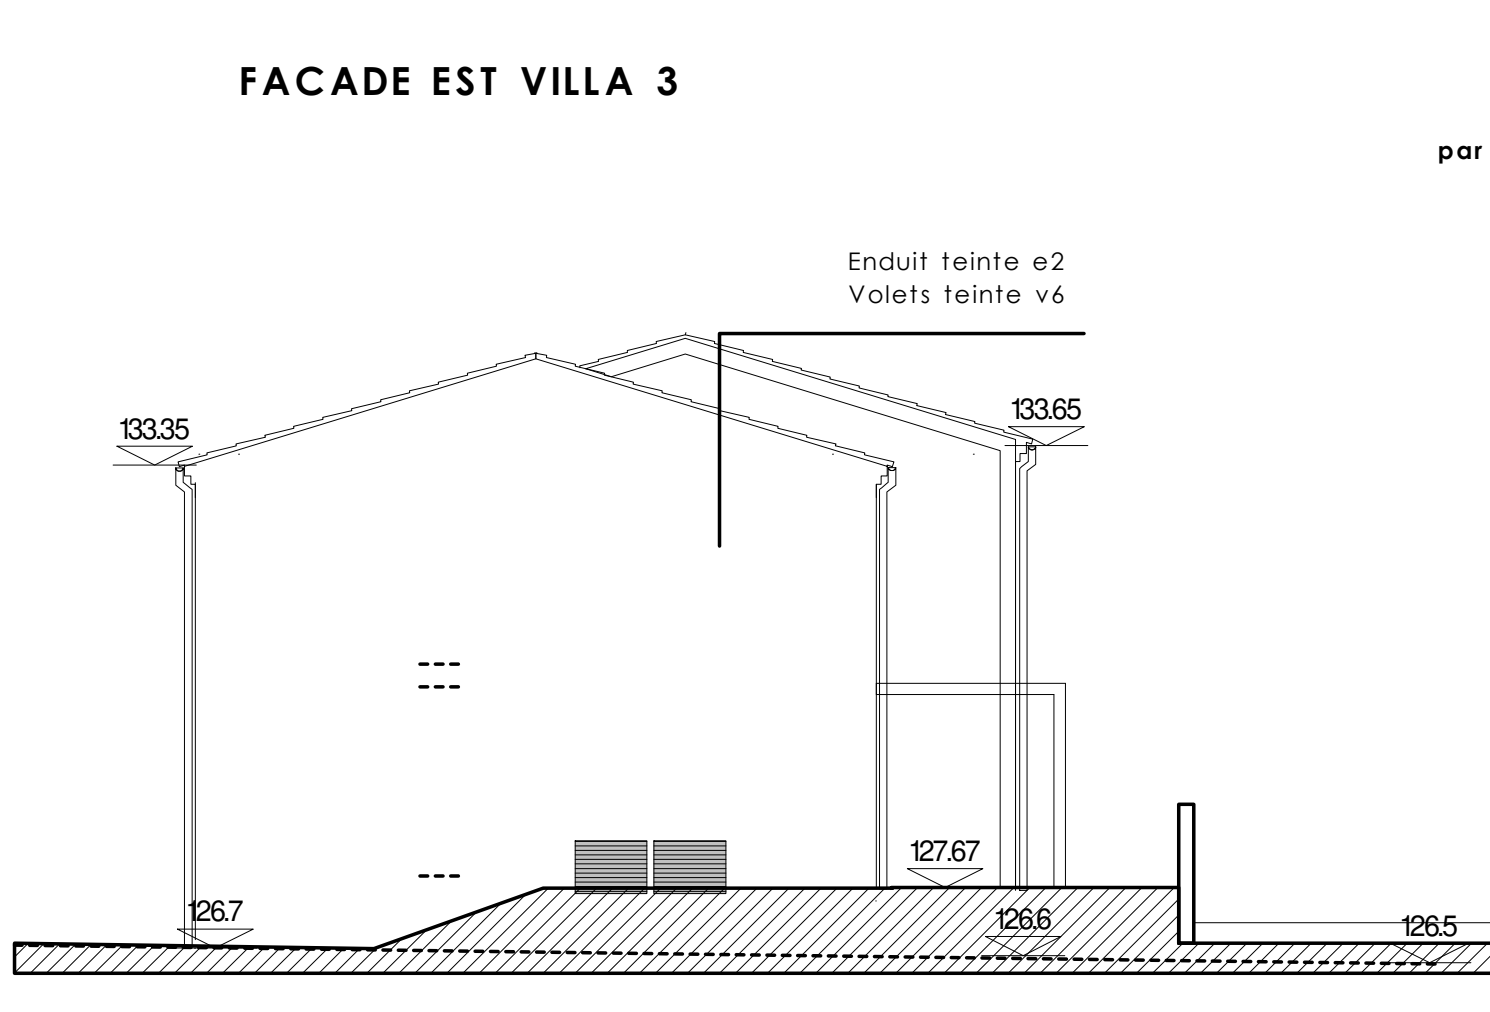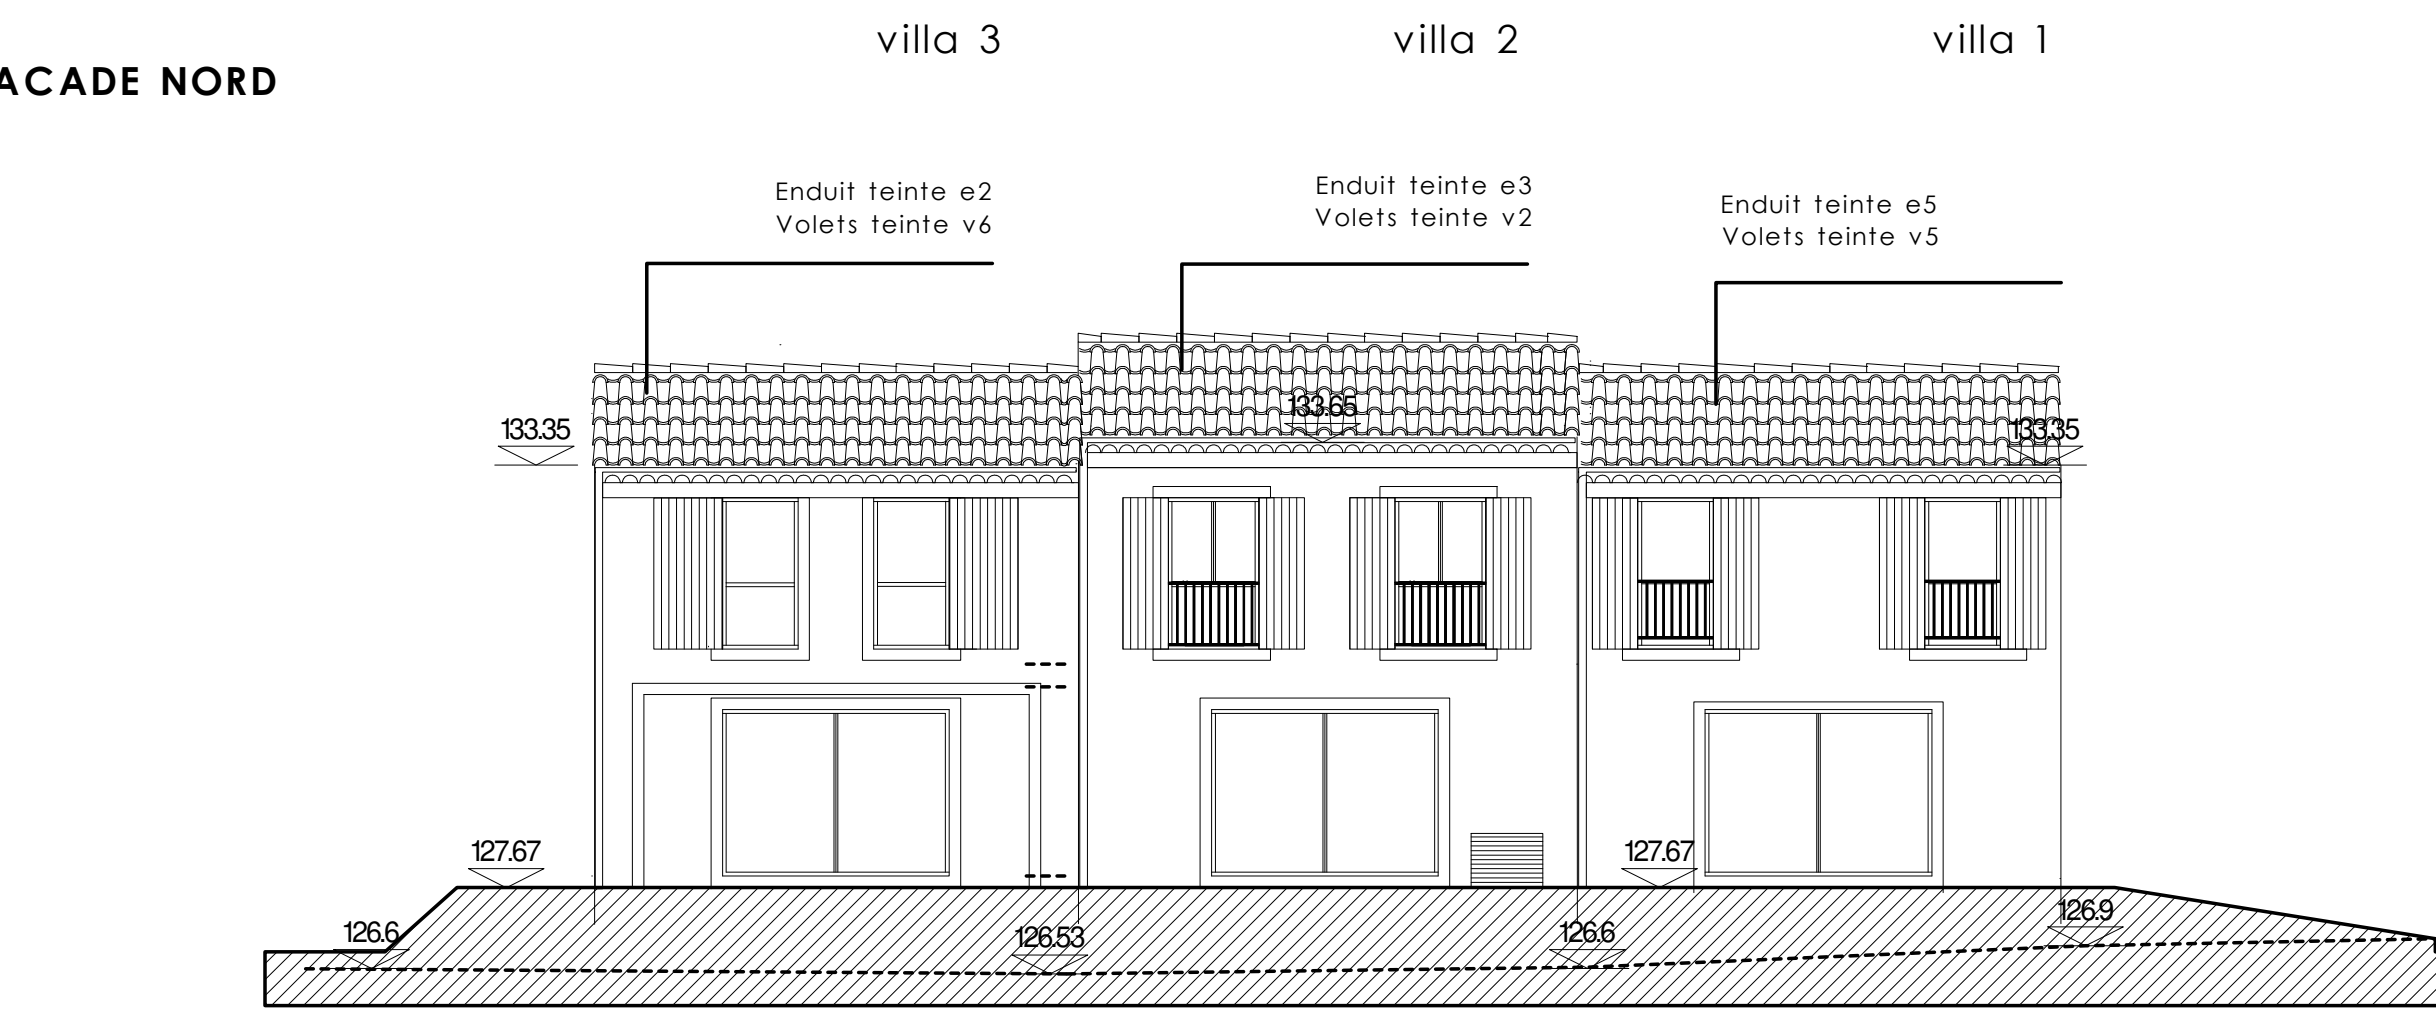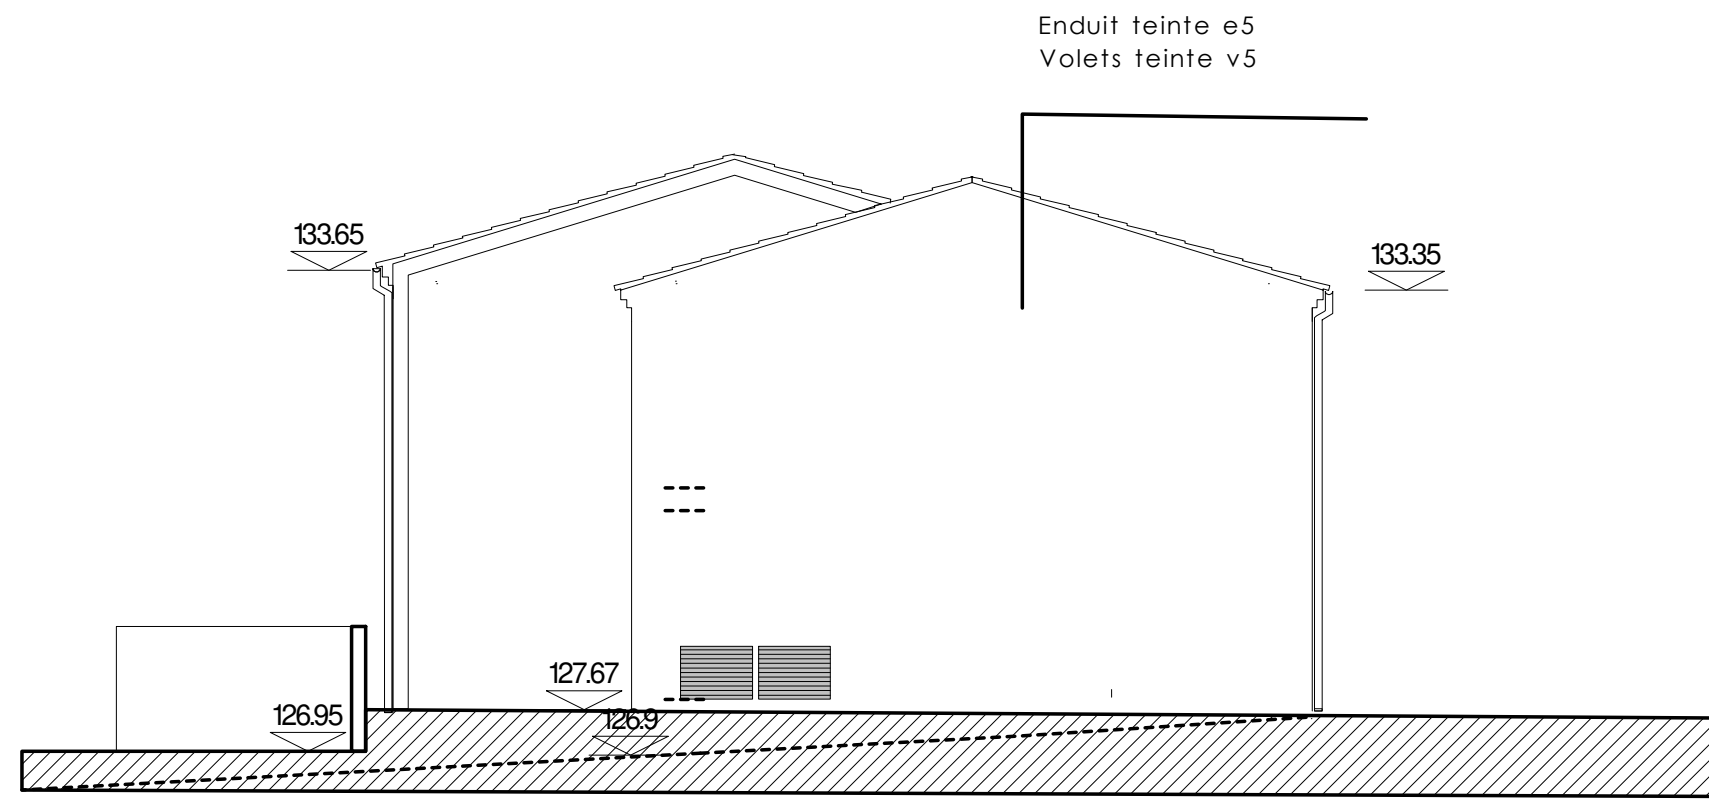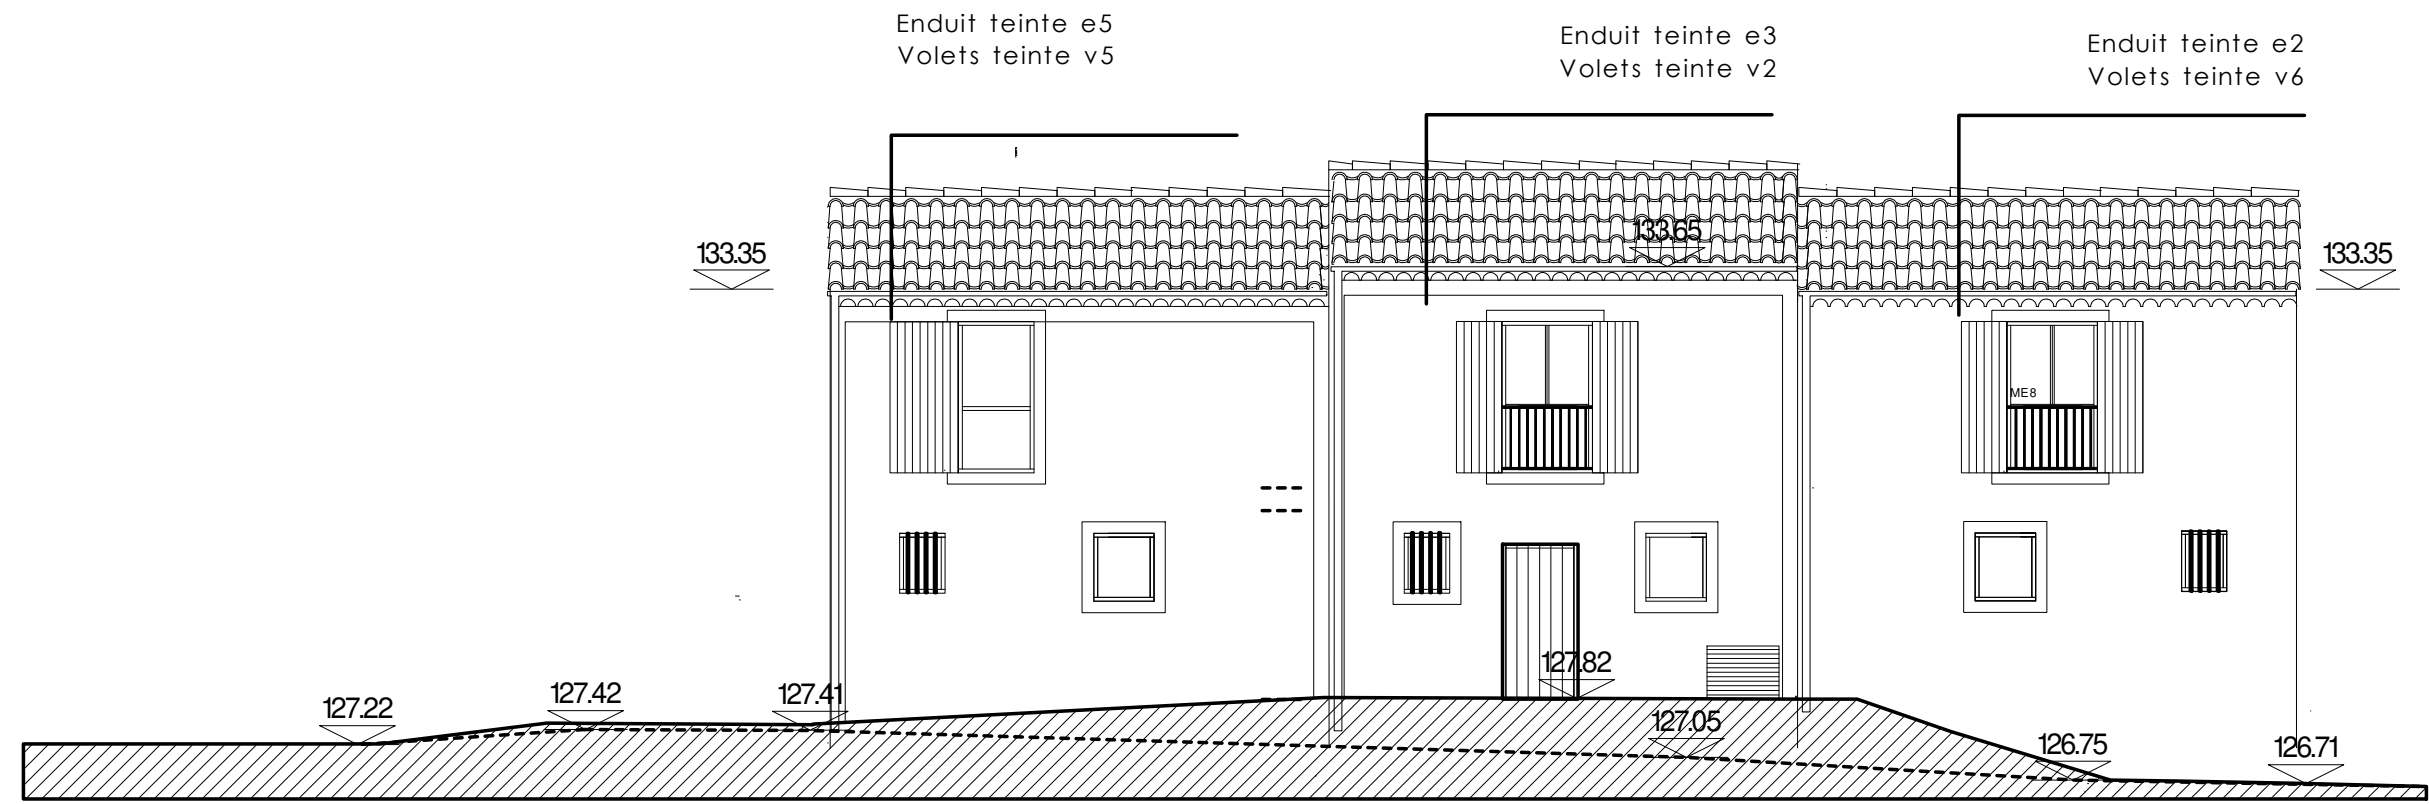

Les couleurs d'Aureille

En référence aux nuances de teintes recommandées par le CAUE 13 ainsi qu'à l'OAP et au cahier de recommandations architecturales urbaines et paysagères

Couvertures en tuile canal

Volets bois et portes d'entrée en bois

Gardes corps en serrurerie

Gouttières et chutes en zinc

Volets roulants pour les baies du rd

Grilles en serrurerie noire pour les ouvertures des sdb

FACADES /100

GRANDE TERRE			
INDICE	DATE	MODIFICATIONS	
A	15/06/2026	MODIFICATIONS SUITE REUNION DCE	
B	29/06/2026	SUPPRESSION LAVE MAIN DANS LES VILLAS COURTS MAÎTRISES	
C	06/07/2026	MODIFICATION TE ET IOLANT ACOUSTIQUE	
D			
E			
F			
G			
H			
I			
J			
K			
L			

ARCHITECTES M. CHAUVET A.C. CARRAZZA ARCHITECTES D.P.L.G. ENTREPRENEURS INDIVIDUELS 40 rue FARGES 13008 MARSEILLE michaels@orange.fr ac.carrazza@gmail.com		SCCV GRANDE TERRE (SIRET 942 743 709 R.C.S. Toulouse)		DATE 15/04/2026	A.P.S.
OPERATION RUE NEUVE GRAND TERRE 13930 AUREILLE		PLANS COUPES FACADES VILLAS 1 A 3 PMR		DATE 1/50 1/100	P.C. D.C.F. MARCHÉ