






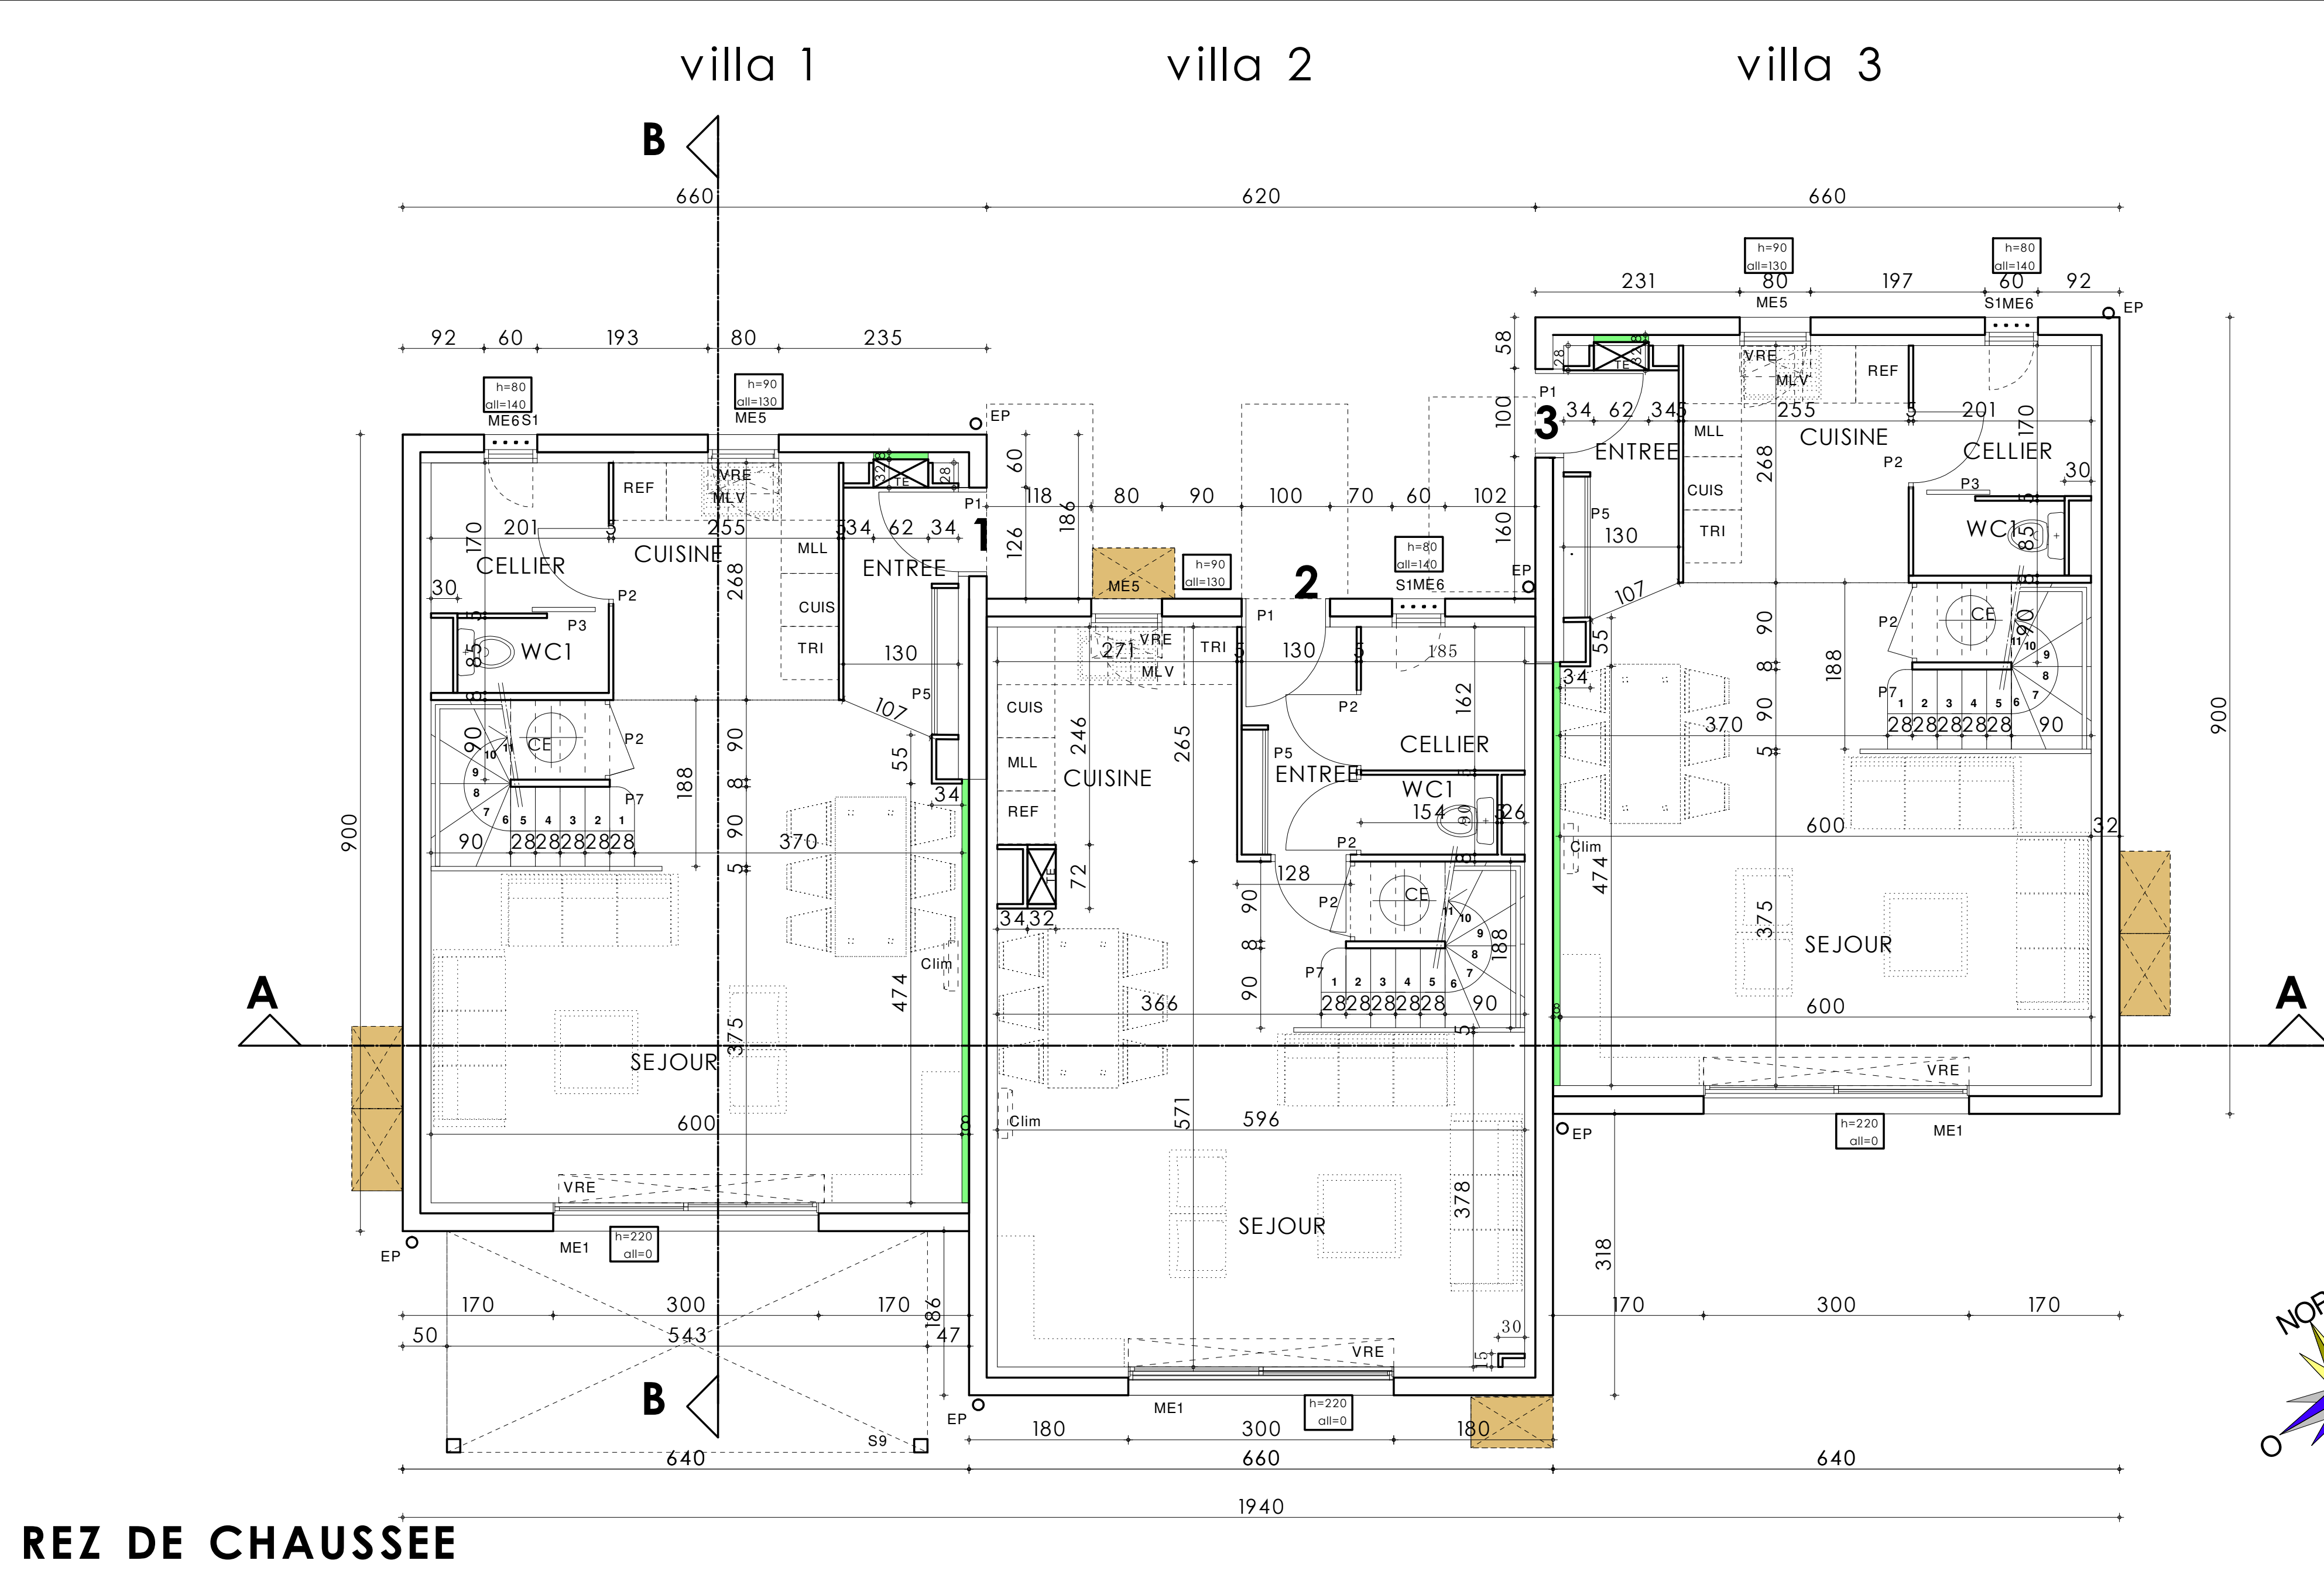


REZ DE CHAUSSEE

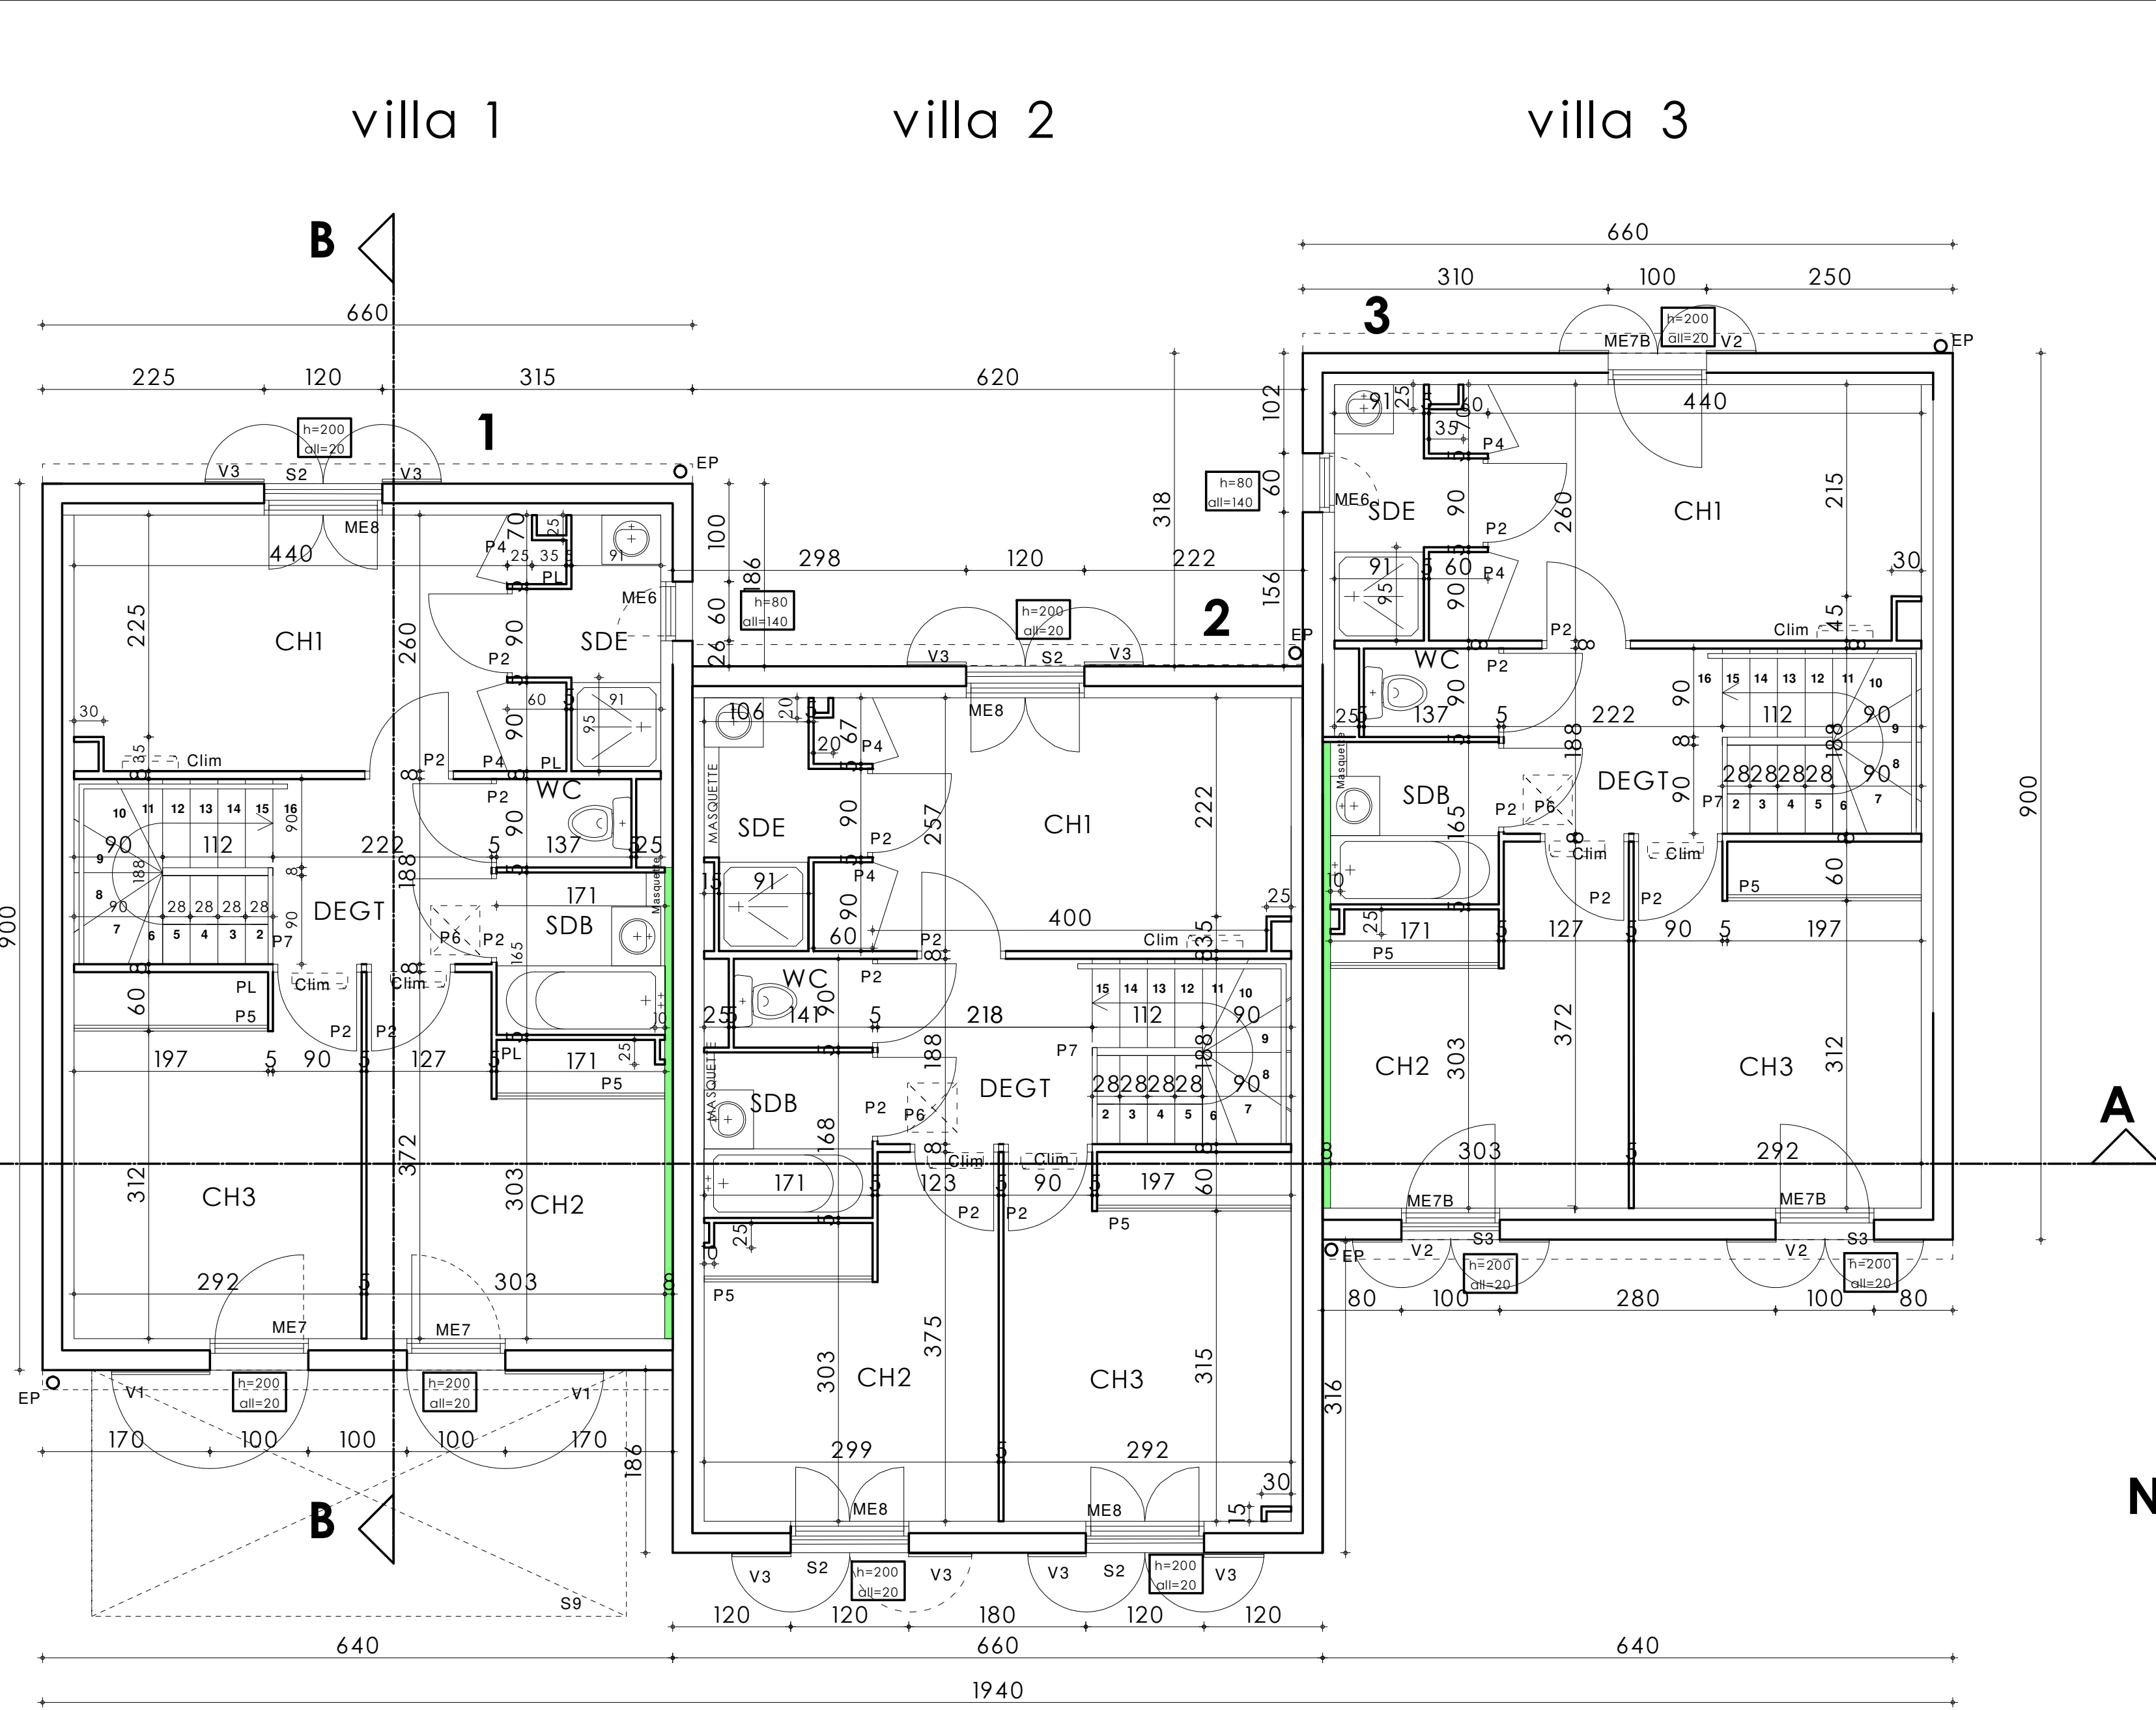

NIVEAU 1

PLAN DE NIVEAU 1/50

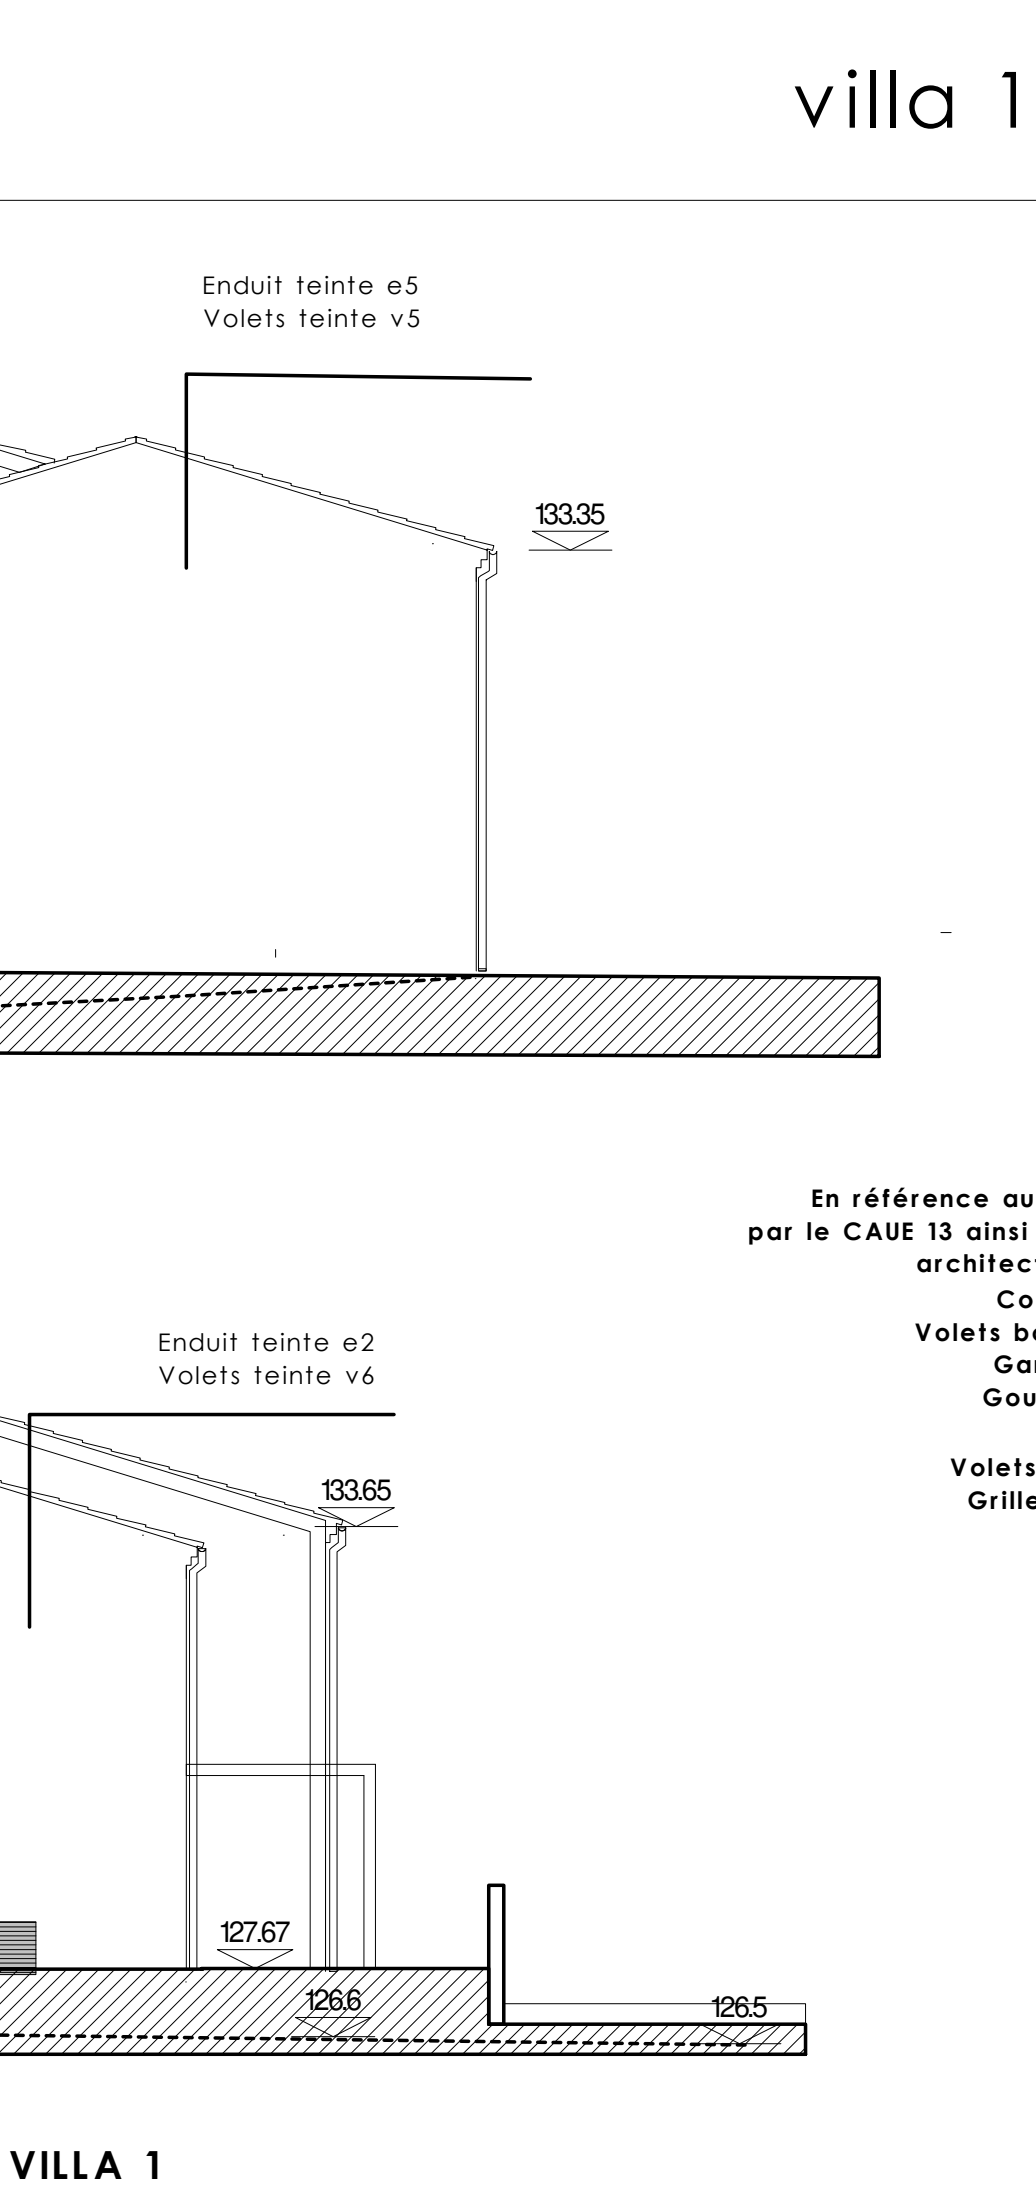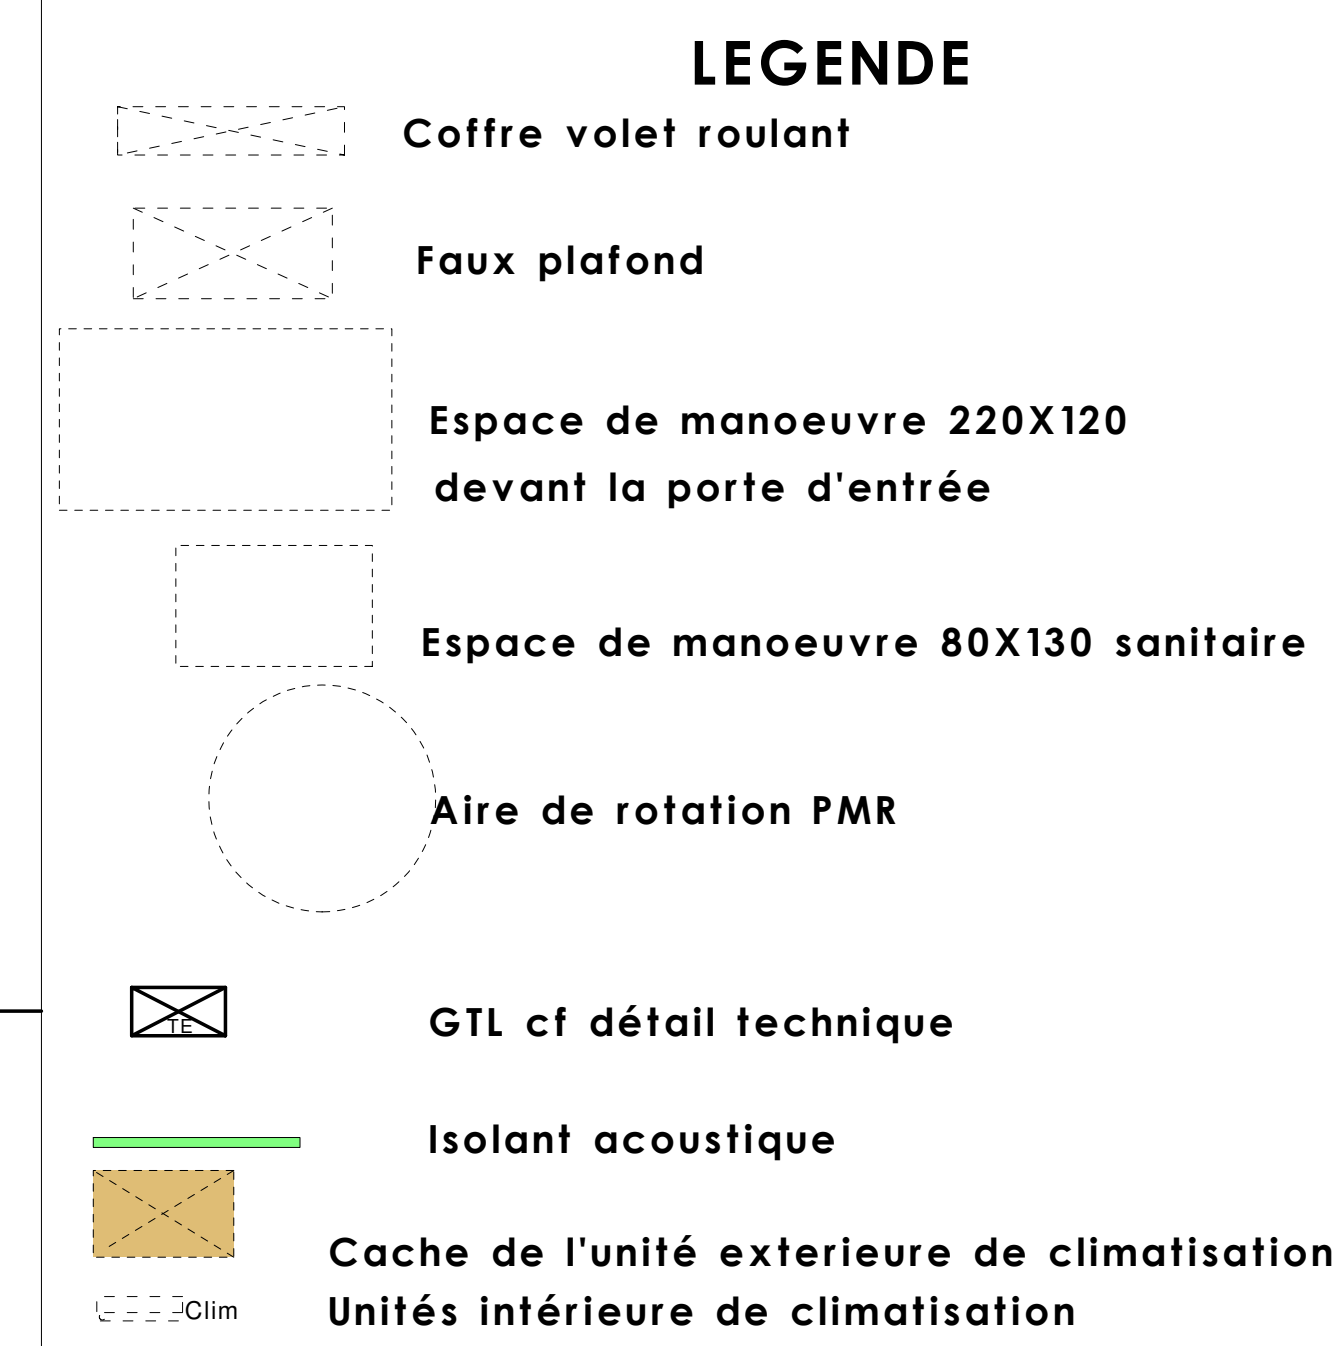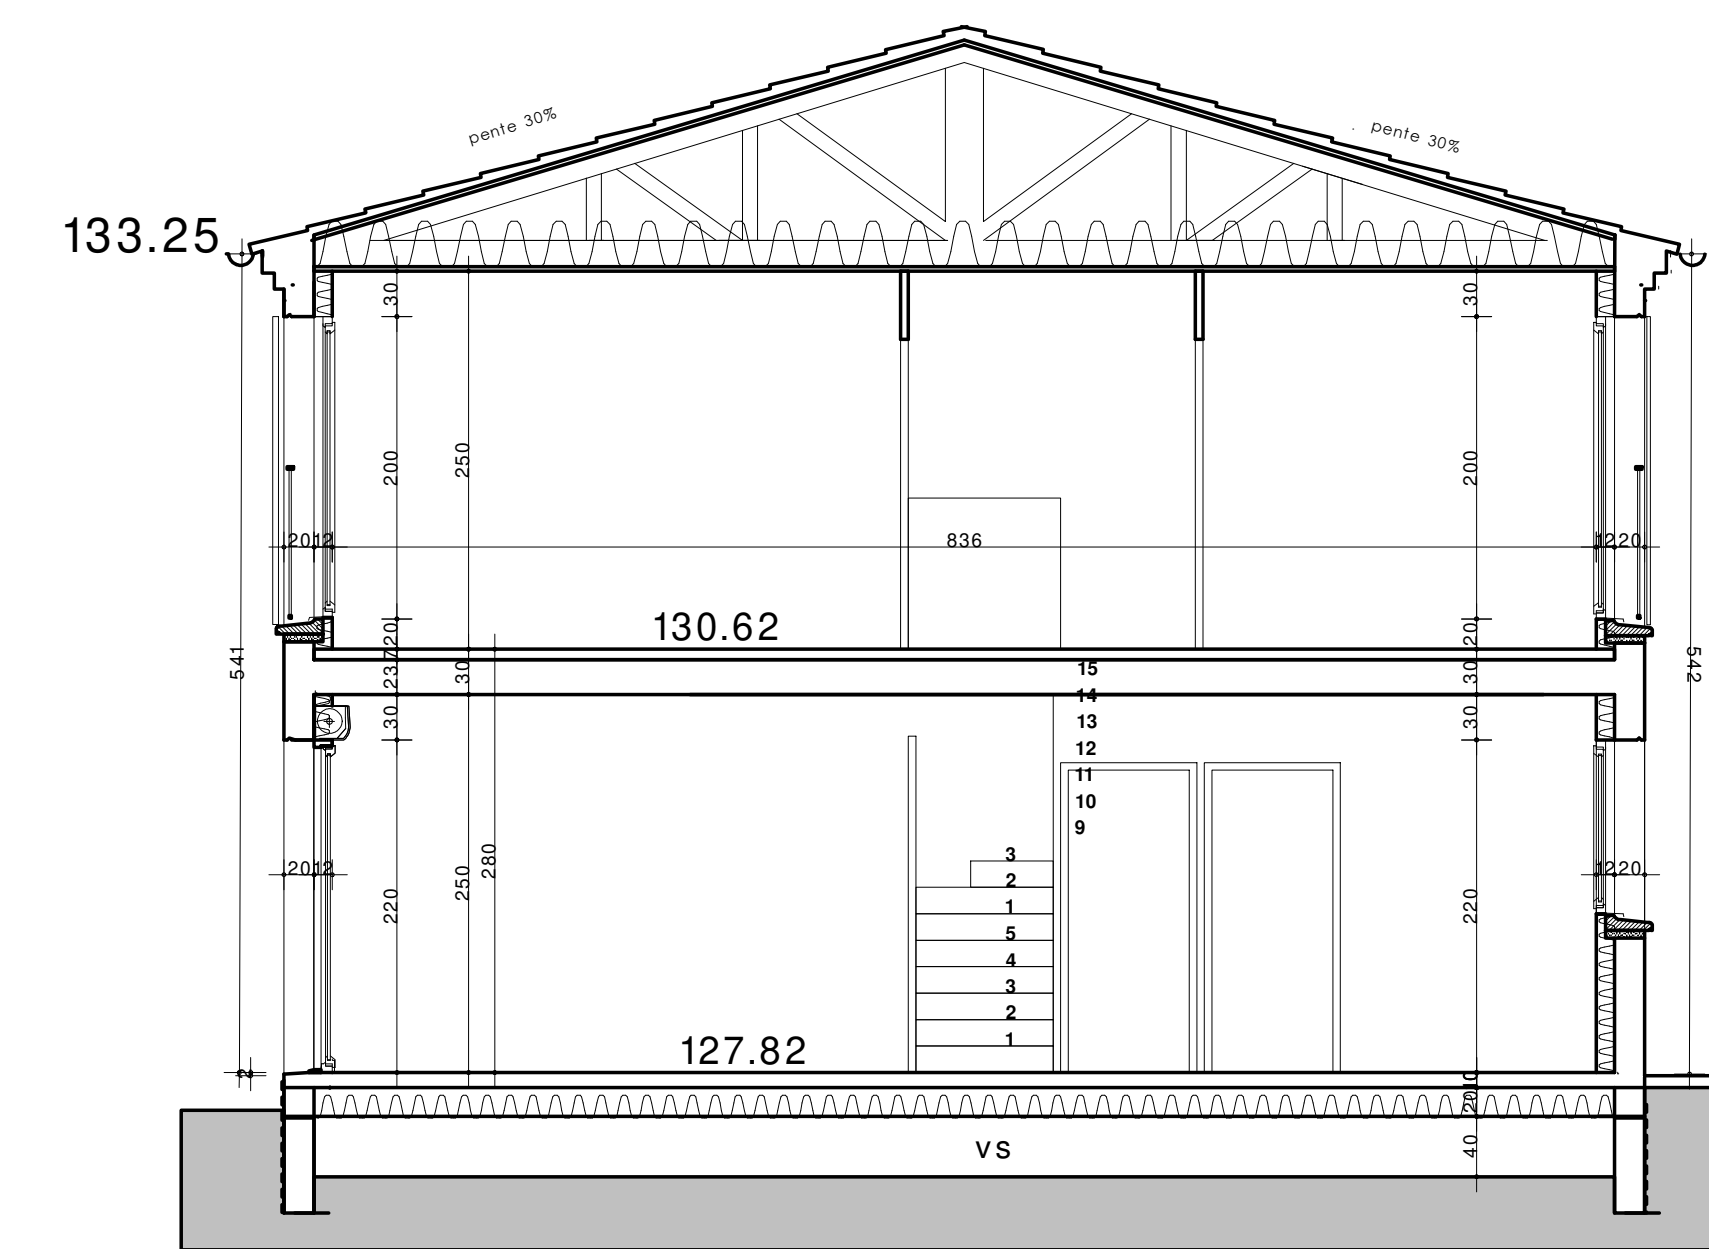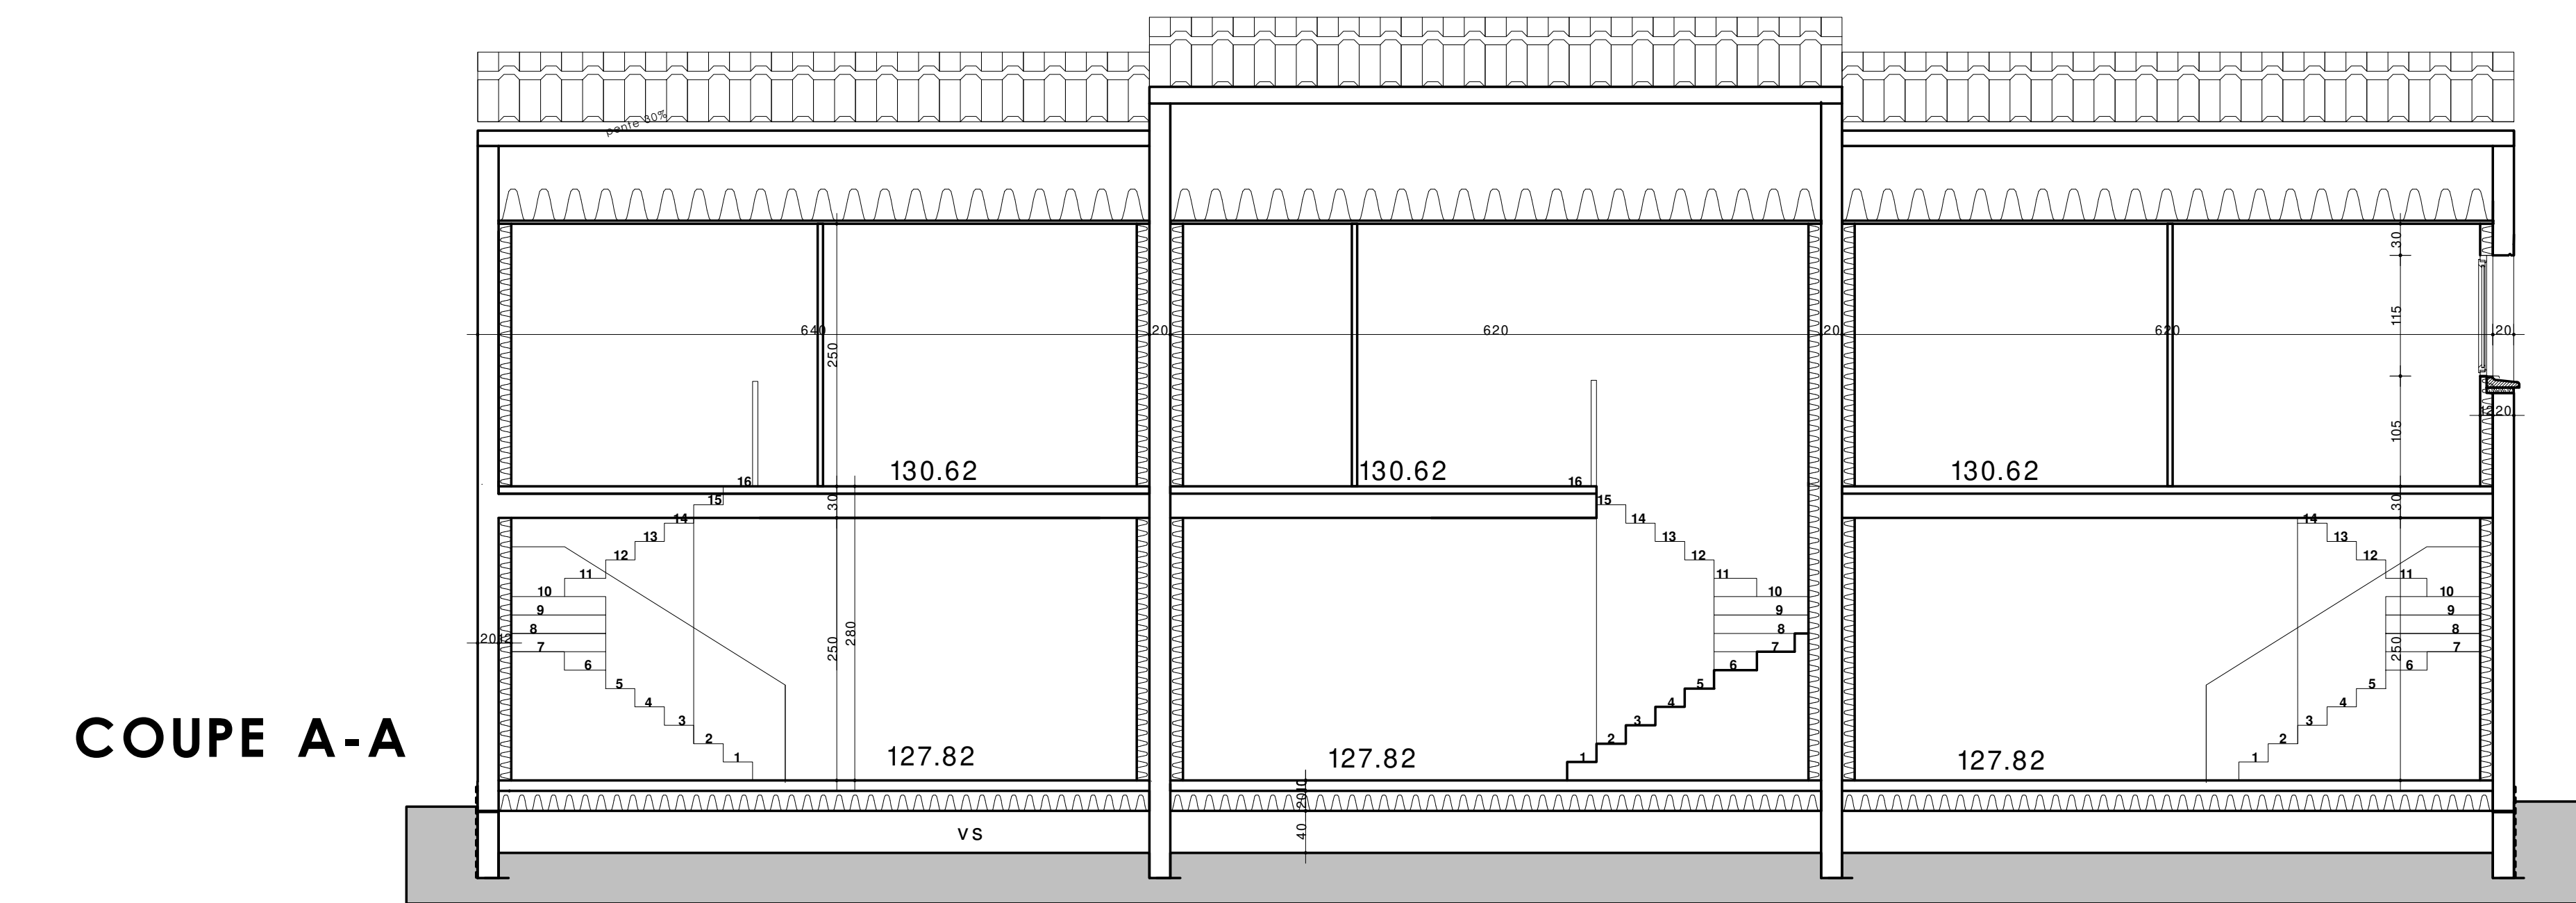

Les couleurs d'Aureille

En référence aux nuances de teintes recommandées par le CAUE 13 ainsi qu'à l'OAP et au cahier de recommandations architecturales urbaines et paysagères

Couvertures en tuile canal

Volets bois et portes d'entrée en bois

Gardes corps en serrurerie

Gouttières et chutes en zinc

Volets roulants pour les baies du rdc

Grilles en serrurerie noire pour les ouvertures des sdb

COUPES 1/50

FACADES /100

GRANDE TERRE		
INDICE	DATE	MODIFICATIONS
A	15/06/2026	MODIFICATIONS SUITE REUNION DCE
B	29/06/2026	SUPPRESSION LAVE MAIN DANS LES VILLAS COUTS MAITRISES
C	06/07/2026	MODIFICATION TE ET IOLANT ACOUSTIQUE
D		
E		
F		
G		
H		
I		
J		
K		
L		

ARCHITECTES M. CHAUVET A.C. CARRAZZA ARCHITECTES D.P.L.G. Entrepreneurs Individuels 40 rue FARGES 13008 MARSEILLE michaels@grandeterre.fr gc.versant1@gmail.com	MAITRISE D'OUVRAGE SCCV GRANDE TERRE (SIRET 942 743 709 R.C.S. Toulouse)	DATE 15/04/2026	A.P.S.
	OPERATION RUE NEUVE GRAND TERRE 13930 AUREILLE	BOULE 1/50 1/100	D.C.F.
	PLANS COUPES FACADES VILLAS 1 A 3 NON PMR	MARCHES	