



## villa 5

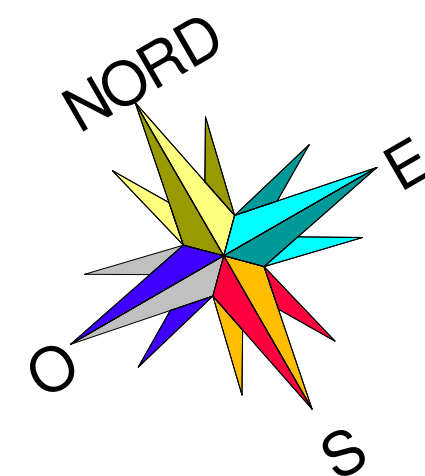


**REZ DE CHAUSSEE**

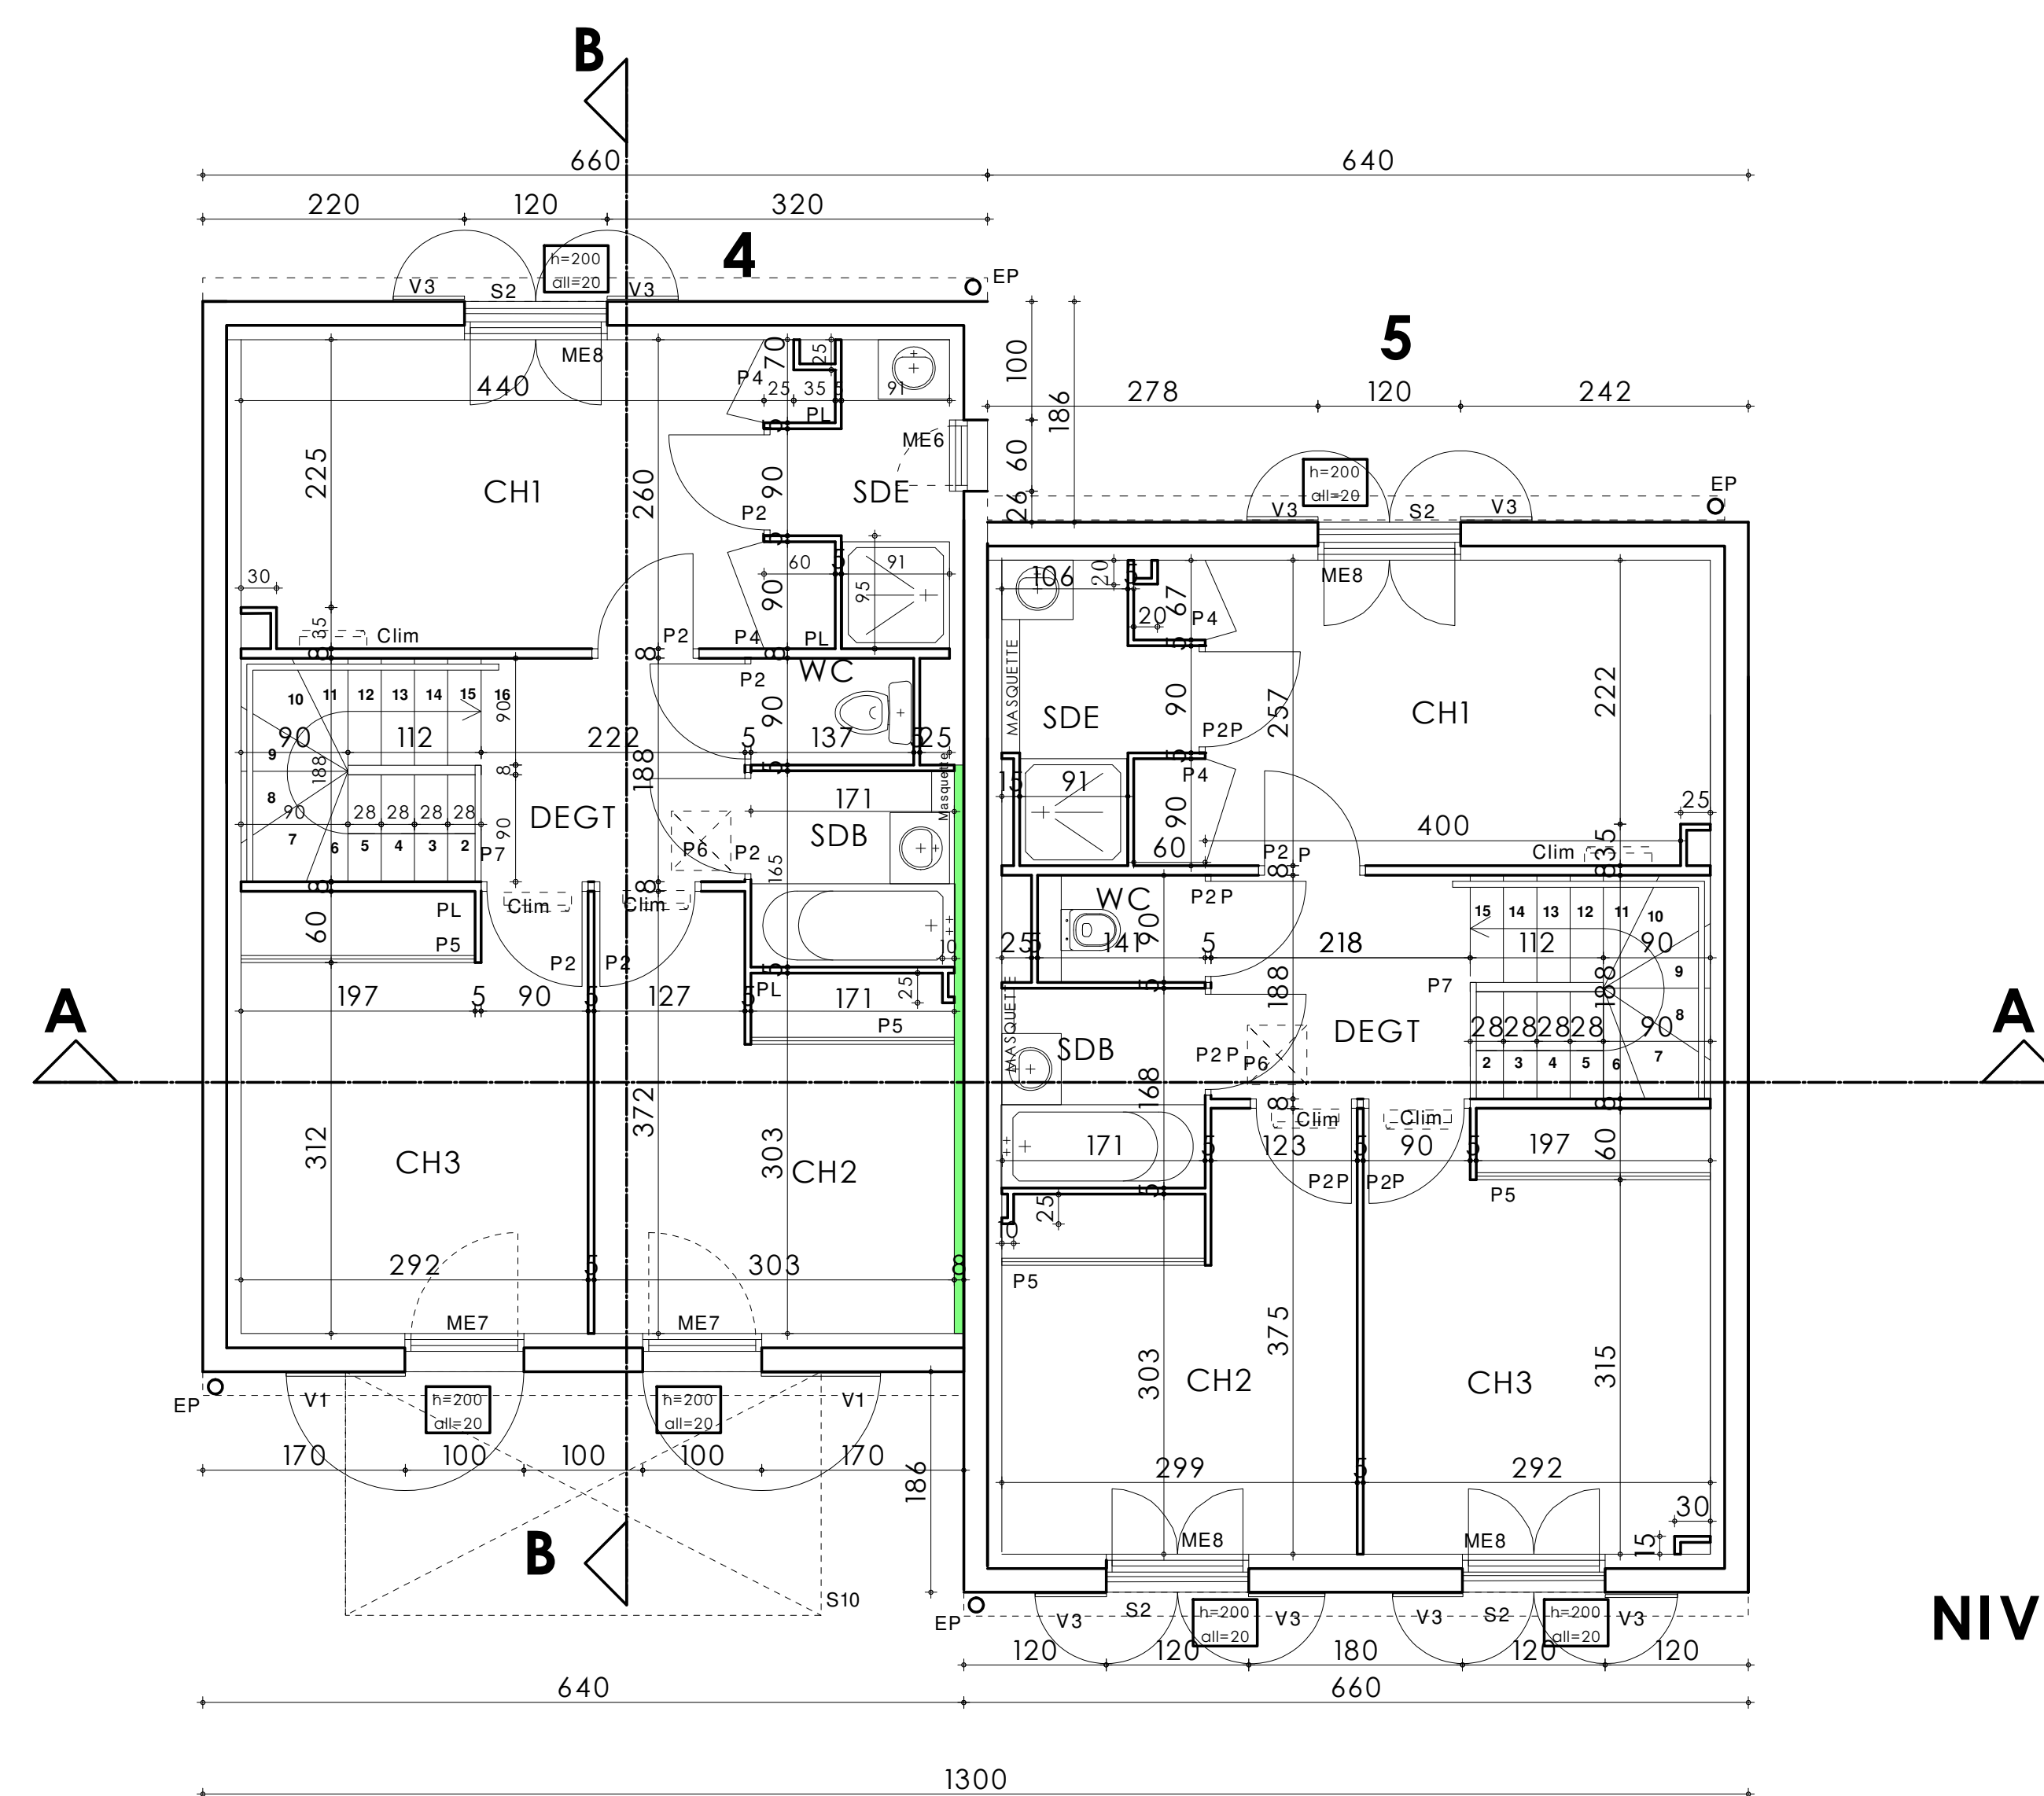



## NIVEAU 1

## PLAN DE NIVEAU 1/50

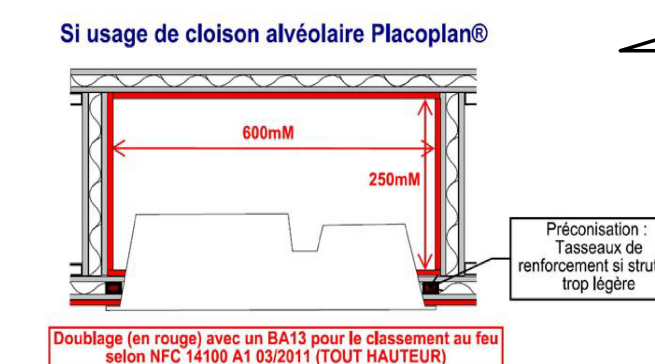


**LEGENDE**

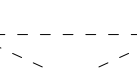 Coffre volet roulant

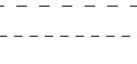 Faux plafond

 Espace de manoeuvre 220X120  
devant la porte d'entrée

 Espace de manoeuvre 80X130 sanitaire

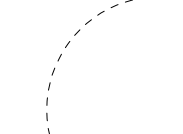 Aire de rotation PMR

 GTL cf détail technique

 Isolant acoustique

 Cache de l'unité extérieure de climatisation

 Unités intérieure de climatisation



villg 5



villa 4

**COUPES 1/50**



## Les couleurs d'Aureille

En référence aux nuanciers de teintes recommandées  
par le CAUE 13 ainsi qu'à l'OAP et au cahier de recommandations  
architecturales urbaines et paysagères  
Couvertures en tuile canal  
Volets bois et portes d'entrée en bois  
Gardes corps en serrurerie  
Gouttières et chutes en zinc

Volets roulants pour les baies du rd  
Grilles en serrurerie noire pour les  
ouvertures des sdh

**FACADES /100**

|                                                                                       |            |                                             |  |
|---------------------------------------------------------------------------------------|------------|---------------------------------------------|--|
|  |            |                                             |  |
| INDICE                                                                                | DATE       | MODIFICATIONS                               |  |
| A                                                                                     | 15/06/2026 | MODIFICATIONS SUITE REUNION DCE             |  |
| B                                                                                     | 29/06/2026 | SUPPRESSION LAVE MAIN VILLAS COUTS MATRICES |  |
| C                                                                                     | 06/07/2026 | MODIFICATION TE ET IOLANT ACOUSTIQUE        |  |
| D                                                                                     |            |                                             |  |
| E                                                                                     |            |                                             |  |
| F                                                                                     |            |                                             |  |
| G                                                                                     |            |                                             |  |
| H                                                                                     |            |                                             |  |
| I                                                                                     |            |                                             |  |
| J                                                                                     |            |                                             |  |
| K                                                                                     |            |                                             |  |
| L                                                                                     |            |                                             |  |

|   |   |   |        |
|---|---|---|--------|
| <b>ARCHITECTES</b><br><b>M. CHAUVET</b><br><b>A.C. CARNAZZA</b><br><b>ARCHITECTES D.P.L.G.</b><br><b>Entrepreneurs Individuels</b><br><b>40 Rue FARCES 13008 MARSEILLE</b><br><small>m.chauvet@orange.fr</small><br><small>ac.carnazza@orange.fr</small> | <b>MATRE D'OUVRAGE</b><br><b>SCCV GRAND TERRE</b><br><small>(SIRET 942 743 709 R.C.S. Toulouse)</small><br><br><small>OPERATION:</small><br><b>RUE NEUVE GRAND TERRE</b><br><b>13930 AUREILLE</b> | DATE: <b>15/04/2026</b>                                                                                | A.P.   |
|   |   | DOUELLE: <b>1/50</b>                                                                                   | P.I.   |
|   |   |   | D.C.   |
|   |   |   | MARCHÉ |
|   |   | <small>TITRE DU PLAN</small><br><b>PLANS COUPES FACADES</b><br><b>VILLAS 4 et 5</b><br><b>NON PAMP</b> | 10     |