

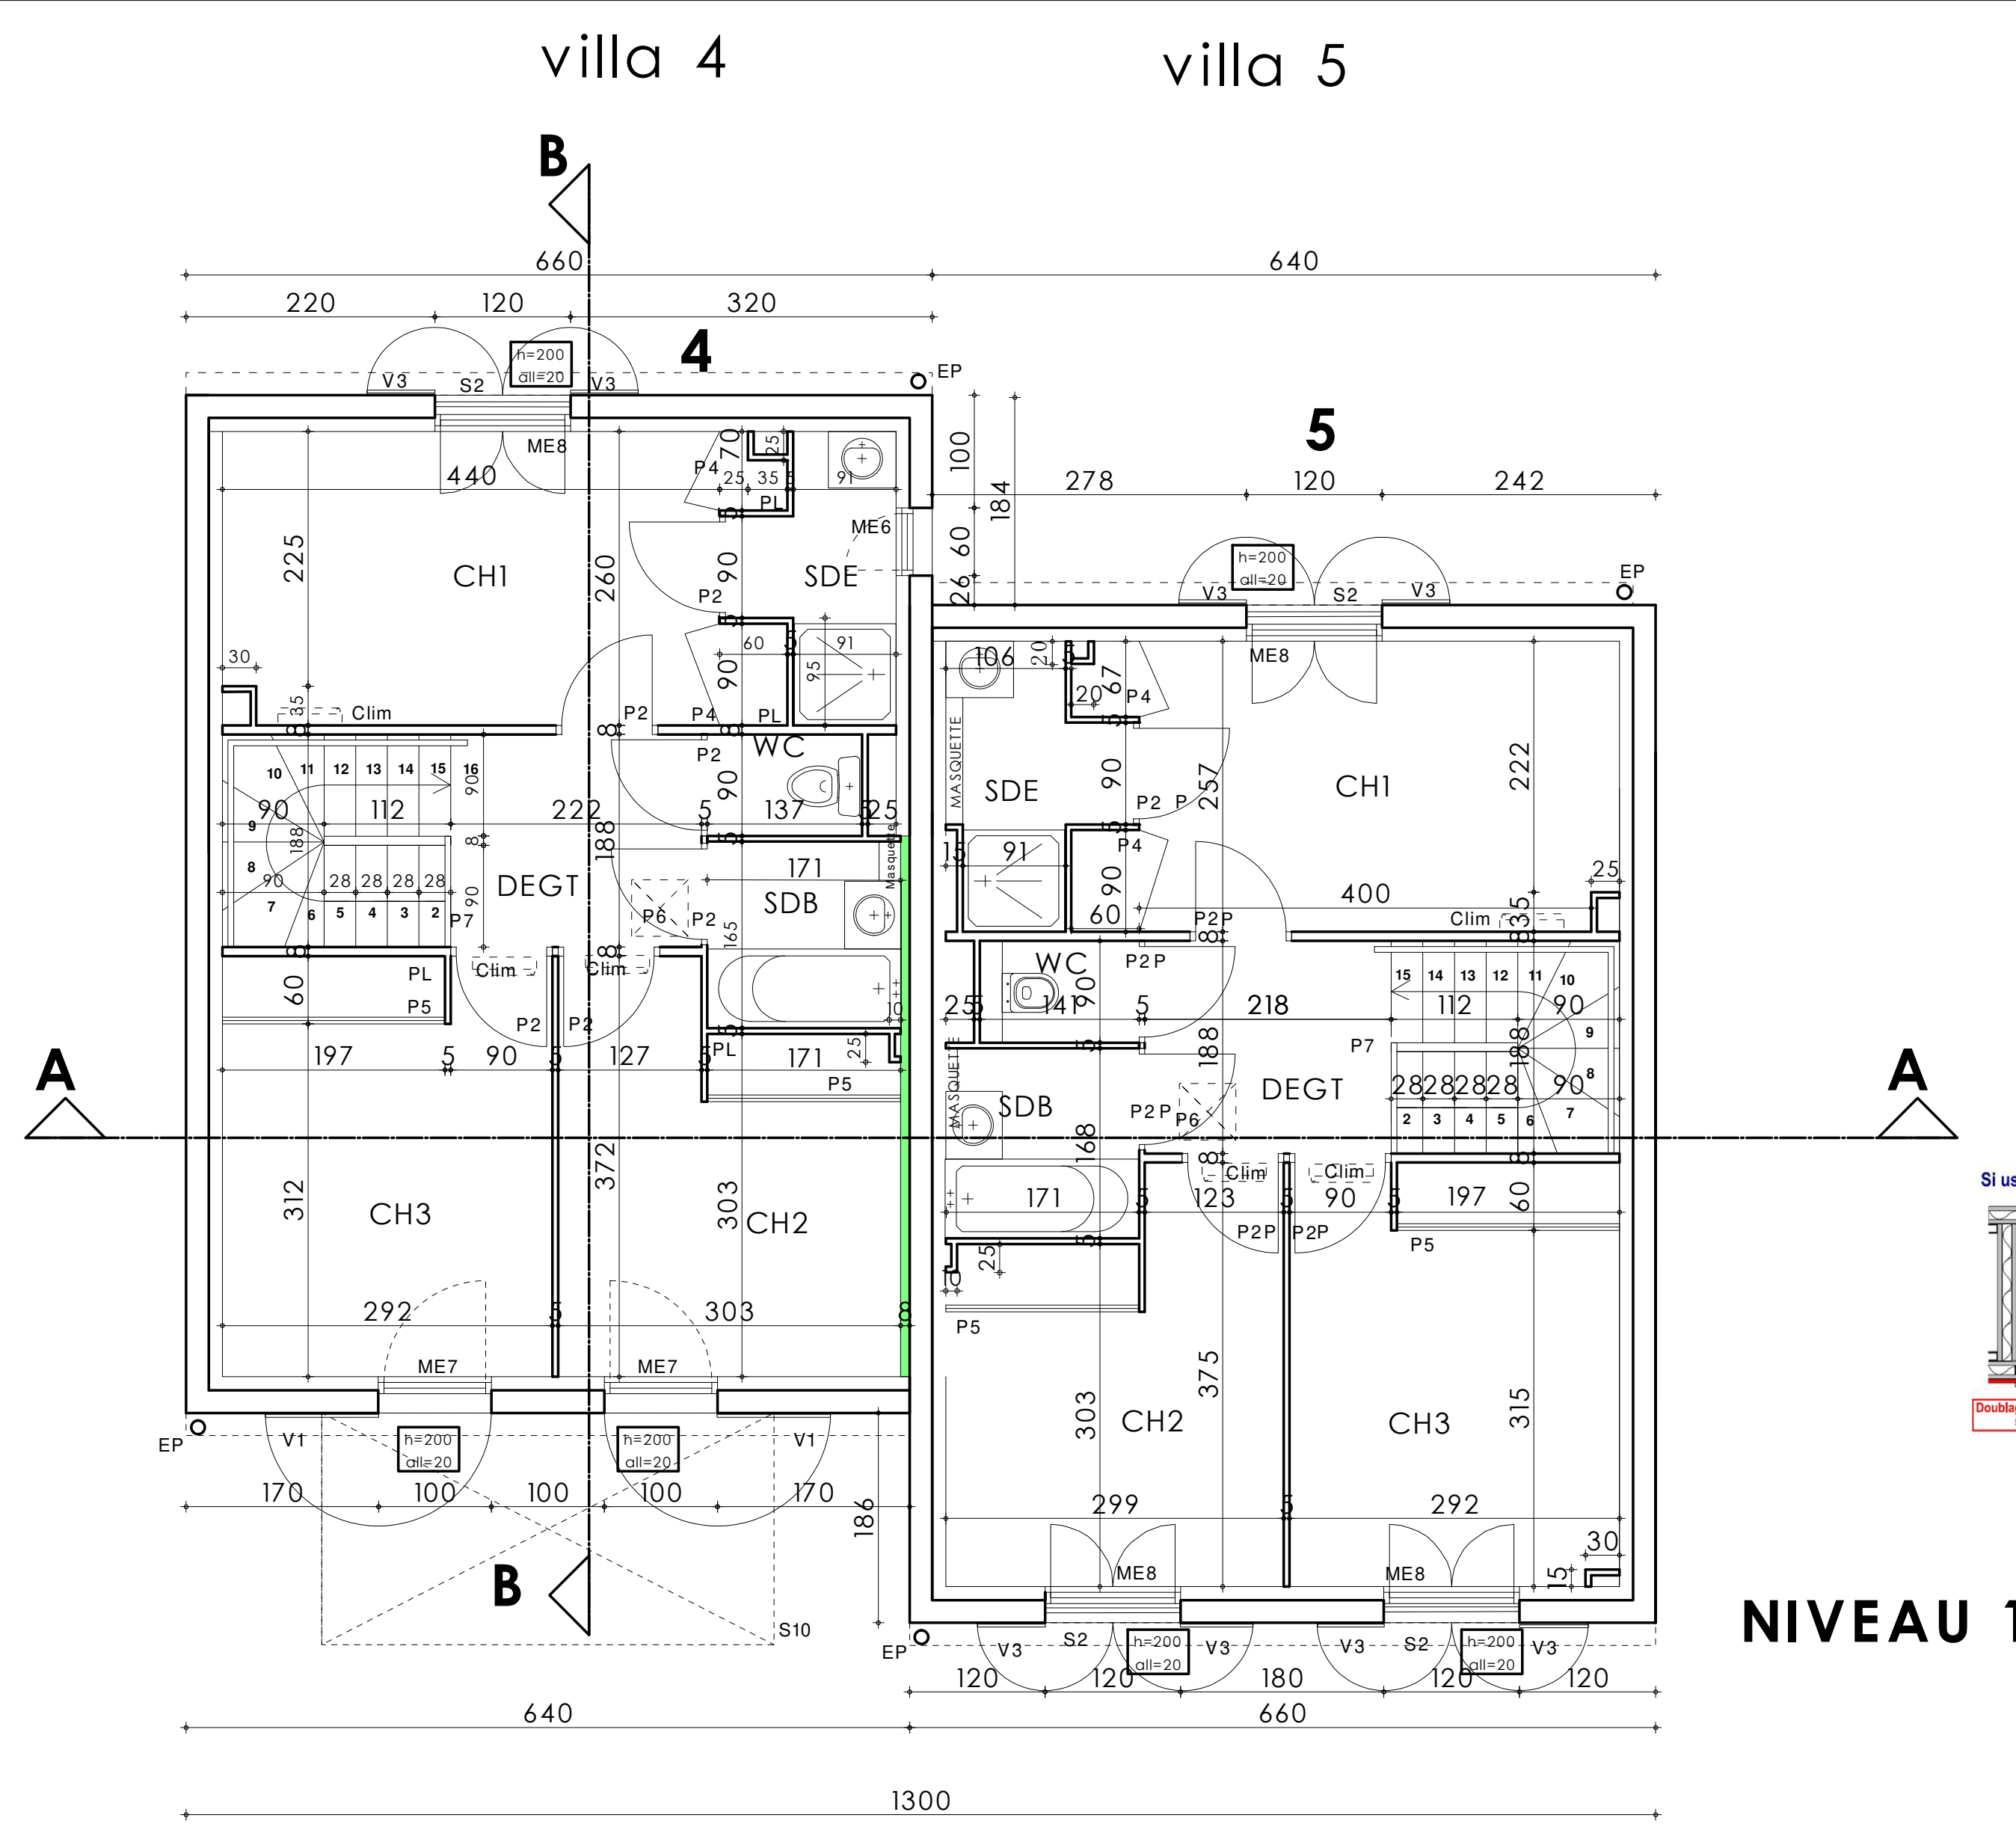



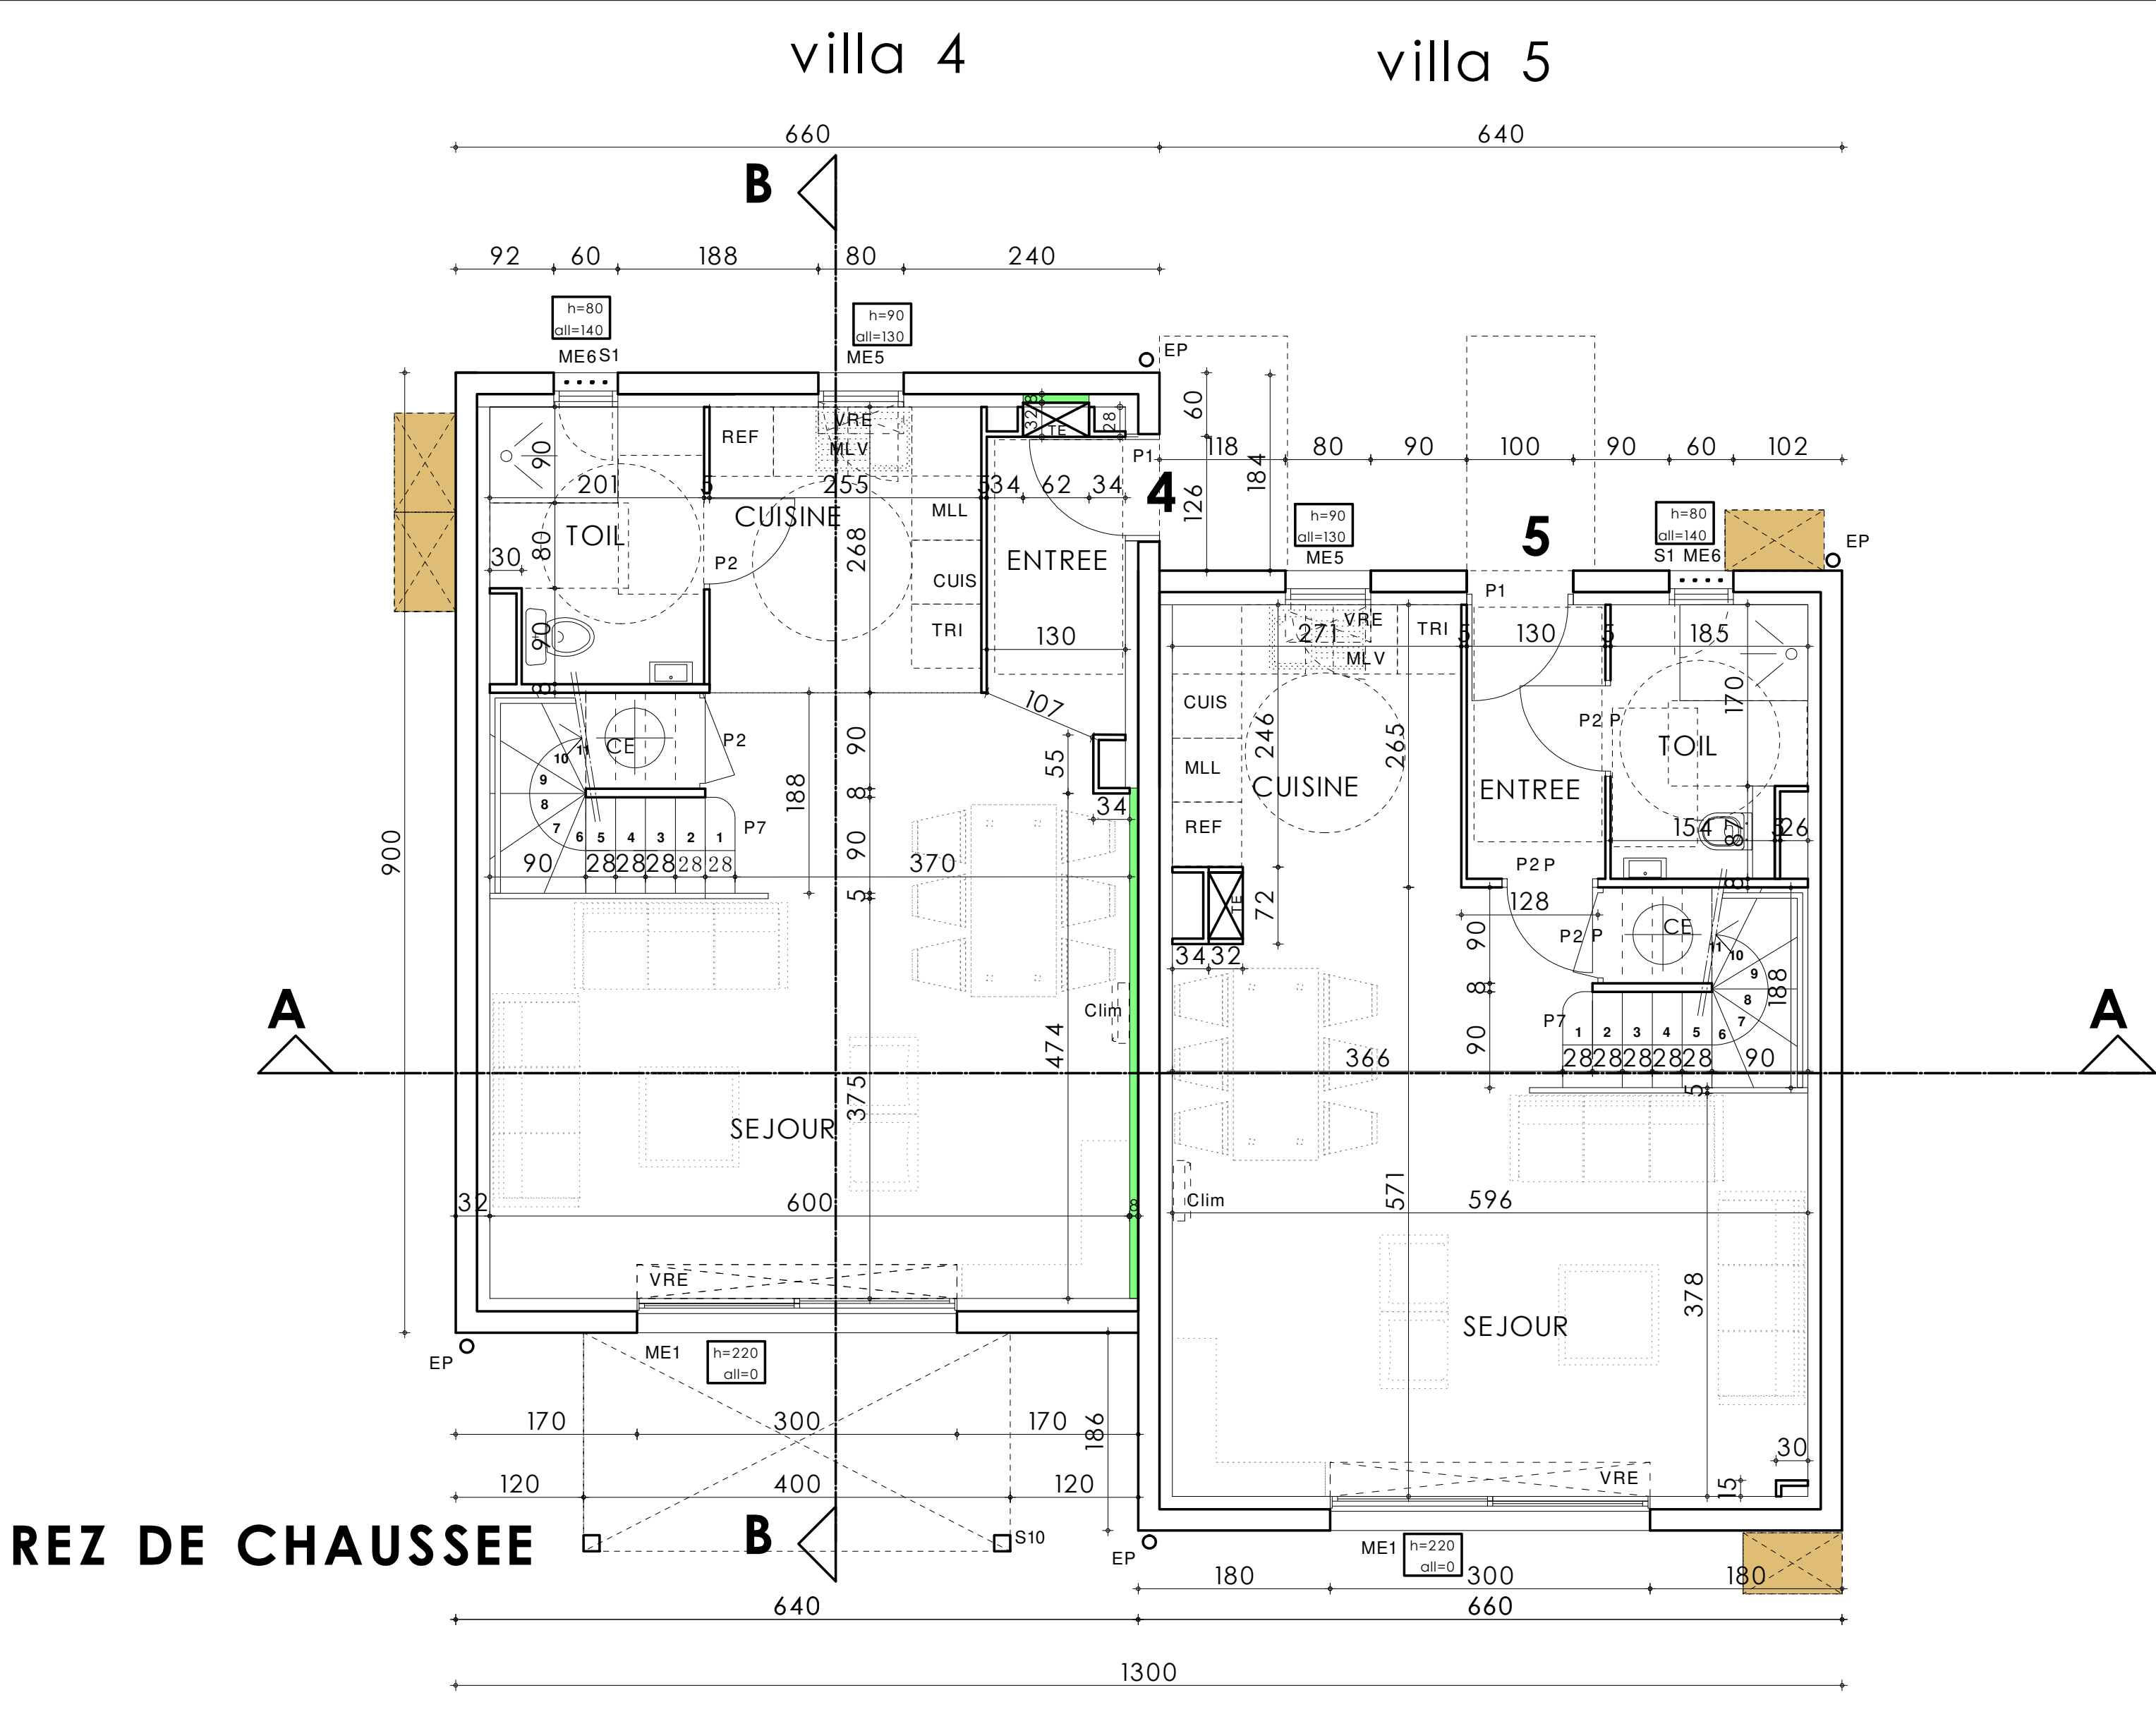


LEGENDE


- Coffre volet roulant
- Faux plafond
- Espace de manoeuvre 220X120 devant la porte d'entrée
- Espace de manoeuvre 80X130 sanitaire
- Aire de rotation PMR
- GTL cf détail technique
- Isolant acoustique
- Cache de l'unité extérieure de climatisation
- Unités intérieure de climatisation

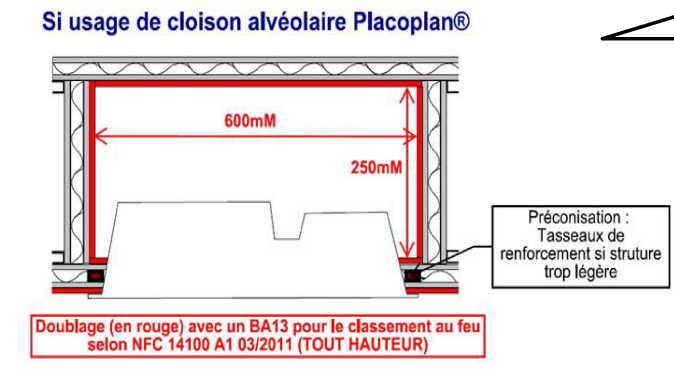

PLAN DE NIVEAU 1/50

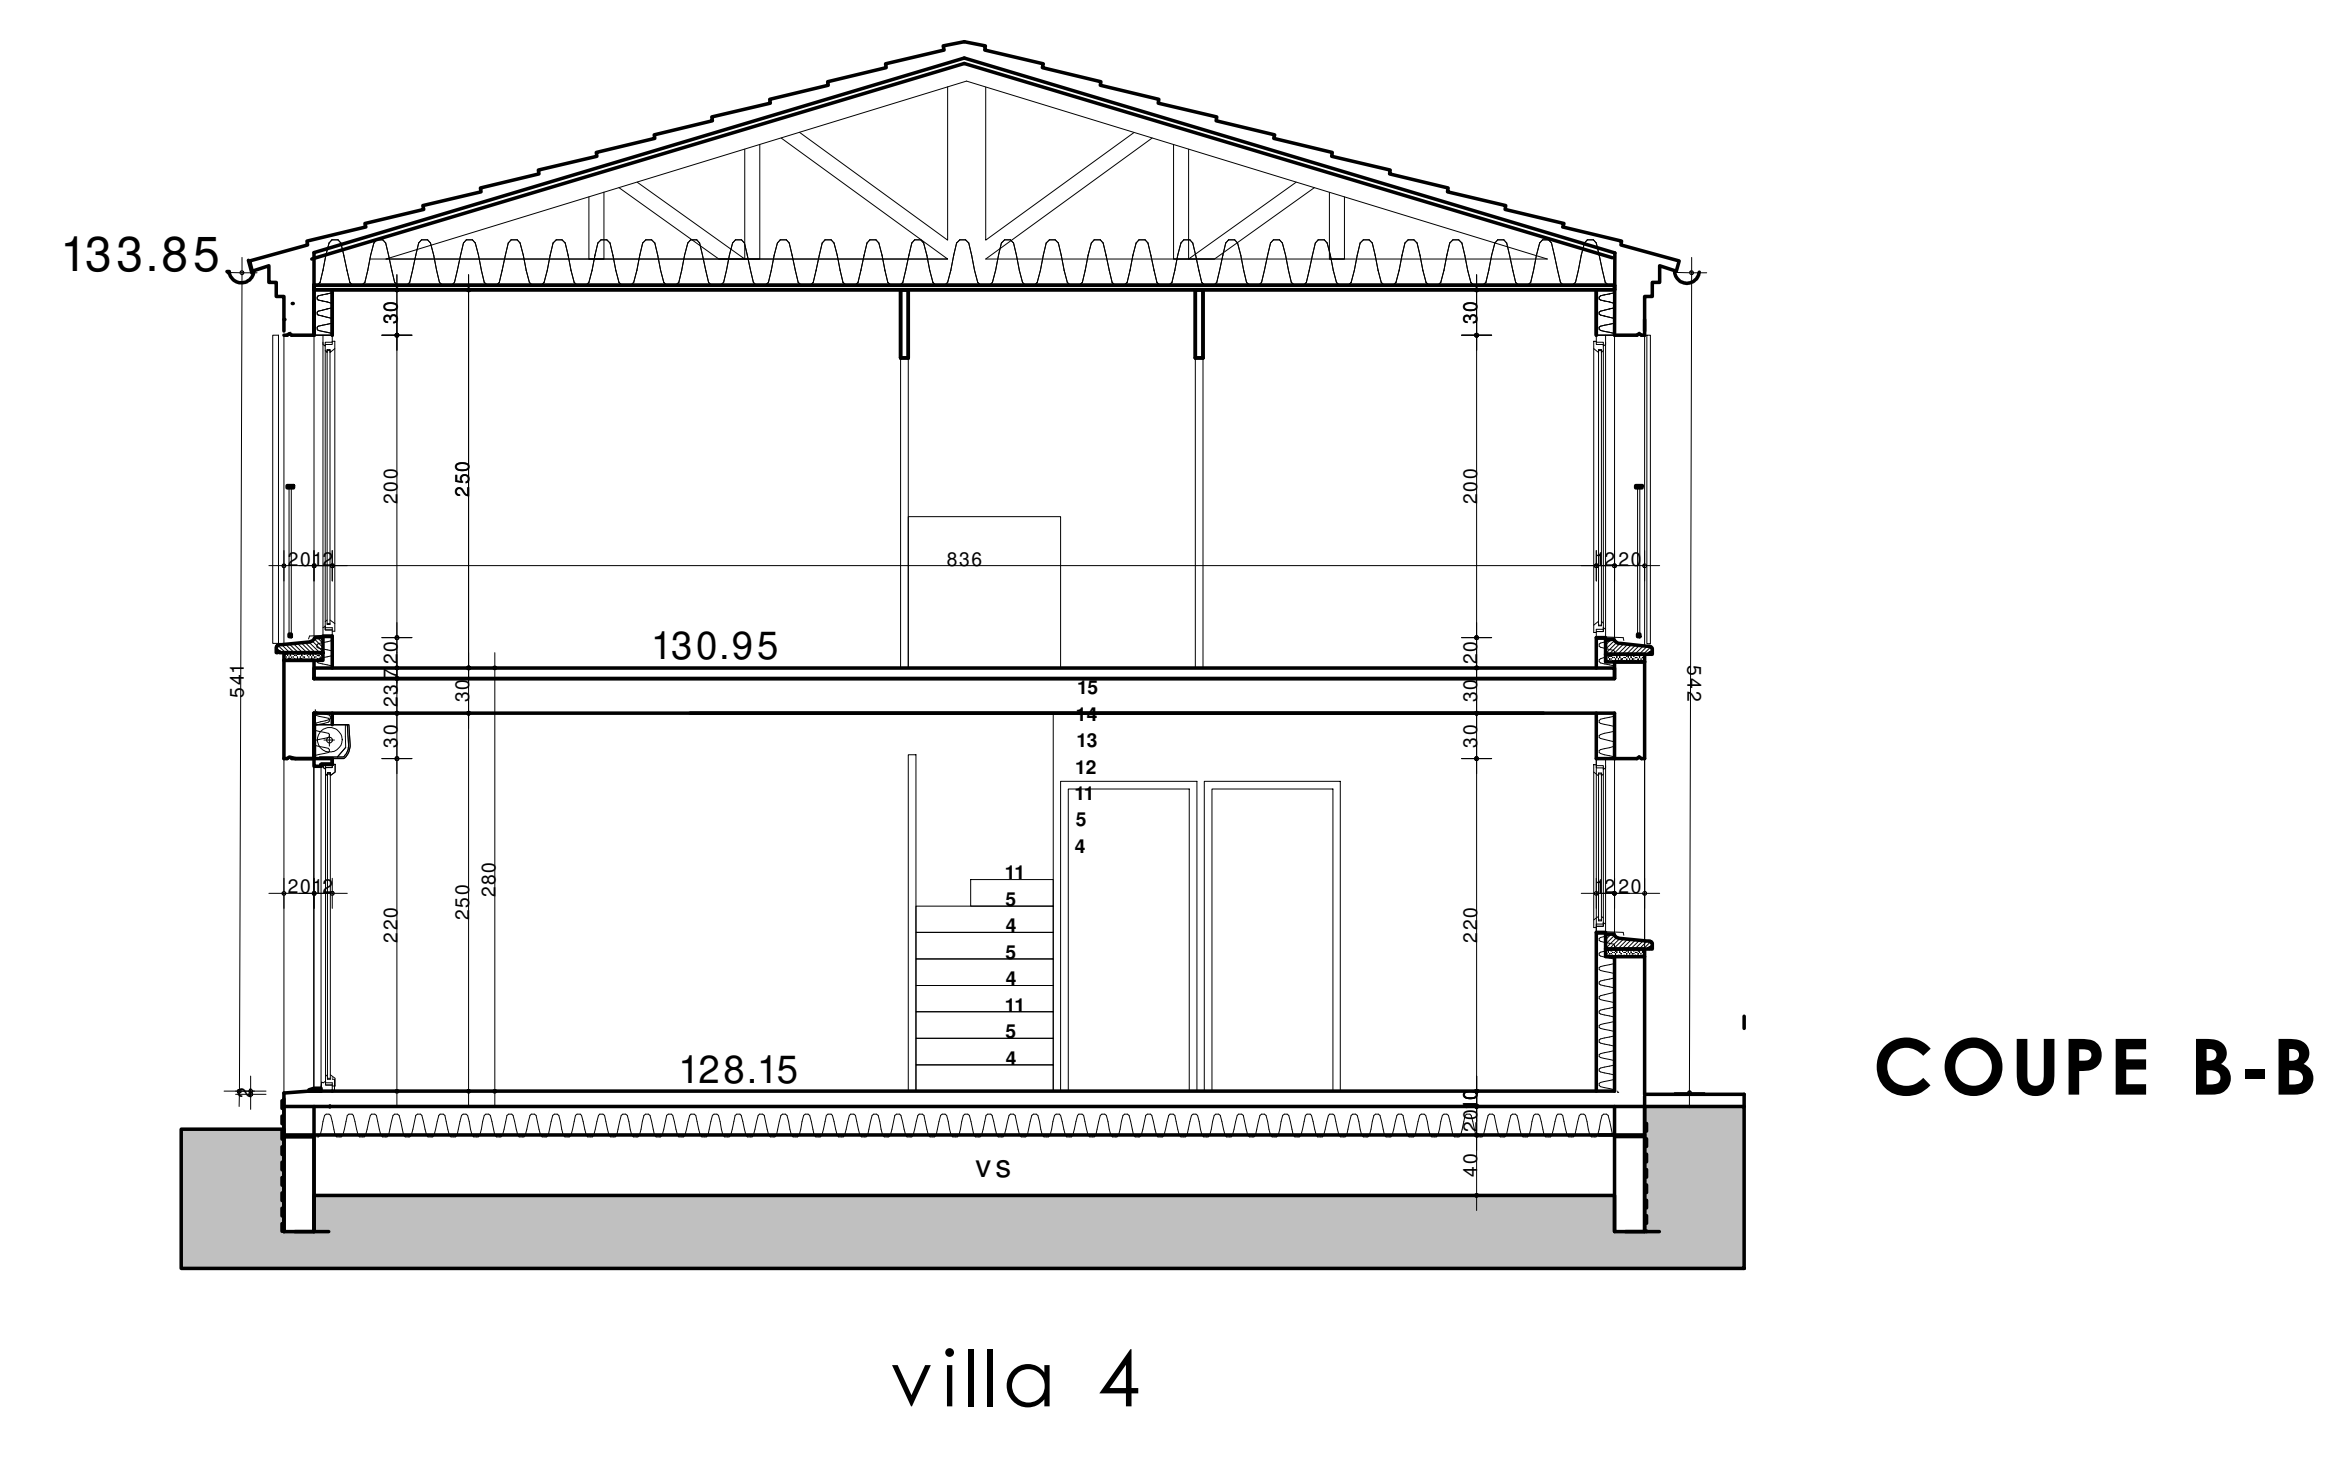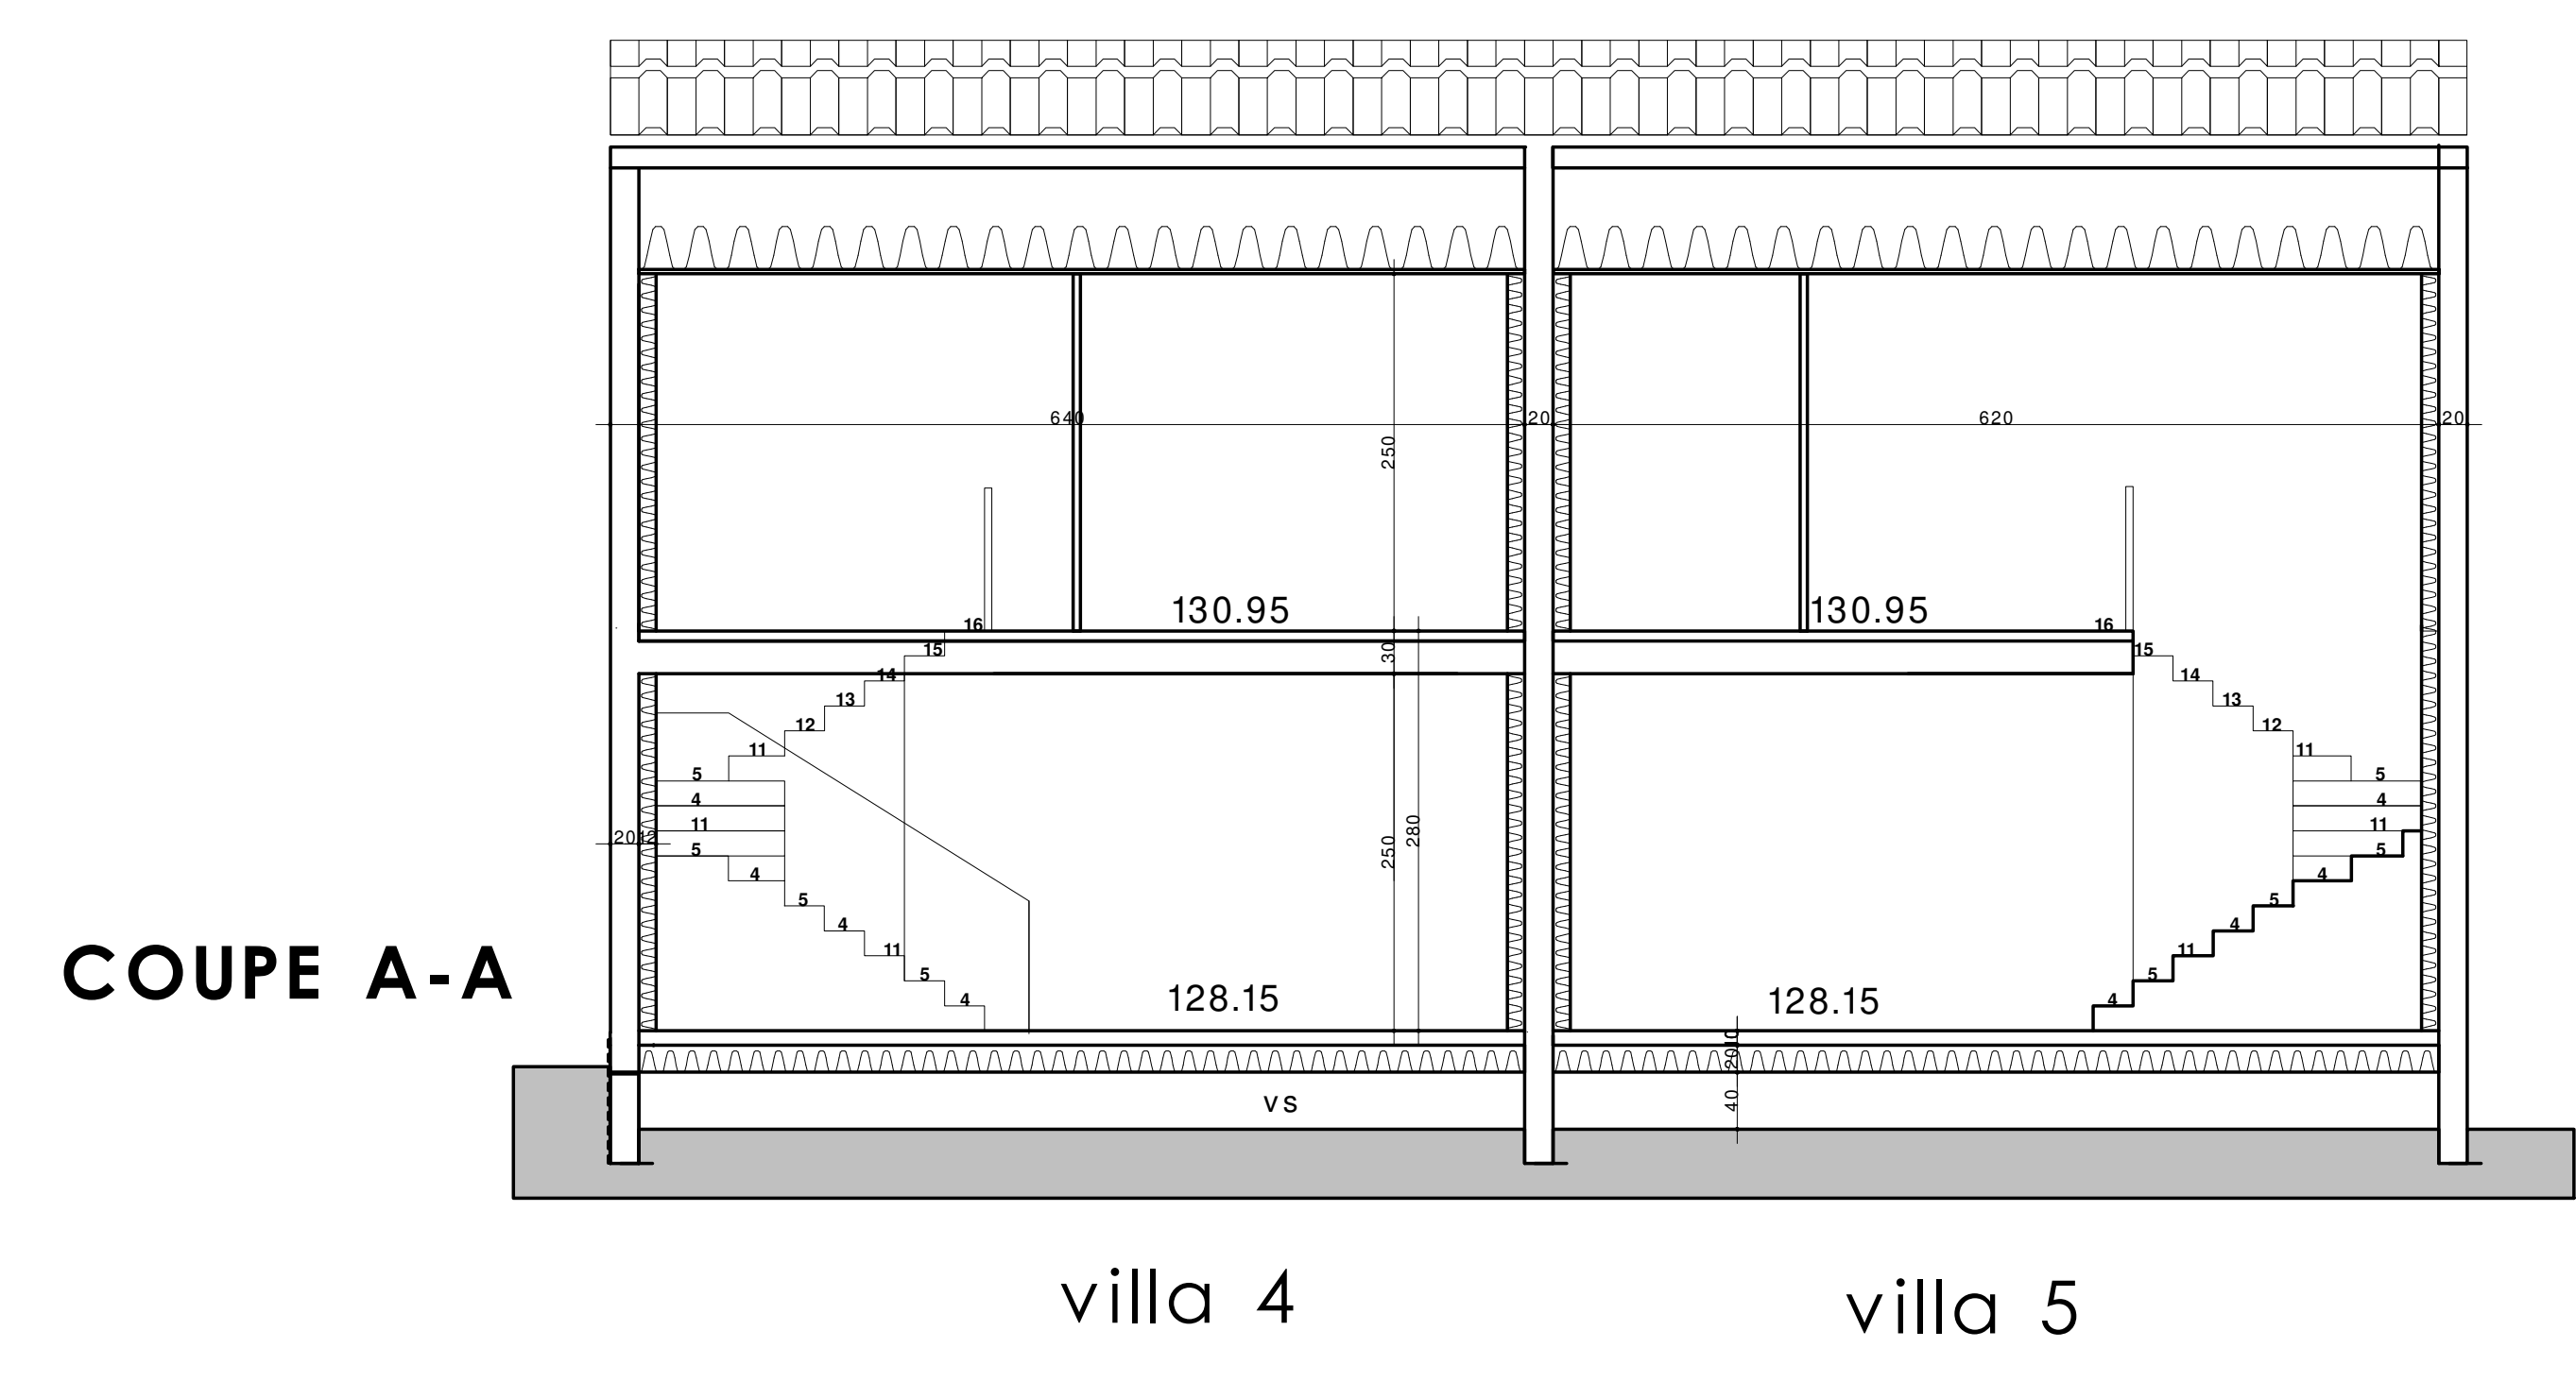

COUPES 1/50

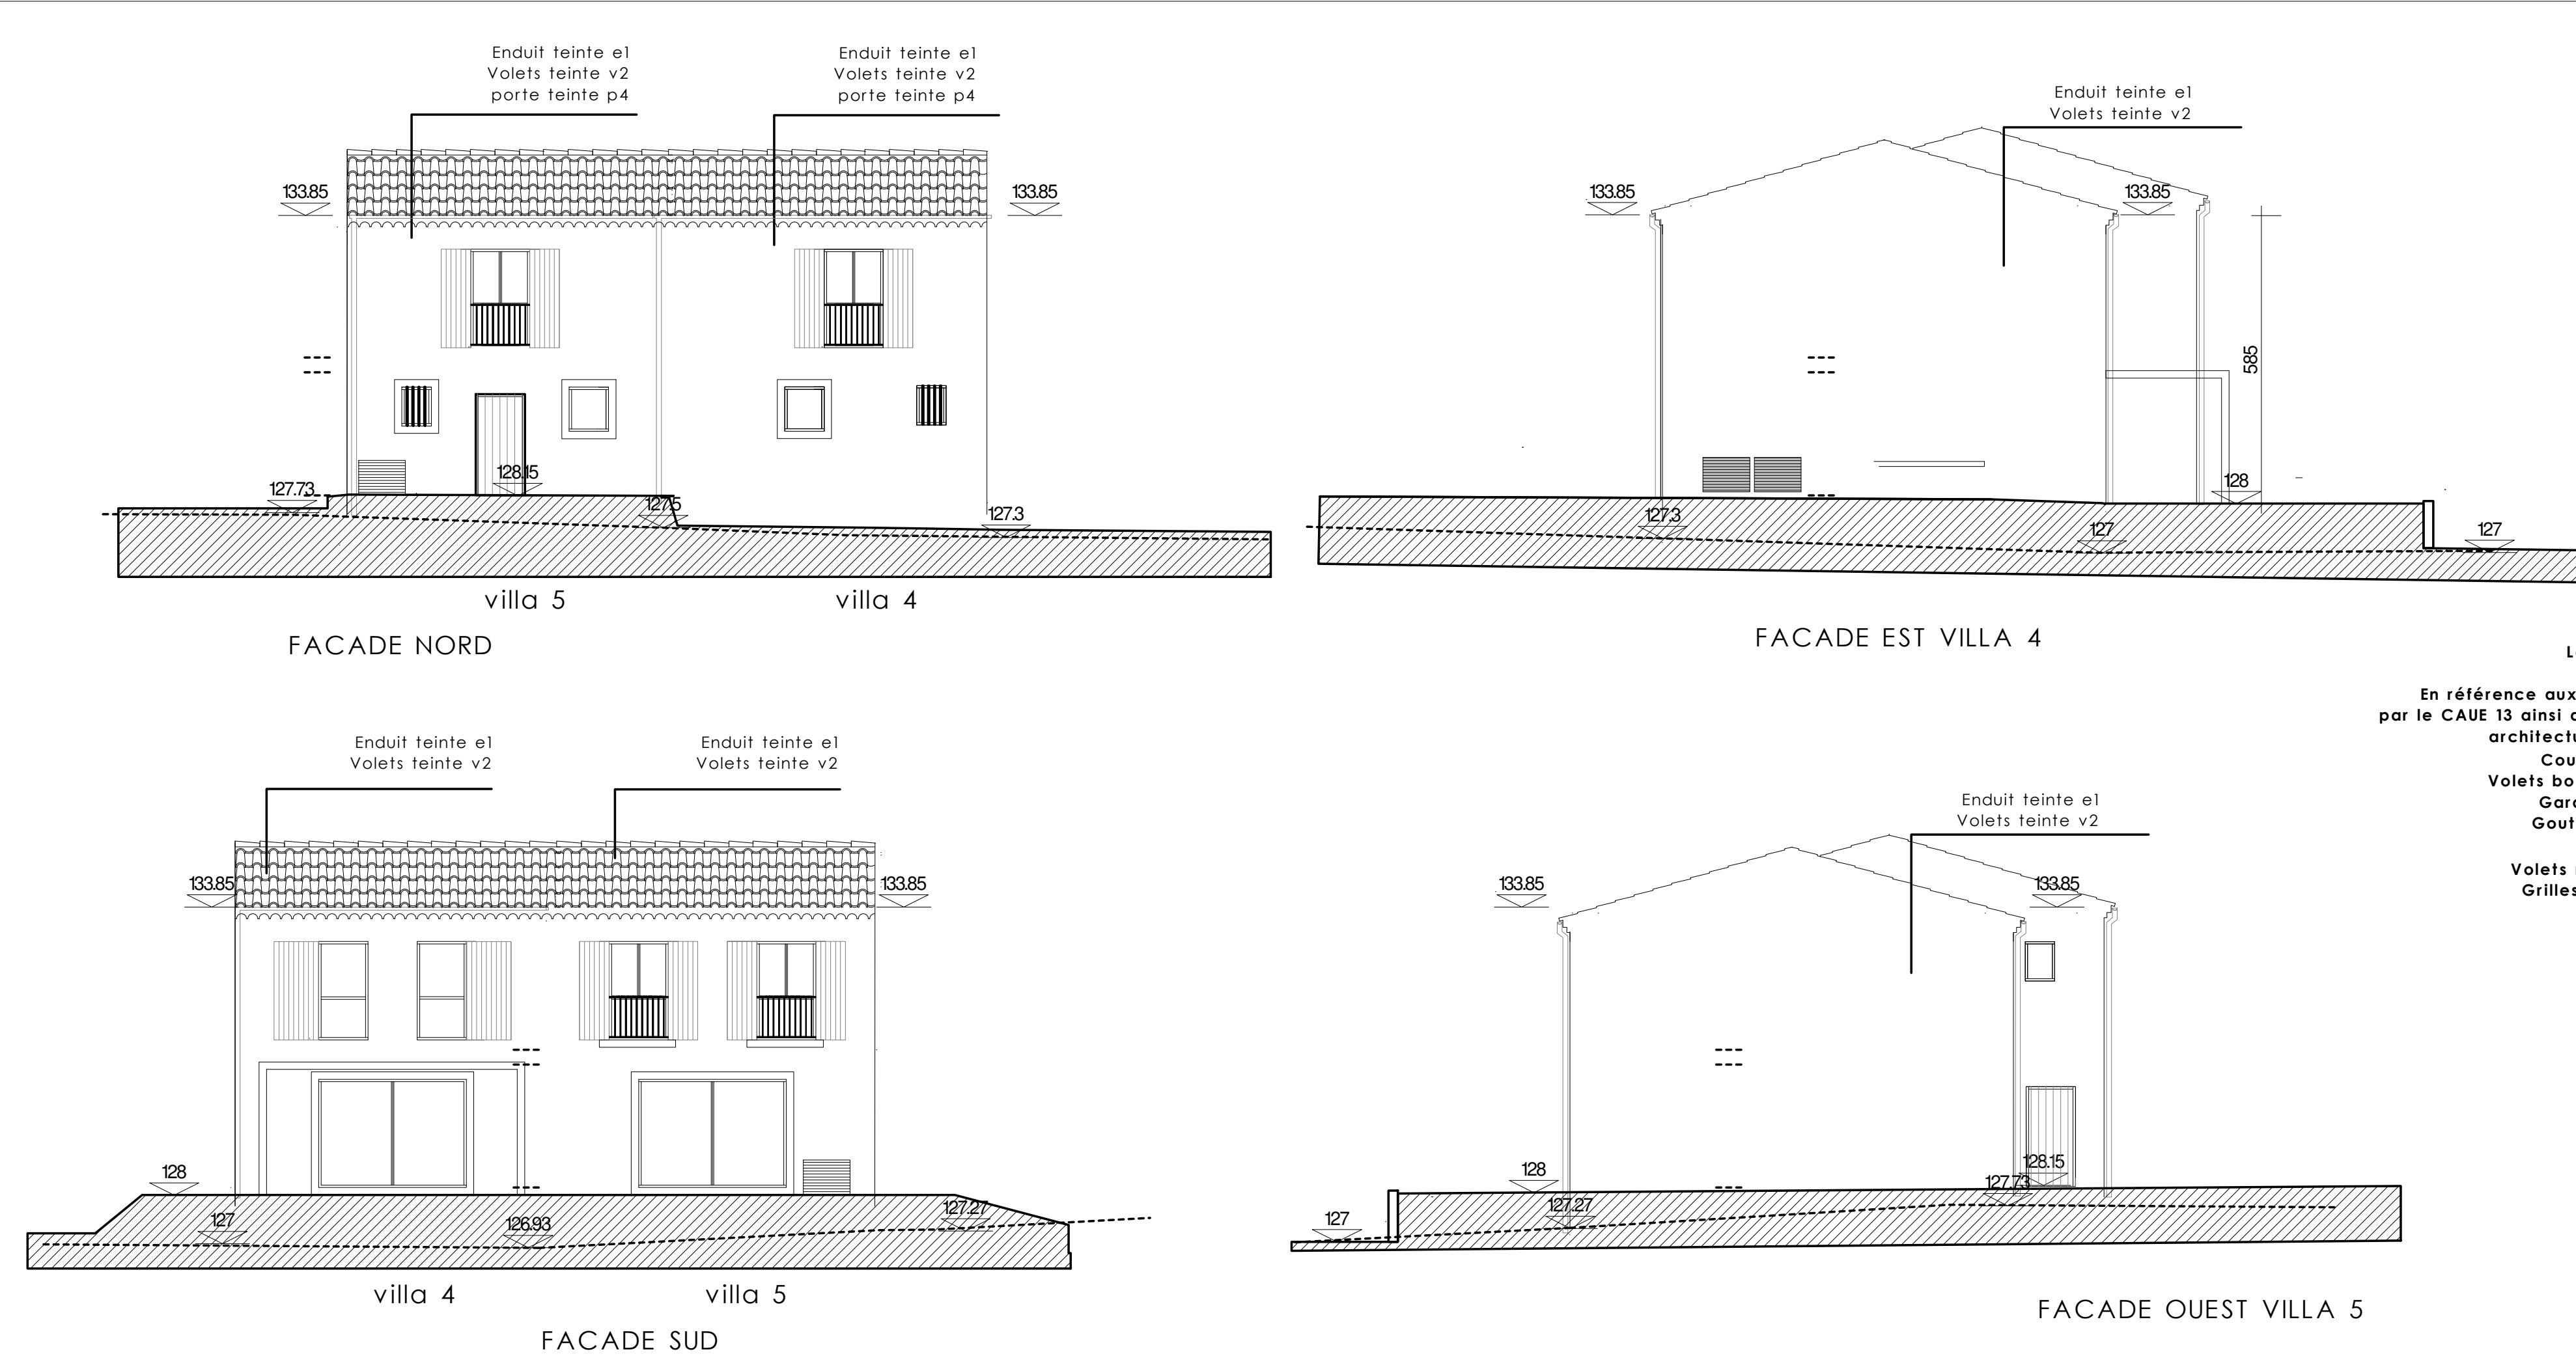

FACADES /100

GRANDE TERRE			
INDICE	DATE	MODIFICATIONS	
A	15/06/2024	MODIFICATIONS SUITE REUNION DCE	
B			
C	06/07/2026	MODIFICATION TE ET ISOLANT ACOUSTIQUE	
D			
E			
F			
G			
H			
I			
J			
K			
L			
ARCHITECTES M. CHAUVET A.C. CARNAZZA ARCHITECTES D.P.L.G. Entrepreneurs Individuels 40 Rue FARGES 13008 MARSEILLE P.L.Chaudet@orange.fr 06.44.11.11.11		MATRE D'OUVRAGE SCCV GRANDE TERRE (SIRET 942 743 709 R.C.S. Toulouse) OPERATION RUE NEUVE GRAND TERRE 13930 AUREILLE	DATE 15/04/2026 RÉVISEUR 1/50 TITRE DU PLAN PLANS COUPES FACADES VILLAS 4 et 5 PMR
		A.P.S. P.C. D.C.E. MARQUES	101