



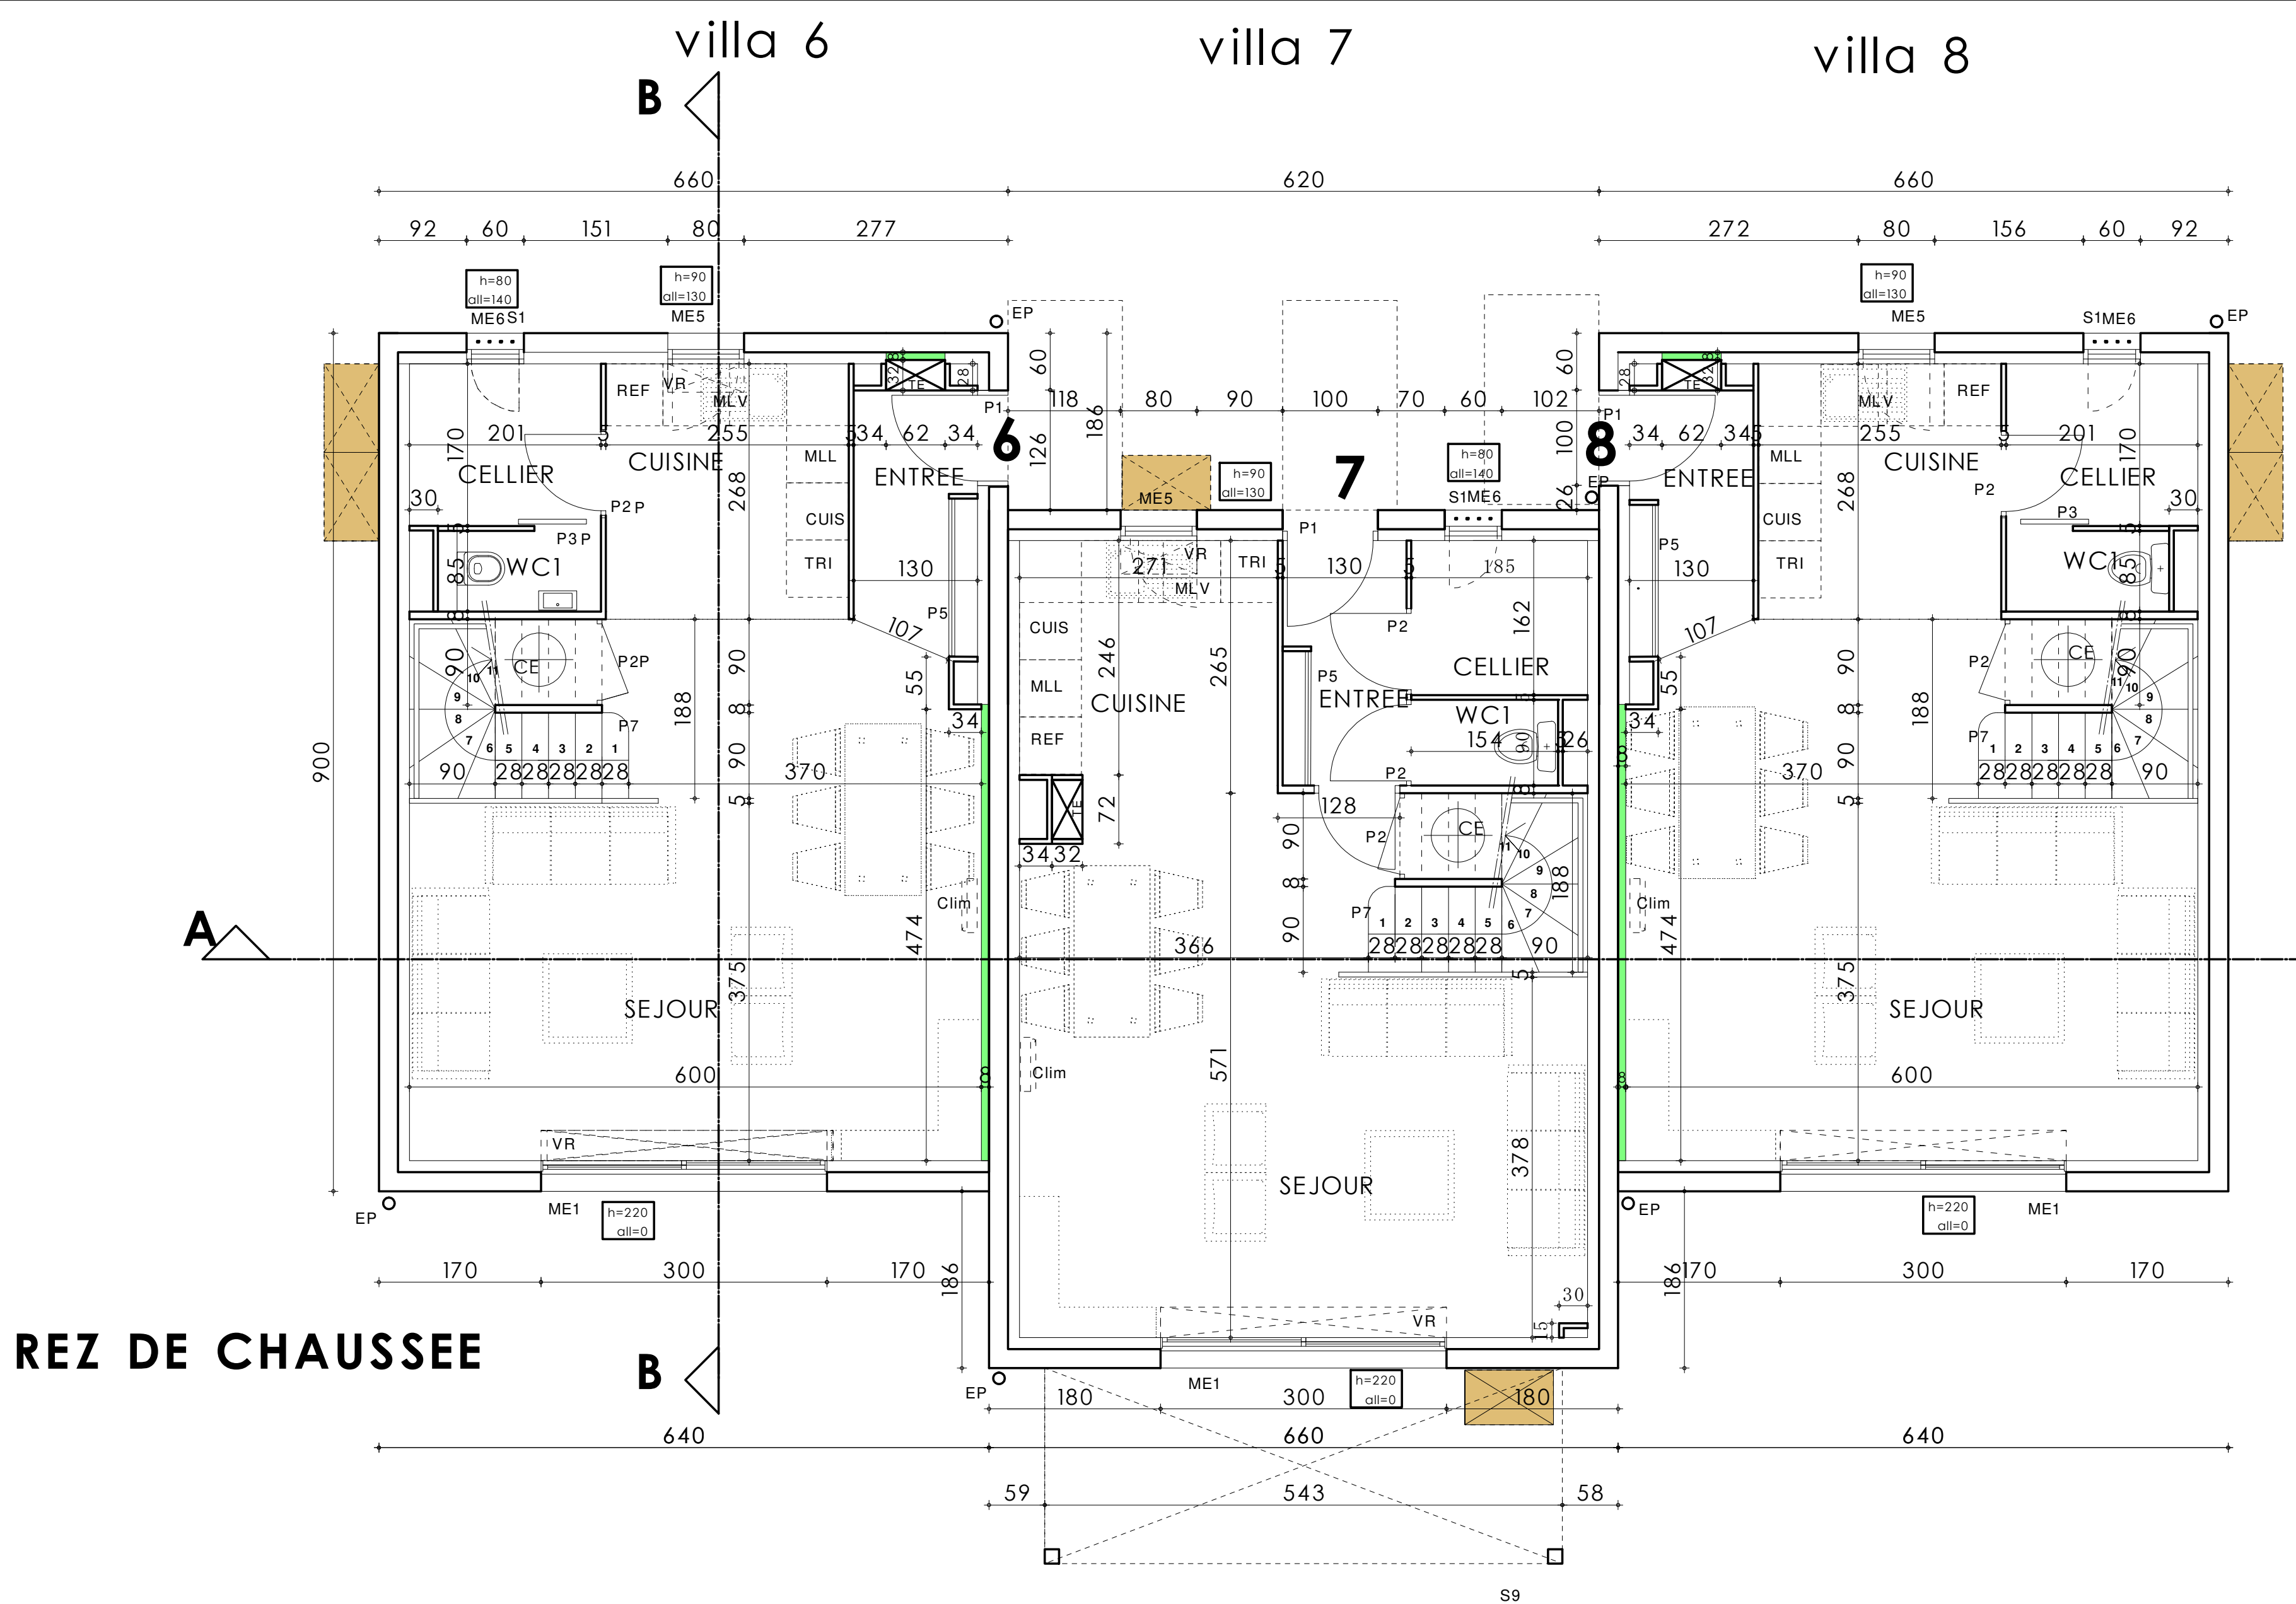


REZ DE CHAUSSEE

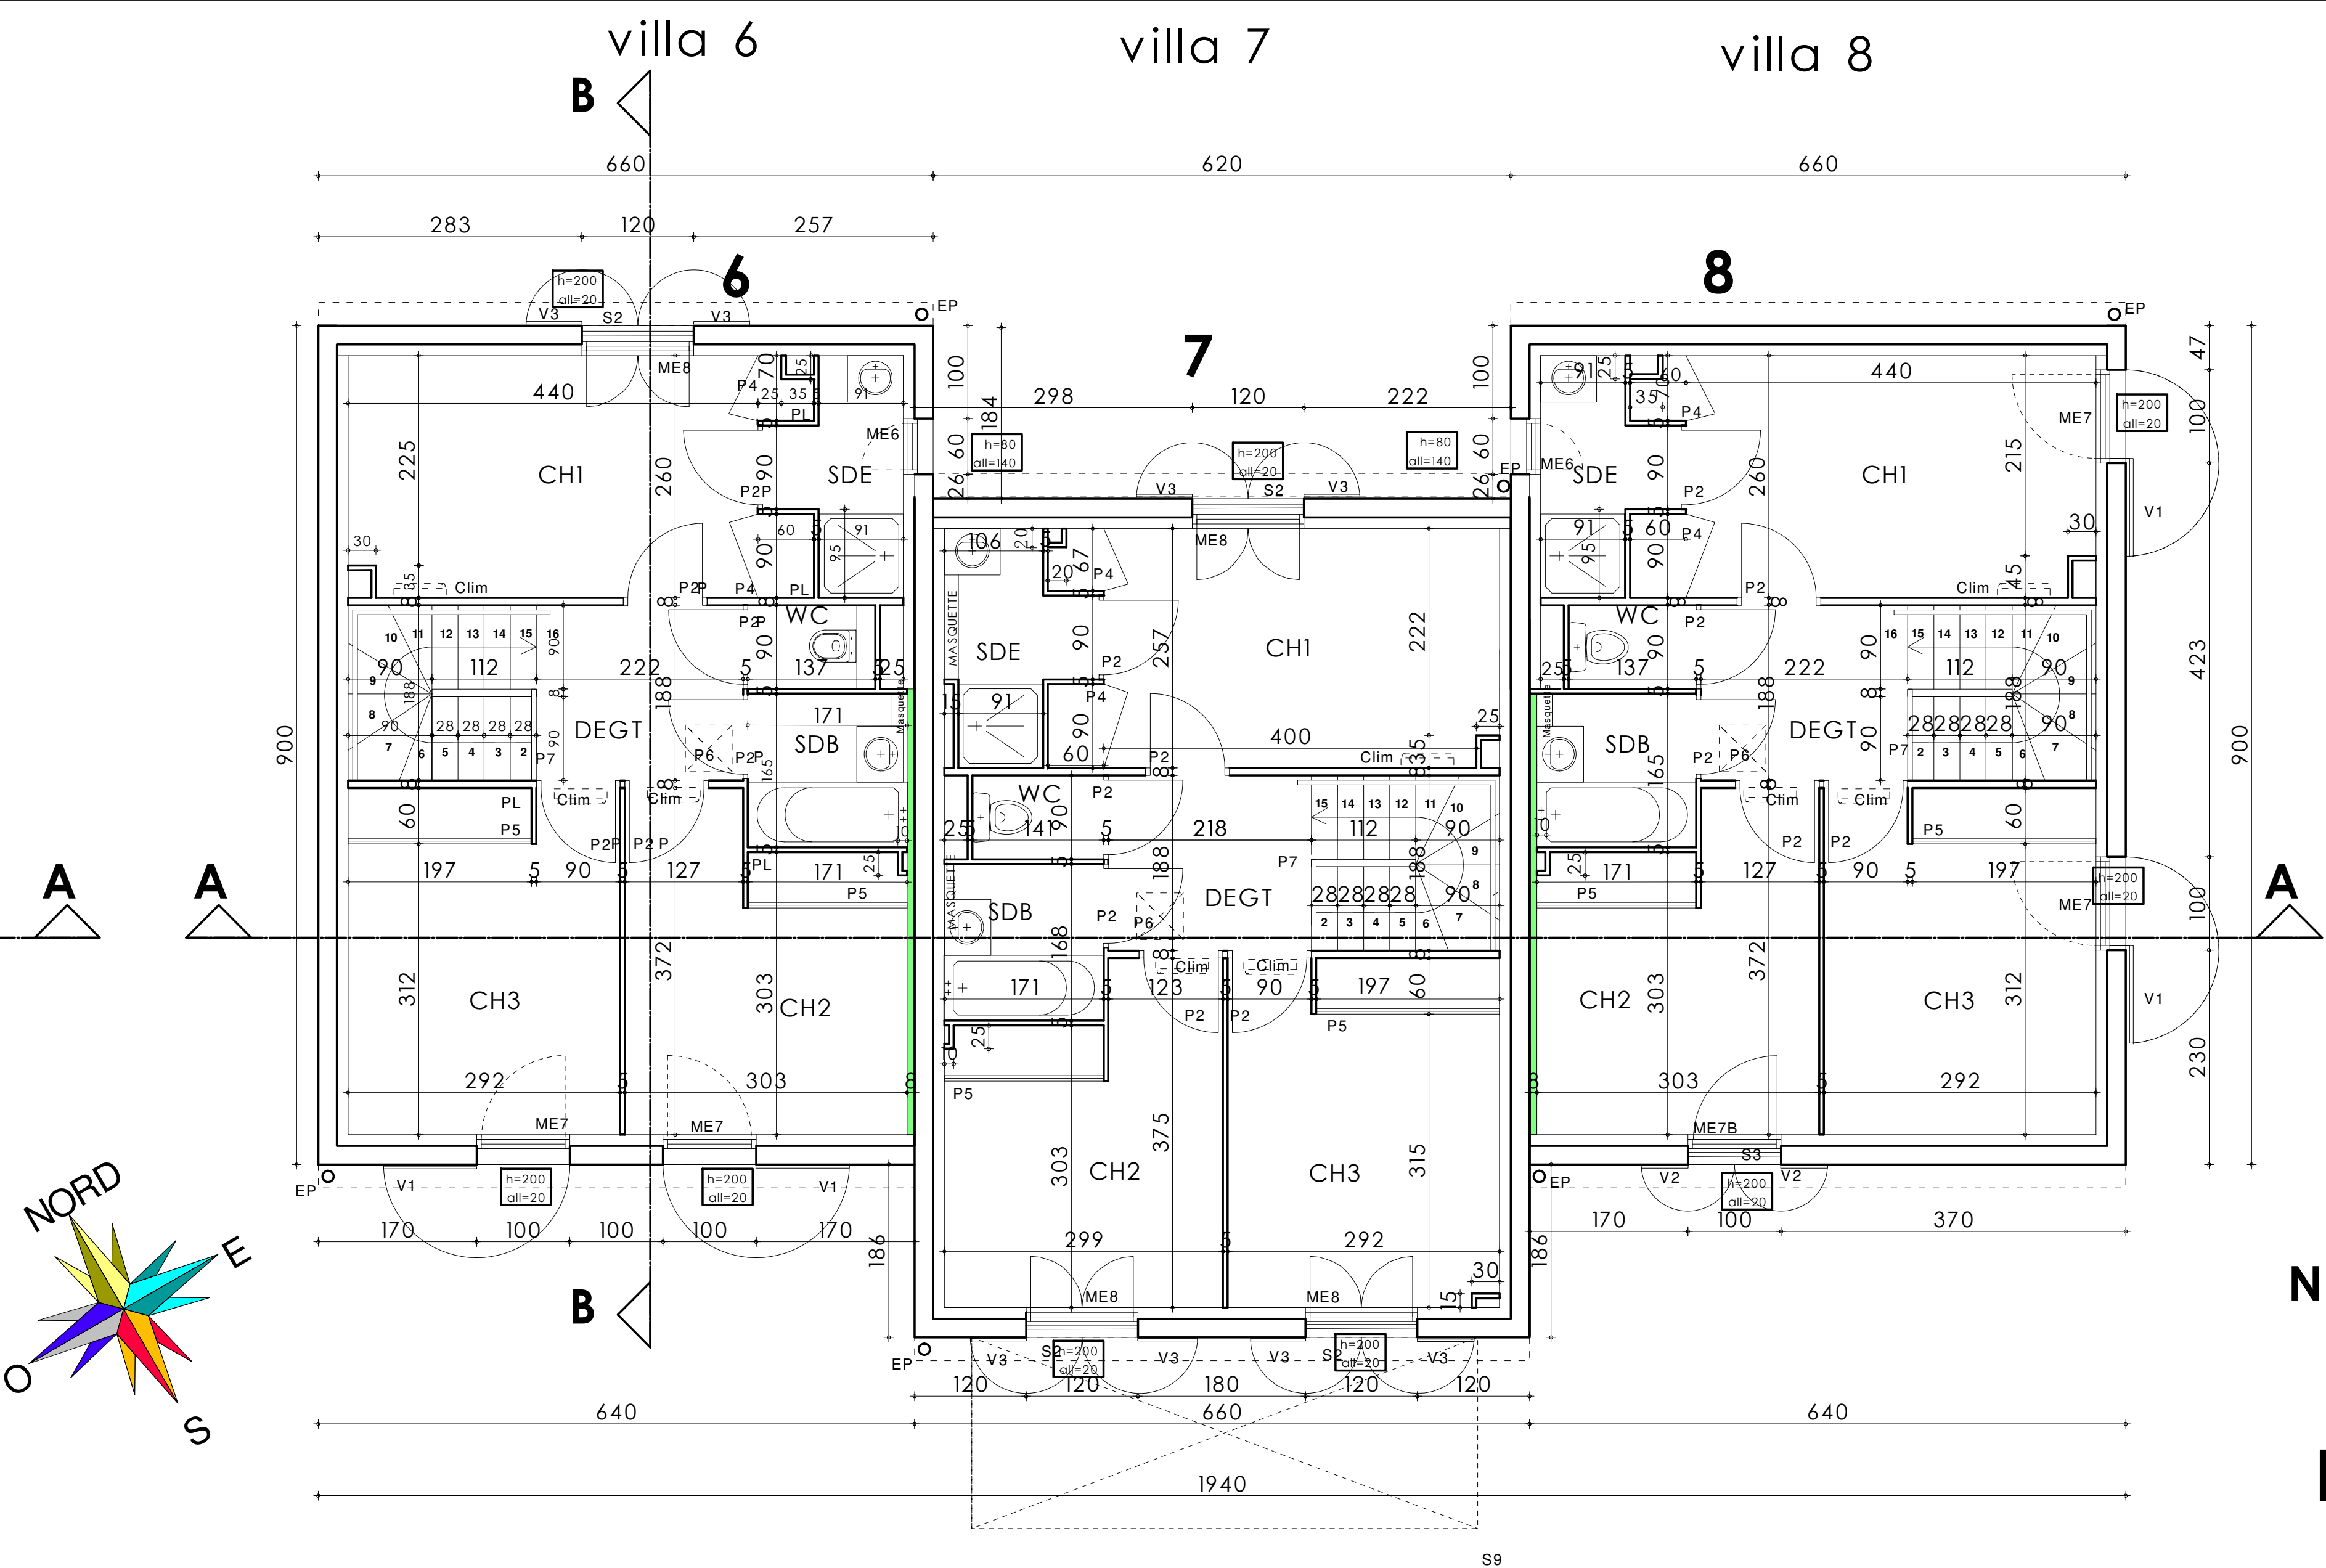


NIVEAU 1

PLAN DE NIVEAU 1/50

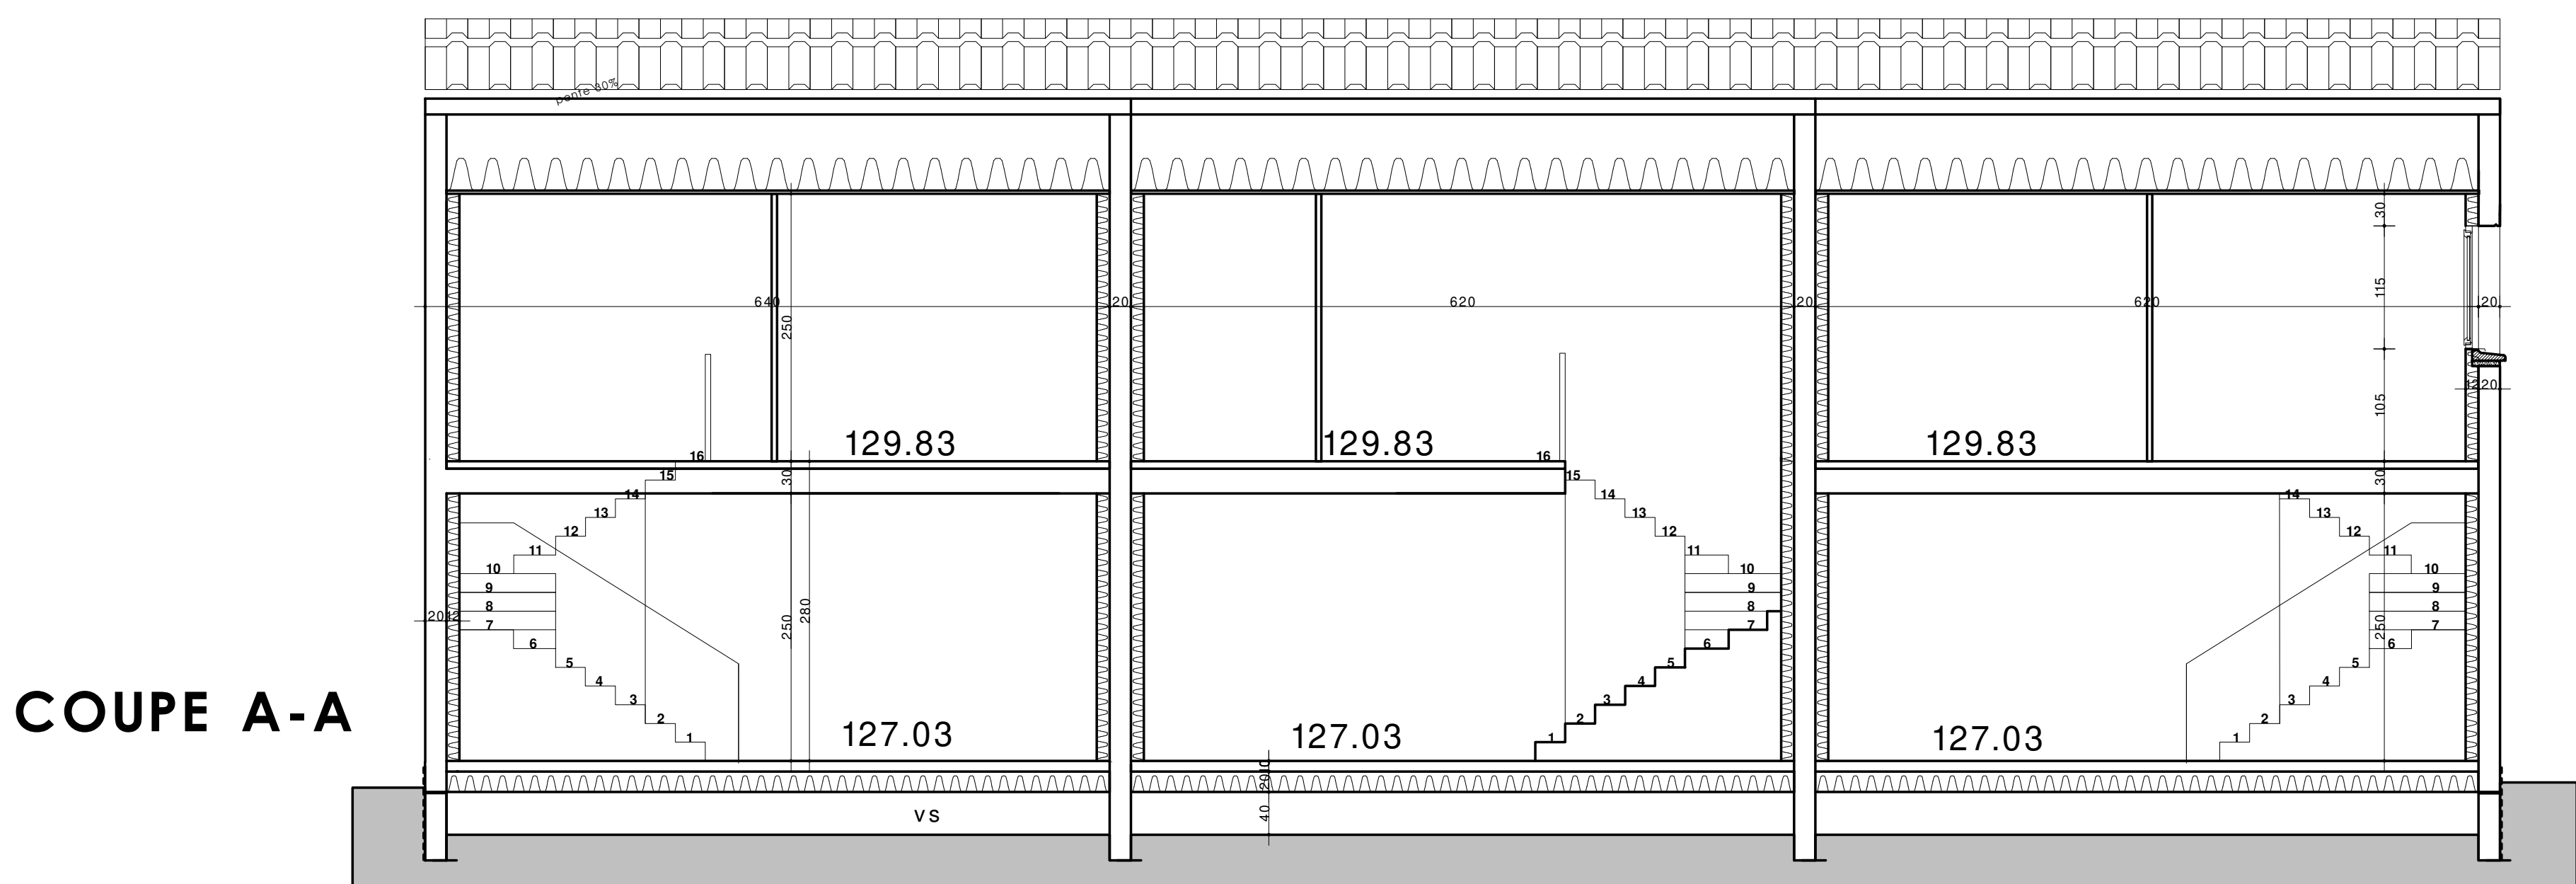

COUPE A-A

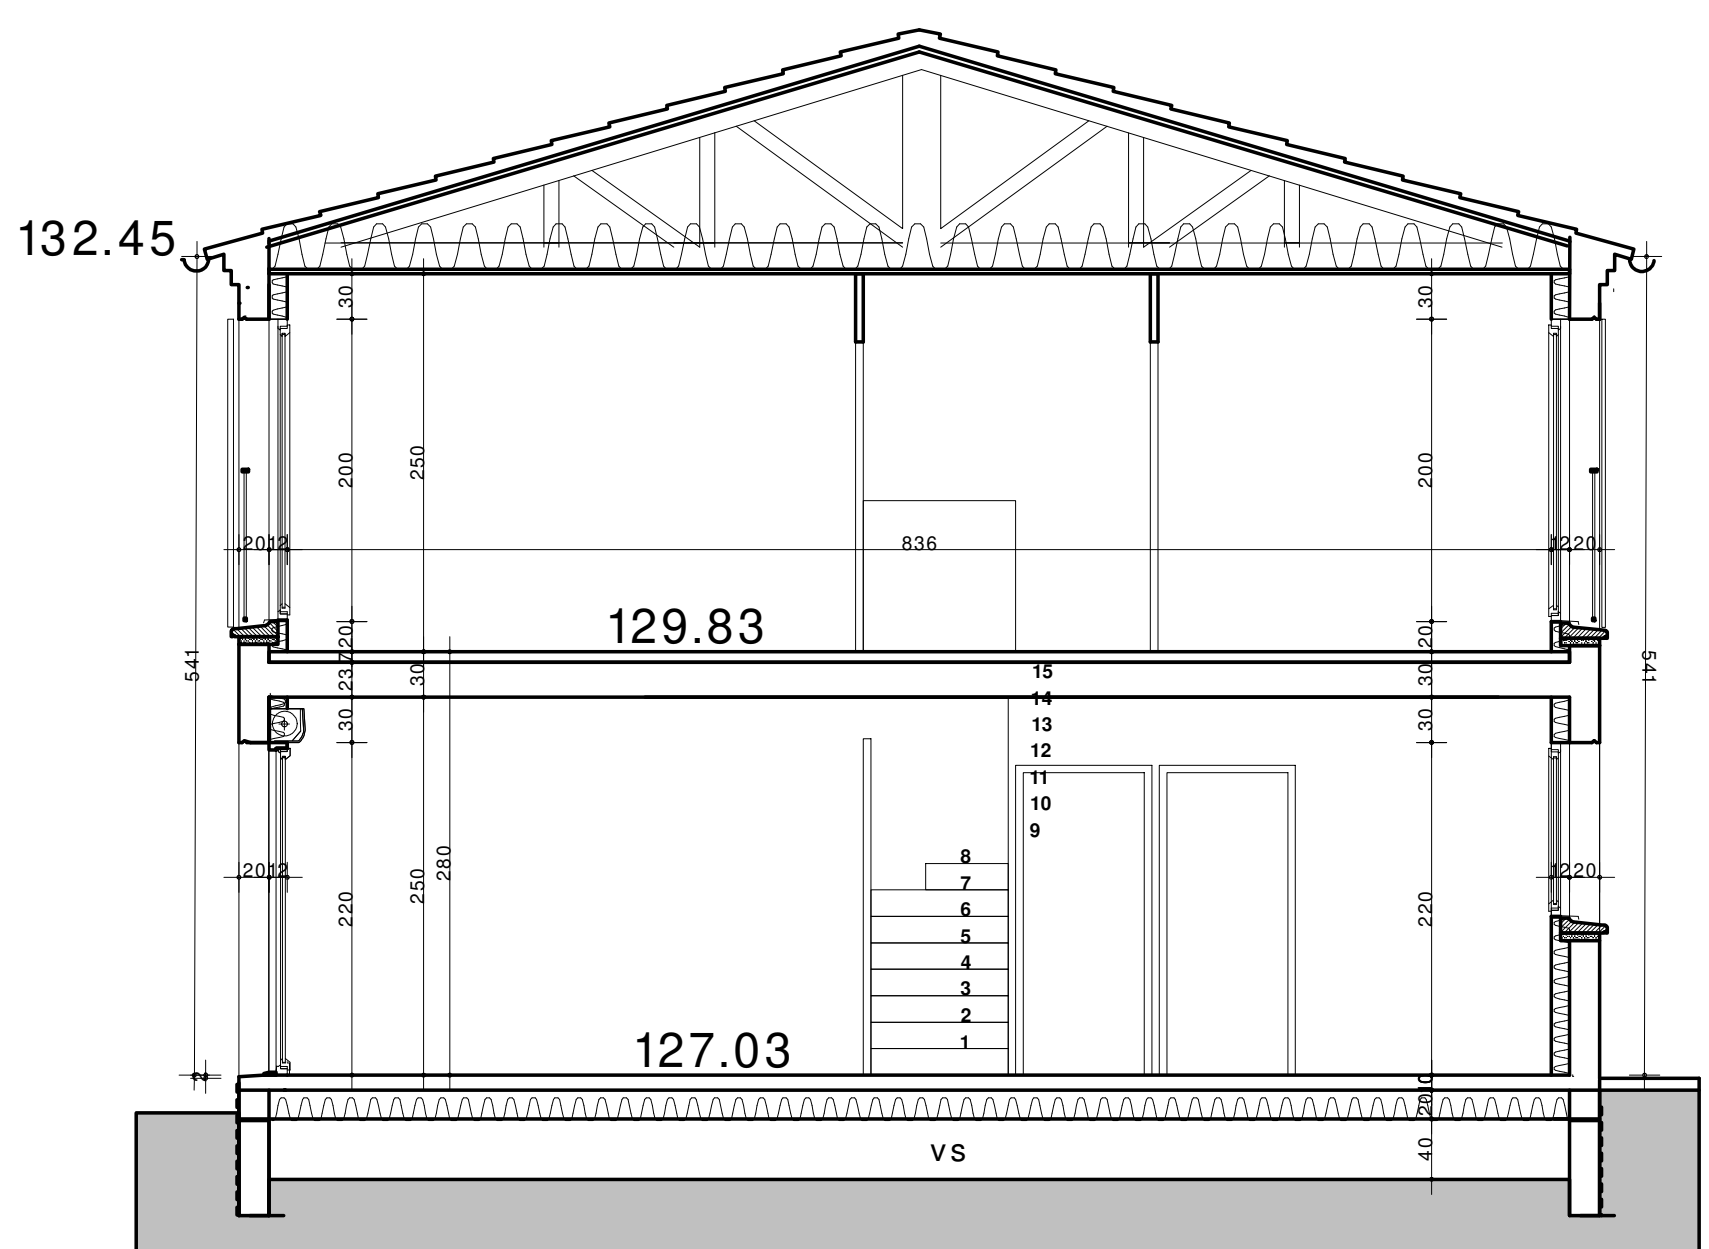


COUPE B-B

COUPES 1/50

LEGENDE

- Coffre volet roulant
- Faux plafond
- Espace de manoeuvre 220X120 devant la porte d'entrée
- Espace de manoeuvre 80X130 sanitaire
- Aire de rotation PMR
- GTL cf détail technique
- Isolant acoustique
- Cache de l'unité extérieure de climatisation
- Unités intérieure de climatisation

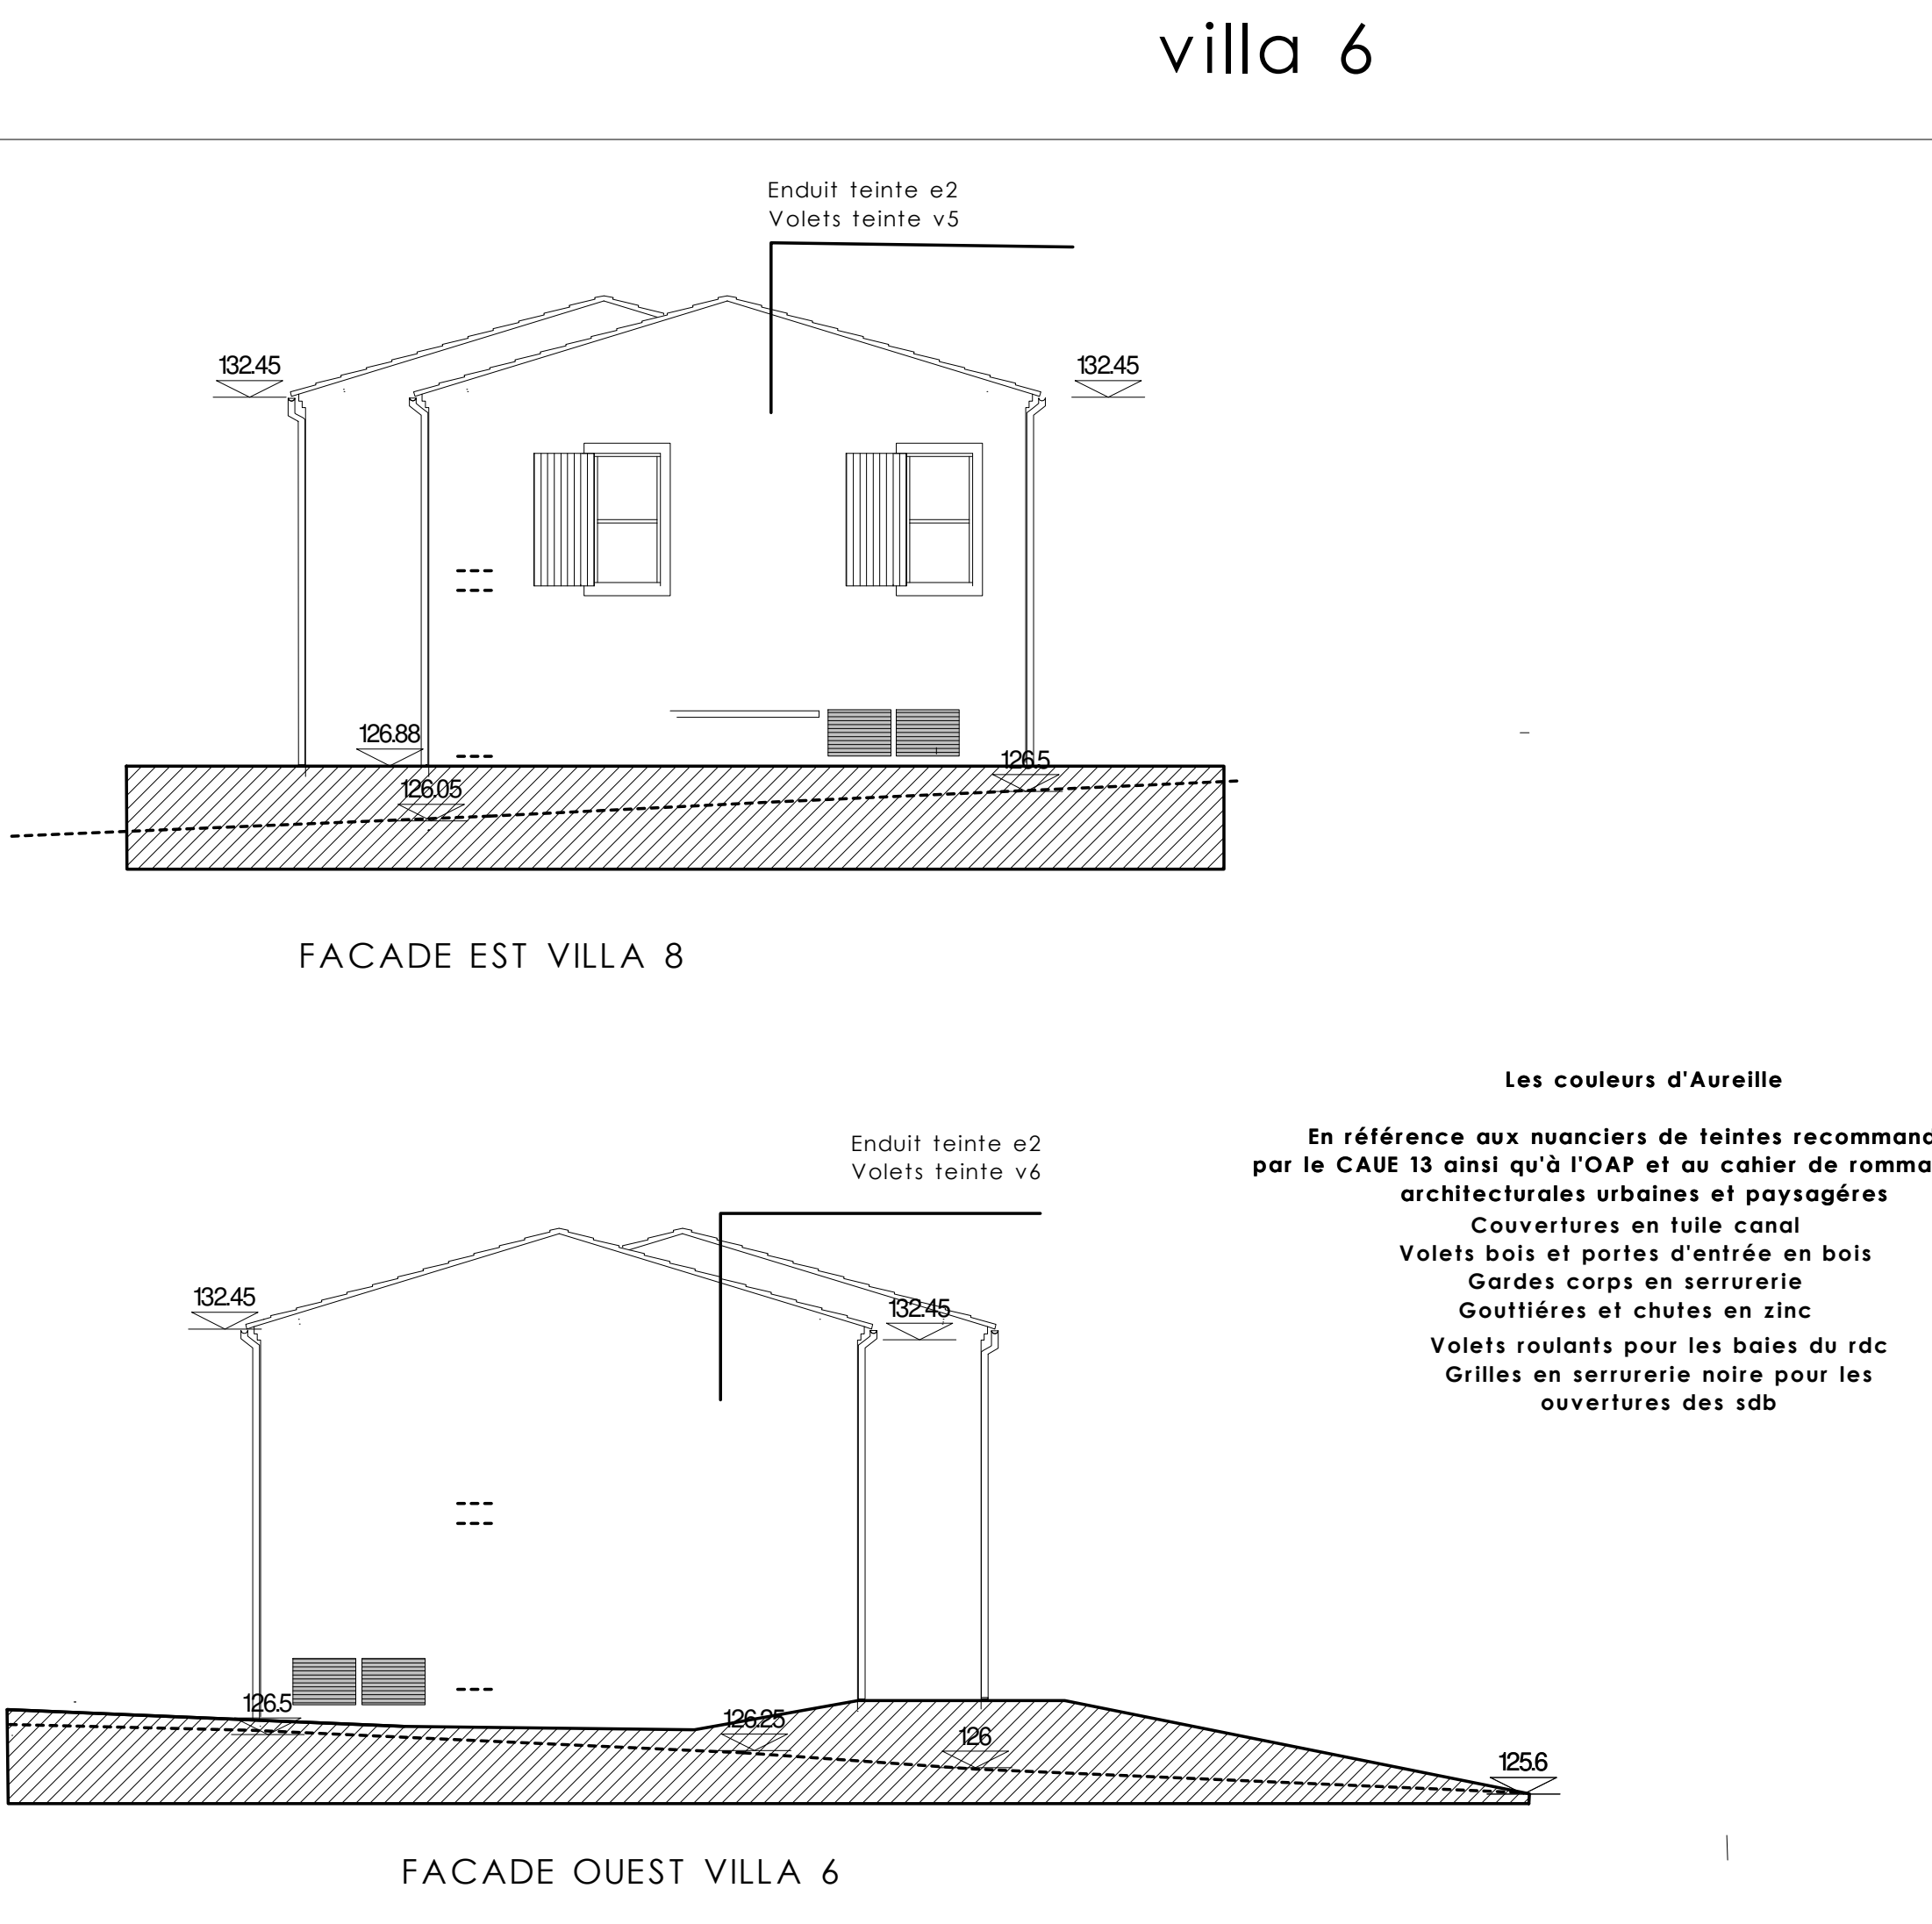

Les couleurs d'Aureille

En référence aux nuanciers de teintes recommandés par le CAUE 13 ainsi qu'à l'OAP et au cahier de recommandations architecturales urbaines et paysagères

- Couvertures en tuile canal
- Volets bois et portes d'entrée en bois
- Gardes corps en serrurerie
- Gouttières et chutes en zinc
- Volets roulants pour les baies du rdc
- Grilles en serrurerie noire pour les ouvertures des sdb

FACADES /100

GRANDE TERRE			
INDICE	DATE	MODIFICATIONS	
A	15/04/2026	MODIFICATIONS SUITE REUNION DCE	
B	29/06/2026	SUPPRESSION LAVE MAIN DANS LES VILLAS COUTS MAITRISES	
C	06/07/2026	MODIFICATION TE ET ISOLANT ACOUSTIQUE	
D			
E			
F			
G			
H			
I			
J			
K			
L			
ARCHITECTES M. CHAUVET A.C. CARNAZZA ARCHITECTES D.P.L.G. Entrepreneurs Individuels 40 rue FARGES 13008 MARSEILLE P.L.Chaudet@grandterre.fr A.C.Carnazza@grandterre.fr		MATRE D'OUVRAGE SCCV GRANDE TERRE (SIRET 942 743 709 R.C.S. Toulouse)	DATE 15/04/2026 P.C. 1/50 1/100 A.P.S. D.C.E. MARCHES
OPERATION RUE NEUVE GRAND TERRE 13930 AUREILLE		TITRE DU PLAN PLANS COUPES FACADES VILLAS 6 A 8 NON PMR	102