

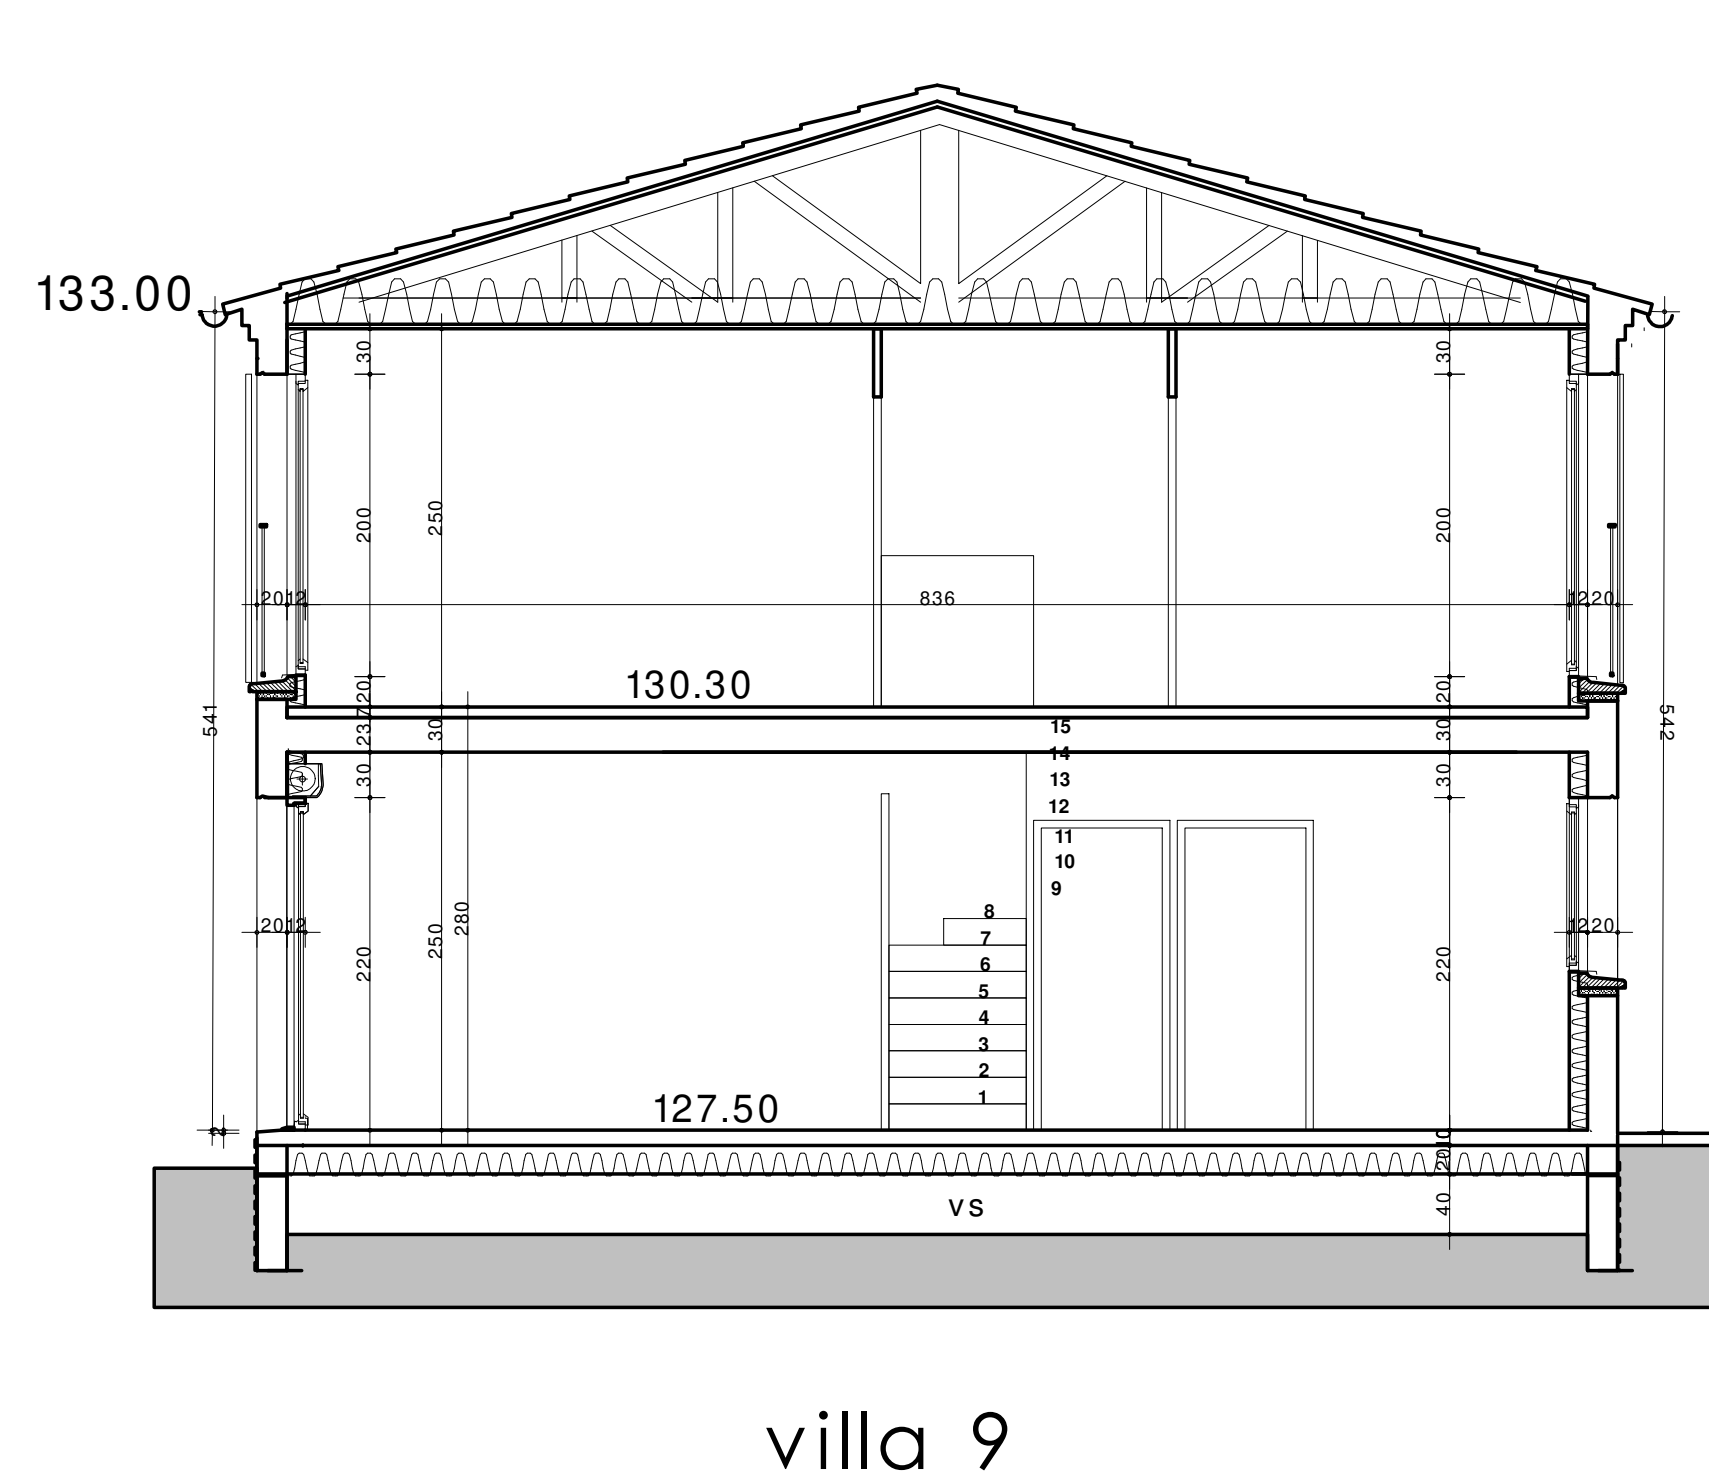
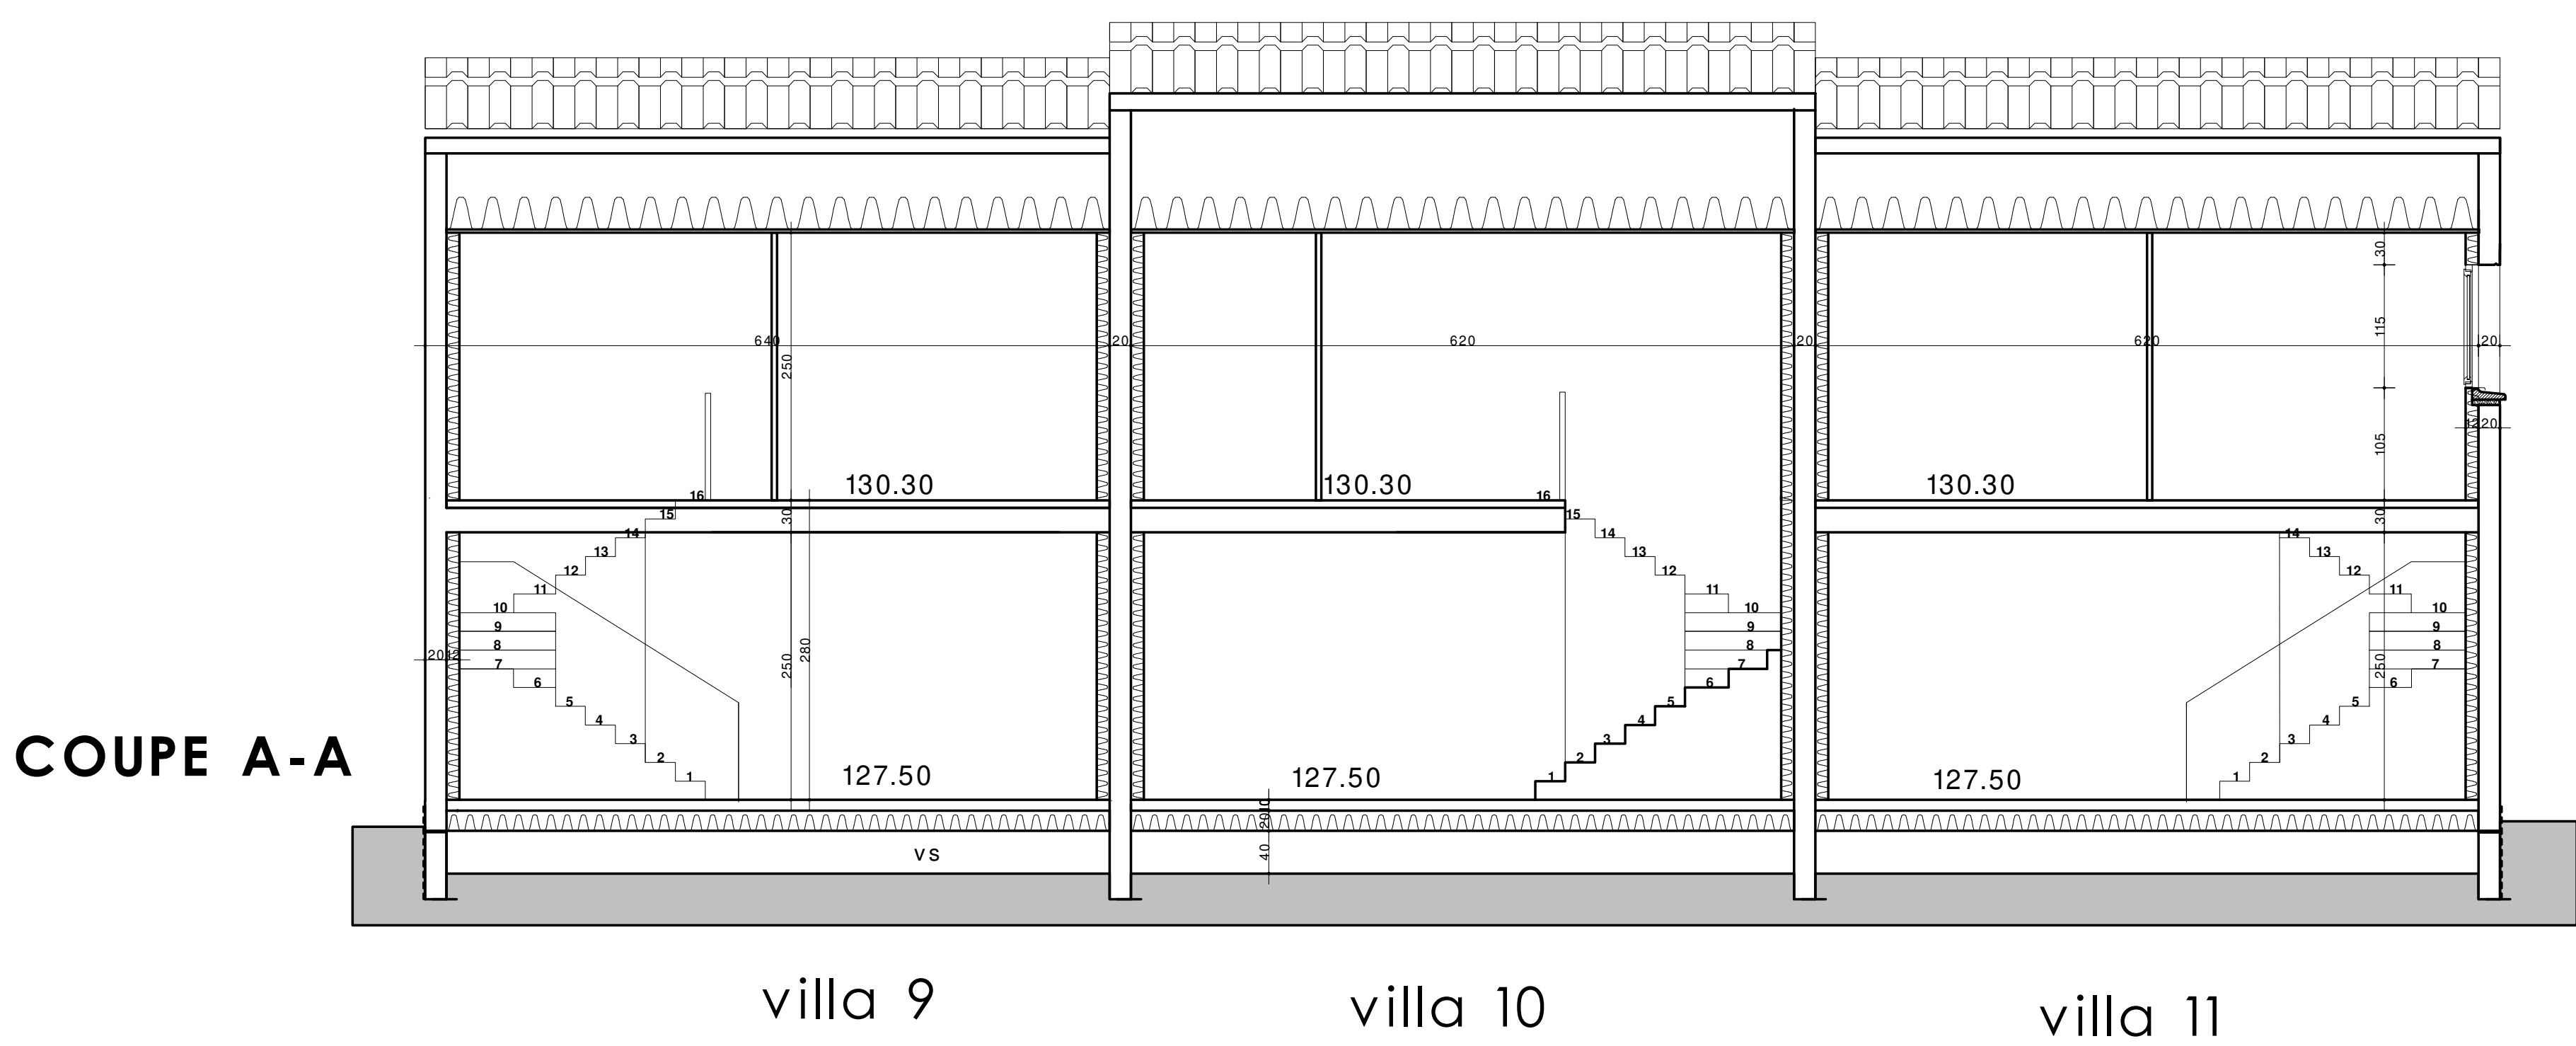
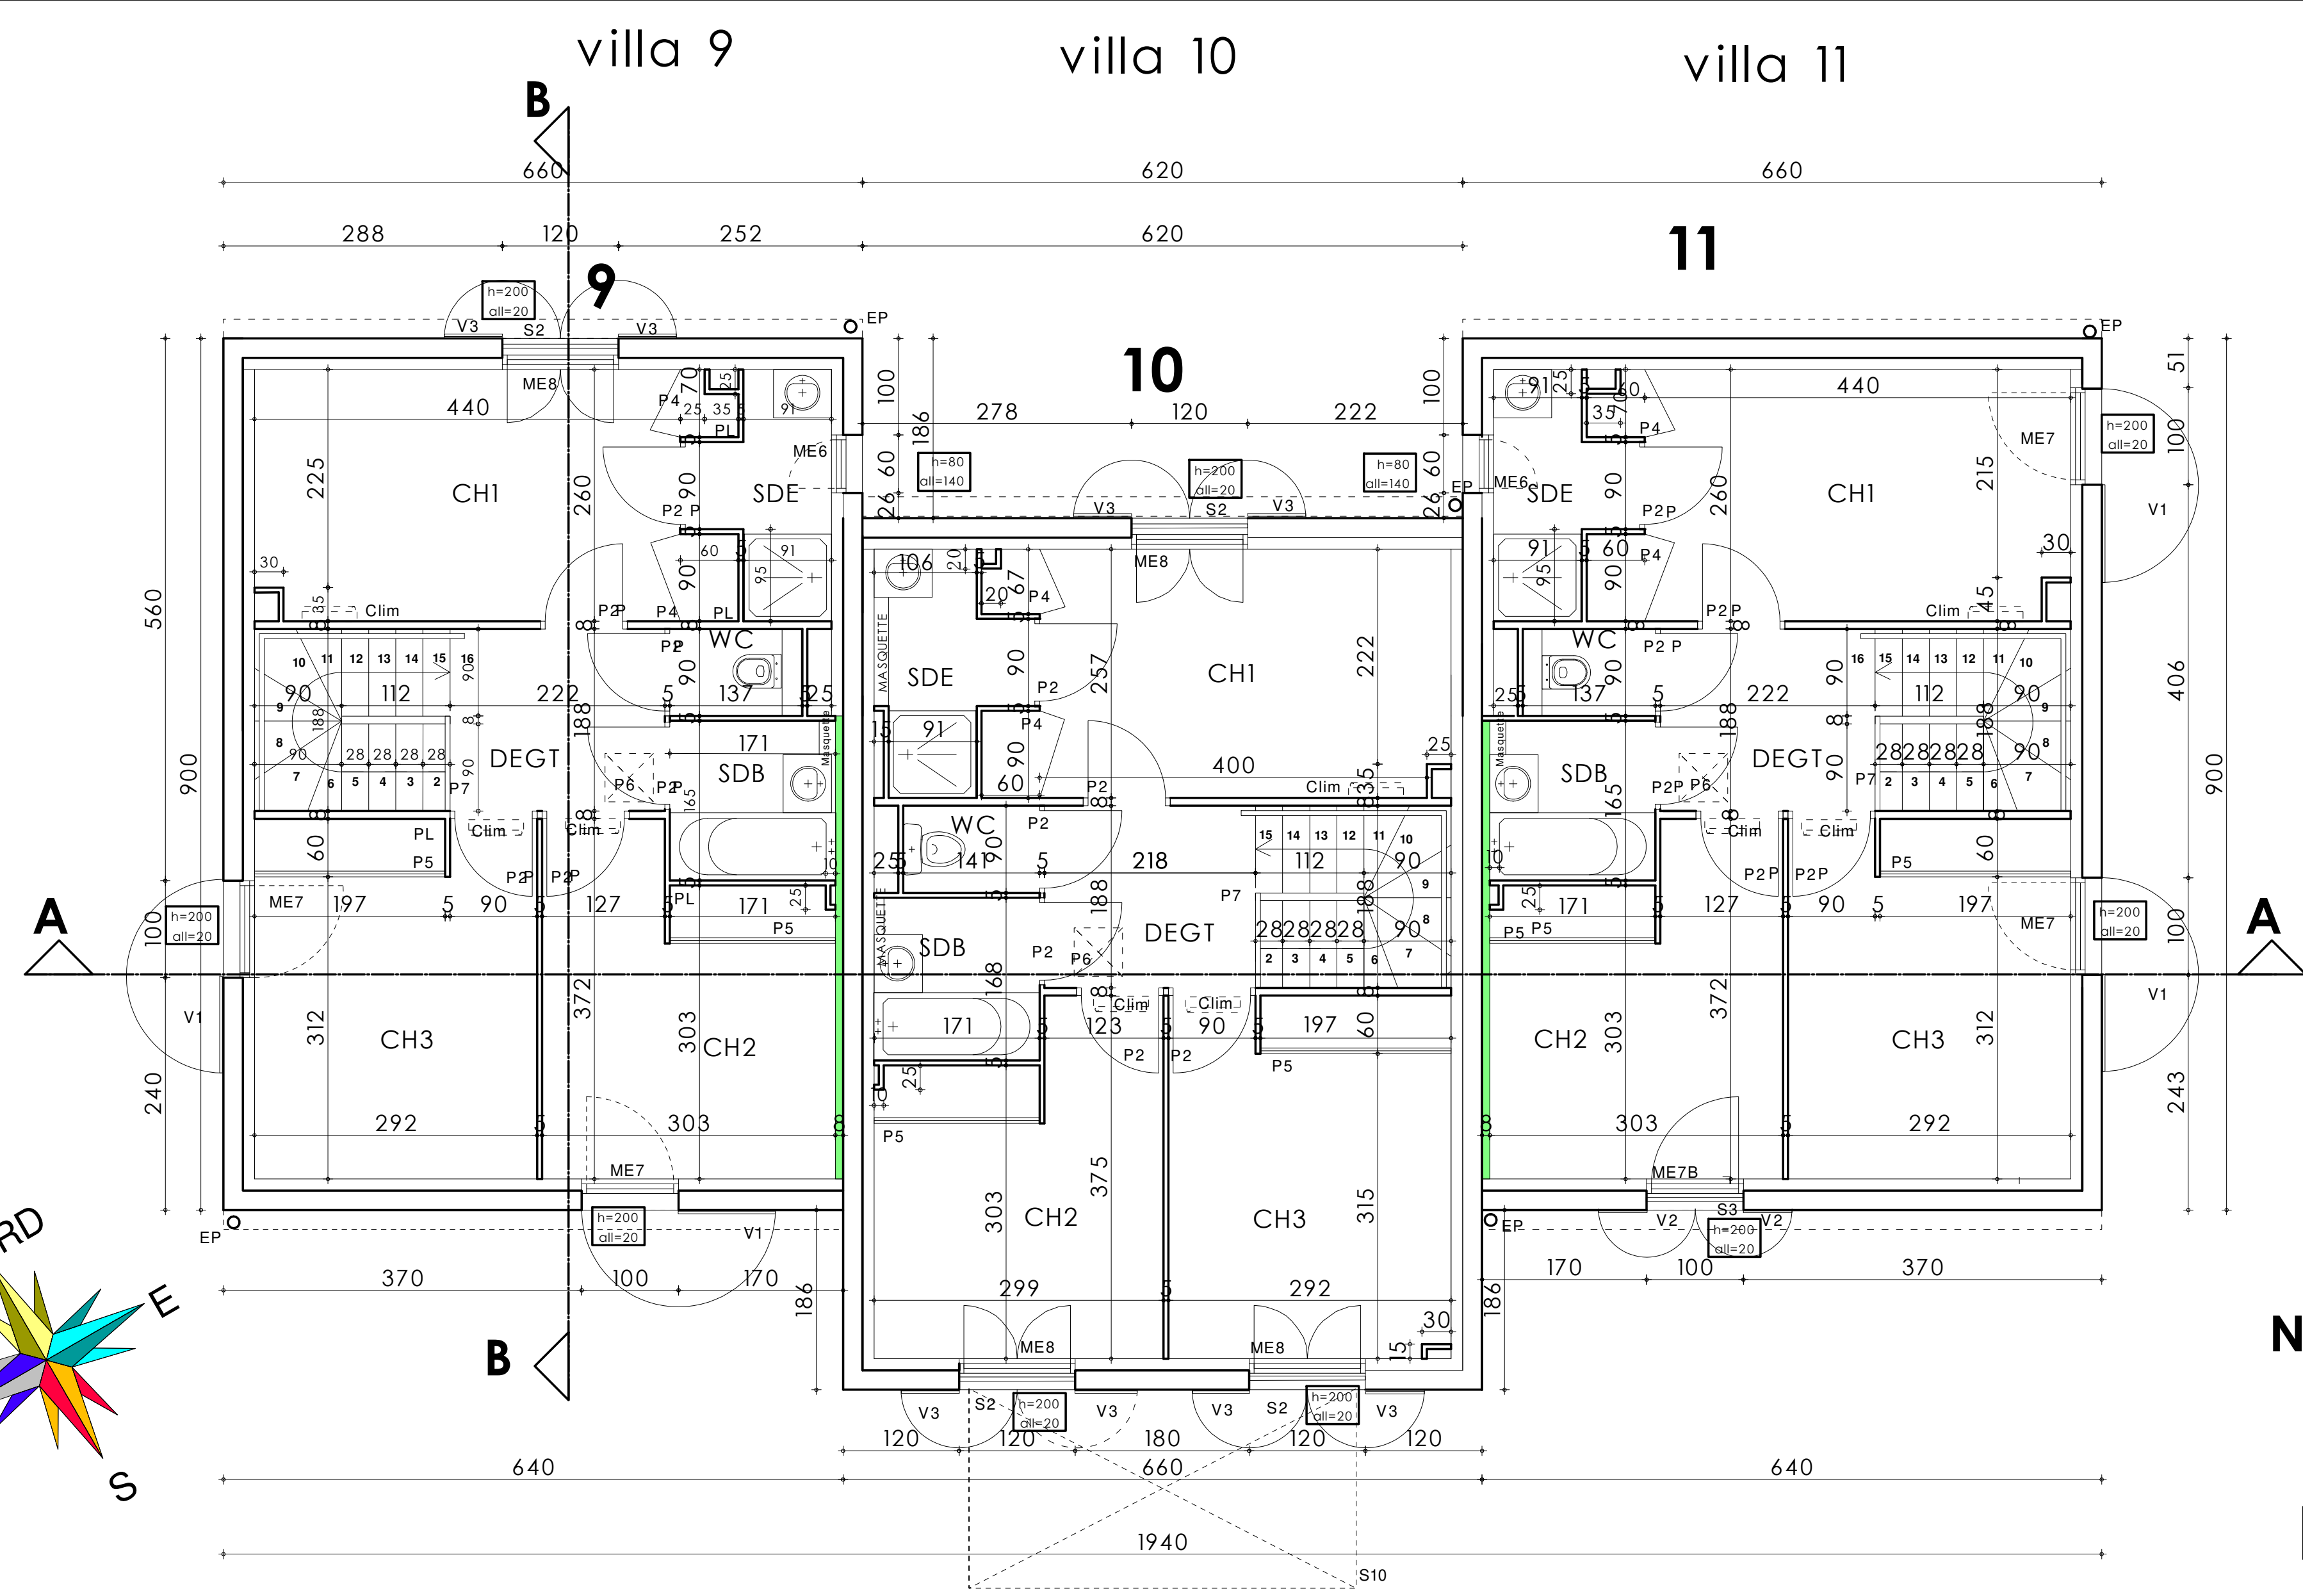


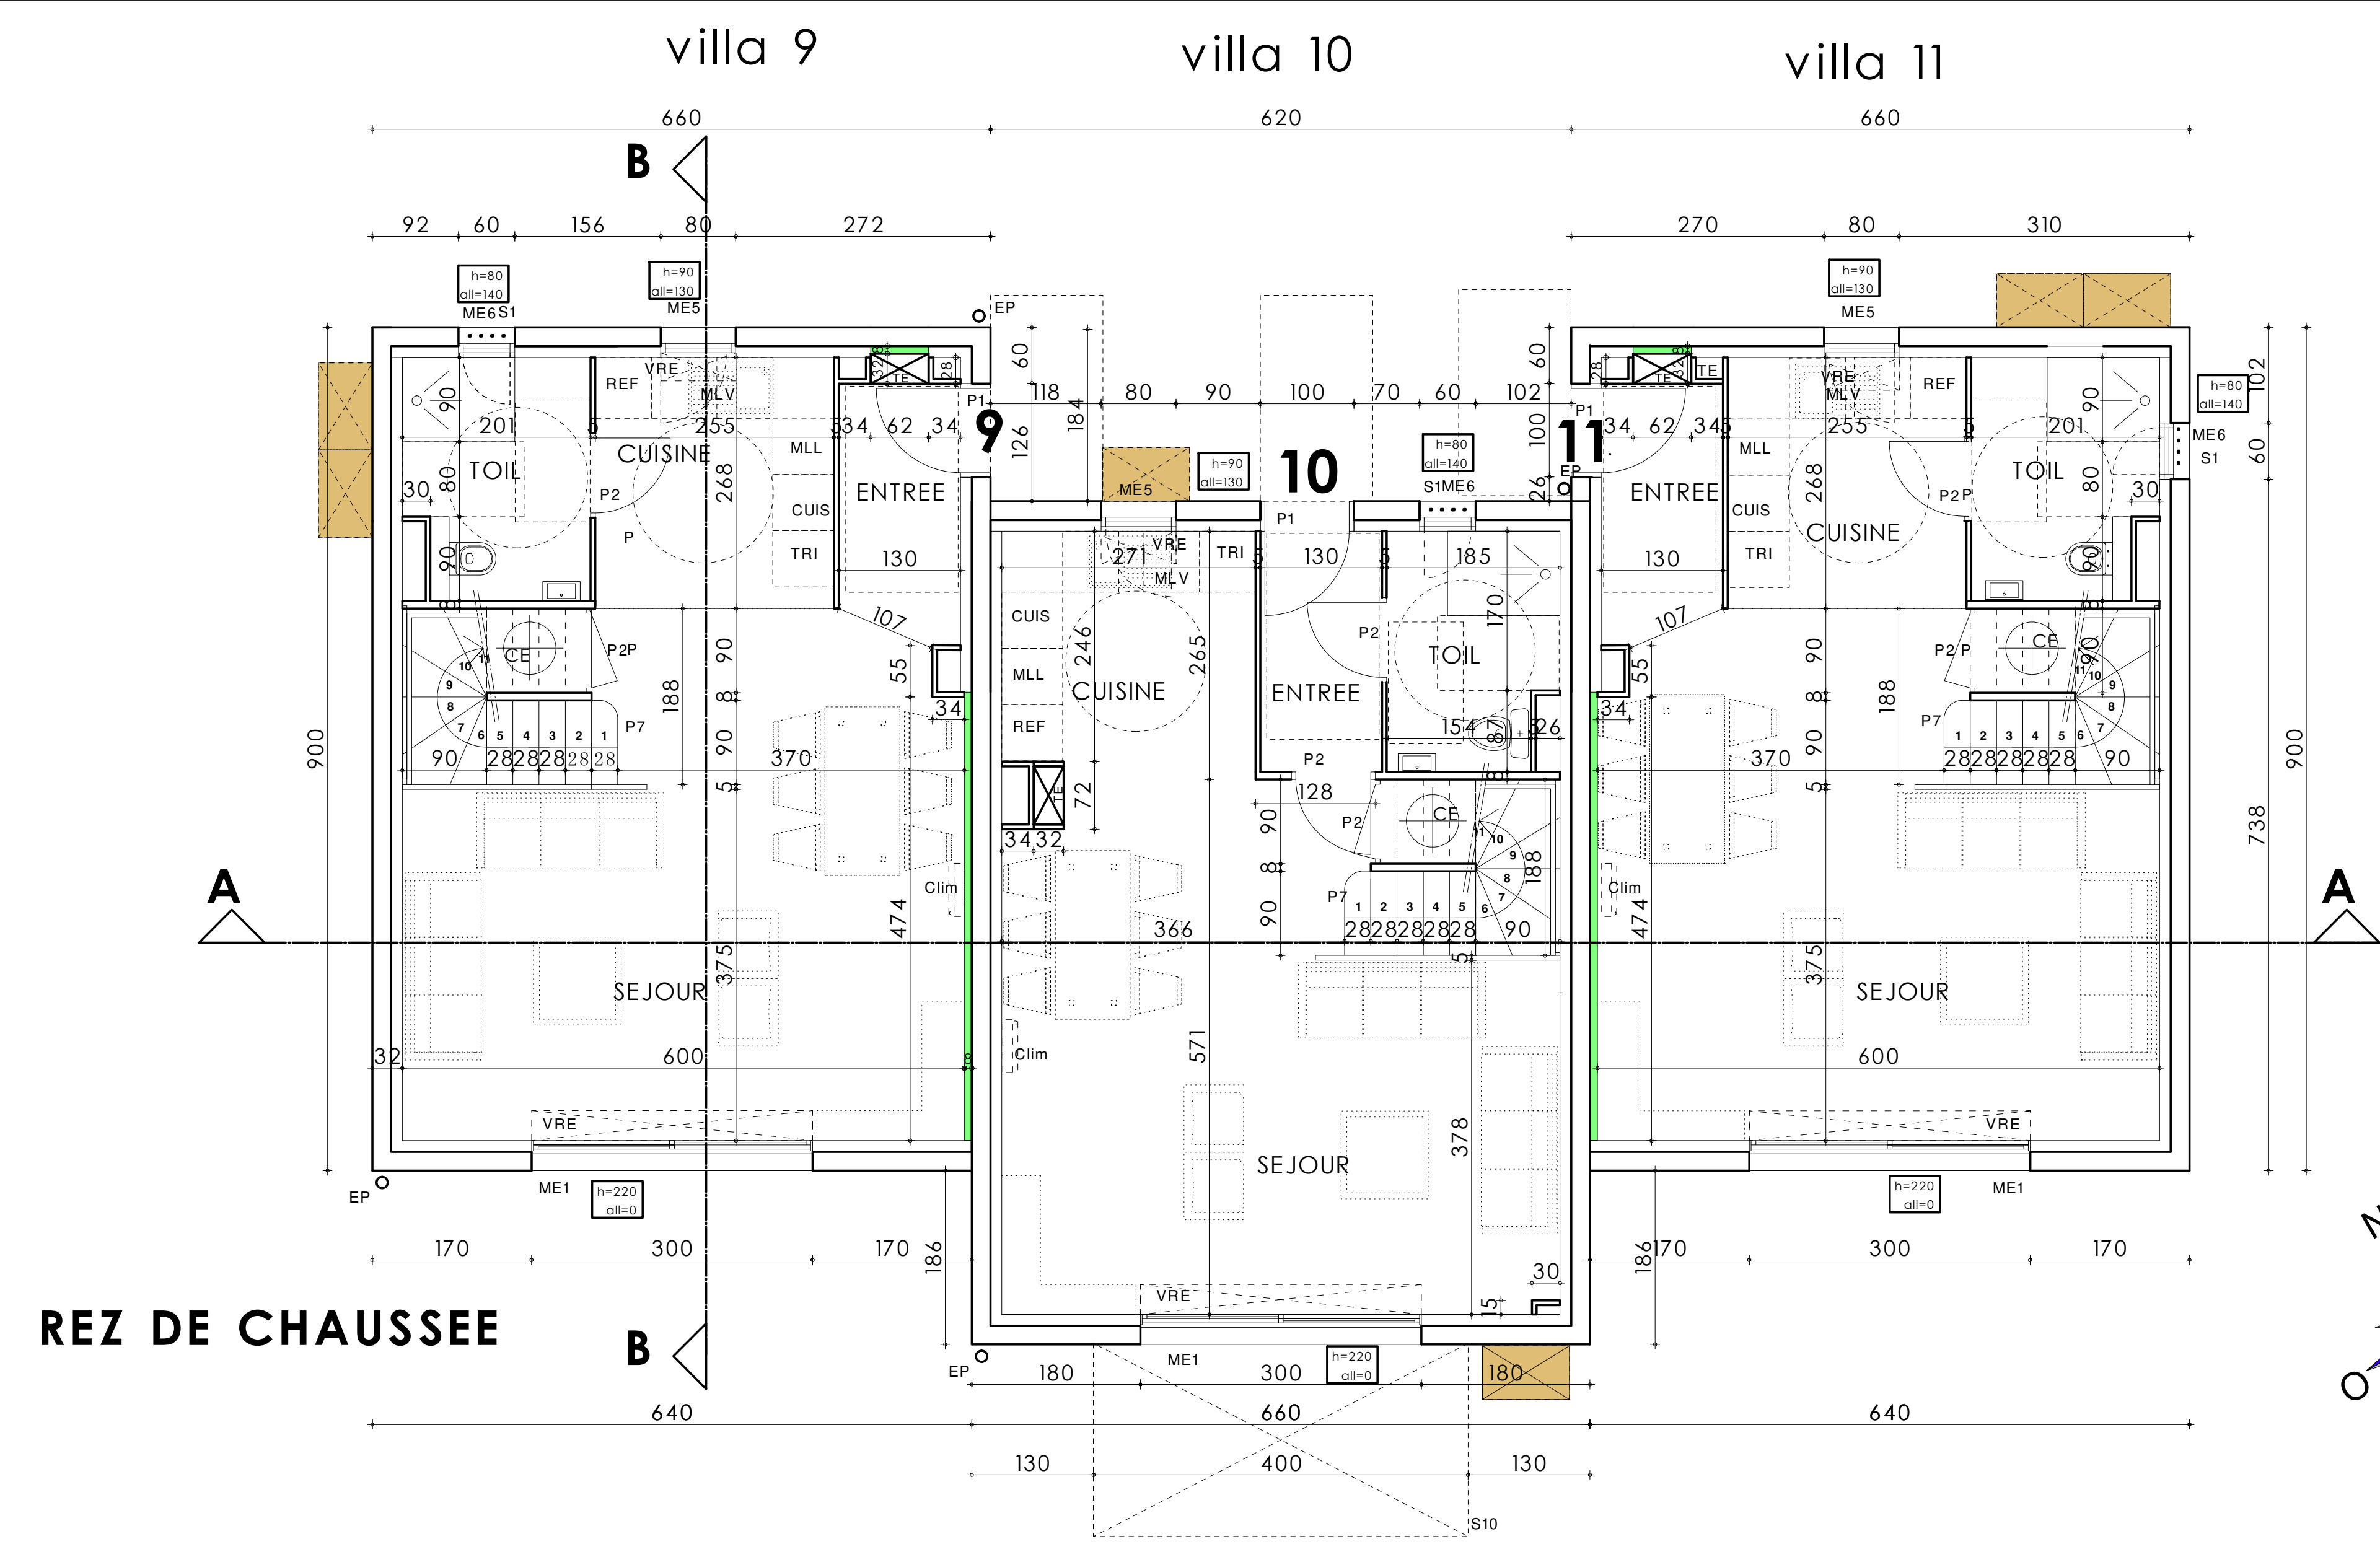

COUPES 1/50

LEGENDE

- Coffre volet roulant
- Faux plafond
- Espace de manoeuvre 220X120 devant la porte d'entrée
- Espace de manoeuvre 80X130 sanitaire
- Aire de rotation PMR
- GTL cf détail technique
- Isolant acoustique
- Cache de l'unité extérieure de climatisation
- Unités intérieure de climatisation

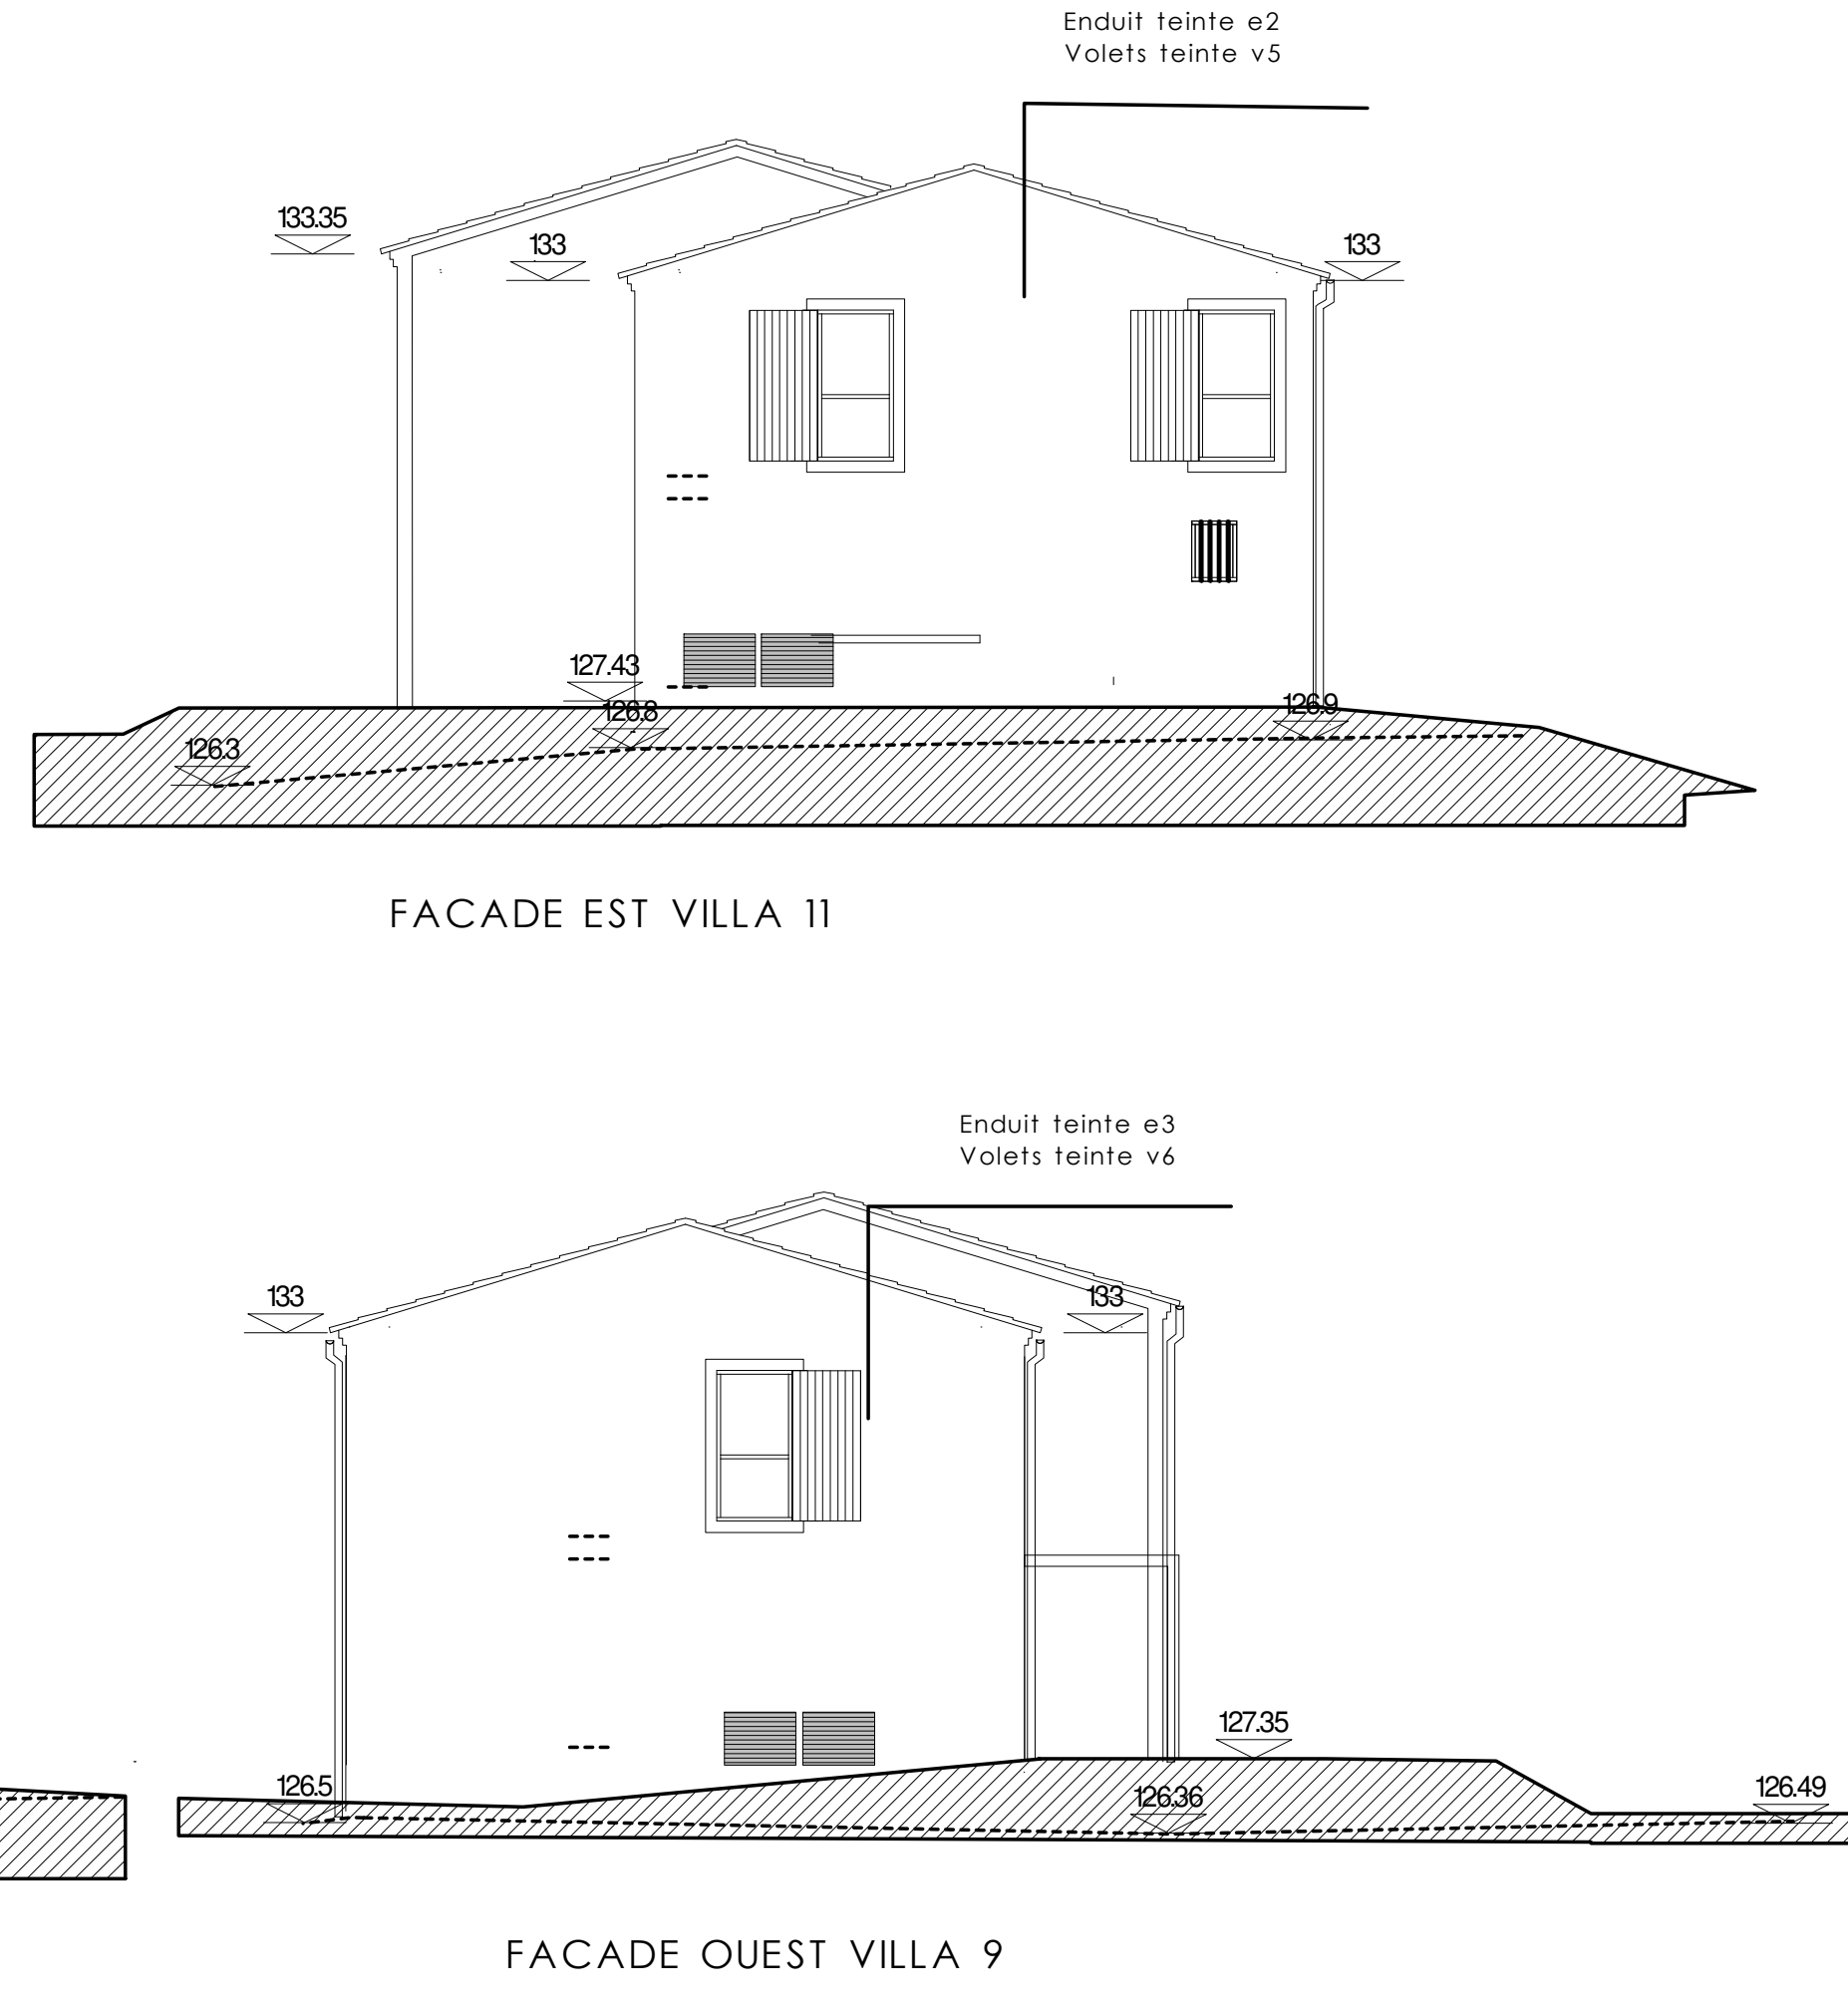

Les couleurs d'Aureille

En référence aux nuanciers de teintes recommandées par le CAUE 13 ainsi qu'à l'OAP et au cahier de recommandations architecturales urbaines et paysagères

Couvertures en tuile canal

Volets bois et portes d'entrée en bois

Gardes corps en serrurerie

Gouttières et chutes en zinc

Volets roulants pour les baies du rdc

Grilles en serrurerie noire pour les ouvertures des sdb

FACADES /100

GRANDE TERRE			
INDICE	DATE	MODIFICATIONS	
A	15/06/2026	MODIFICATIONS SUITE REUNION DCE	
B	29/06/2026	SUPPRESSION LAVE MAIN DANS LES VILLAS COUTS MAITRISES	
C	06/07/2026	MODIFICATION TE ET ISOLANT ACOUSTIQUE	
D			
E			
F			
G			
H			
I			
J			
K			
L			
ARCHITECTES M. CHAUVET A.C. CARNAZZA ARCHITECTES D.P.L.G. Entrepreneurs Individuels 40 rue FARGES 13008 MARSEILLE P.L.Chaudet@orange.fr A.C.Carnazza@orange.fr		MAITRE D'OUVRAGE SCCV GRANDE TERRE (SIRET 742 743 709 R.C.S. Toulouse) OPERATION RUE NEUVE GRAND TERRE 13930 AUREILLE	
DATE 15/04/2026 PROJETS 1/50 1/100		A.P.S. P.C. D.C.E. MARCHES	
TITRE DU PLAN PLANS COUPES FACADES VILLAS 9-10-11 PMR		103	