



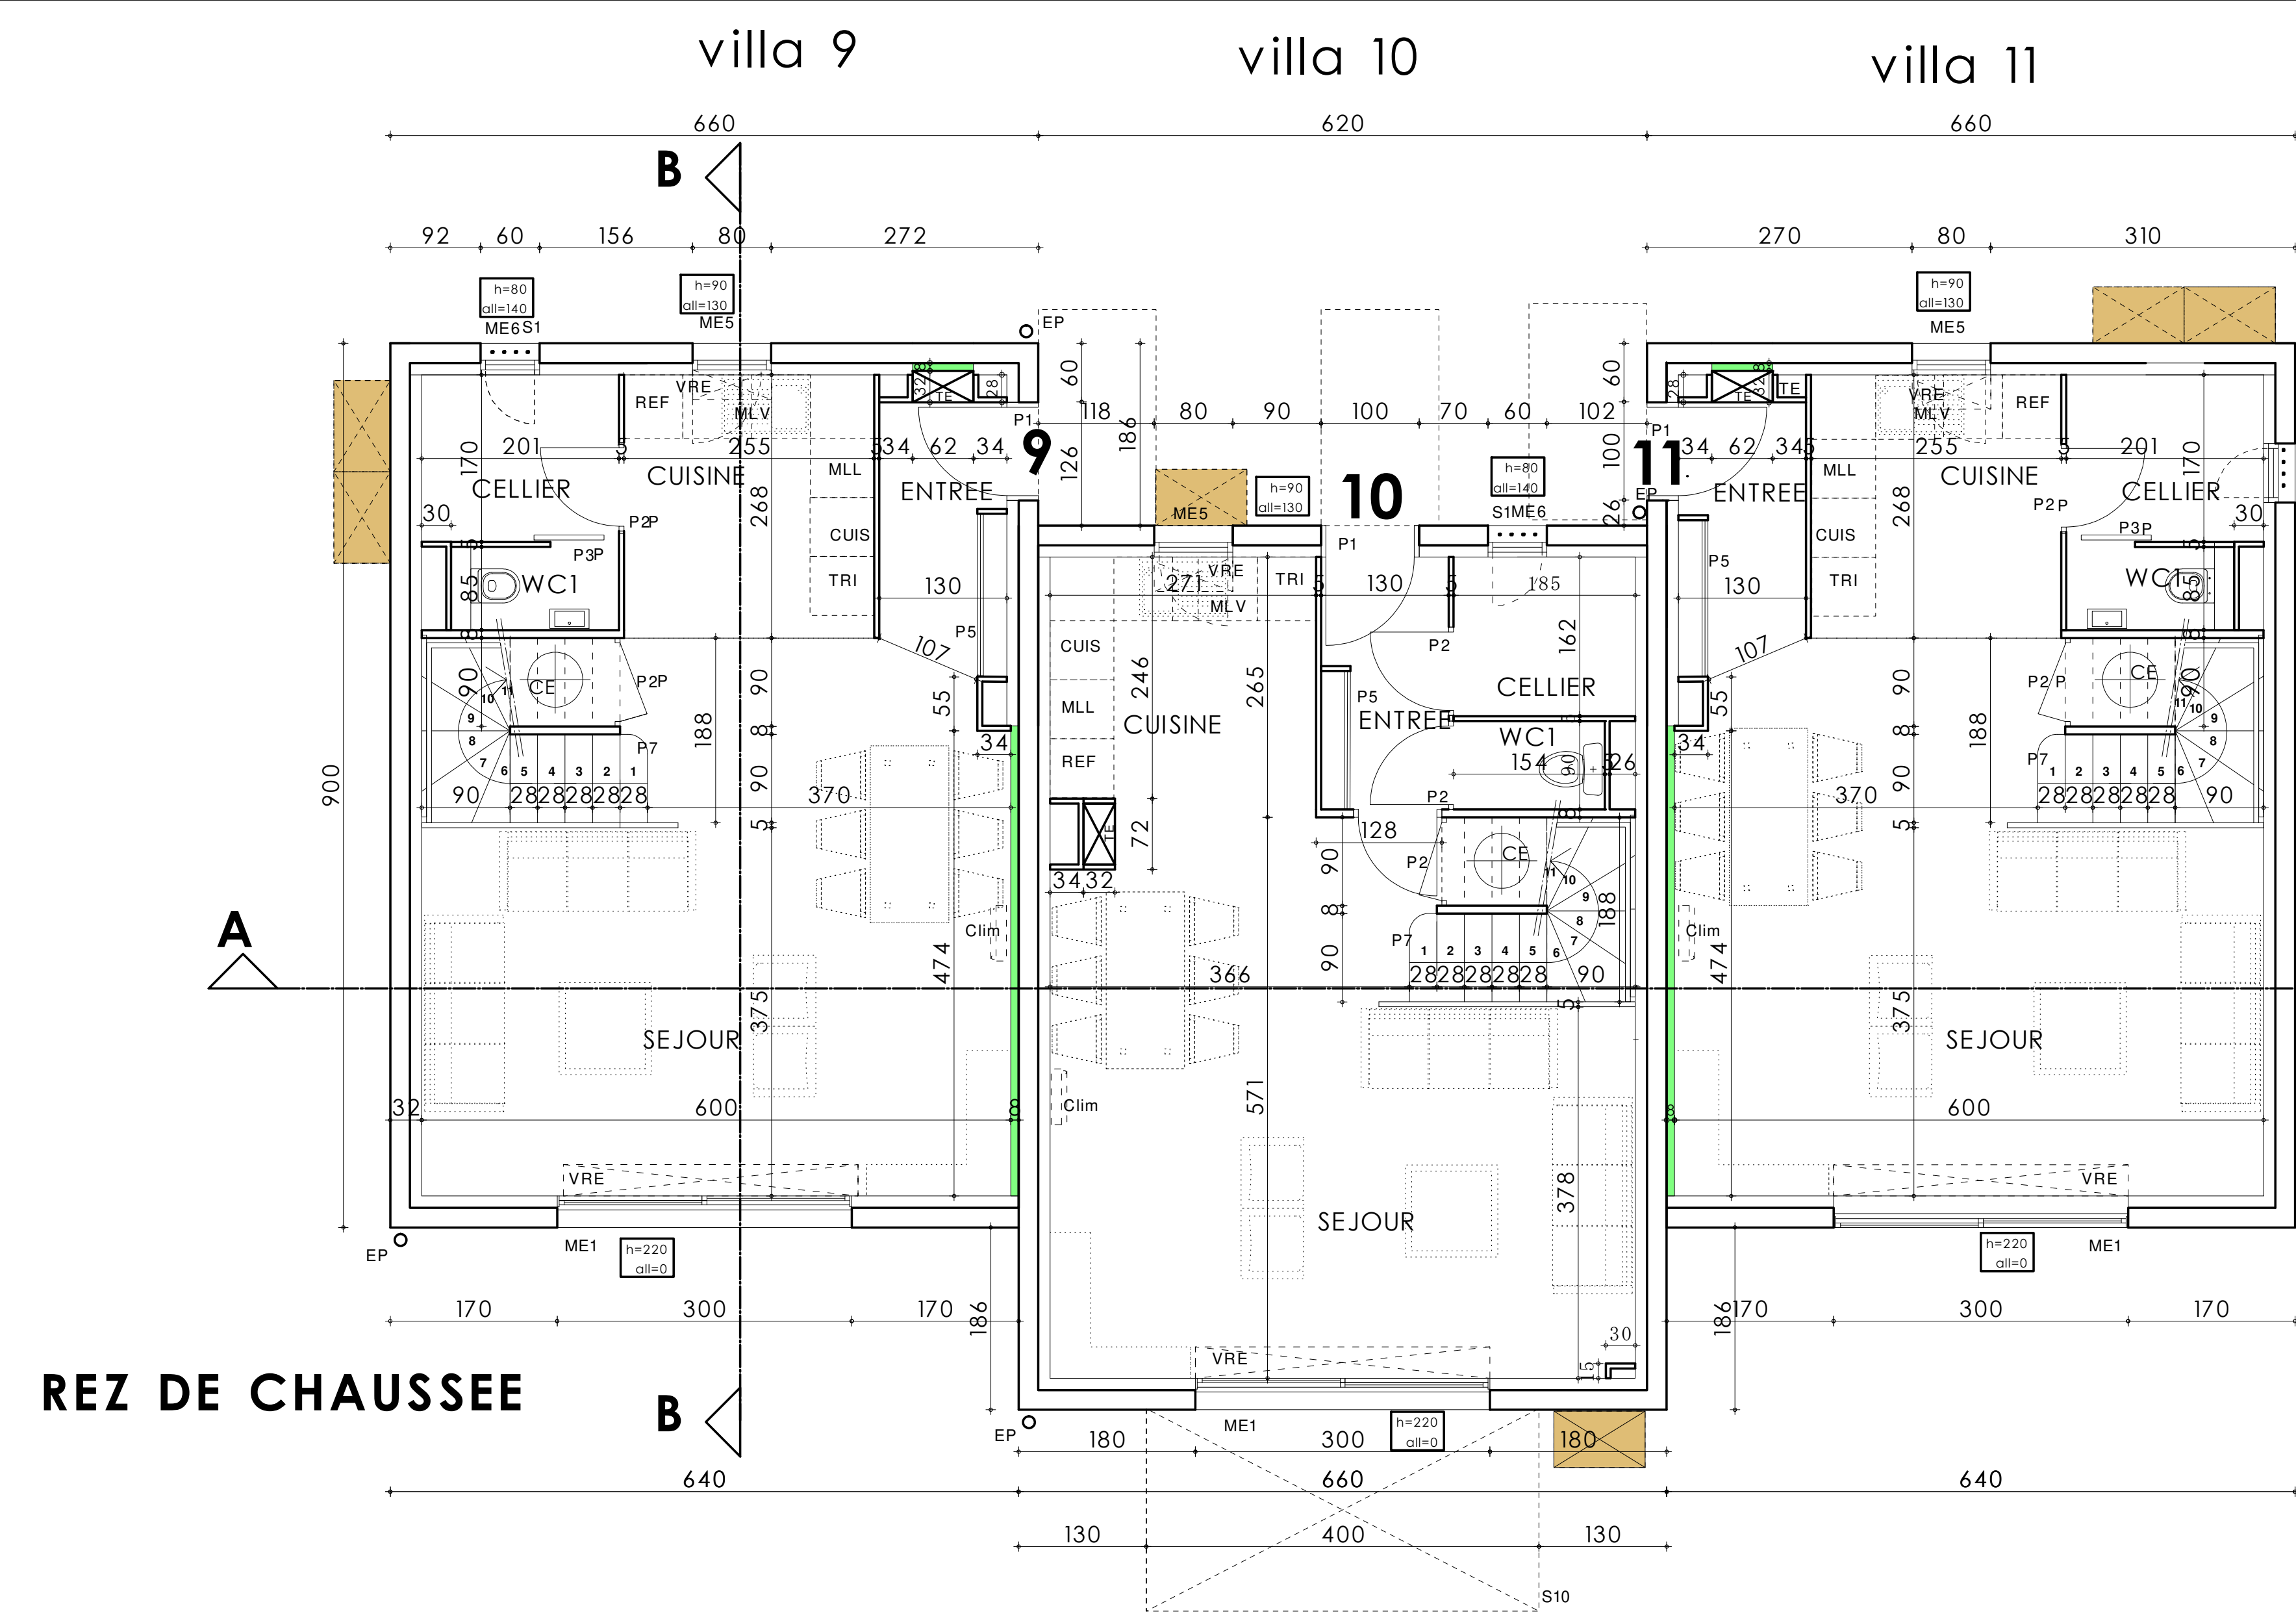



REZ DE CHAUSSEE

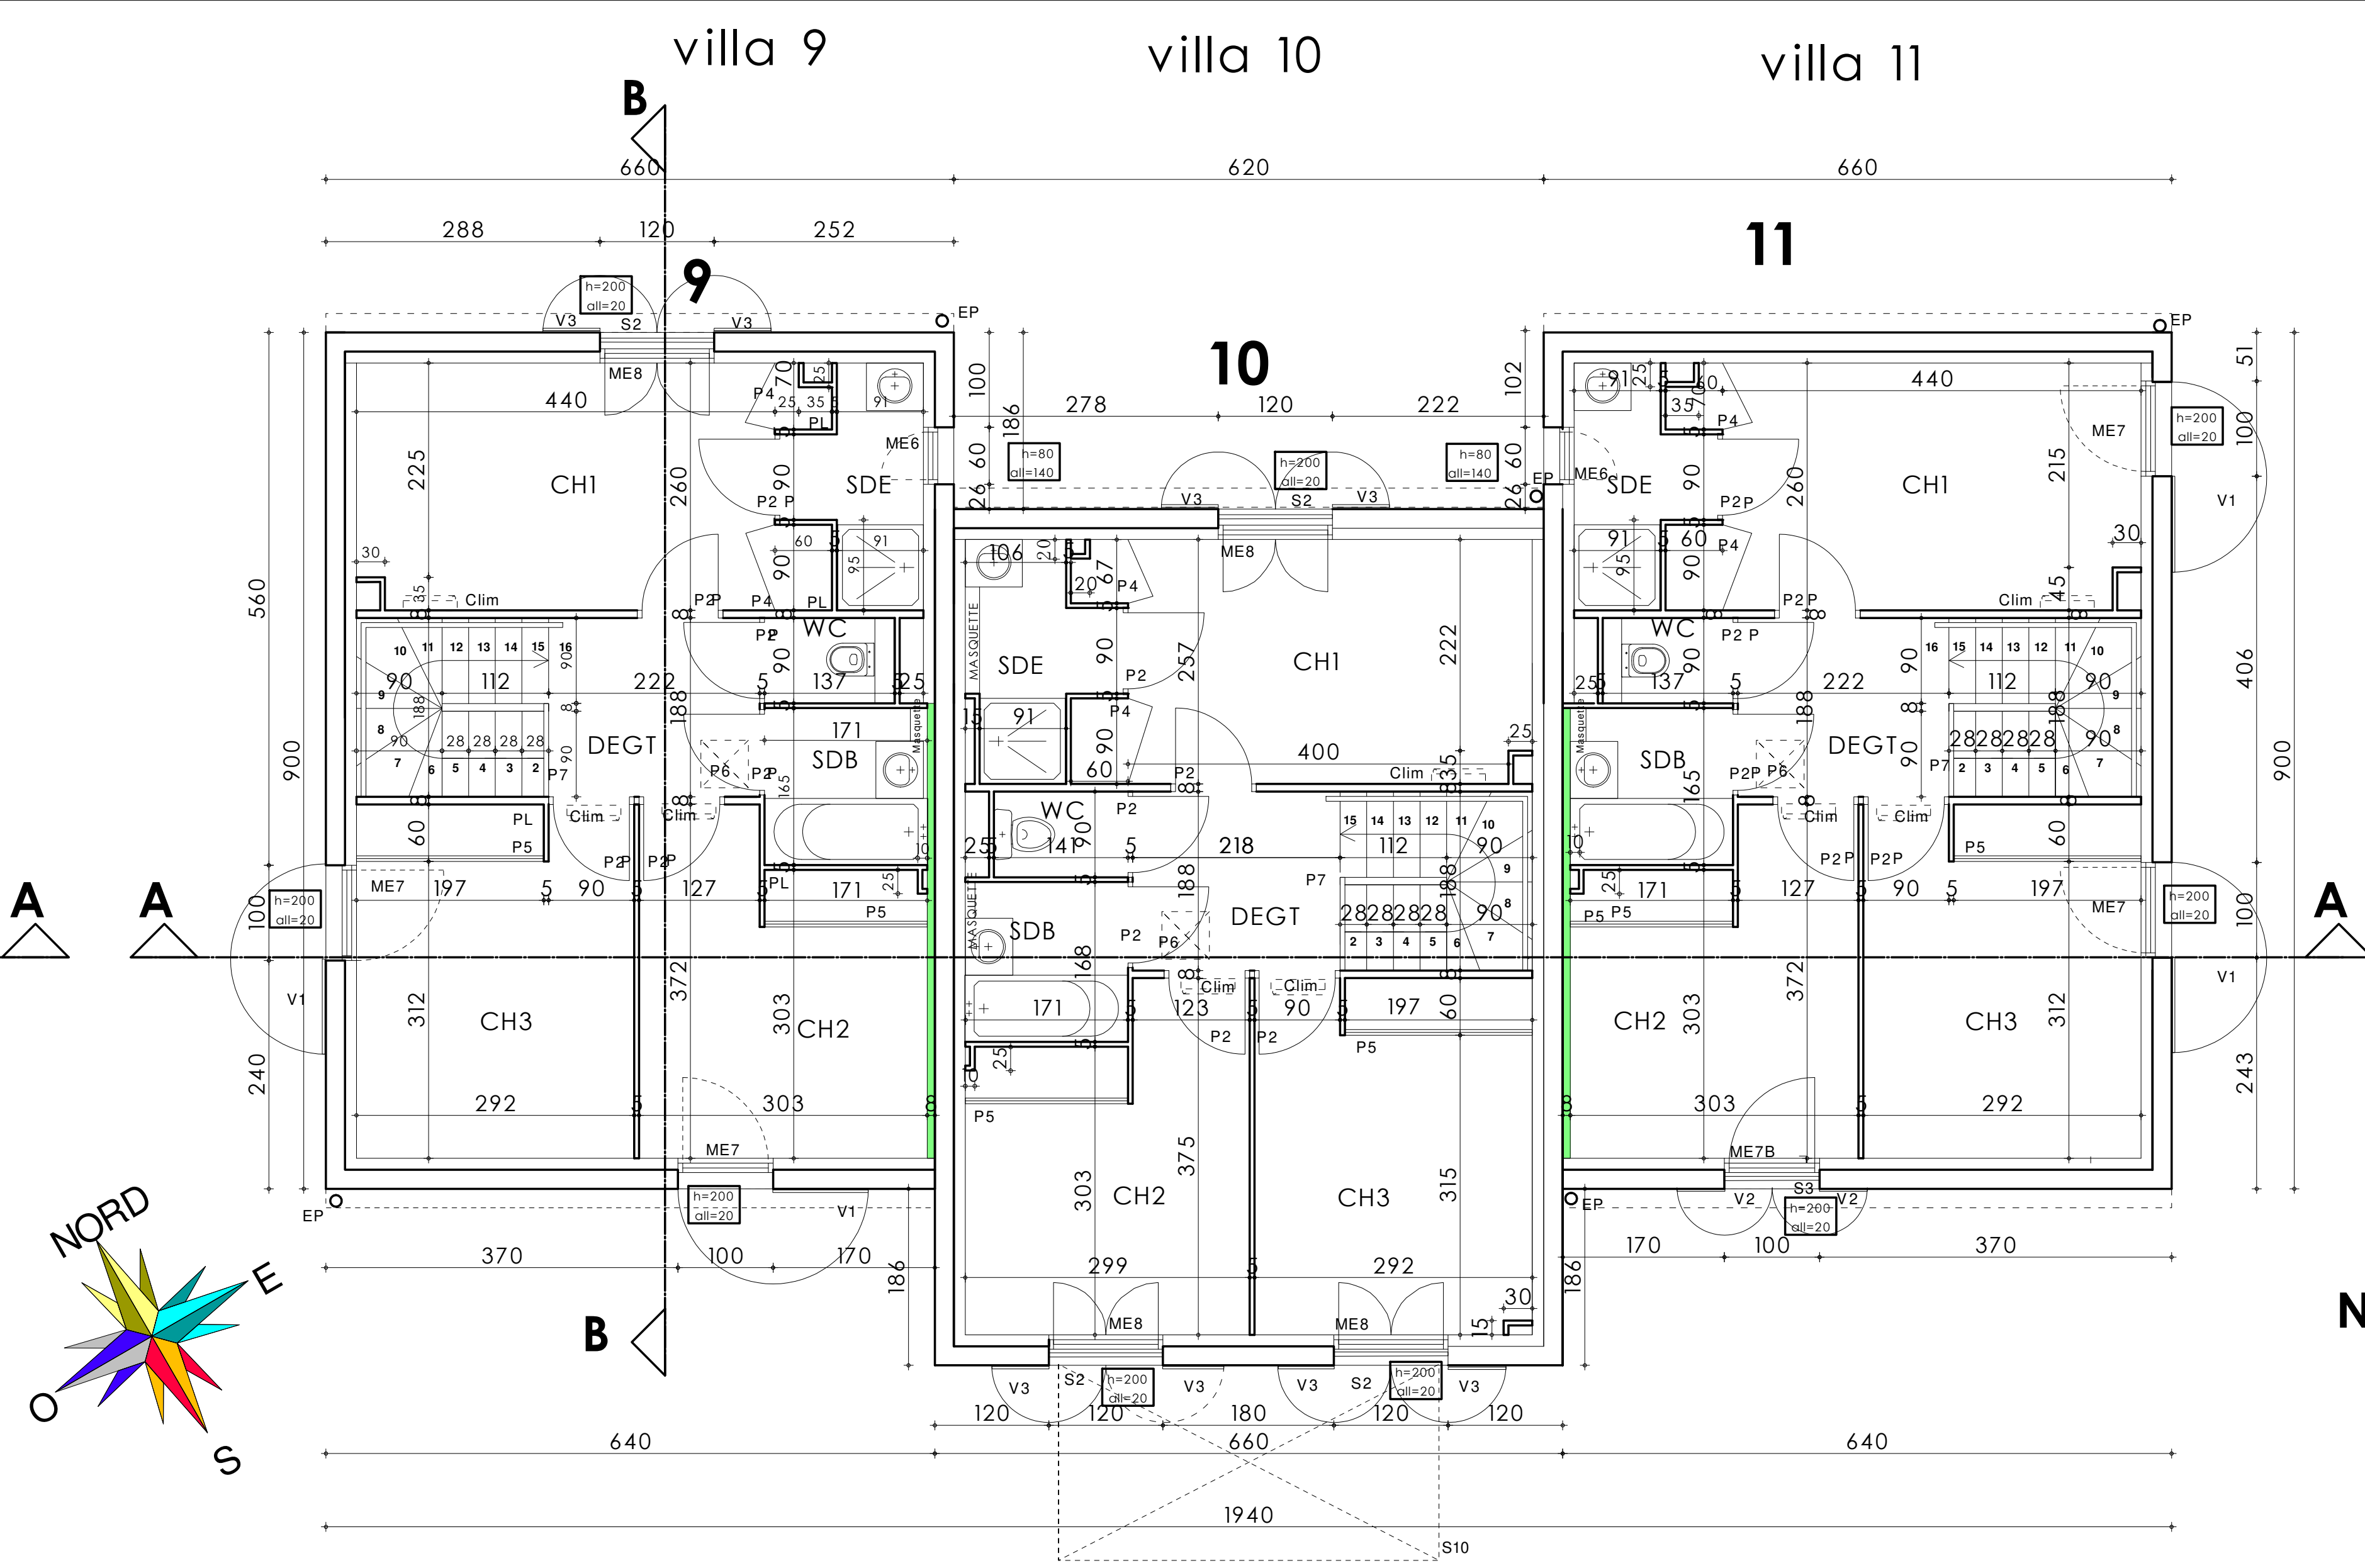

NIVEAU 1


PLAN DE NIVEAU 1/50

- LEGENDE**
- Coffre volet roulant
 - Faux plafond
 - Espace de manoeuvre 220X120 devant la porte d'entrée
 - Espace de manoeuvre 80X130 sanitaire
 - Aire de rotation PMR
 - GTL cf détail technique
 - Isolant acoustique
 - Cache de l'unité extérieure de climatisation
 - Unités intérieure de climatisation

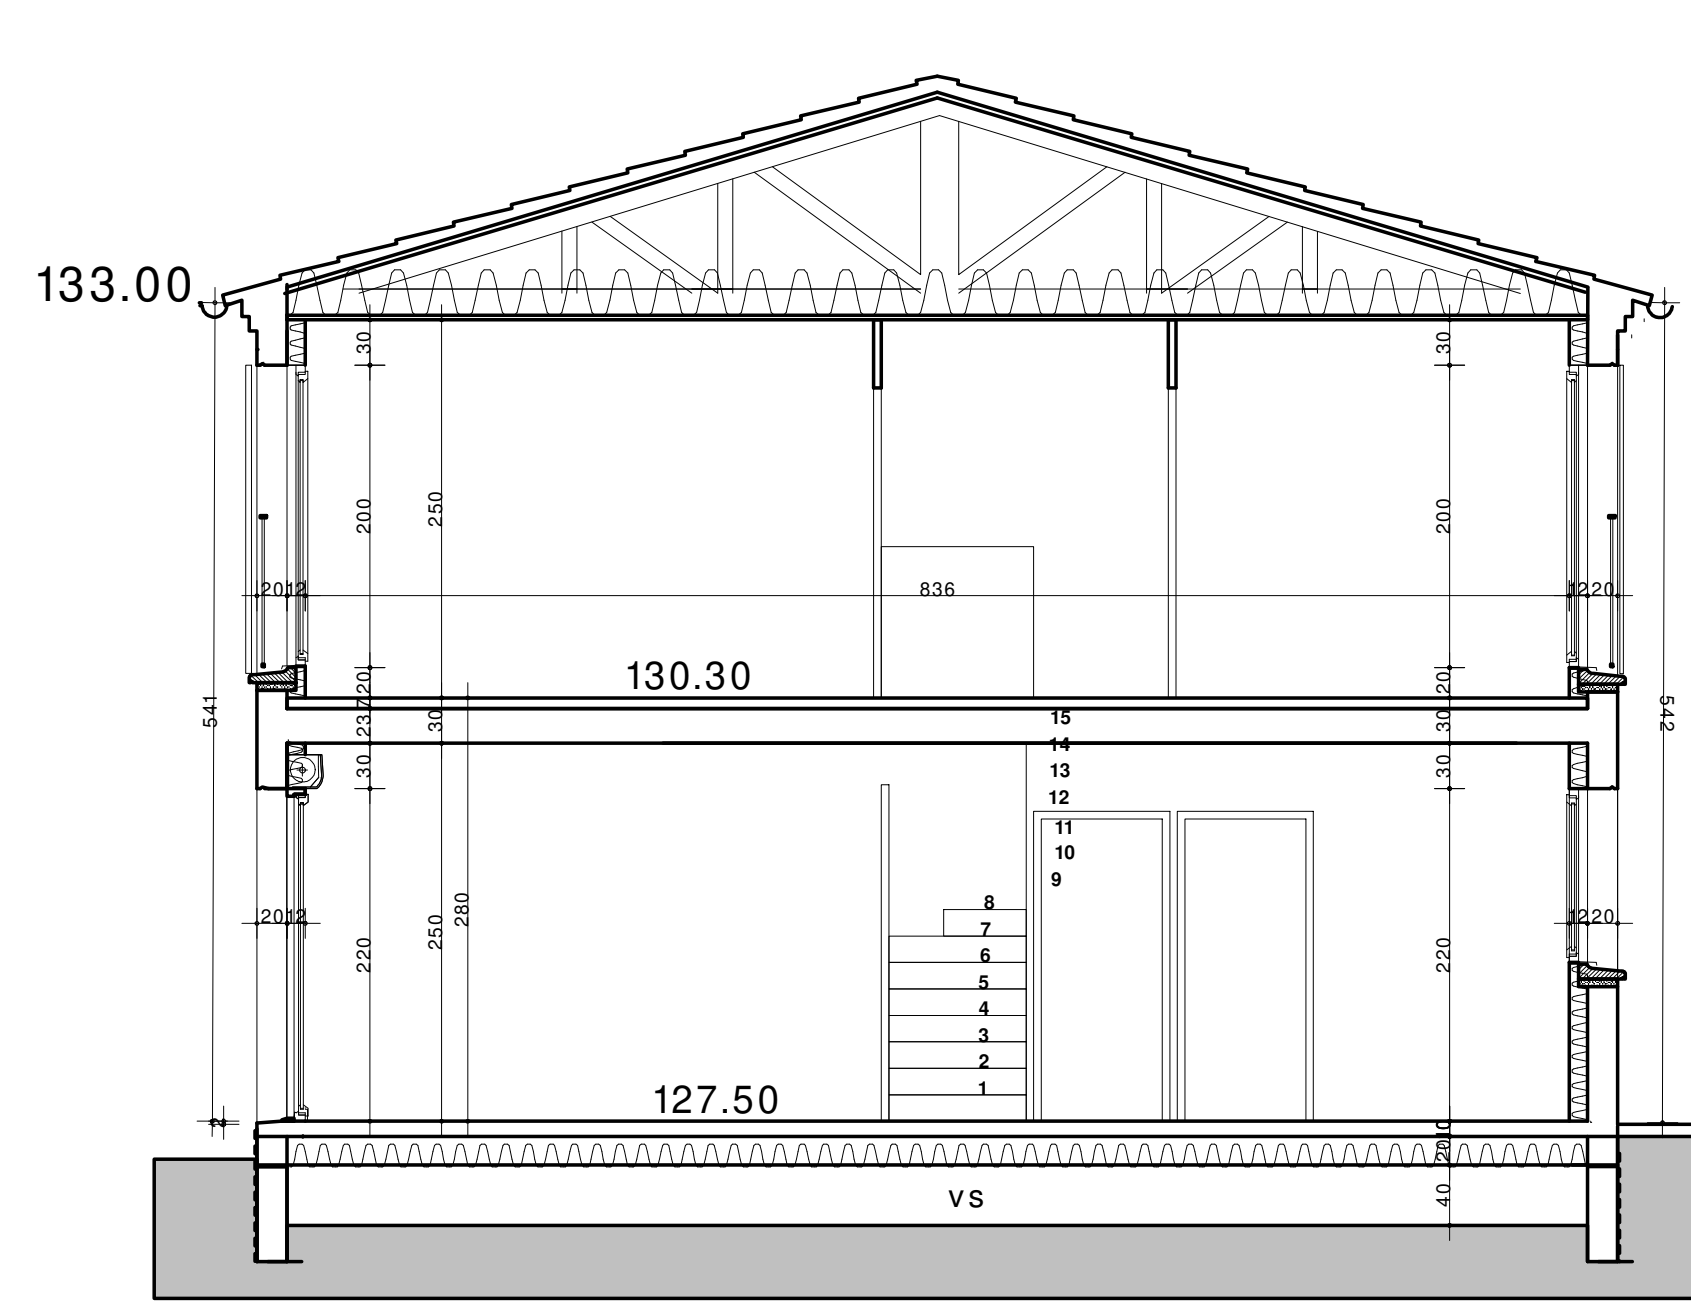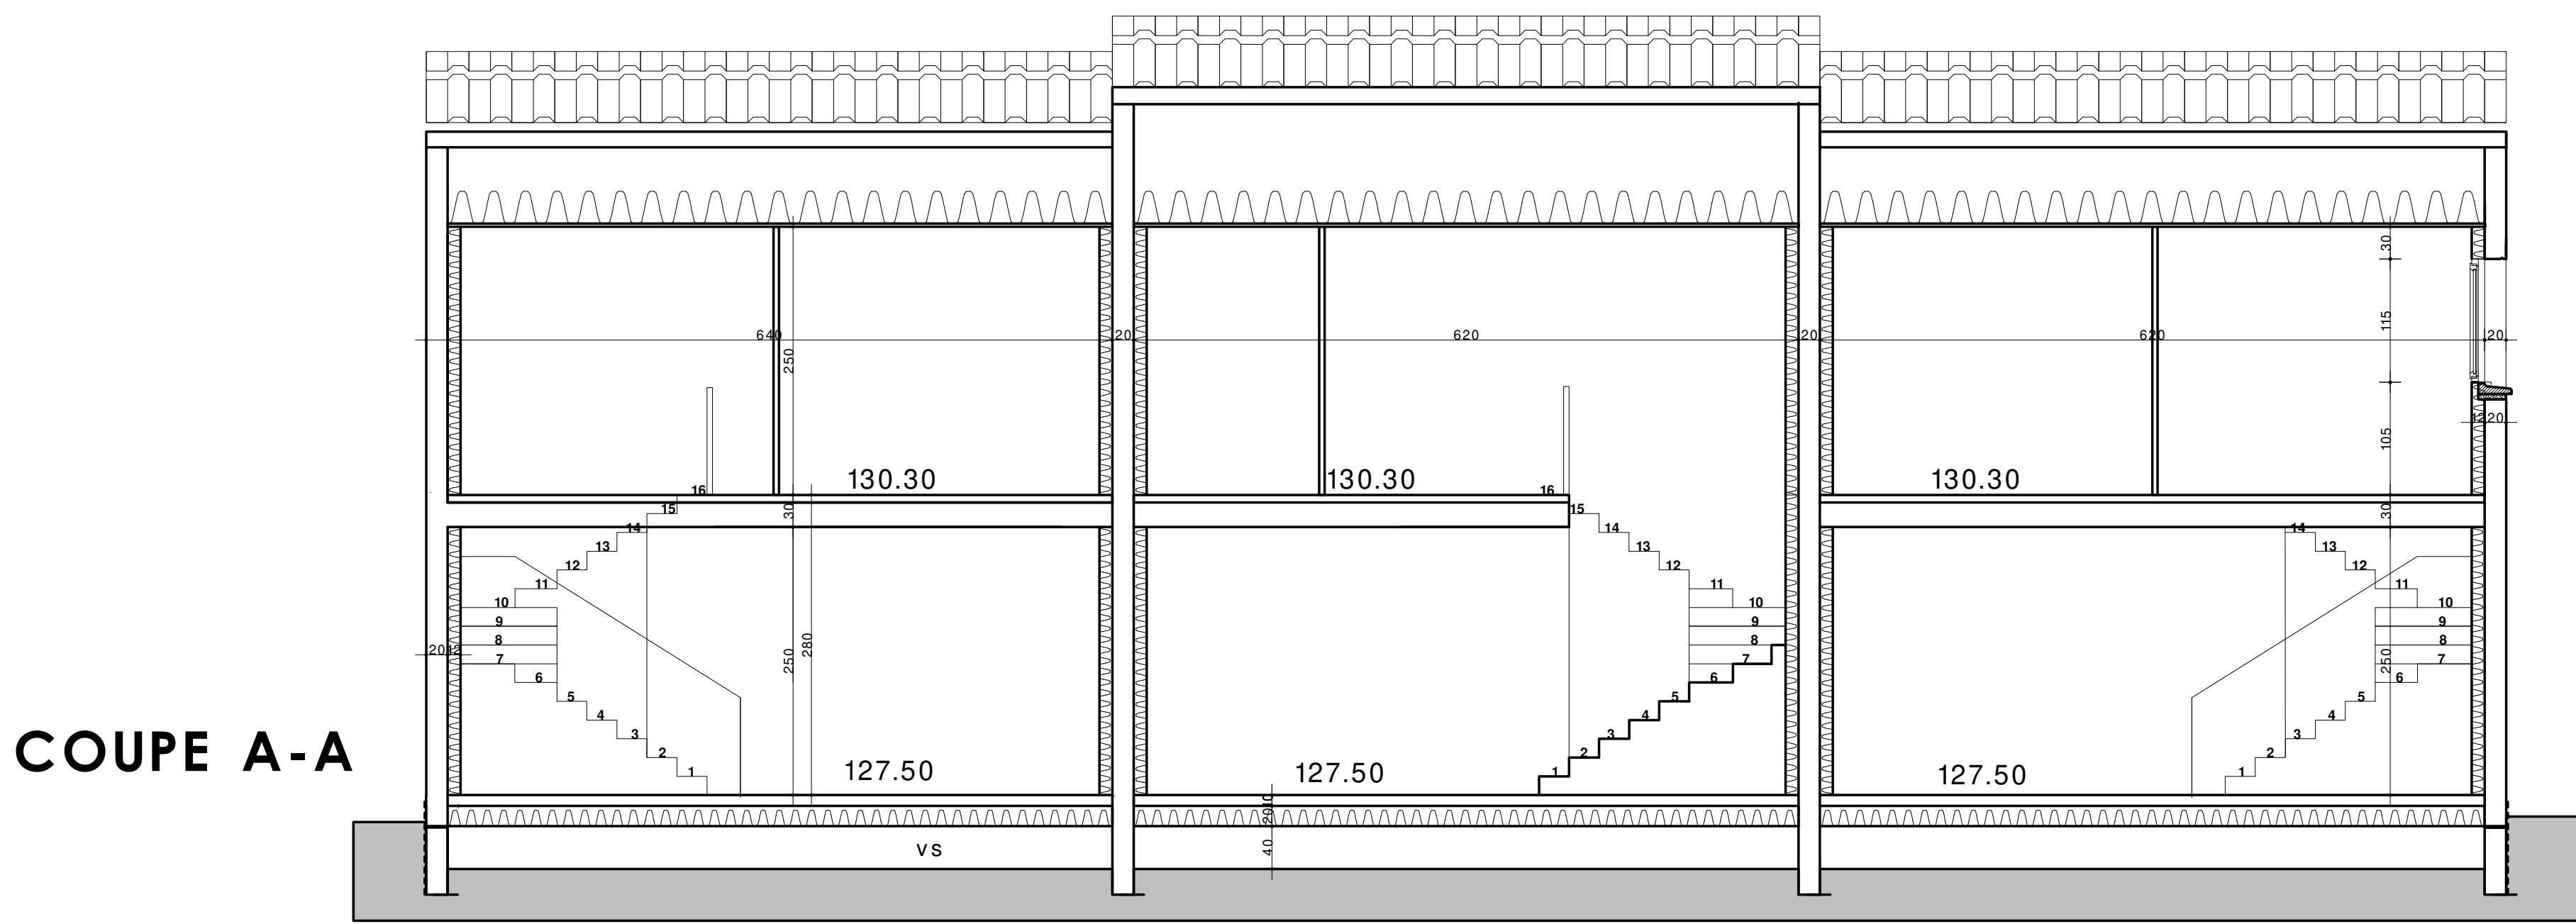

COUPES 1/50

- LEGENDE**
- Coffre volet roulant
 - Faux plafond
 - Espace de manoeuvre 220X120 devant la porte d'entrée
 - Espace de manoeuvre 80X130 sanitaire
 - Aire de rotation PMR
 - GTL cf détail technique
 - Isolant acoustique
 - Cache de l'unité extérieure de climatisation
 - Unités intérieure de climatisation

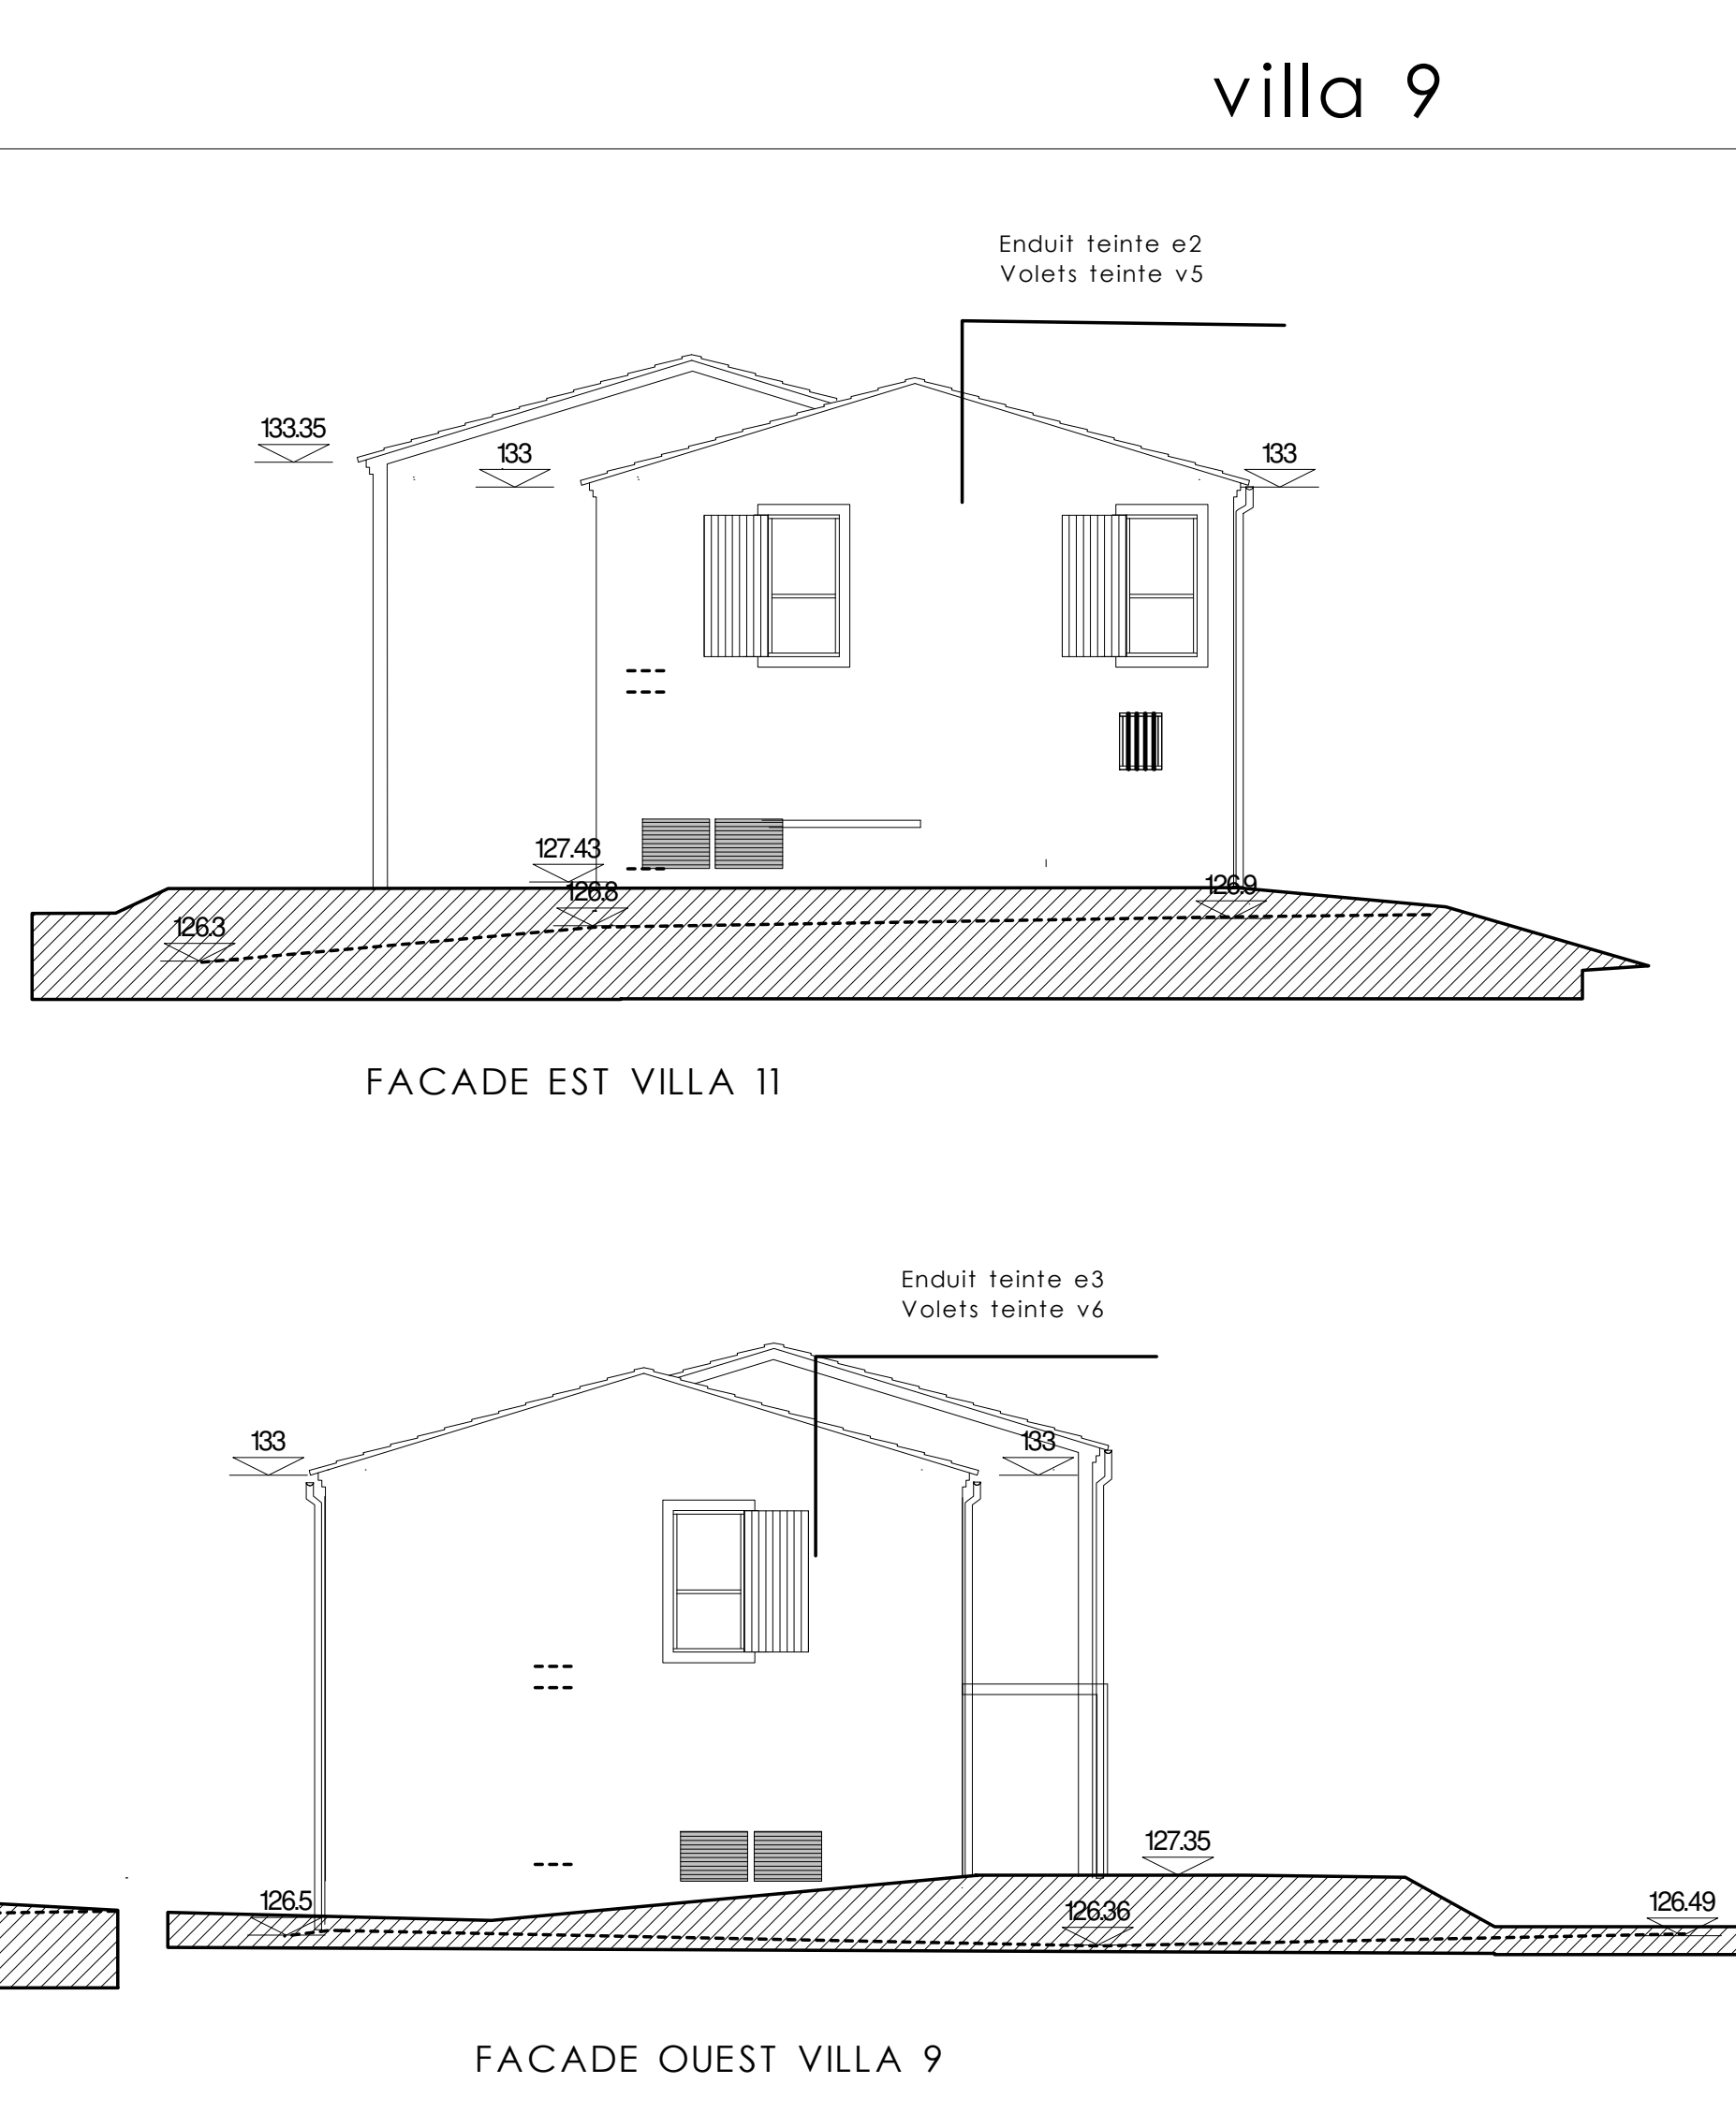

FACADES /100

GRANDE TERRE			
INDICE	DATE	MODIFICATIONS	
A	15/04/2026	MODIFICATIONS SUITE REUNION DCE	
B	29/04/2026	SUPPRESSION LAVE MAIN DANS LES VILLAS COUTS MAITRISES	
C	06/07/2026	MODIFICATION TE ET IOLANT ACOUSTIQUE	
D			
E			
F			
G			
H			
I			
J			
K			
L			
ARCHITECTES M. CHAUVET A.C. CARNAZZA ARCHITECTES D.P.L.G. ENTREPRENEURS INDIVIDUELS 40 RUE FARGES 13008 MARSEILLE P.L.CHAUVET@ARCHITECTES-PT.COM A.C.CARNAZZA@ARCHITECTES-PT.COM		MAITRE D'OUVRAGE SCCV GRANDE TERRE (SIRET 942 743 709 R.C.S. Toulouse) OPERATION RUE NEUVE GRAND TERRE 13930 AUREILLE	
DATE 15/04/2026 PROJETS 1/50 1/100 TITRE DU PLAN PLANS COUPES FACADES VILLAS 9-10-11 NON PMR		A.P.S. P.C. D.C.E. MARCHES 103	