
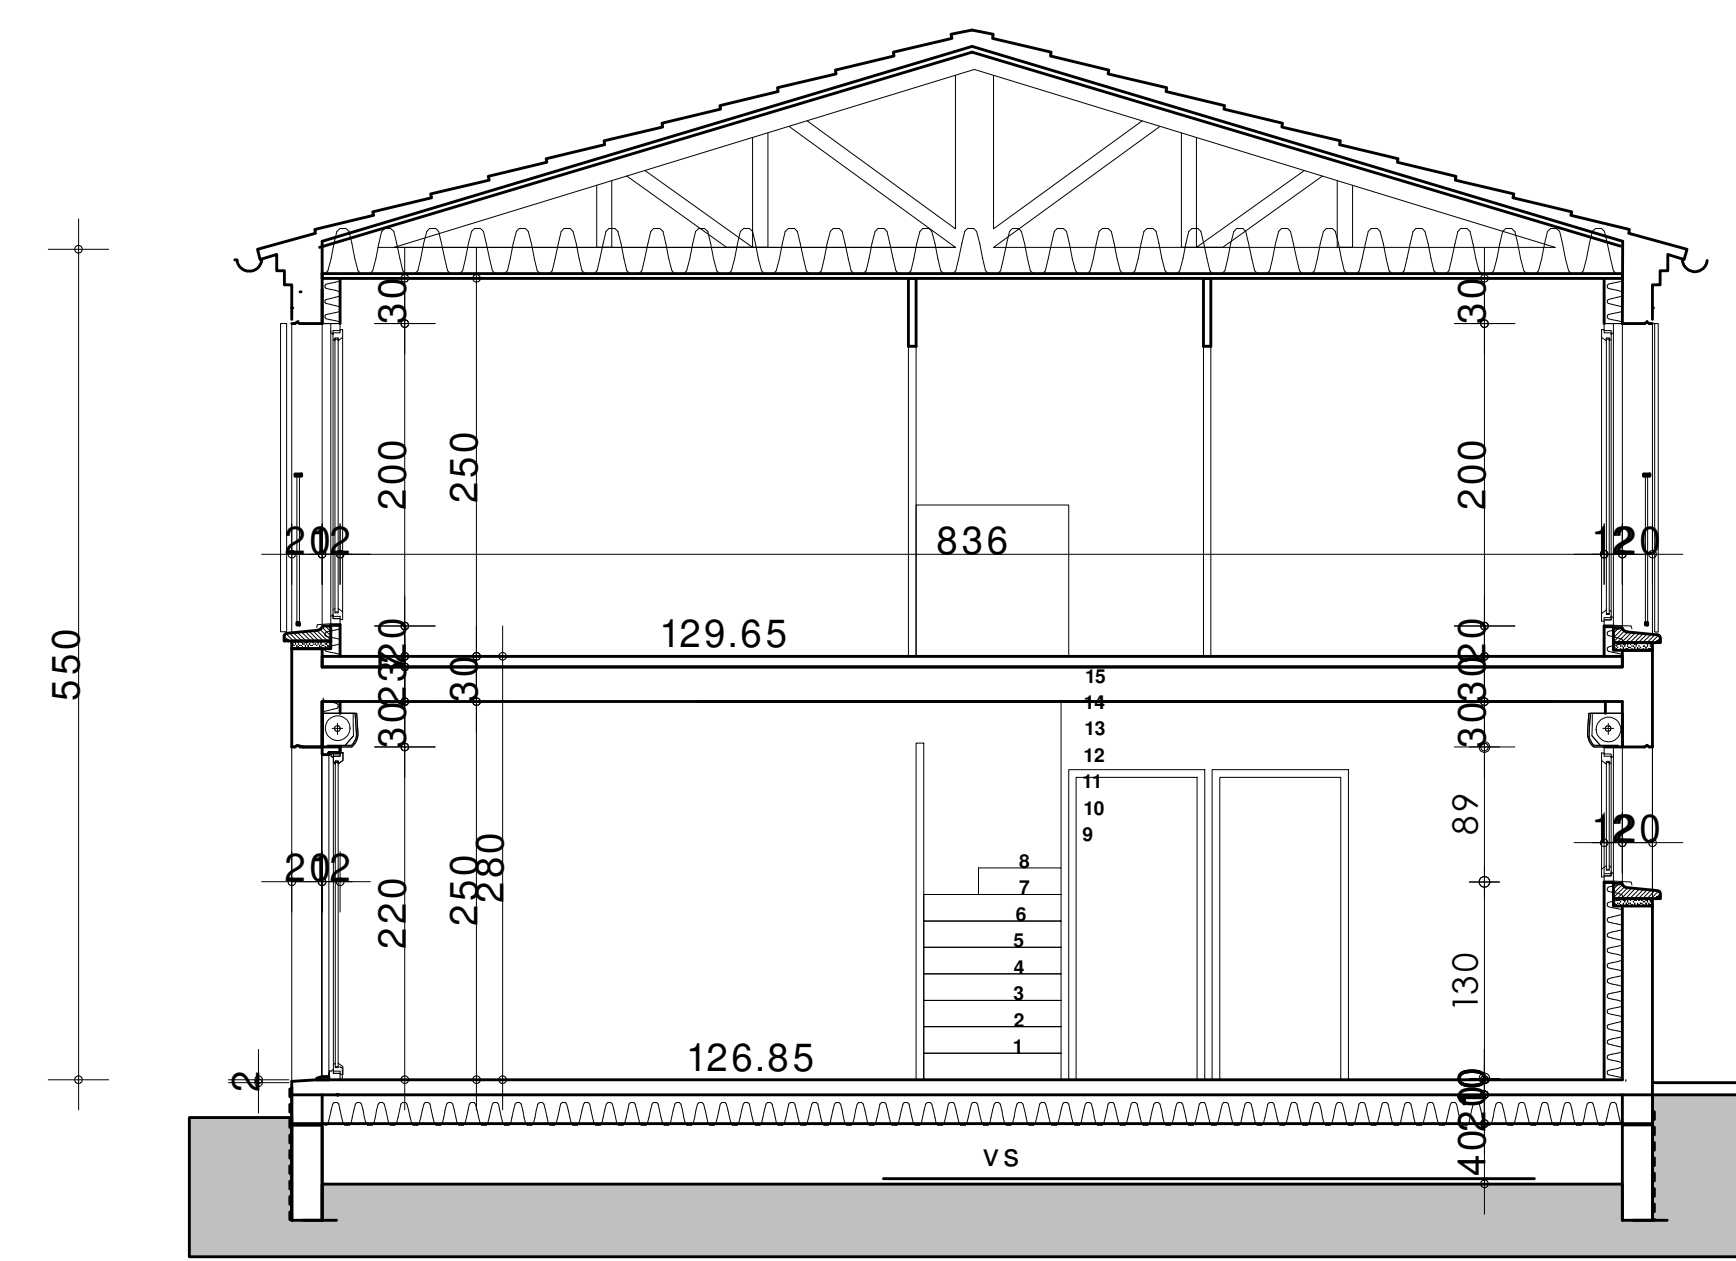
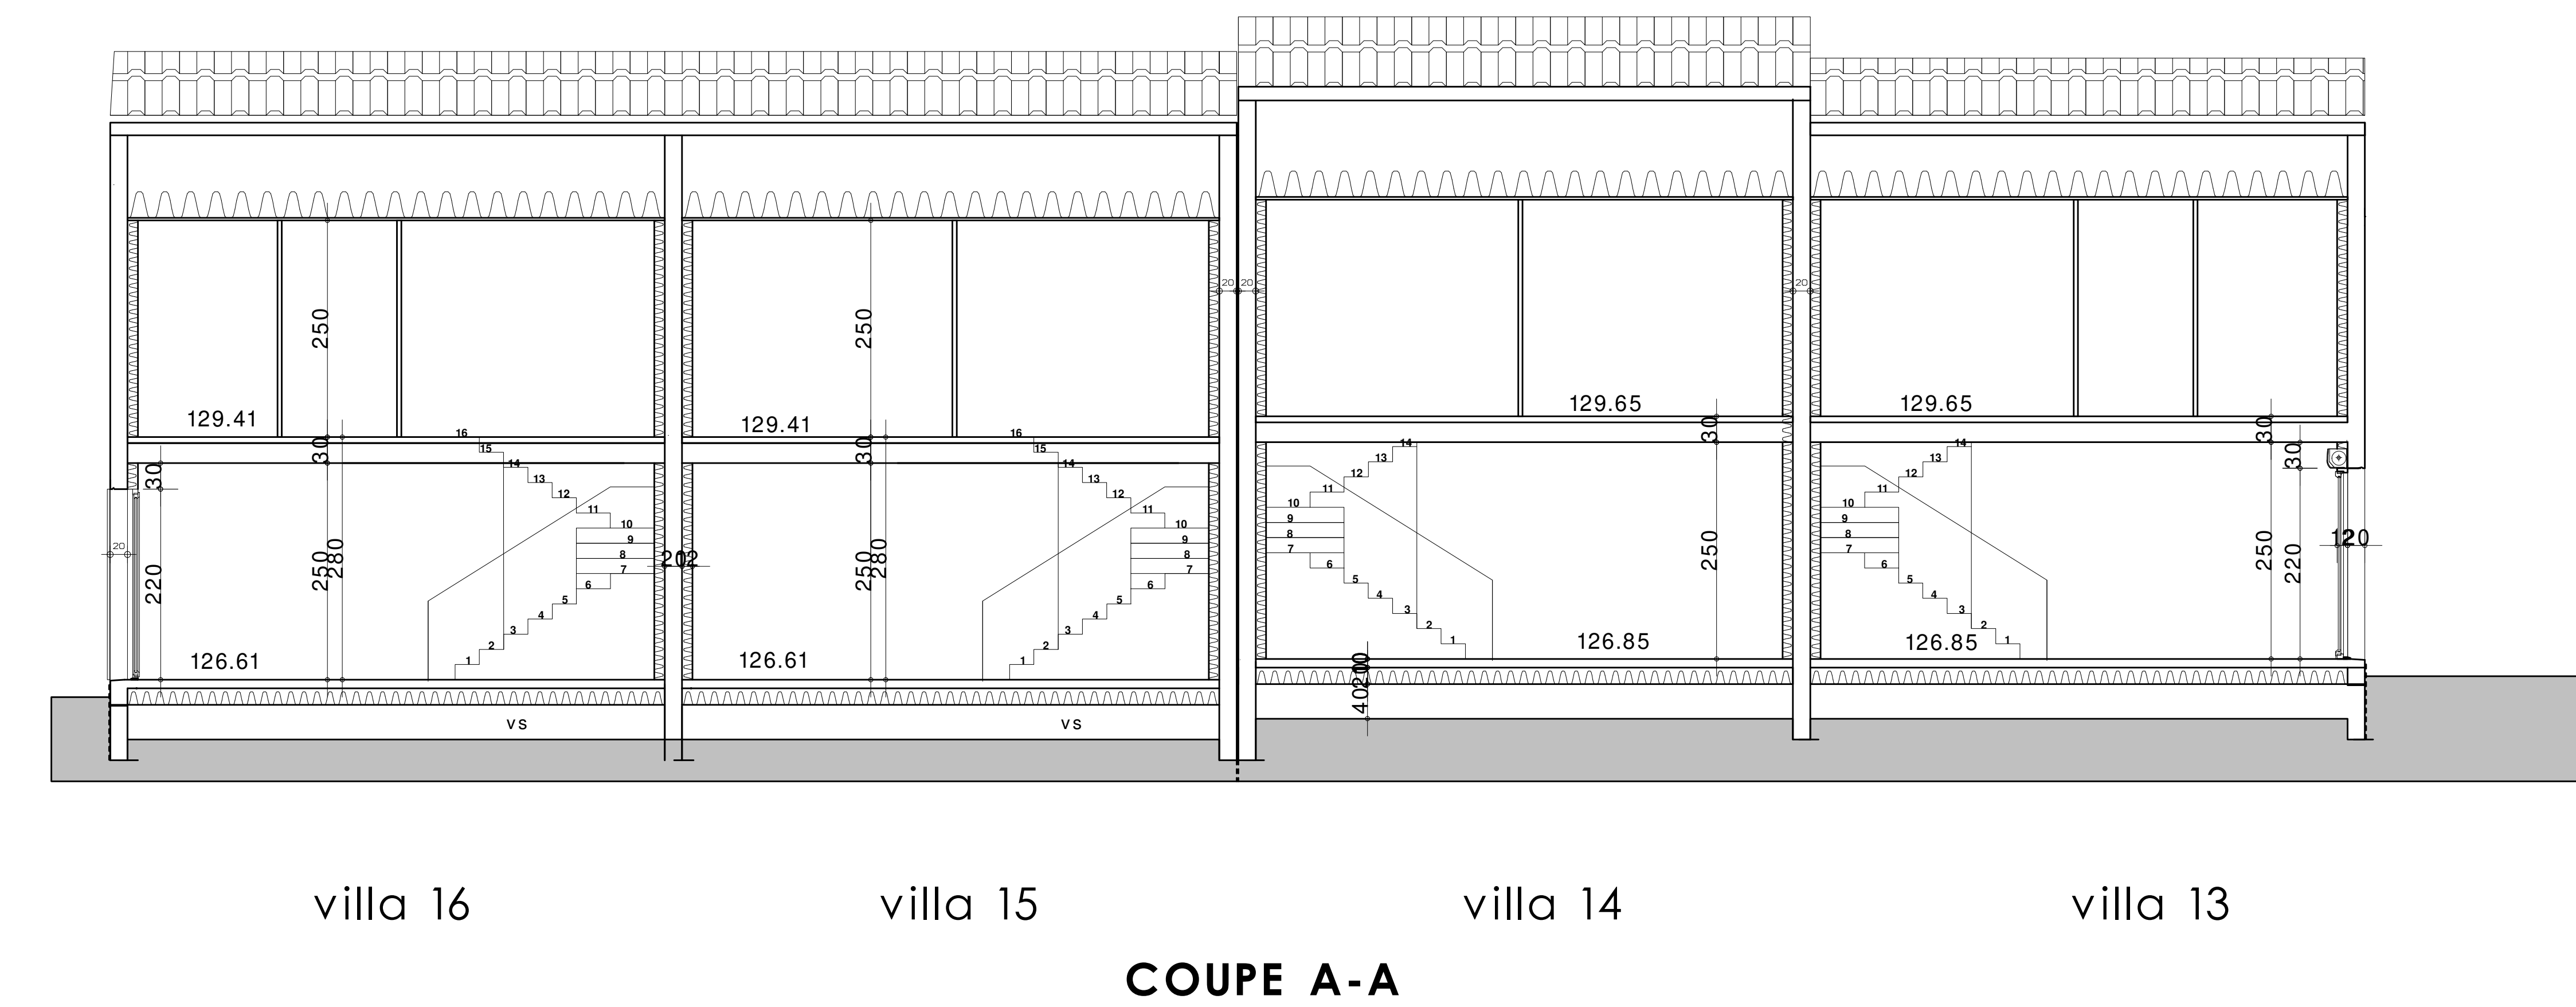


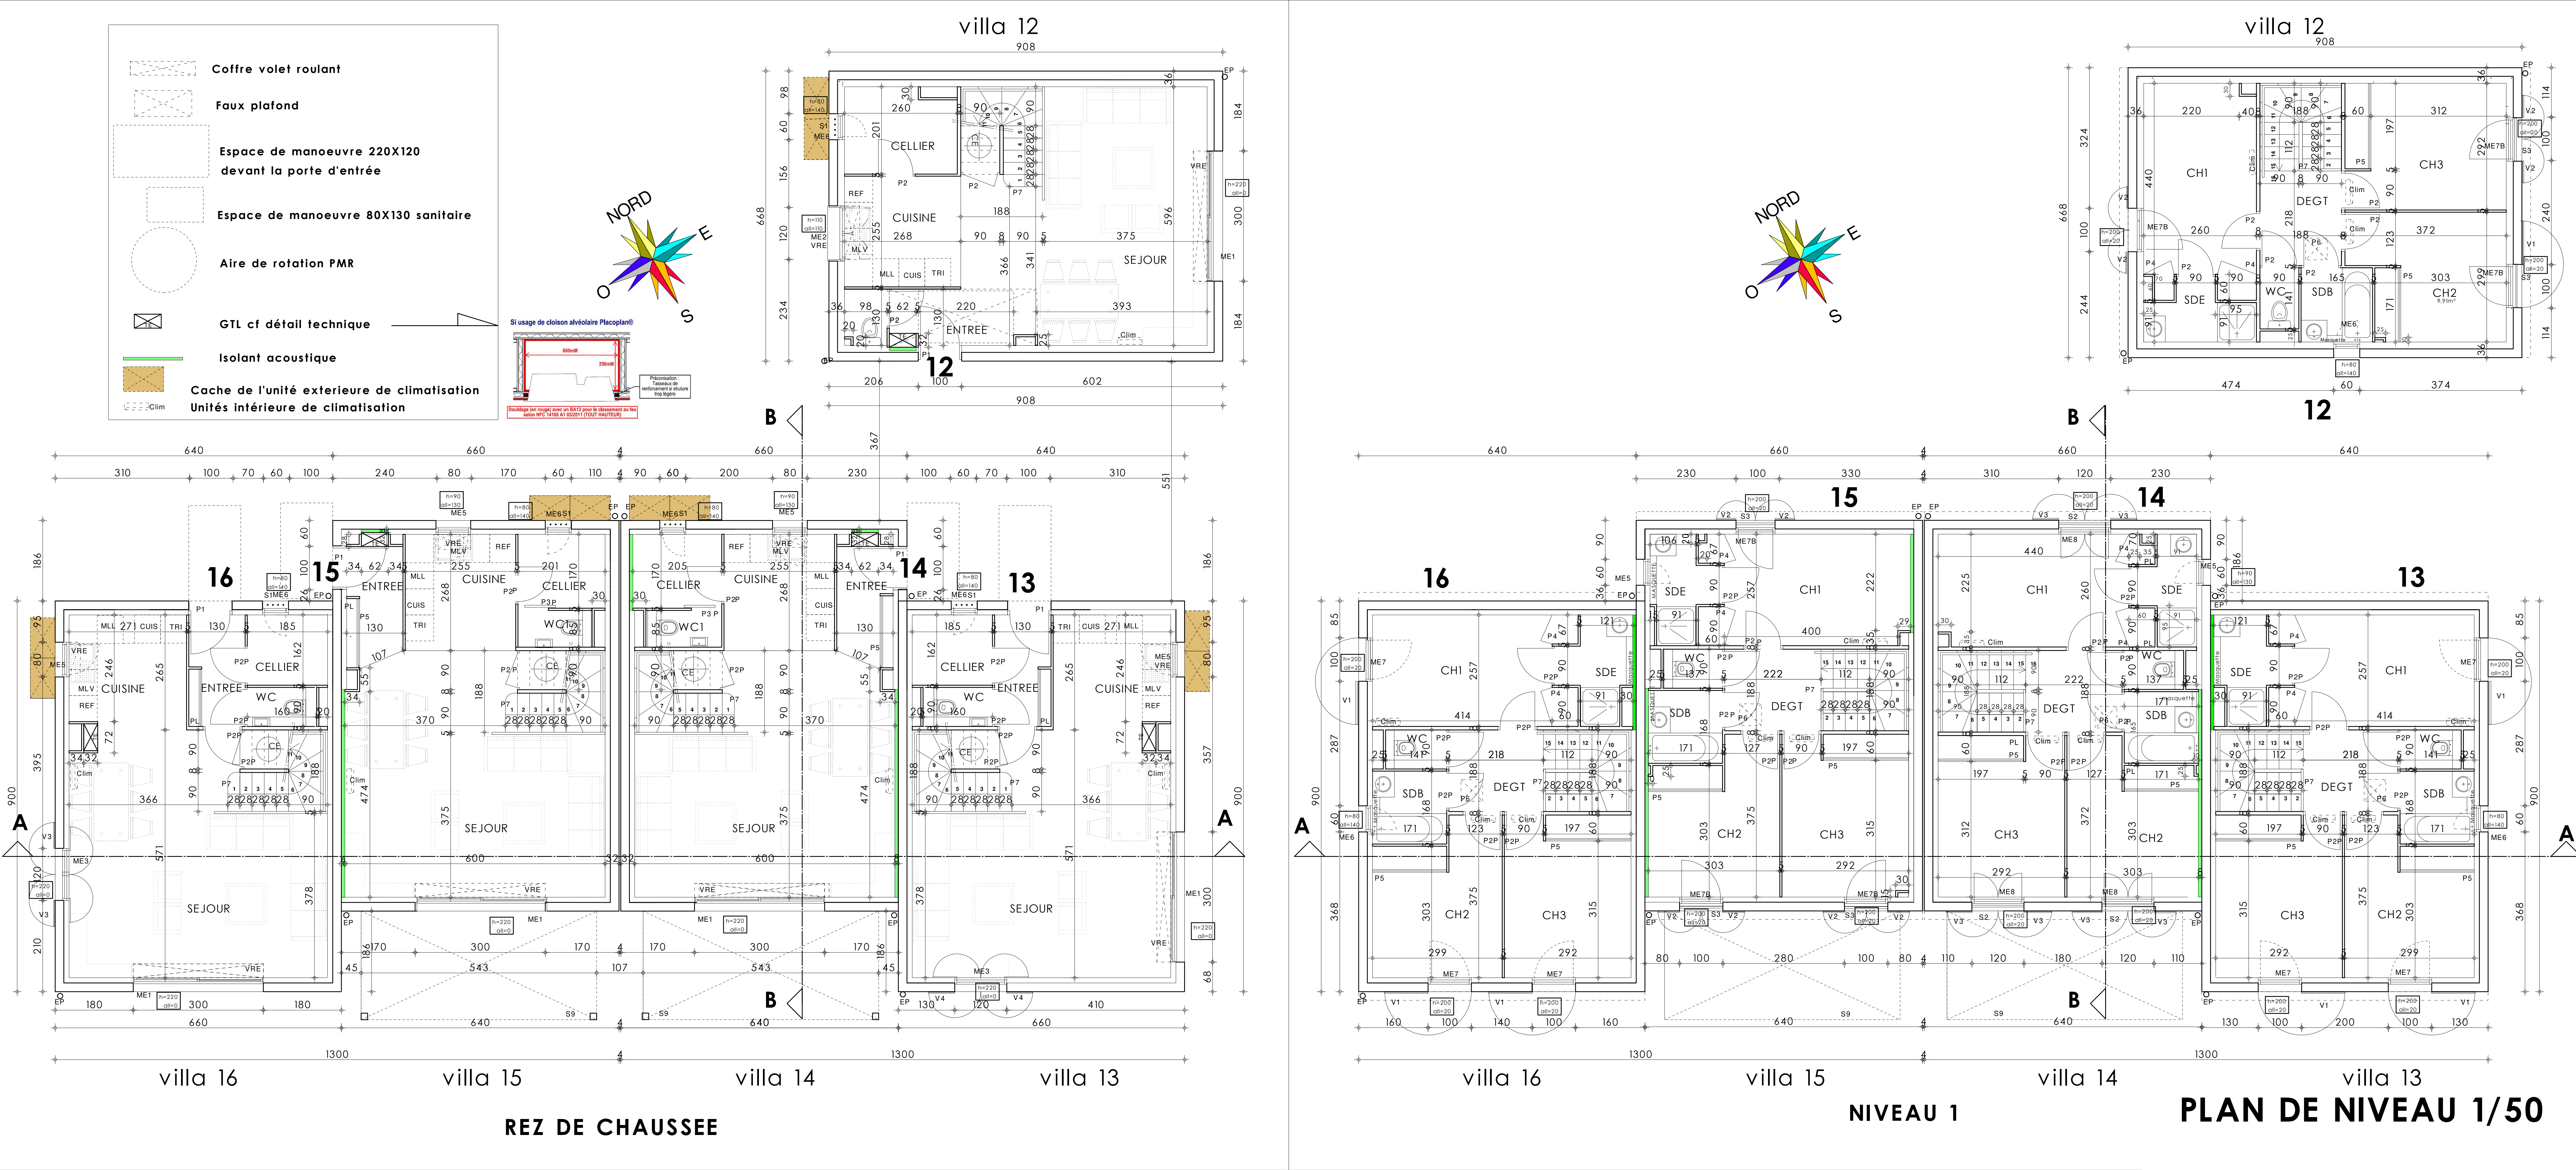

villa 14

COUPES 1/50

GRANDE TERRE			
INDICE	DATE	MODIFICATIONS	
A	15/06/2026	MODIFICATIONS SUITE REUNION DCE	
B	29/06/2026	SUPPRESSION LAVE MAIN DANS LES VILLAS COUTS MAITRISES	
C	06/07/2026	MODIFICATION TE ET ISOLANT ACOUSTIQUE	
D			
E			
F			
G			
H			
I			
J			
K			
L			
ARCHITECTES M. CHAUVET A.C. CARNAZZA ARCHITECTES D.P.L.G. Entrepreneurs Individuels 40 Rue FARGES 13008 MARSEILLE 04 91 27 00 00 www.grandeterre.fr		MATRE D'OUVRAGE SCCV GRANDE TERRE (SIRET 742 743 709 R.C.S. Toulouse) OPERATION RUE NEUVE GRAND TERRE 13930 AUREILLE	DATE 15/04/2026 PROJETS 1/50 PLANS COUPES VILLAS 12-13-14 NON PMR
A.P.S. P.G. D.C.E. MARQUES		104	