
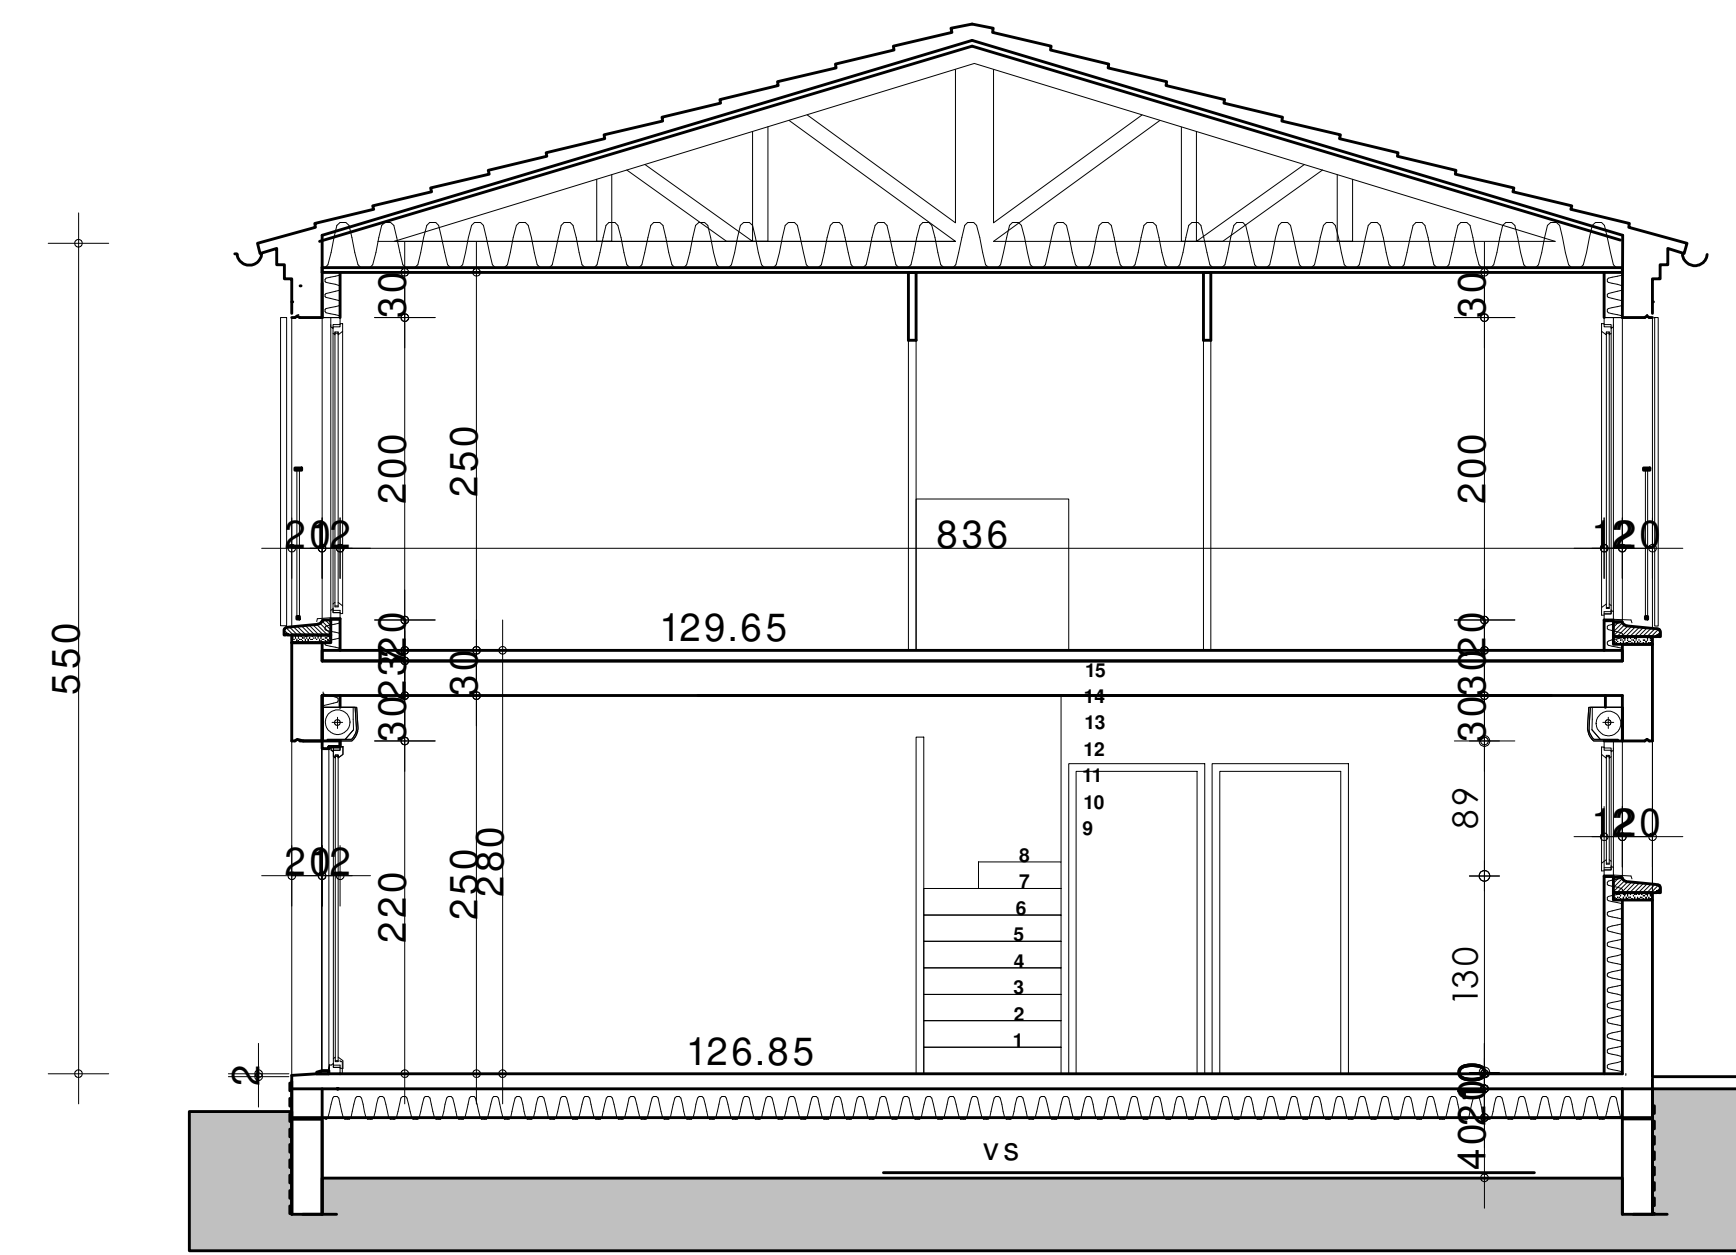
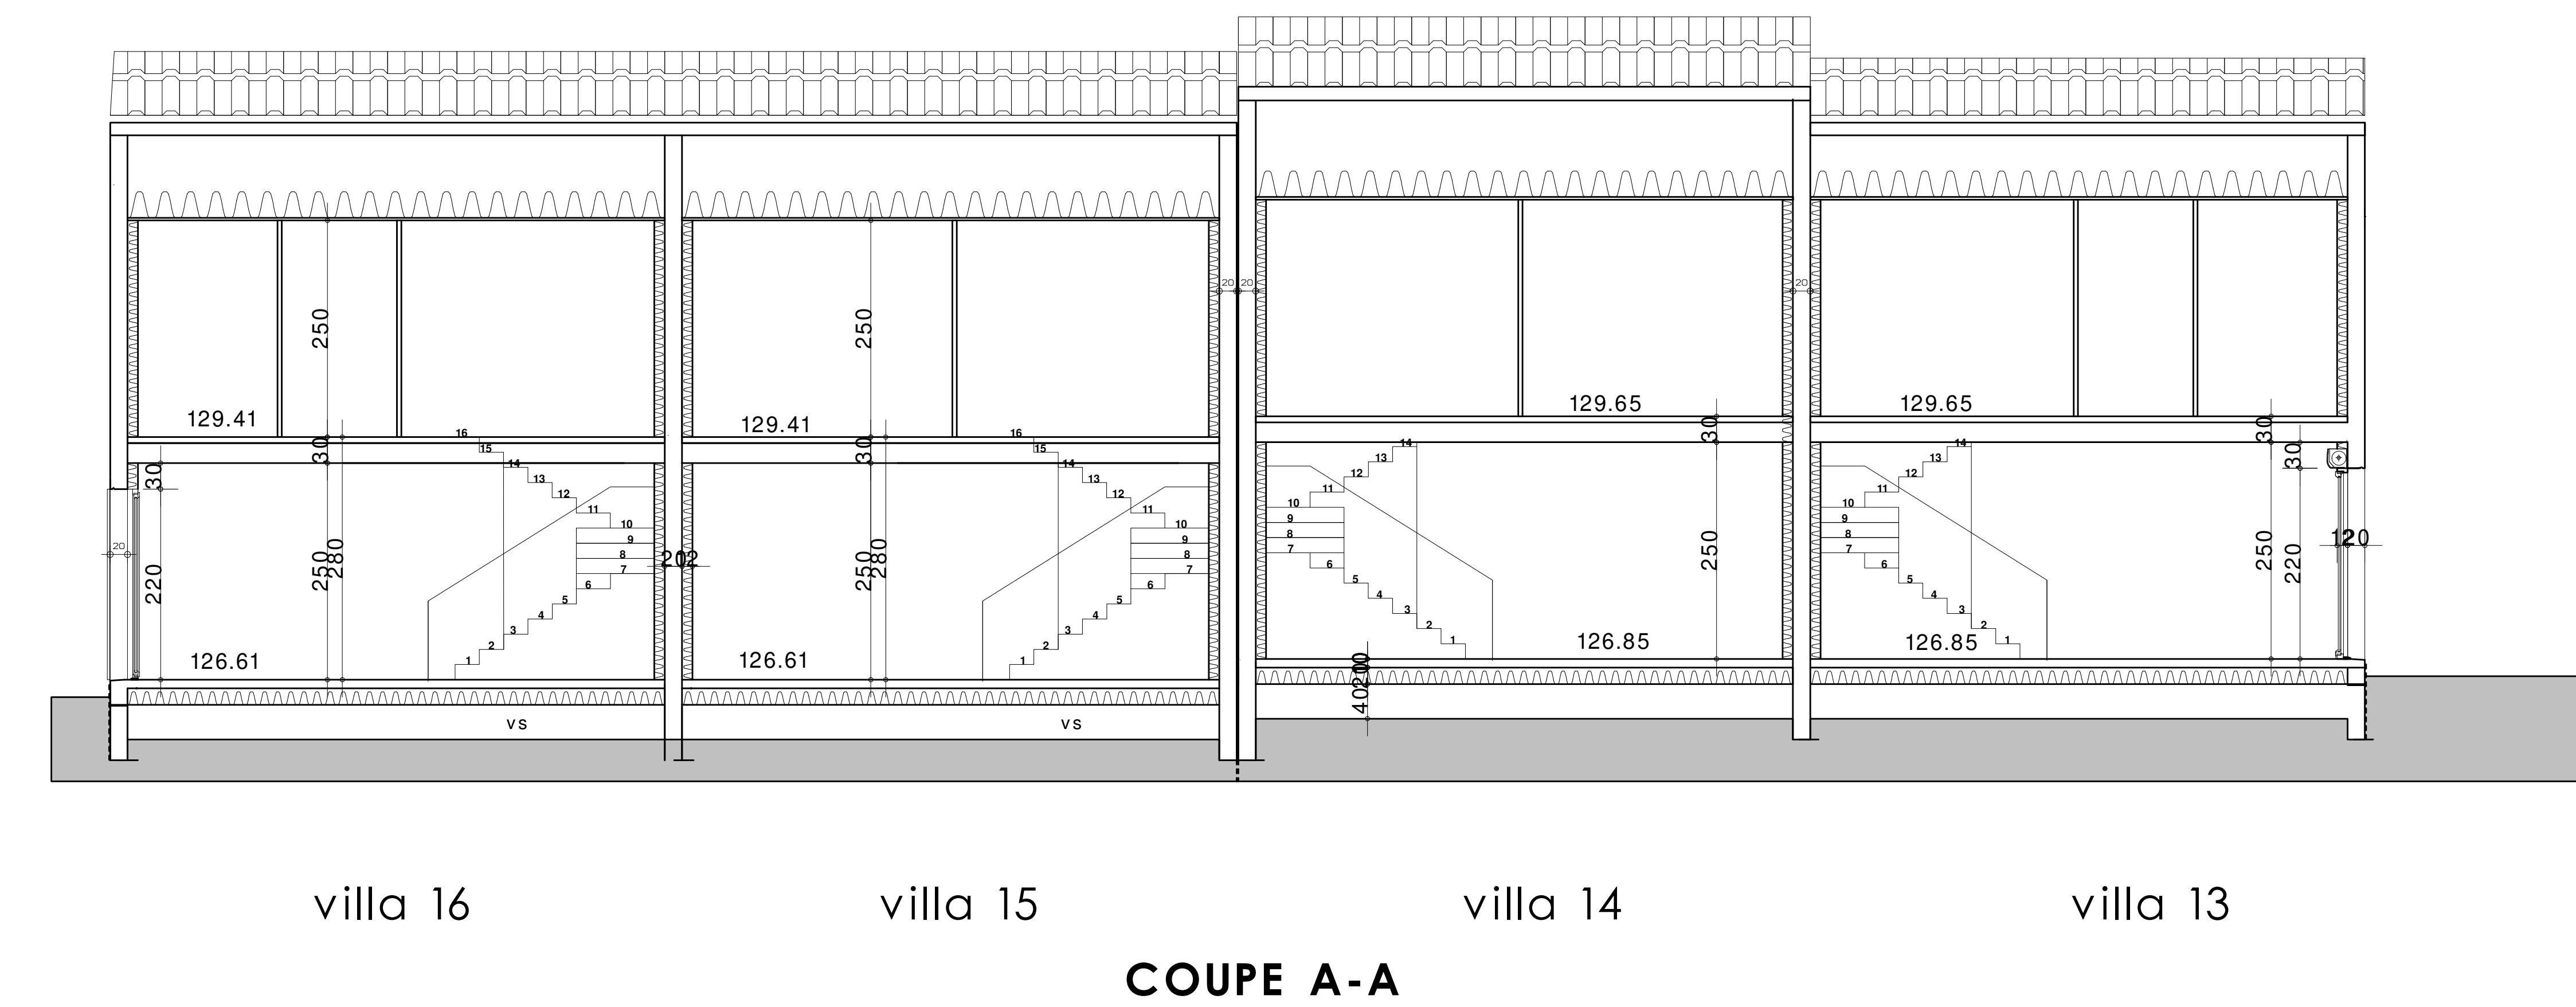


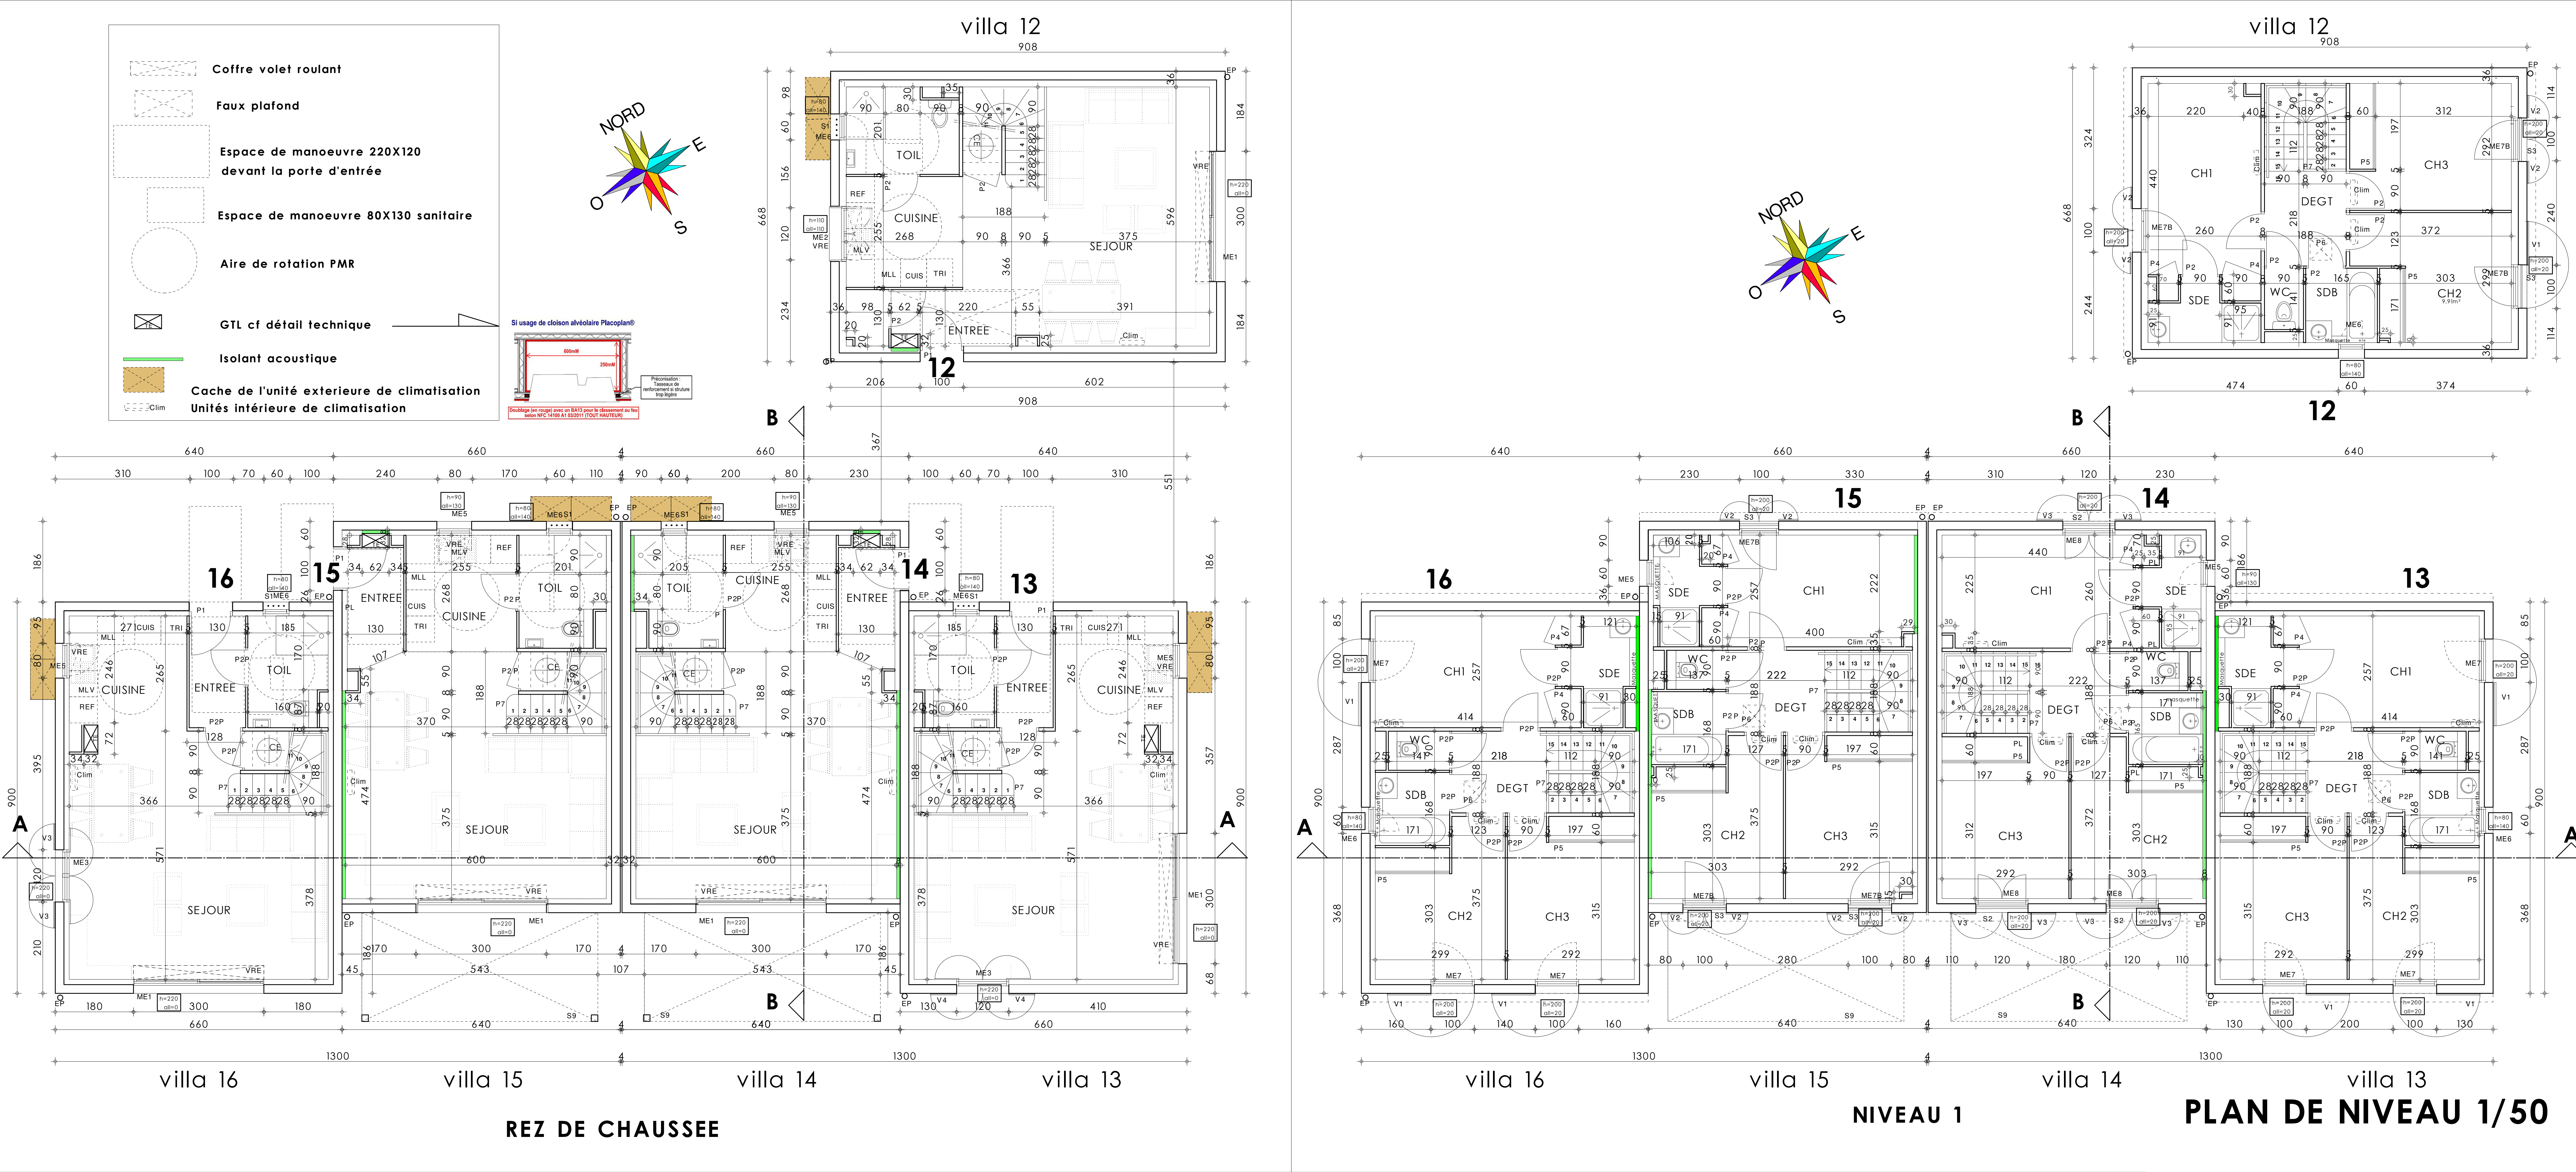

villa 14

COUPES 1/50

GRANDE TERRE			
INDICE	DATE	MODIFICATIONS	
A	15/06/2026	MODIFICATIONS SUITE REUNION DCE	
B	29/06/2026	SUPPRESSION LAVE MAIN DANS LES VILLAS COUTS MAITRISES	
C	06/07/2026	MODIFICATION TE ET IOLANT ACOUSTIQUE	
D			
E			
F			
G			
H			
I			
J			
K			
L			
ARCHITECTES M. CHAUVET A.C. CARNAZZA ARCHITECTES D.I.G. Entrepreneurs Individuels 40 Rue FARGES 13008 MARSEILLE P.L.Chaudet@grandeterre.fr A.C.Carnazza@grandeterre.fr		MATRE D'OUVRAGE SCCV GRANDE TERRE (SIRET 742 743 709 R.C.S. Toulouse) OPERATION RUE NEUVE GRAND TERRE 13930 AUREILLE	
DATE 15/04/2026 PROJETS 1/50 ETAT DU PLAN PLANS COUPES VILLAS 12-2016 PMR		A.P.S. P.G. D.C.E. MARCHE	
		104	