




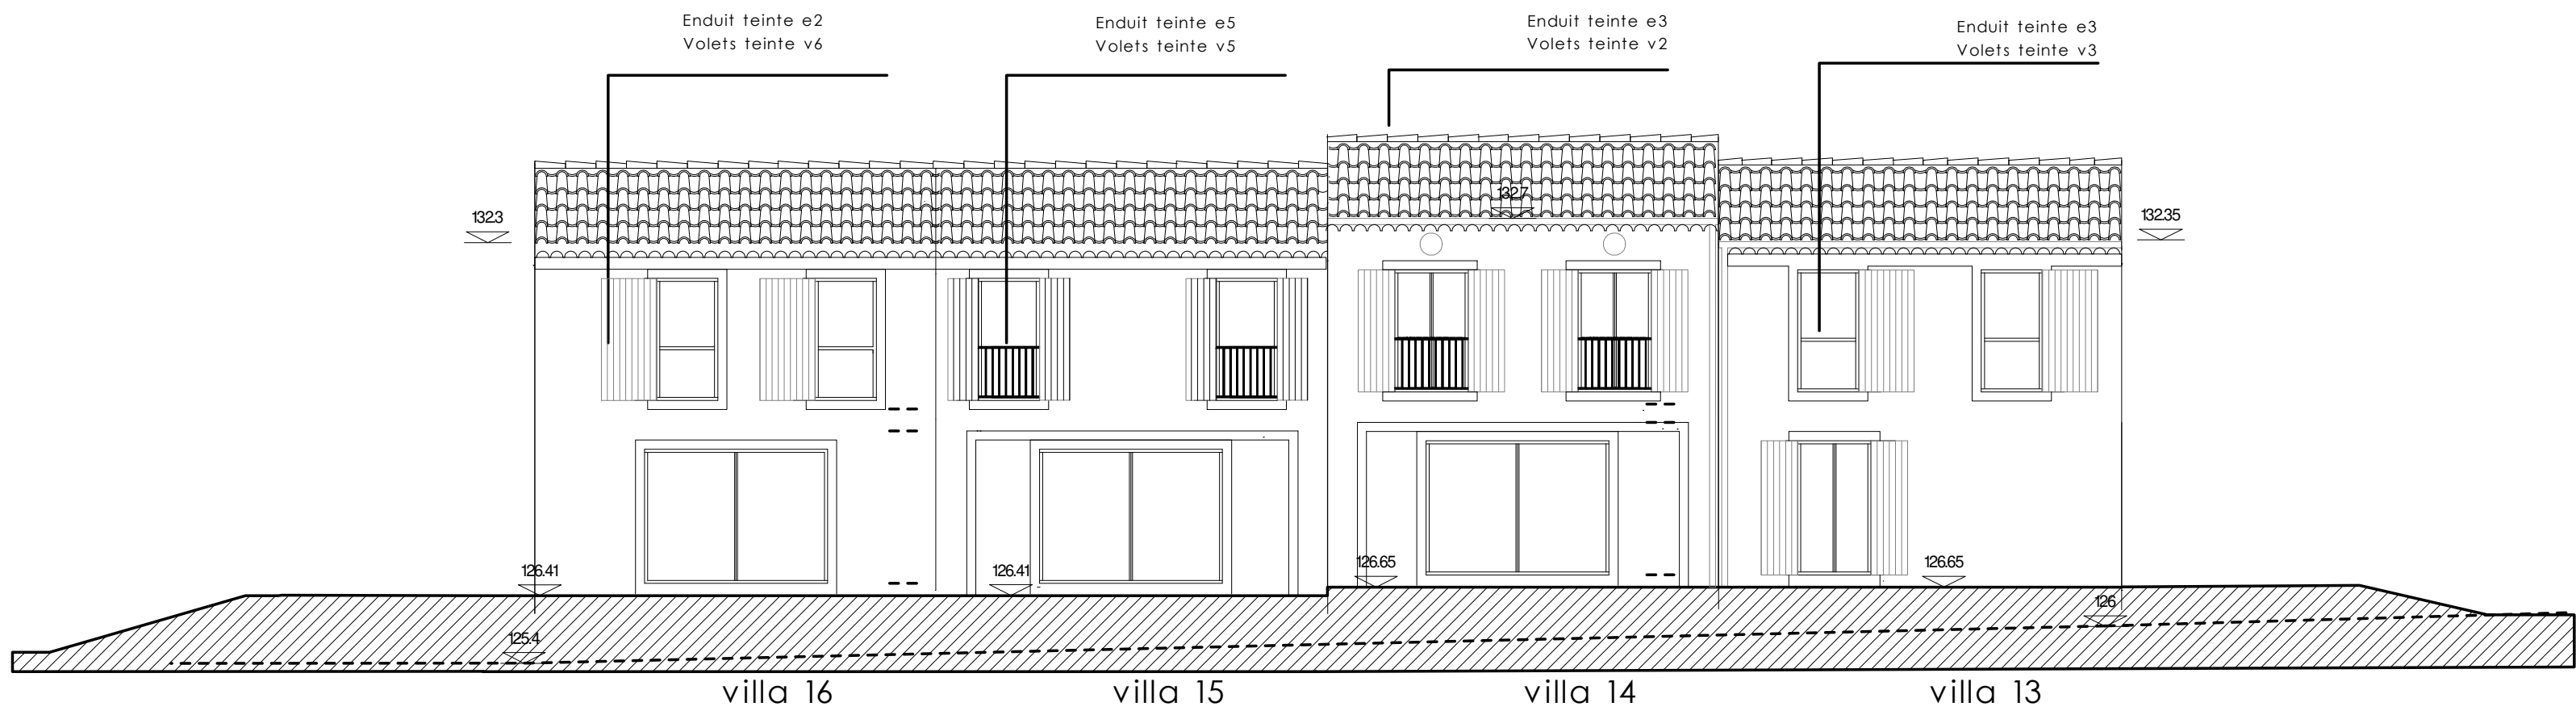


FACADES SUD

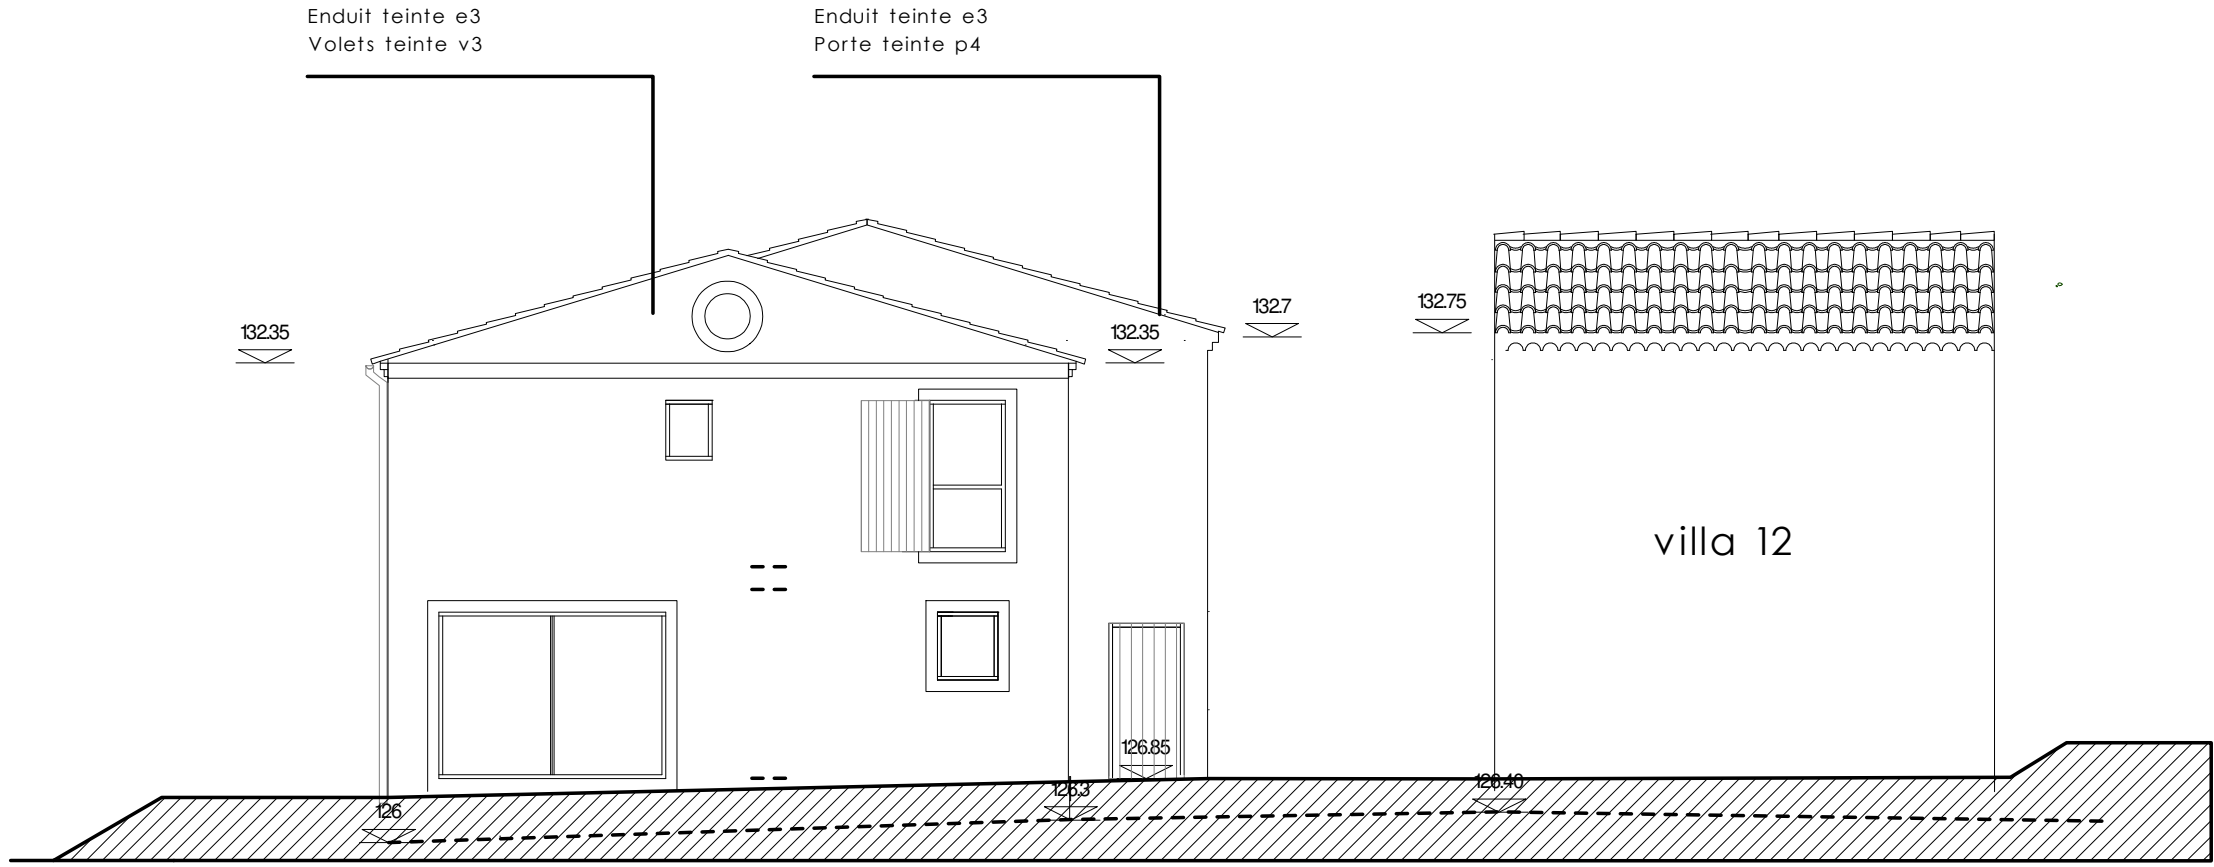


FACADE EST VILLA 13

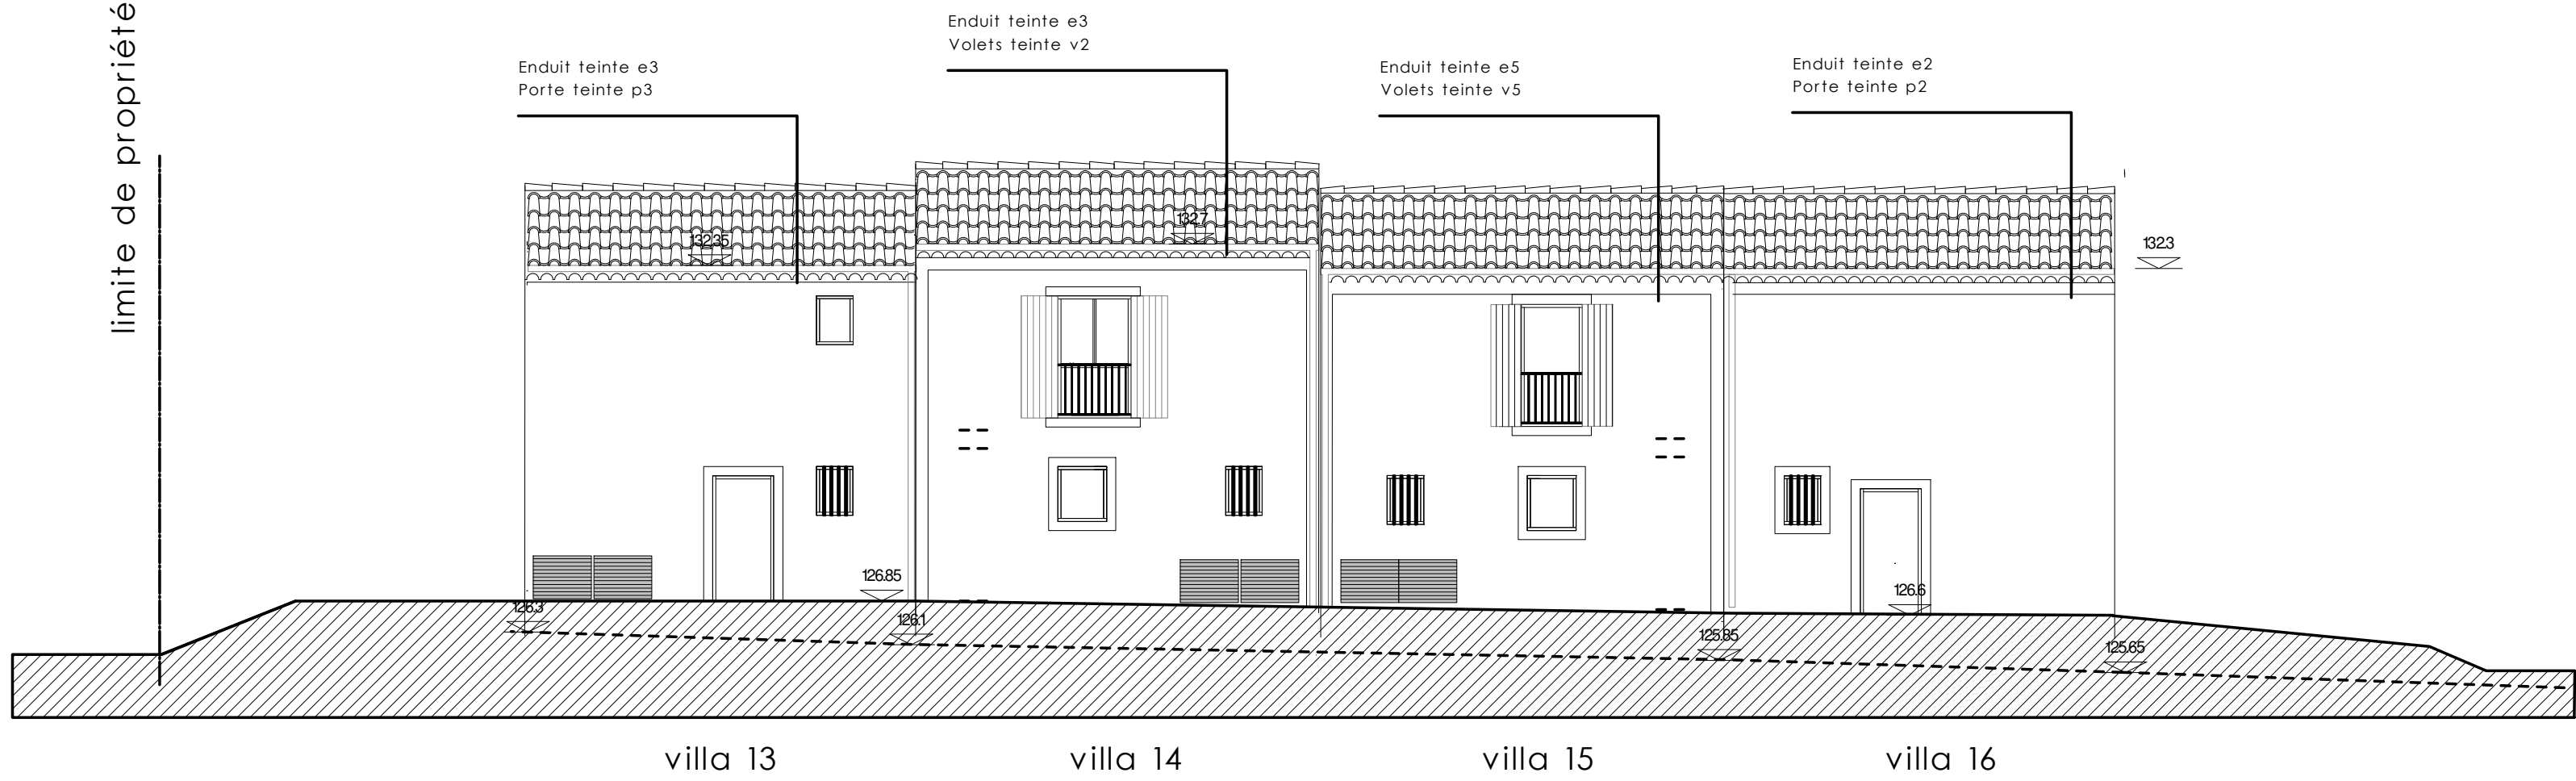


FACADES NORD

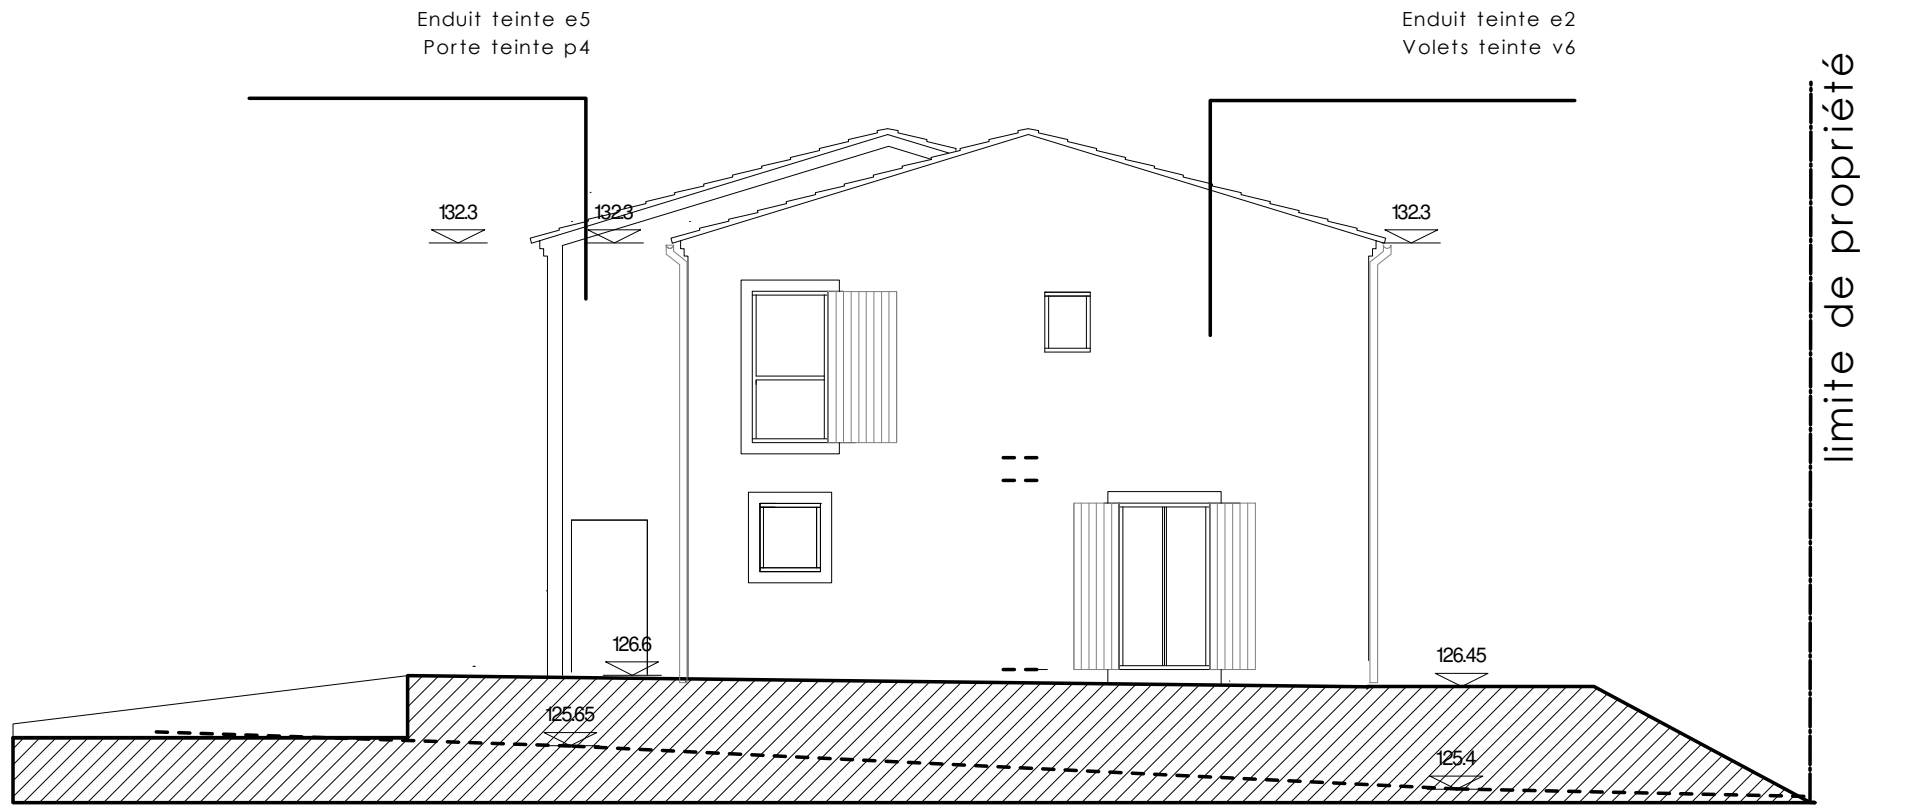


FACADE OUEST VILLA 16

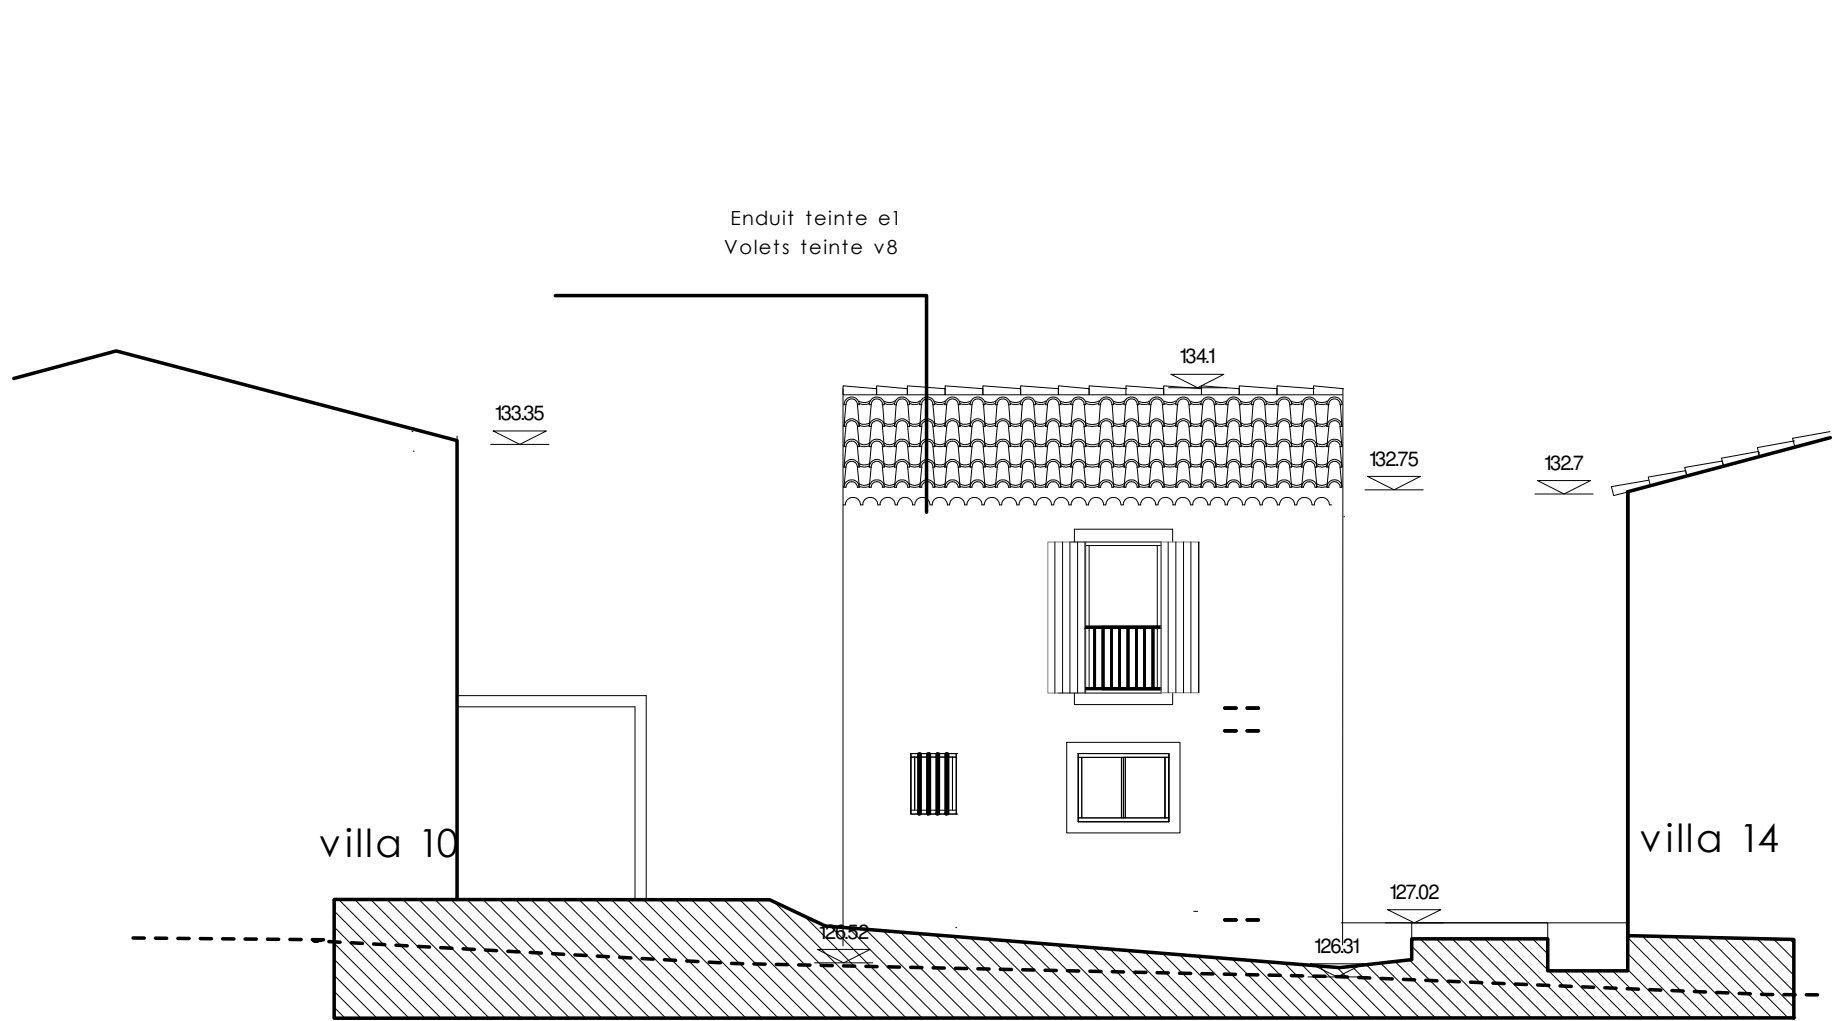


FACADE OUEST VILLA 12

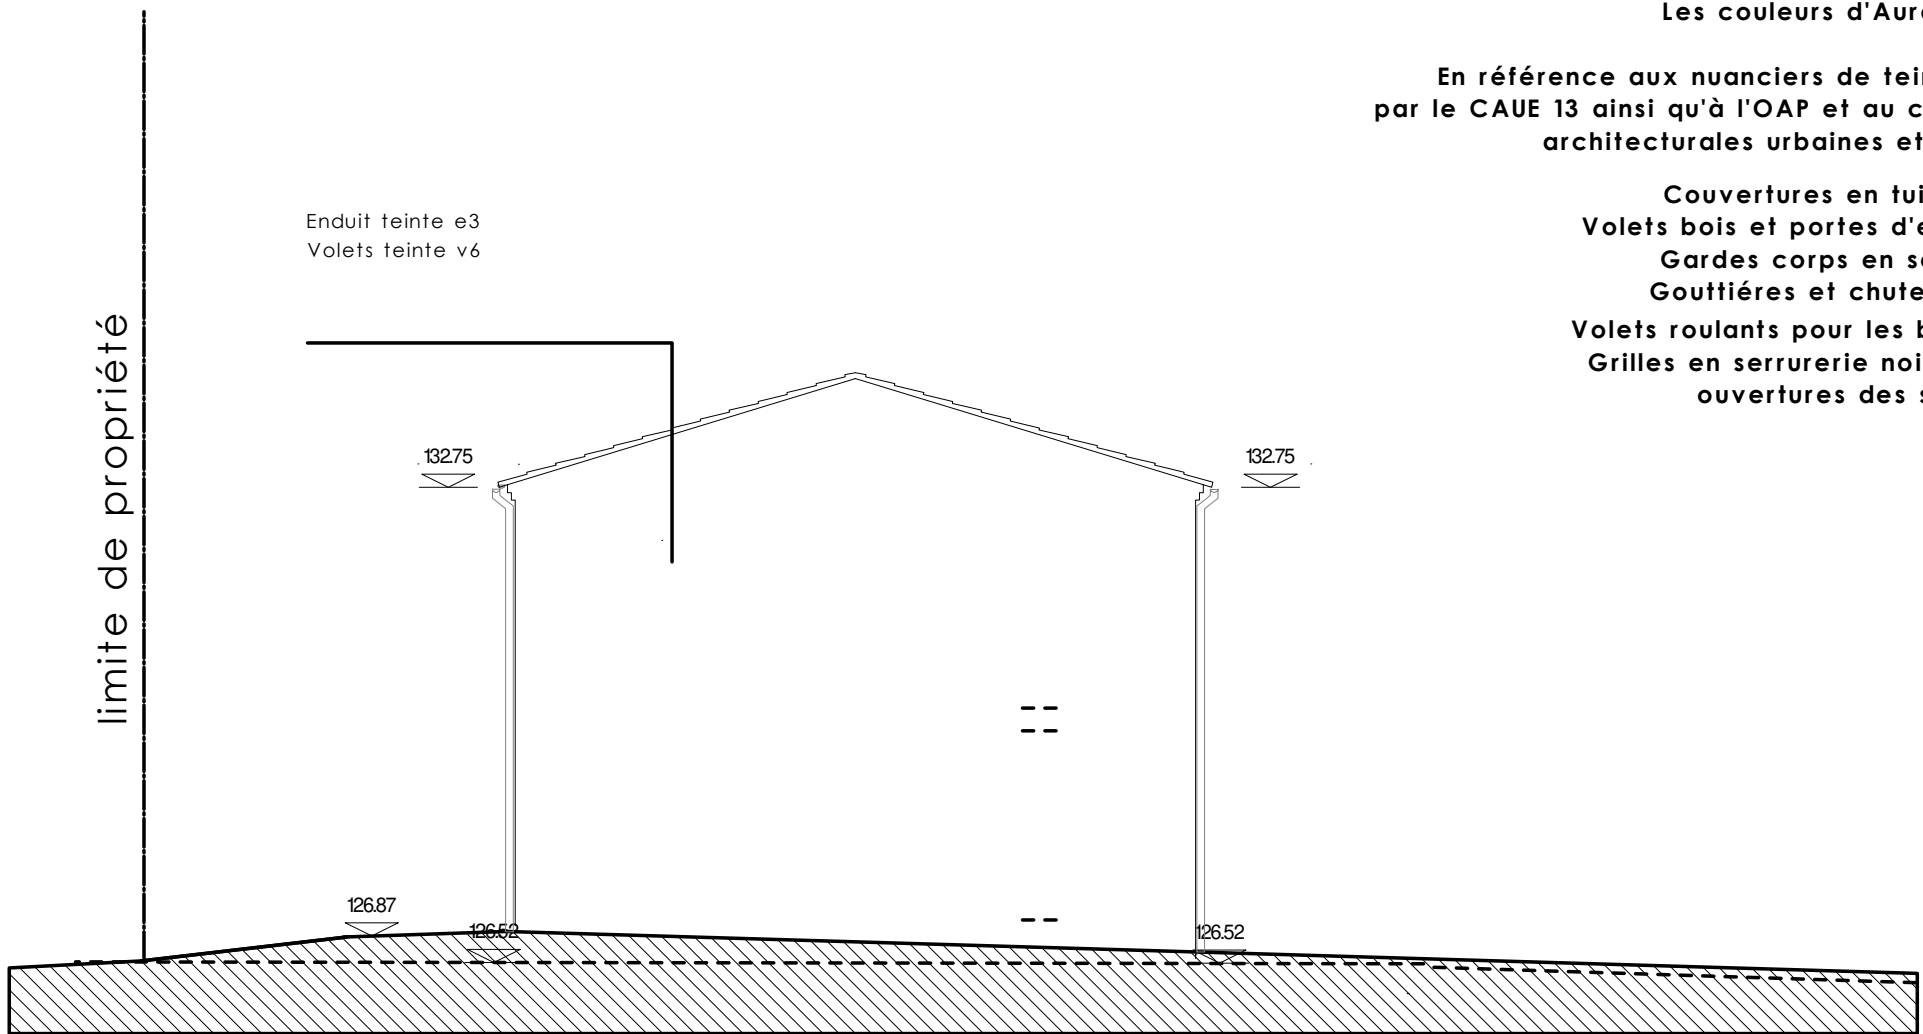

FACADES NORD VILLA 12

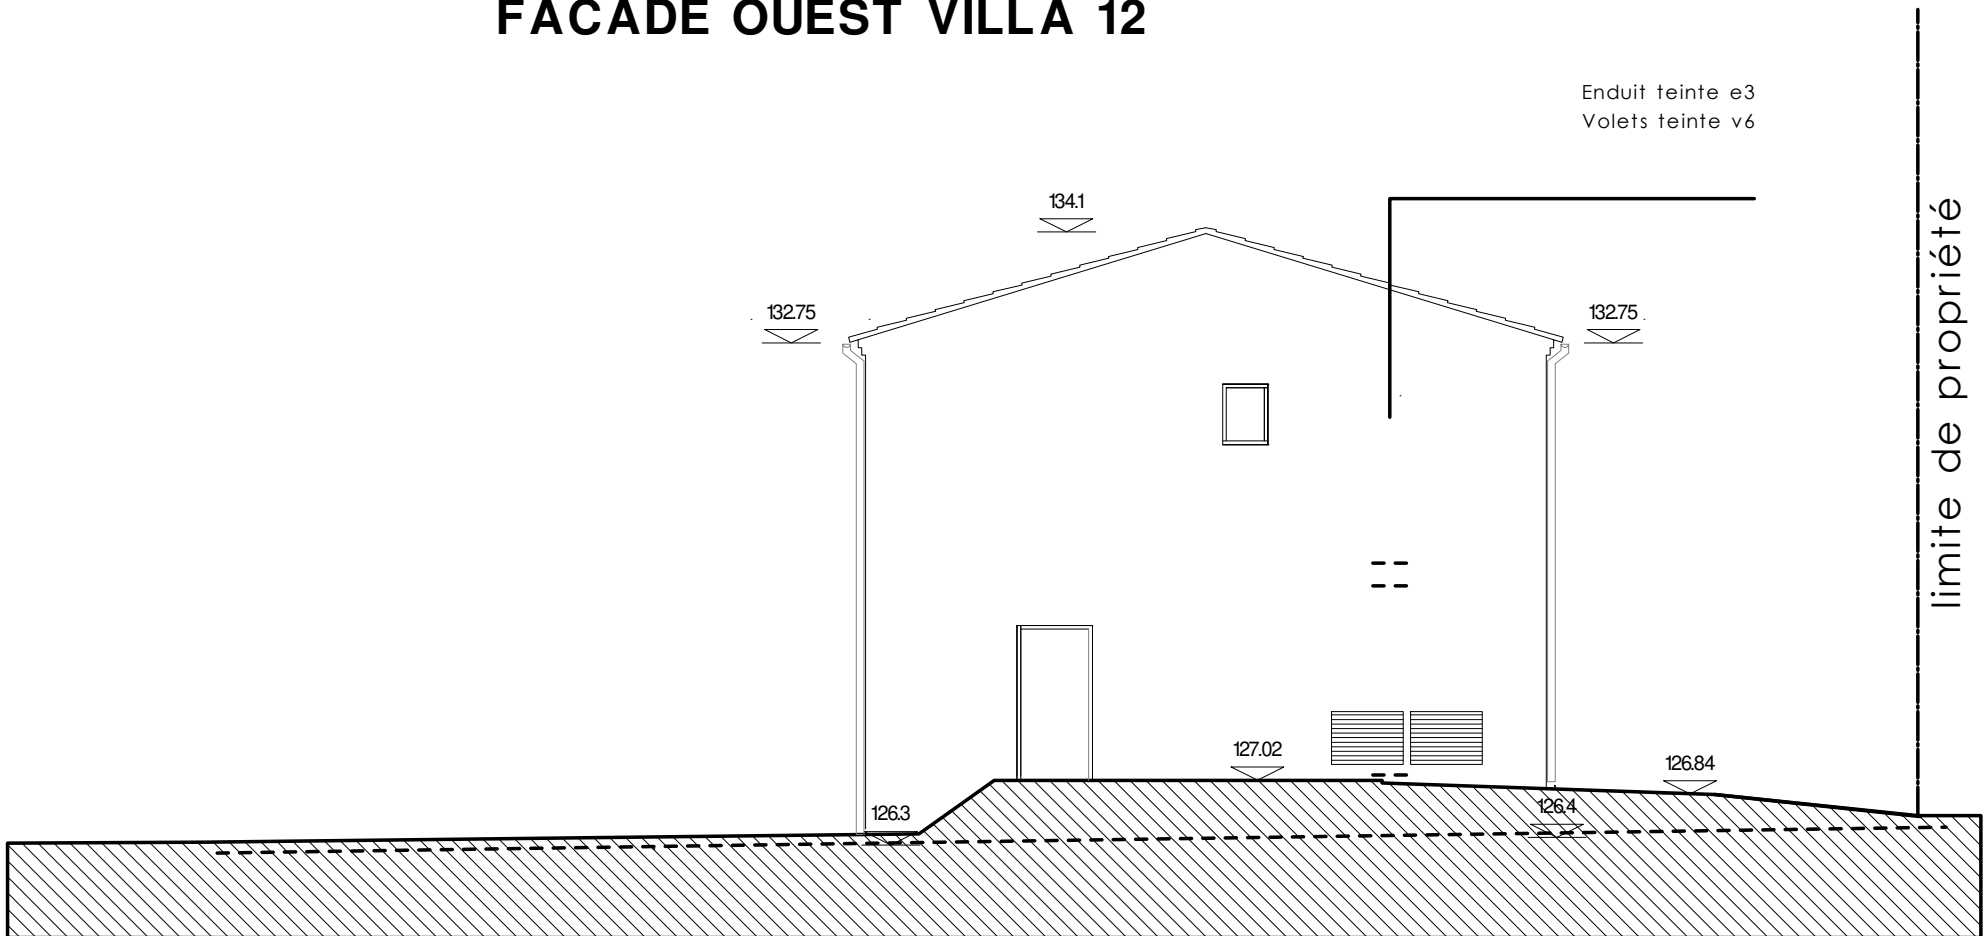

FACADE SUD VILLA 12

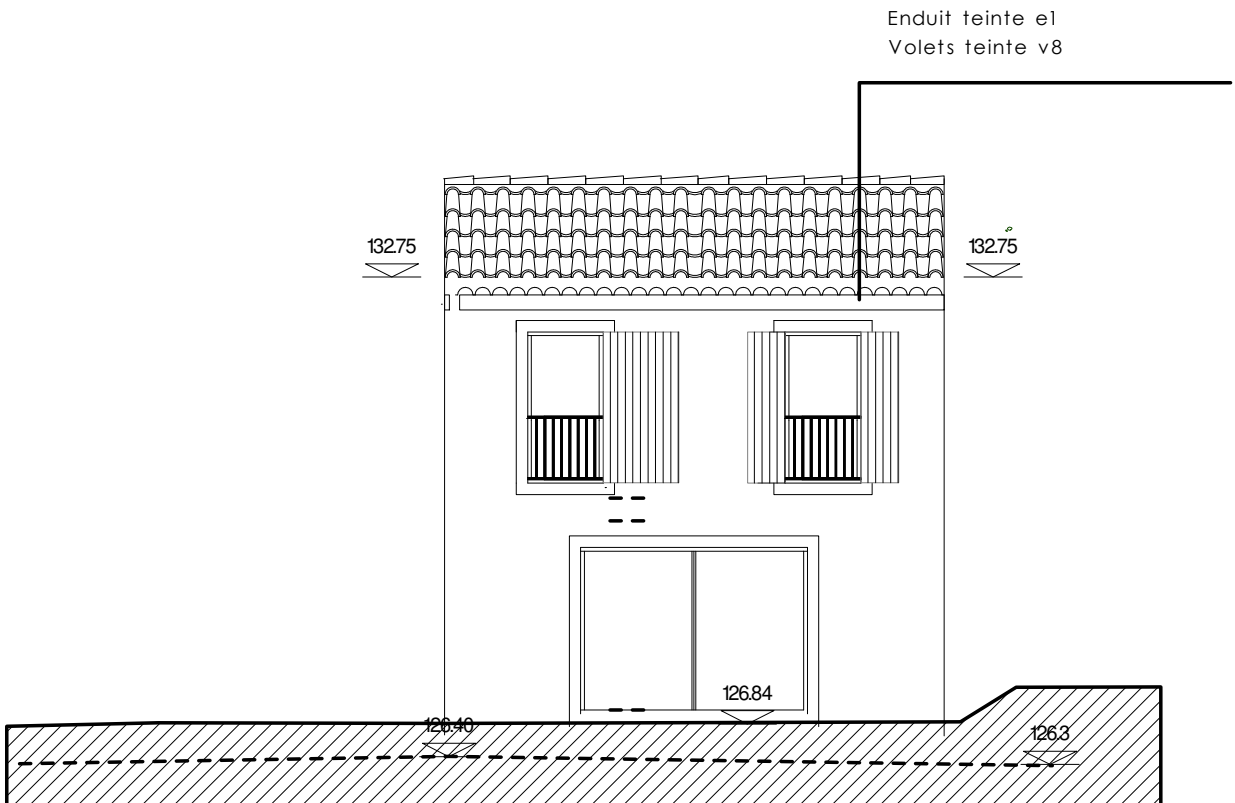

FACADE EST VILLA 12

Les couleurs d'Aureille

En référence aux nuanciers de teintes recommandées par le CAUE 13 ainsi qu'à l'OAP et au cahier de rommandations architecturales urbaines et paysagères

Couvertures en tuile canal
Volets bois et portes d'entrée en bois
Gardes corps en serrurerie
Gouttières et chutes en zinc
Volets roulants pour les baies du rdc
Grilles en serrurerie noire pour les ouvertures des sdb



INDICE	DATE	MODIFICATIONS
A	15/06/2026	MODIFICATIONS SUITE REUNION DCE
B		
C		
D		
E		
F		
G		
H		
I		
J		
K		
L		

ARCHITECTES M. CHAUVET A.C. CARNAZZA ARCHITECTES D.P.L.G. Entrepreneurs Individuels 40 Rue FARGES 13008 MARSEILLE m.chauvet@wanadoo.fr ac.vernet13@gmail.com	MAITRE D'OUVRAGE		DATE	15/04/2026	A.P.S.
	SCCV GRANDE TERRE (SIRET 942 743 709 R.C.S. Toulon)		ECHELLE	1/100	P.C.
	OPERATION		TITRE DU PLAN	FACADES VILLAS 12 à 16	D.C.E.
	RUE NEUVE GRAND TERRE 13930 AUREILLE				MARCHES