



Les couleurs d'Aureille


En référence aux nuanciers de teintes recommandées
par le CAUE 13 ainsi qu'à l'OAP et au cahier de rommandations
architecturales urbaines et paysagères
Volets roulants pour les baies du rdc
Grilles en serrurerie noire pour les
ouvertures des sdb

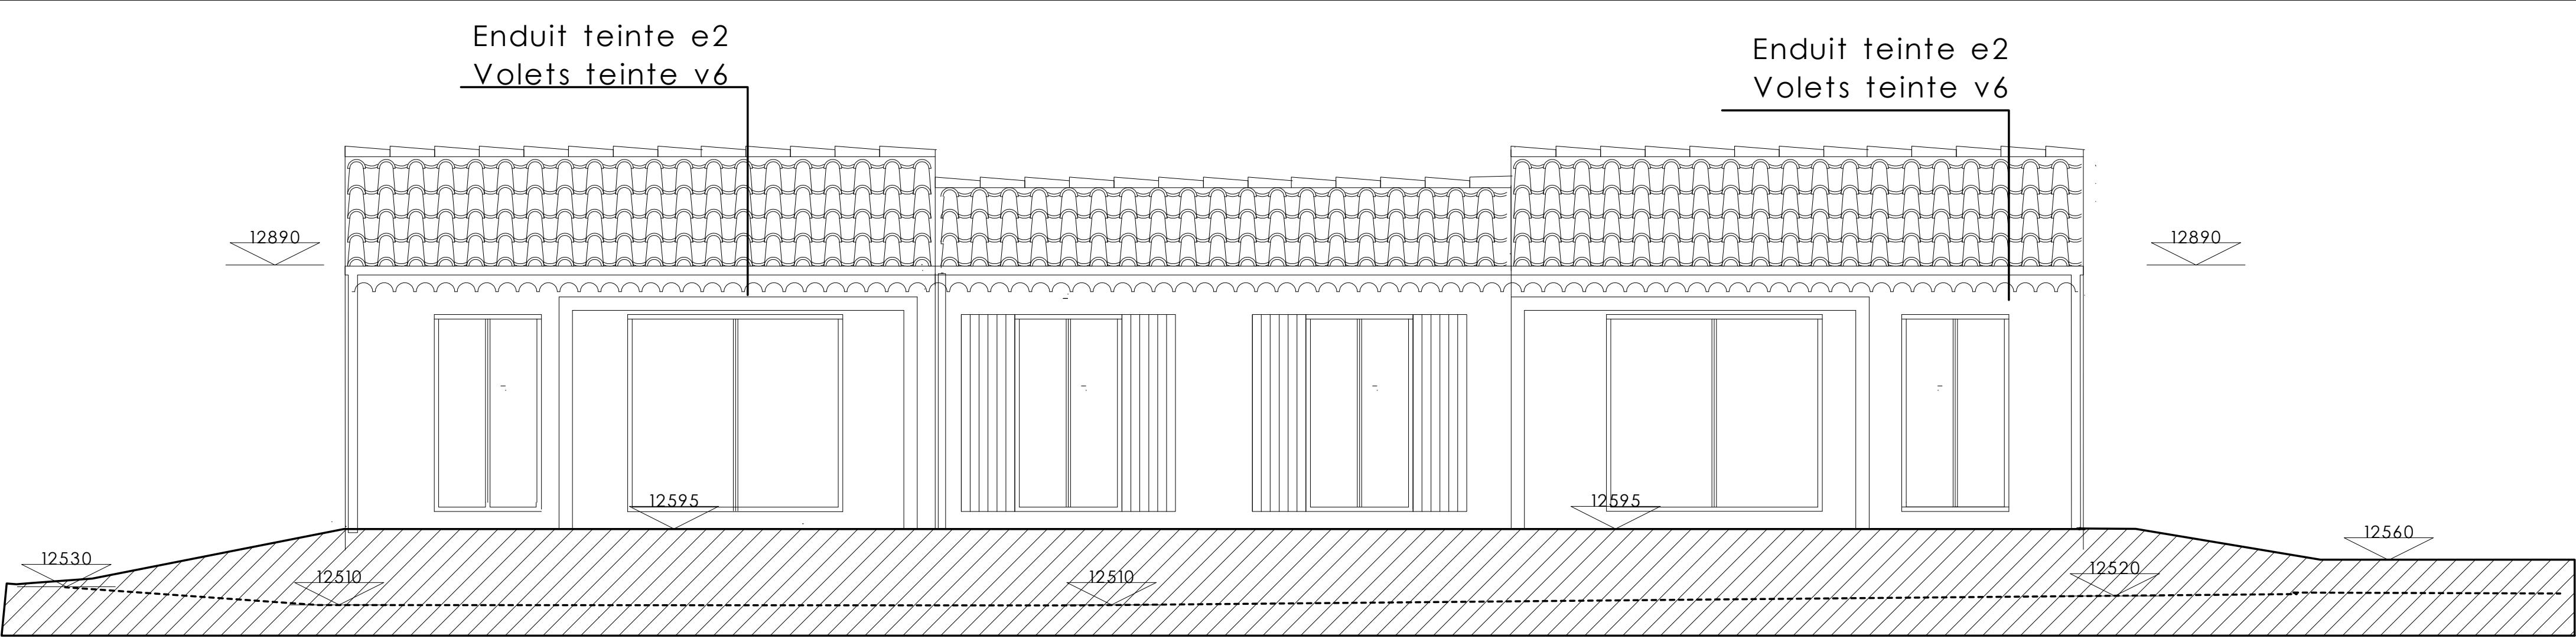

villa 18 FACADES SUD VILLAS 17 ET 18 villa 17

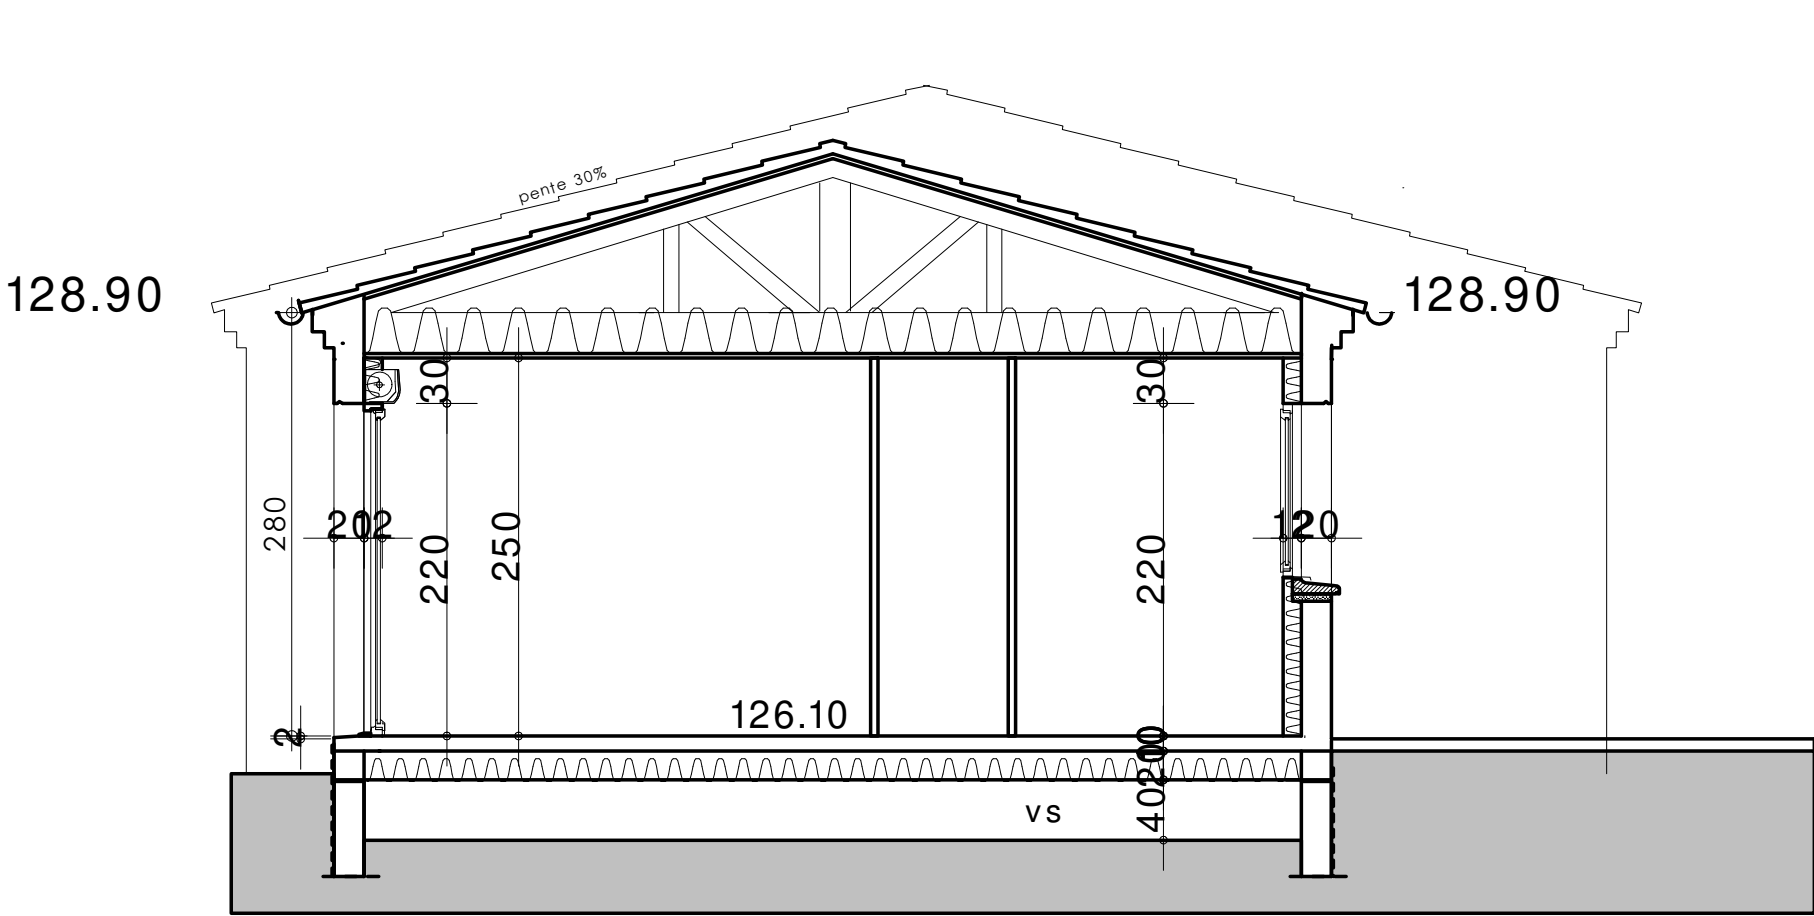


COUPE C-C

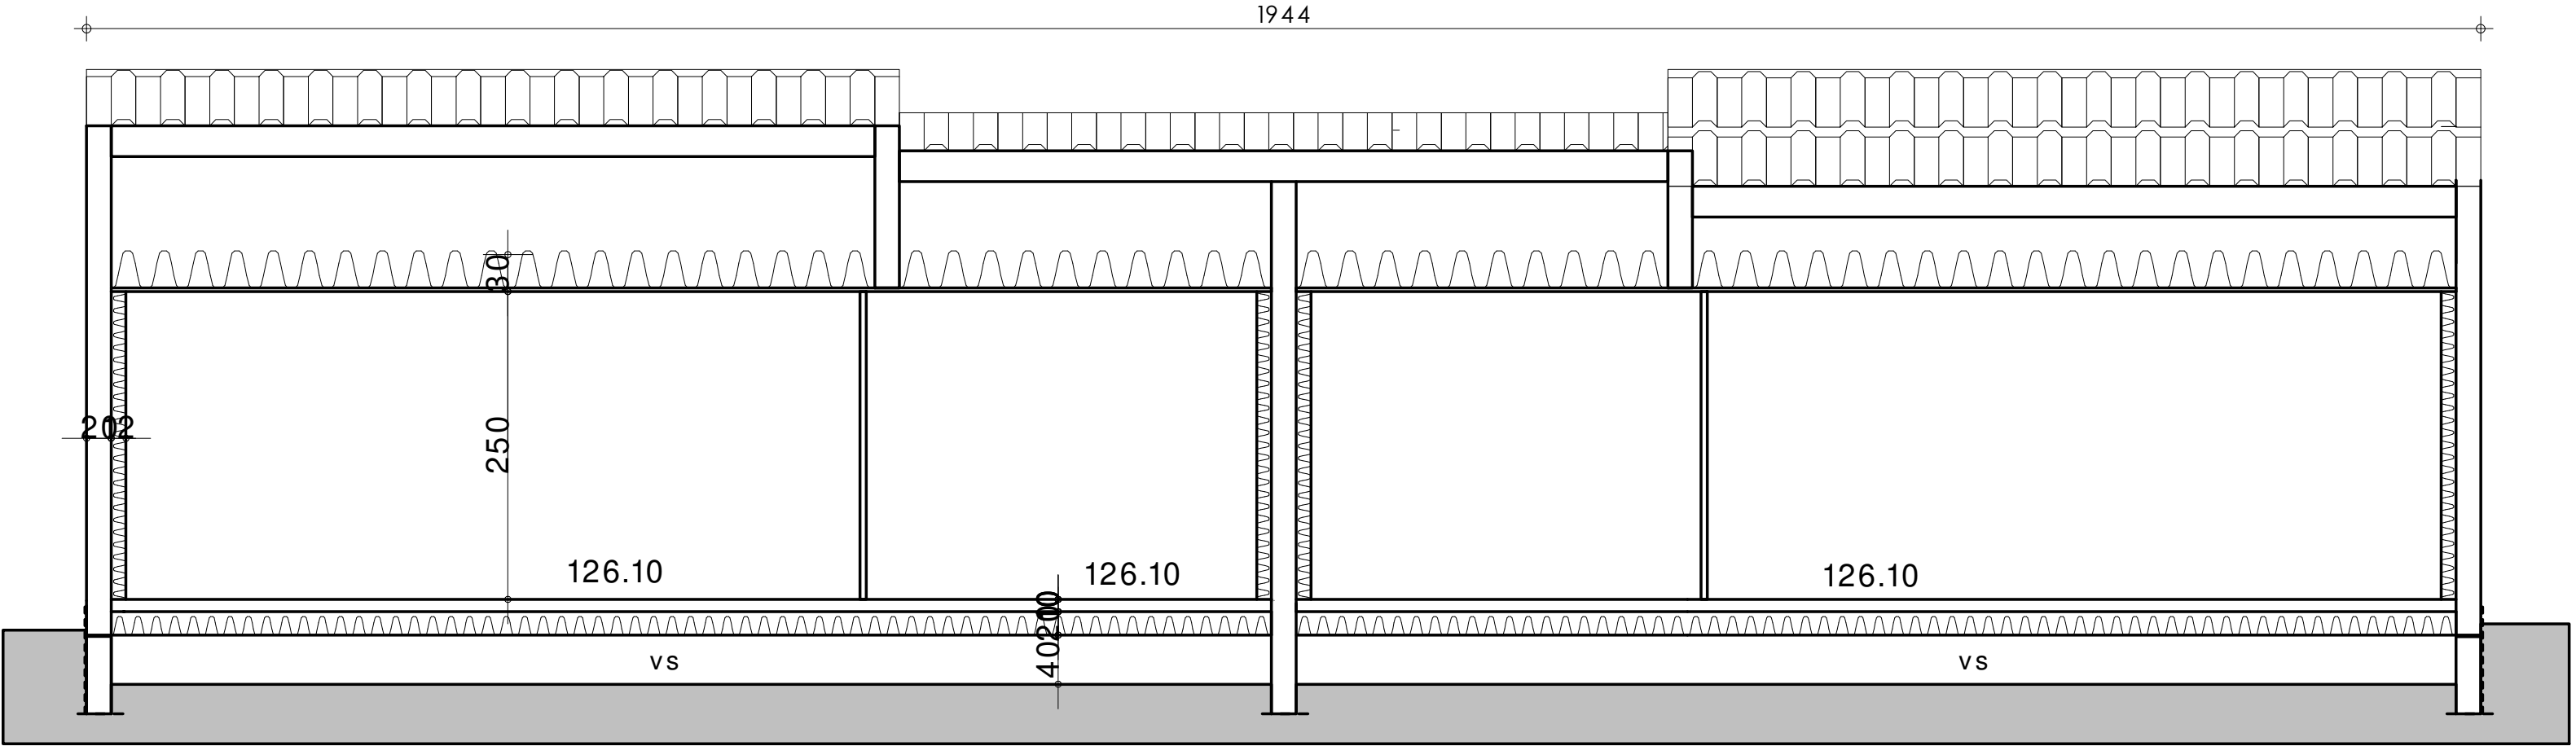


villa 18 villa 17


COUPE A-A

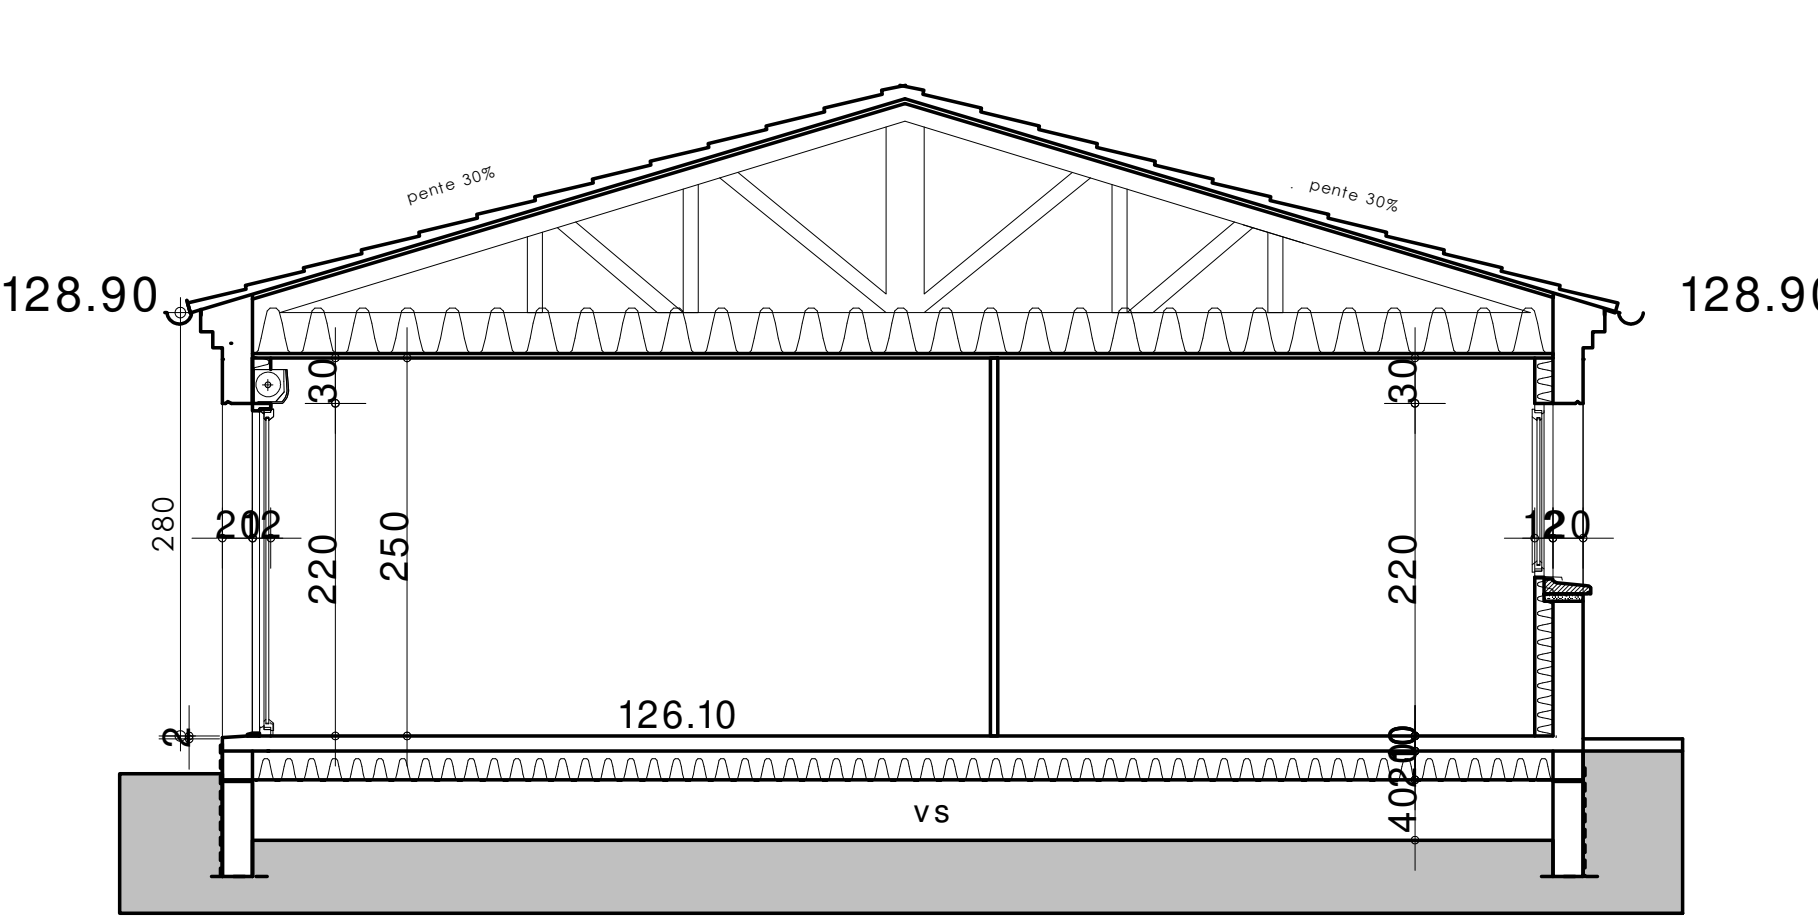

COUPE B-B

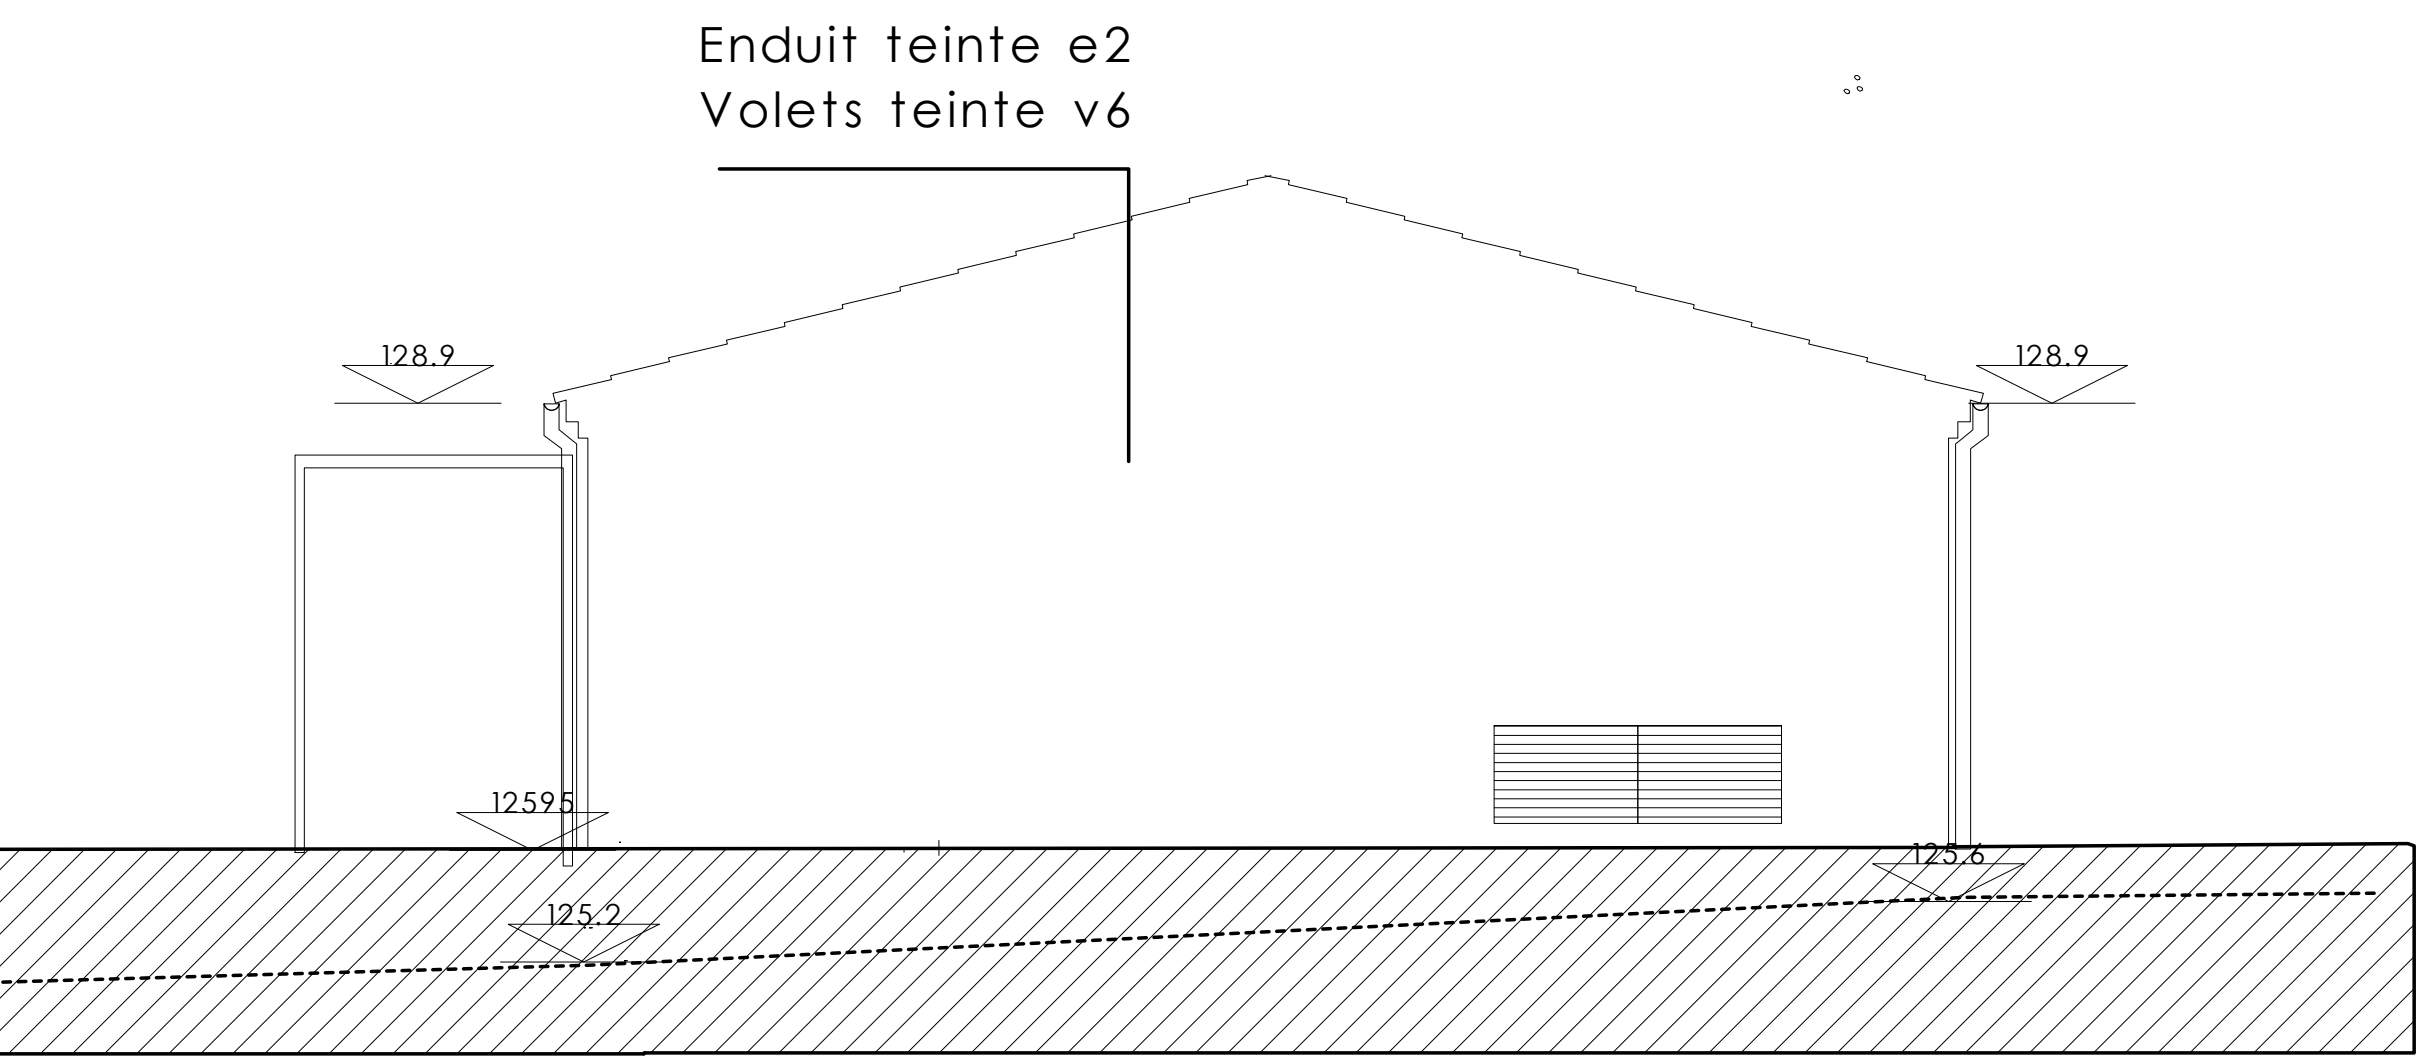


FACADE EST VILLA 17

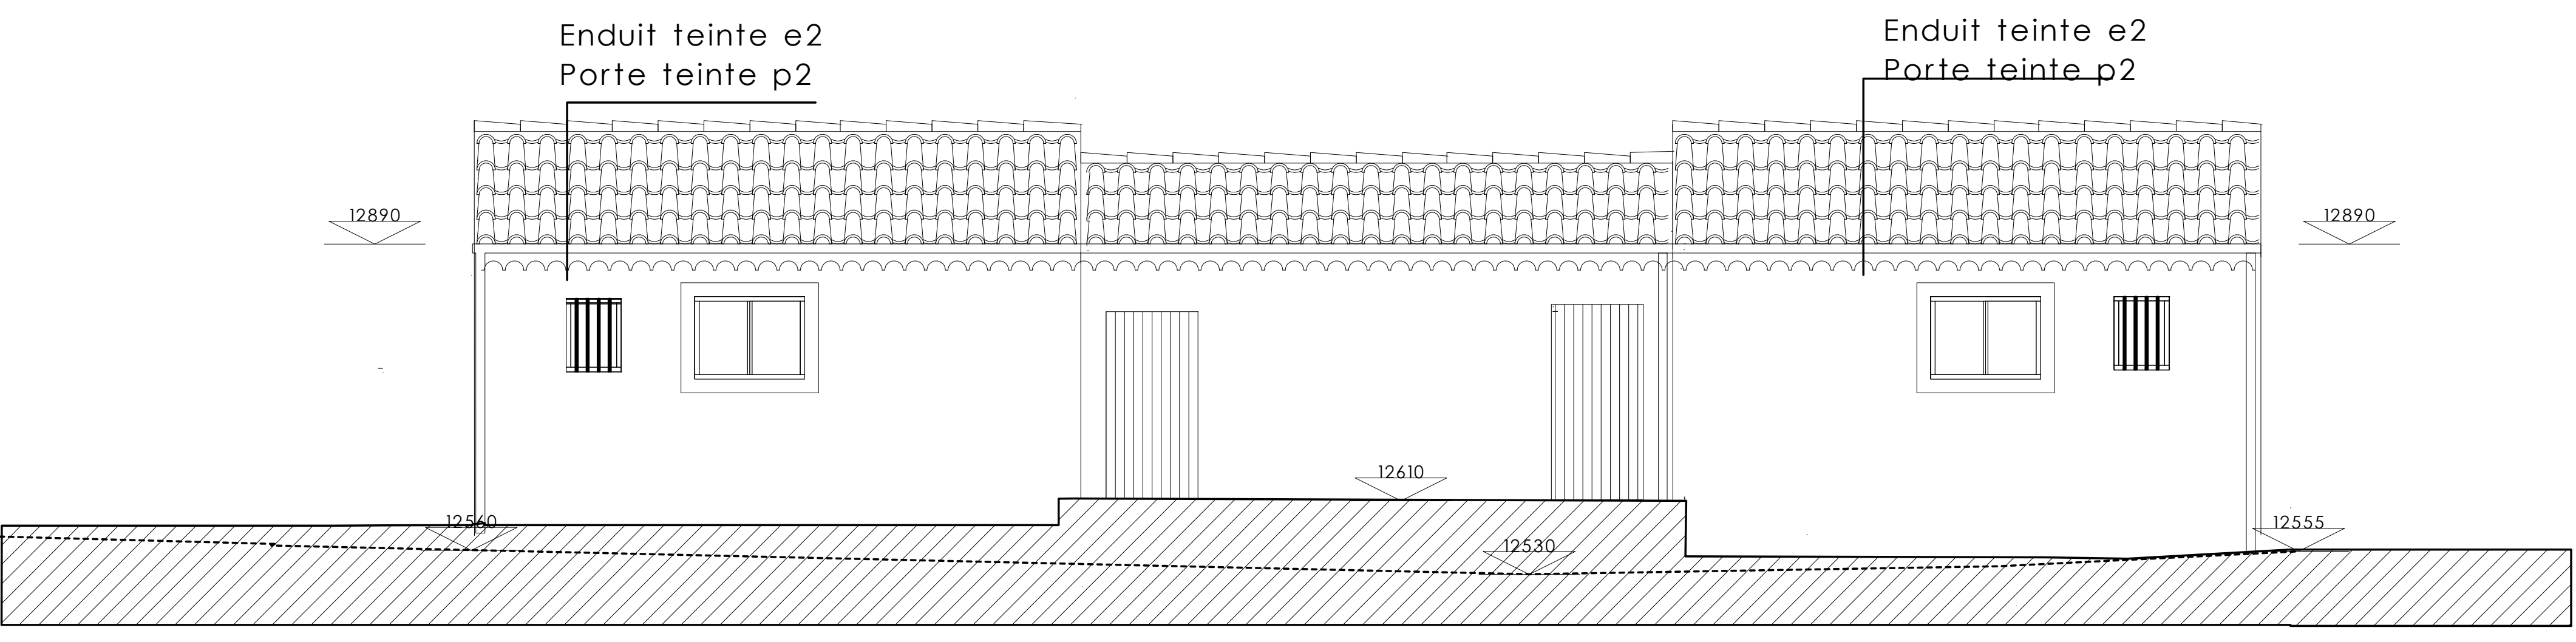


villa 17 FACADES NORD VILLAS 17 ET 18 villa 18


FACADES NORD VILLAS 17 ET 18

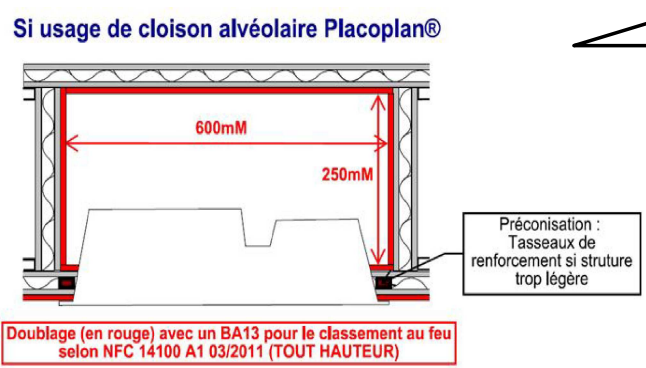


LEGENDE	
	Coffre volet roulant
	Faux plafond
	Espace de manoeuvre 220X120 devant la porte d'entrée
	Espace de manoeuvre 80X130 sanitaire
	Aire de rotation PMR
	GTL cf détail technique
	Isolant acoustique
	Cache de l'unité extérieure de climatisation Unités intérieure de climatisation

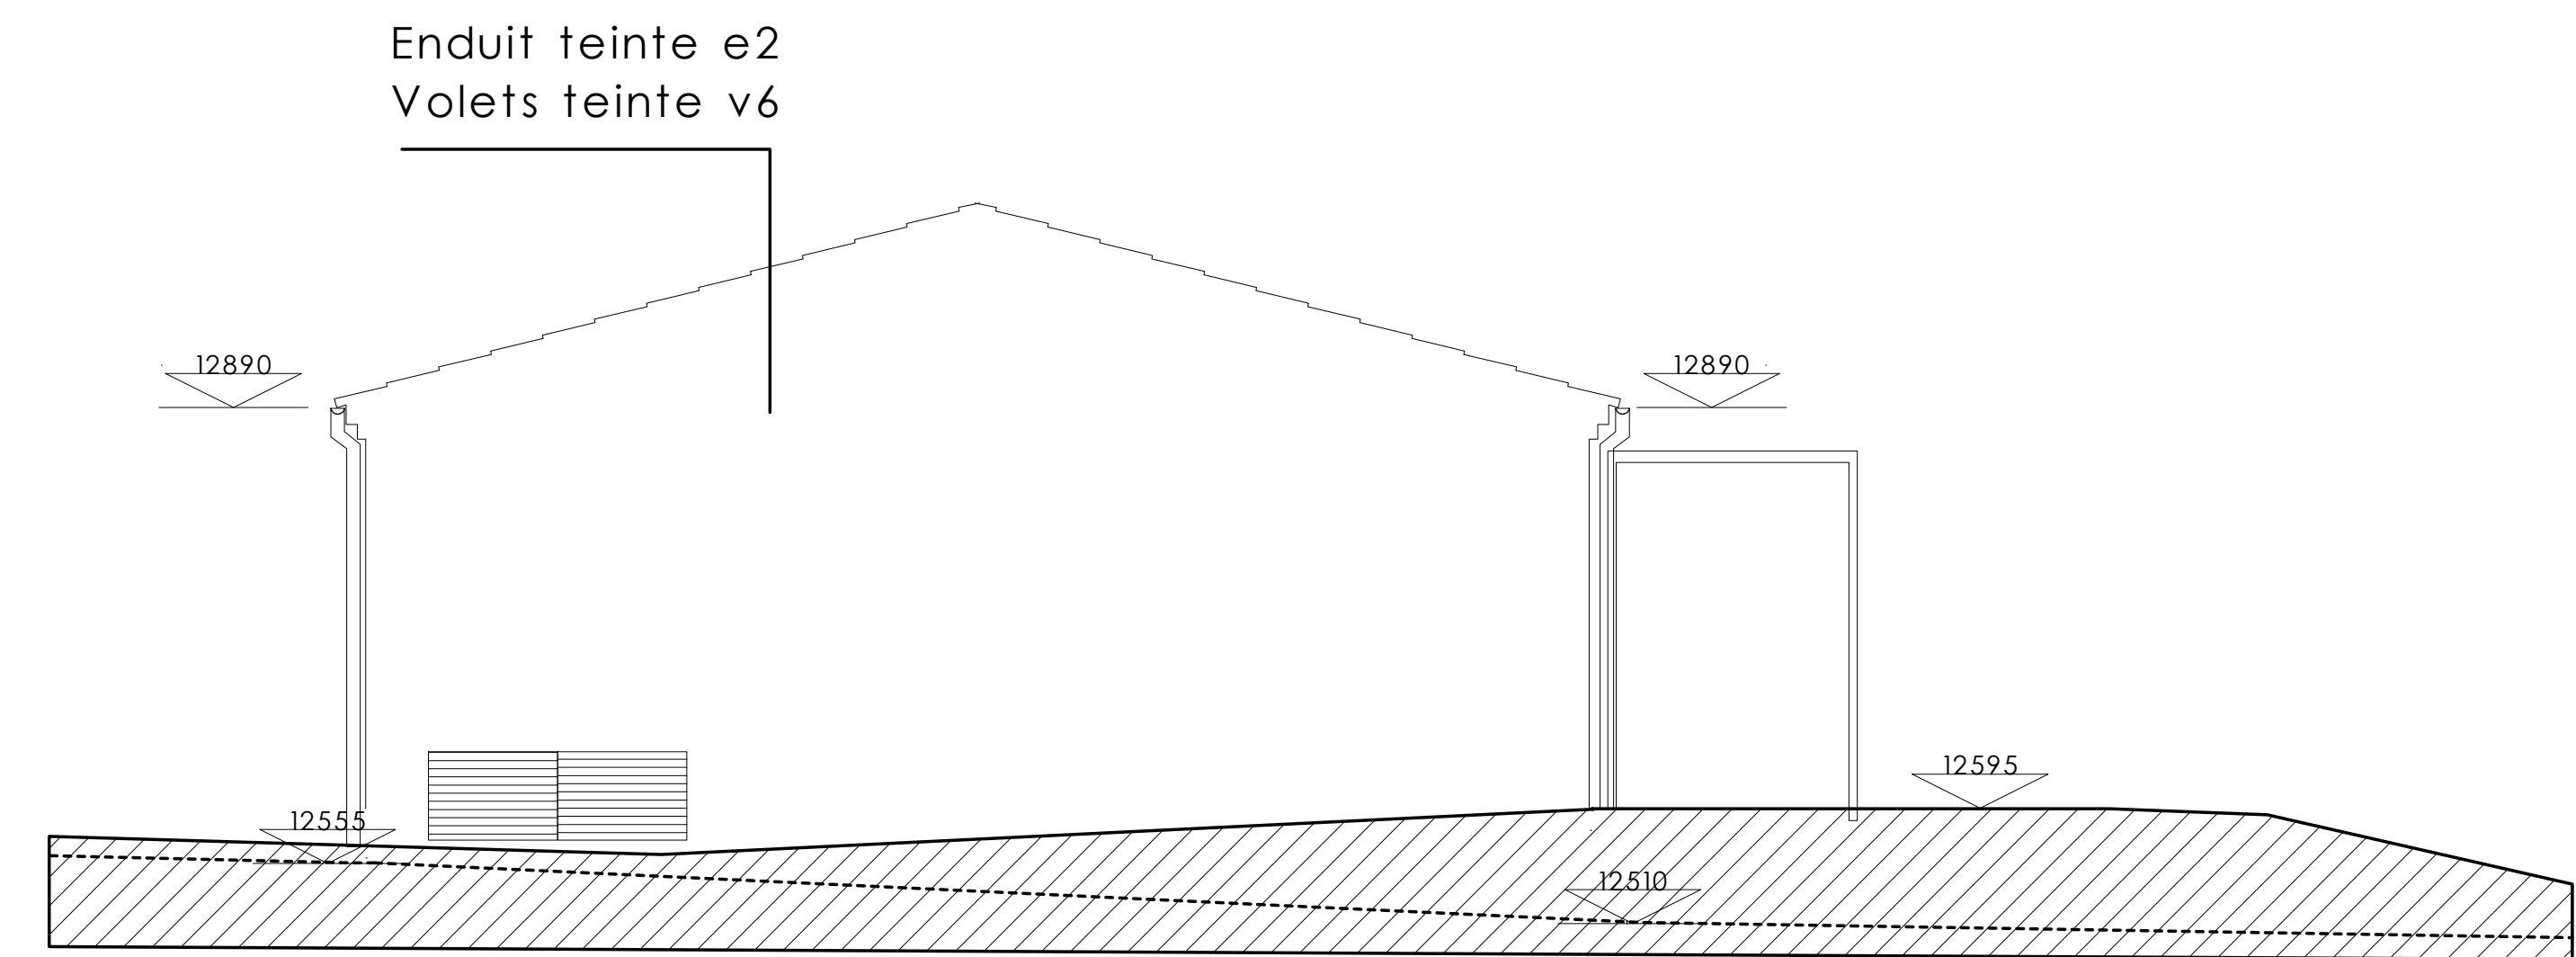

FACADE OUEST VILLA 18

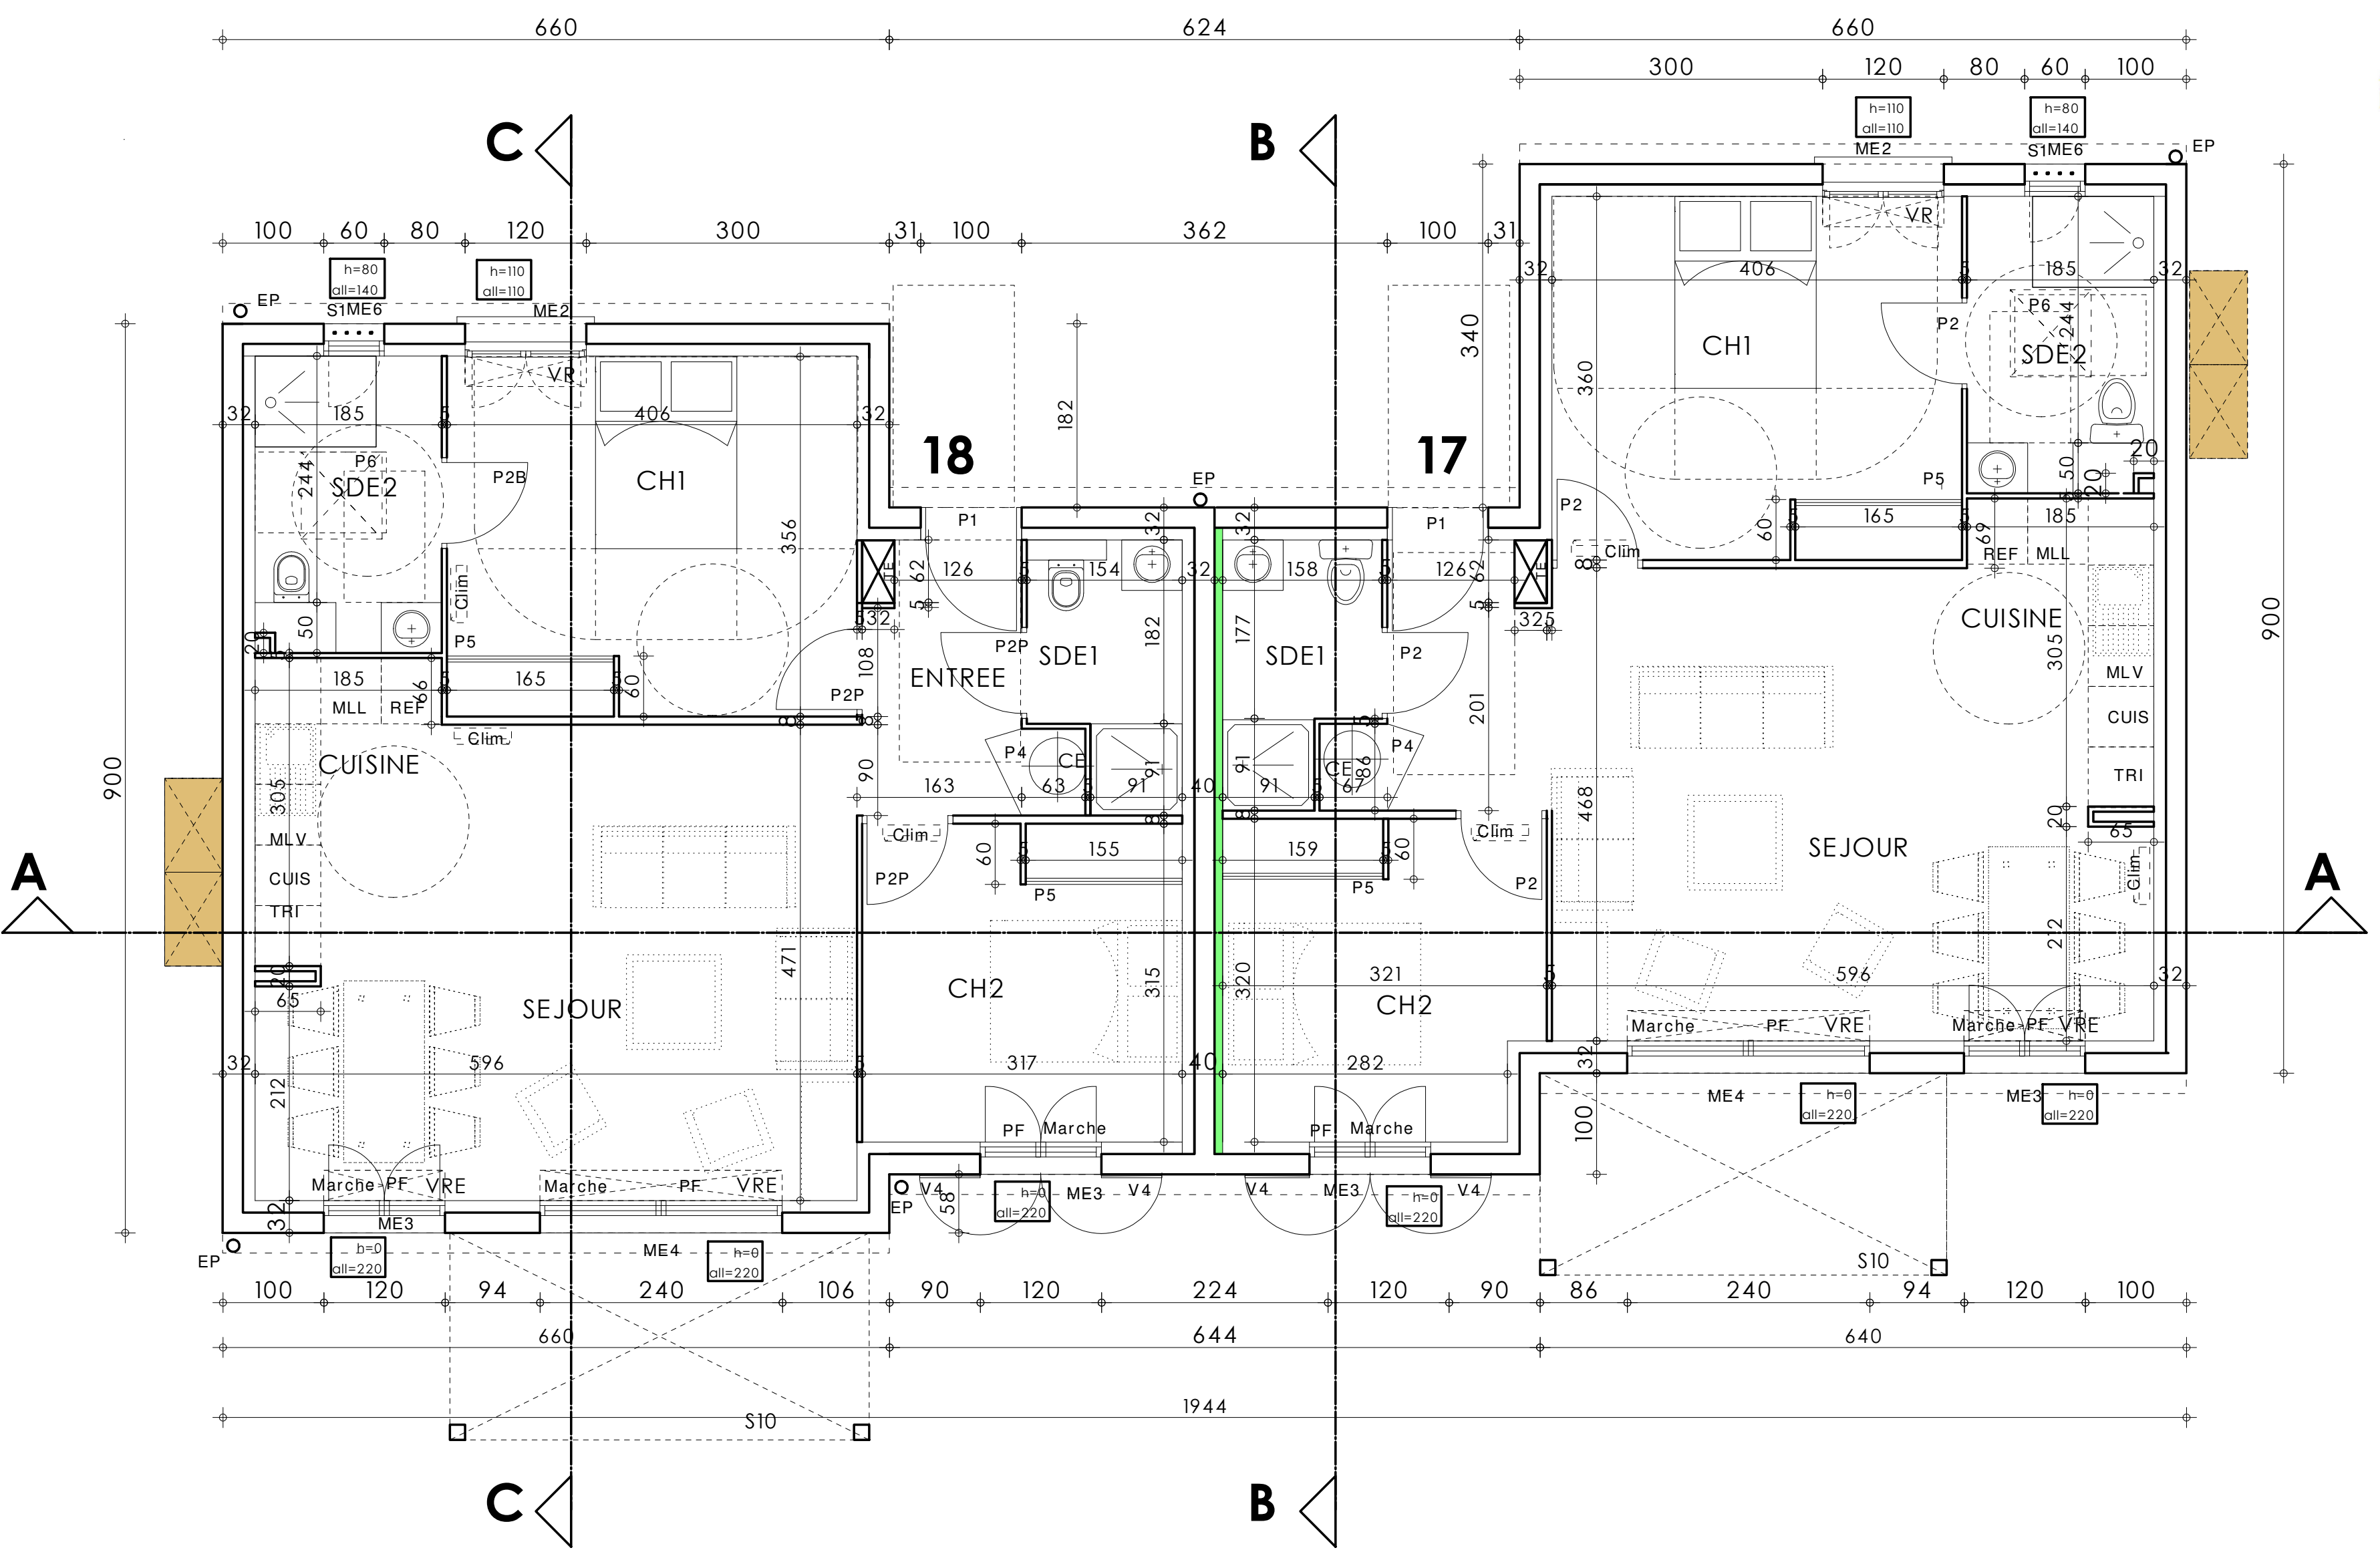

villa 18 villa 17

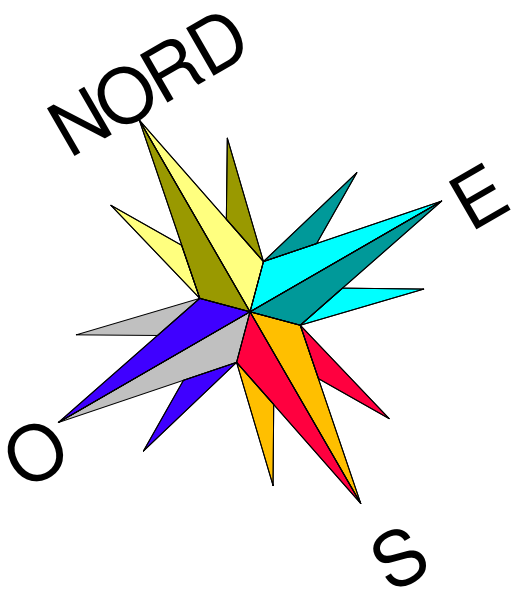

GRANDE TERRE			
INDICE	DATE	MODIFICATIONS	
A	15/06/2026	MODIFICATIONS SUITE REUNION DCE	
B	06/07/2026	MODIFICATION TE ET ISOLANT ACOUSTIQUE	
C			
D			
E			
F			
G			
H			
I			
J			
K			
L			

ARCHITECTES M CHAUVET A.C. CARNAZZA ARCHITECTES D.P.L.G. Entrepreneurs Individuels 40 Rue FARGES 13008 MARSEILLE m.chauvet@wardoc.fr ac.carnazza@gmail.com	MAITRE D'OUVRAGE SCCV GRANDE TERRE (SIRET 842 743 709 R.C.S. Toulon)	DATE 15/04/2026	A.P.S. P.C.
	OPERATION RUE NEUVE GRAND TERRE 13930 AUREILLE	ECHELLE 1/50	D.C.E.
		TITRE DU PLAN PLANS COUPES FACADES VILLAS 17 ET 18	MARCHES

106