



Les couleurs d'Aureille


En référence aux nuanciers de teintes recommandées
par le CAUE 13 ainsi qu'à l'OAP et au cahier de rommandations
architecturales urbaines et paysagères
Volets roulants pour les baies du rdc
Grilles en serrurerie noire pour les
ouvertures des sdb

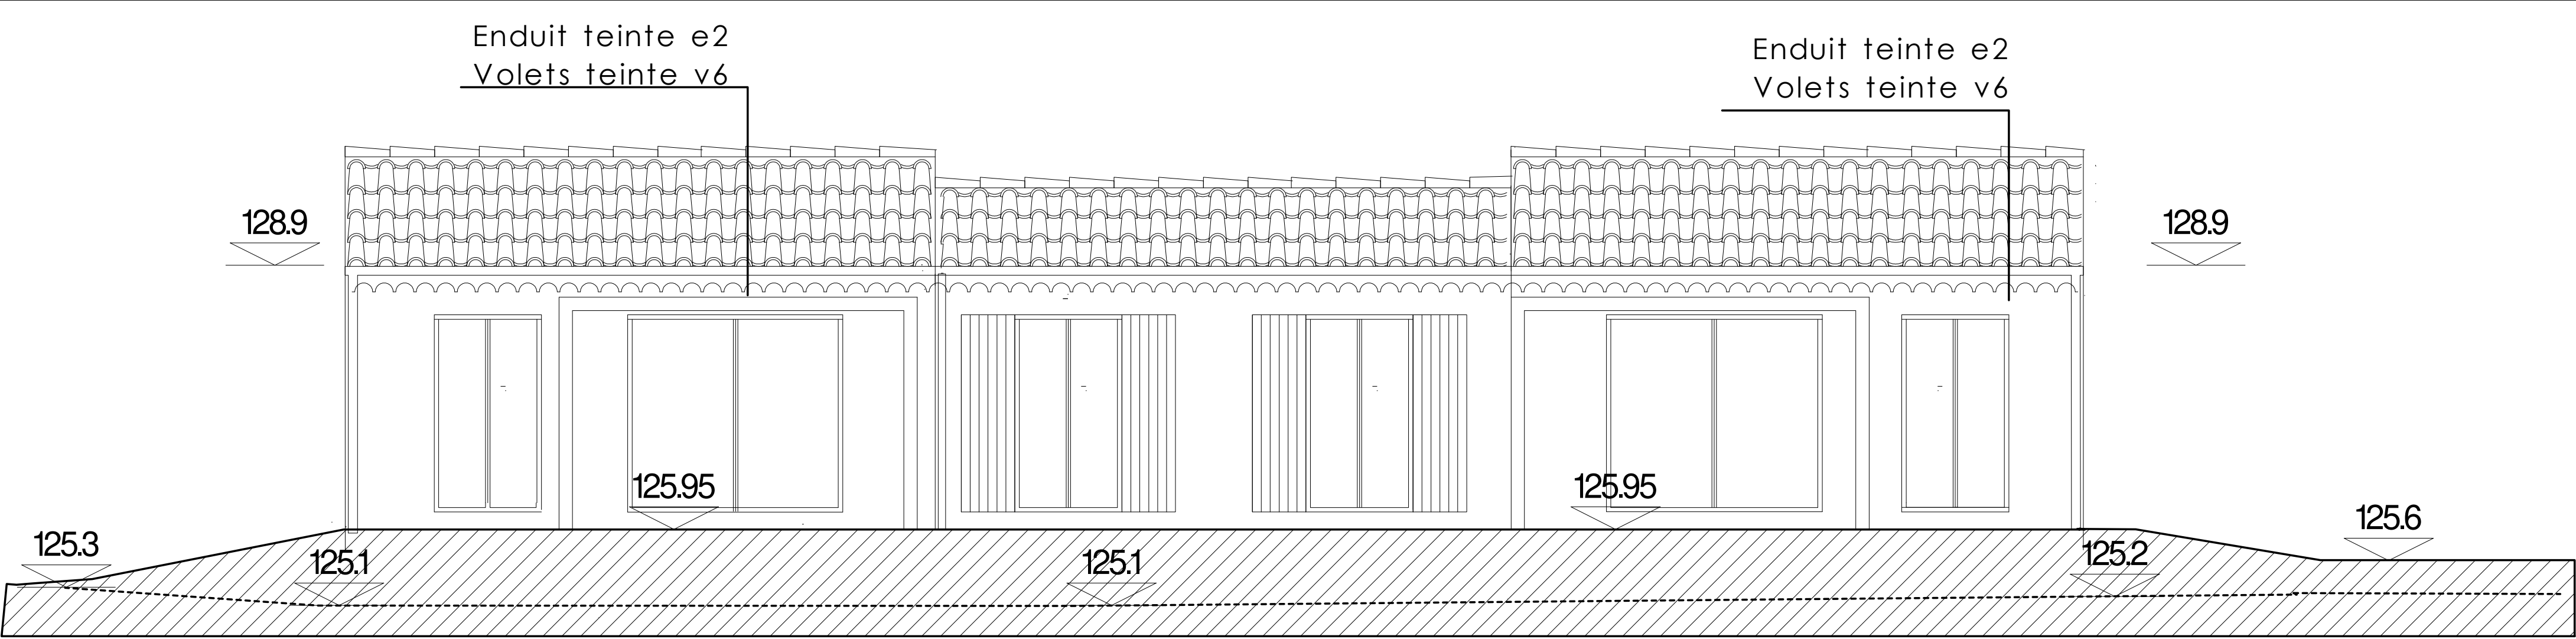


villa 18 FACADES SUD VILLAS 17 ET 18 villa 17

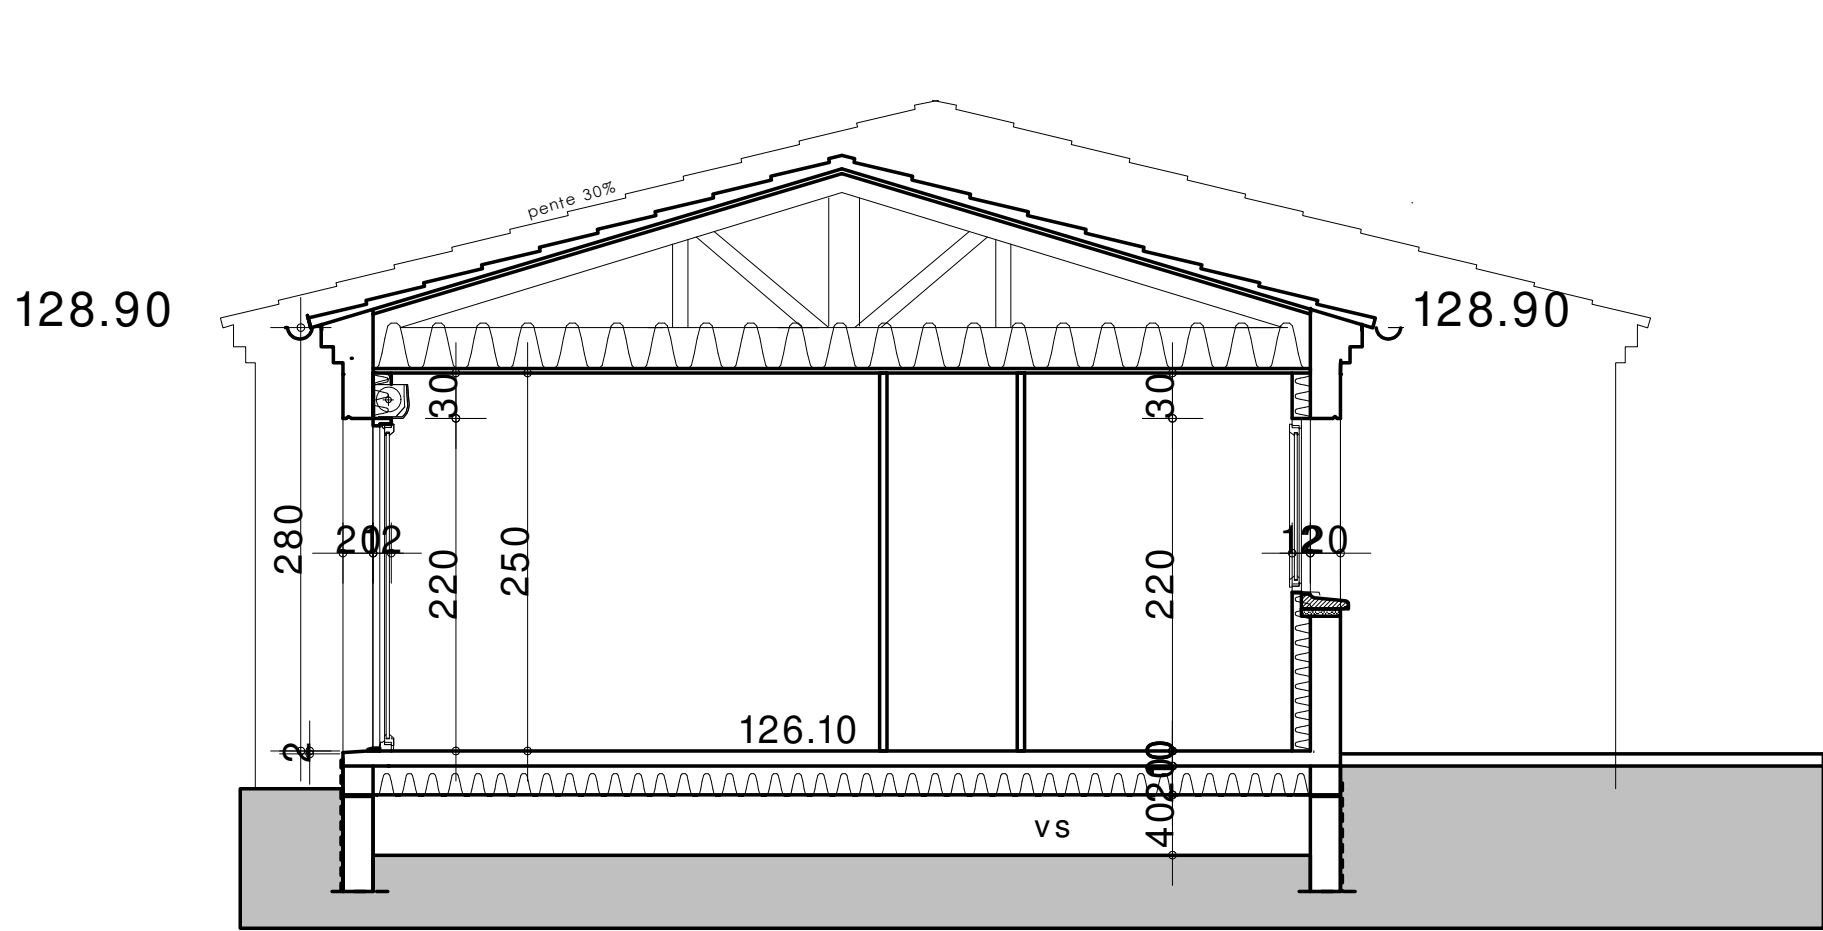


COUPE C-C

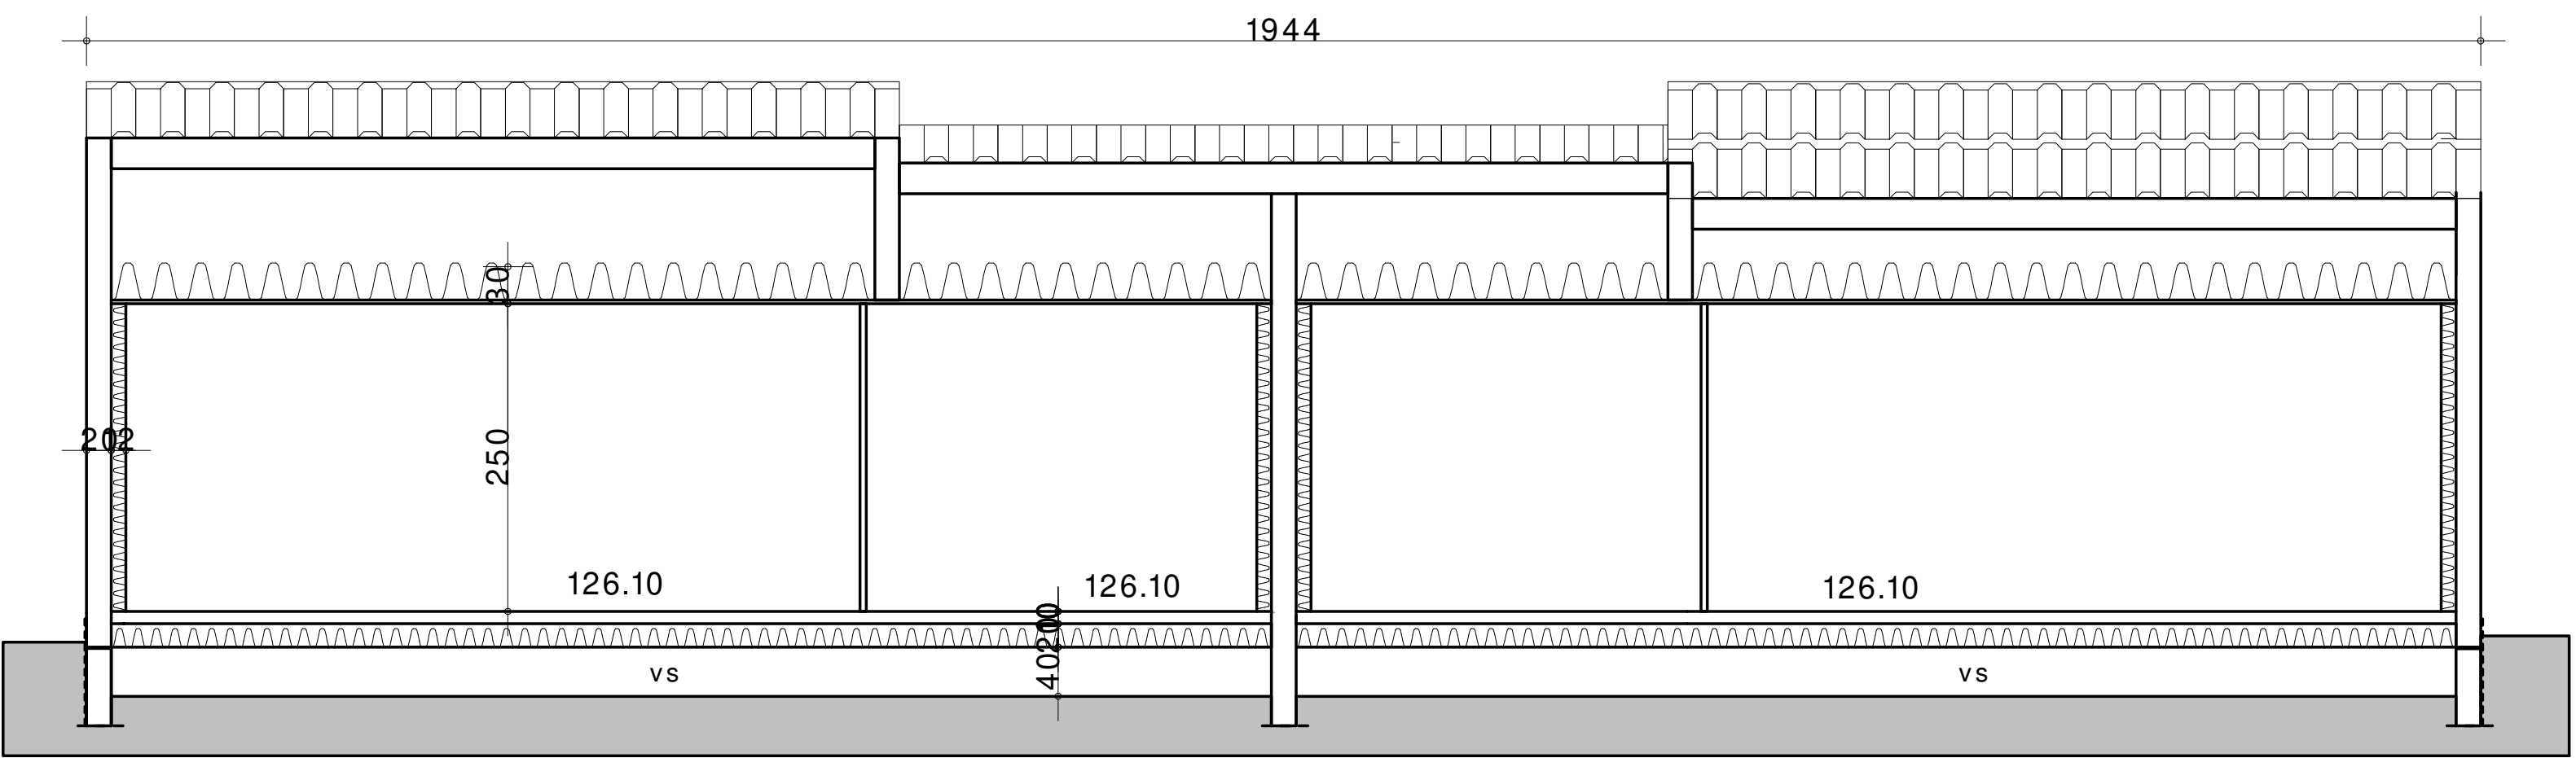


COUPE A-A

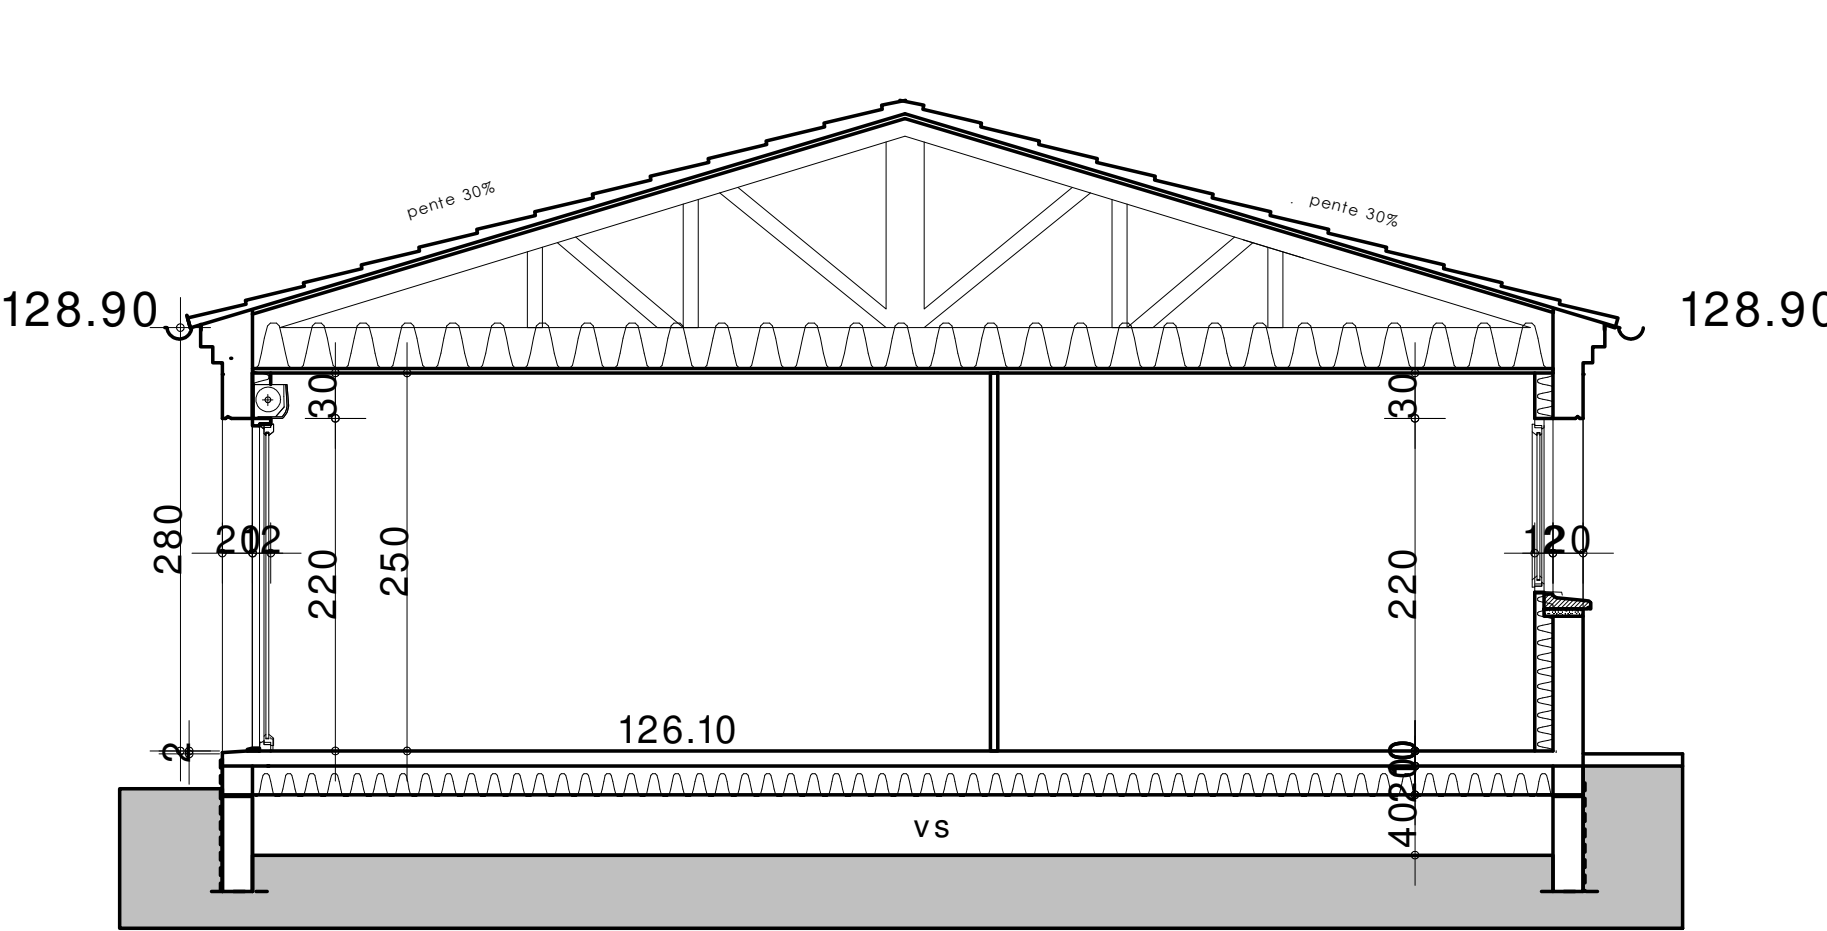

COUPE B-B

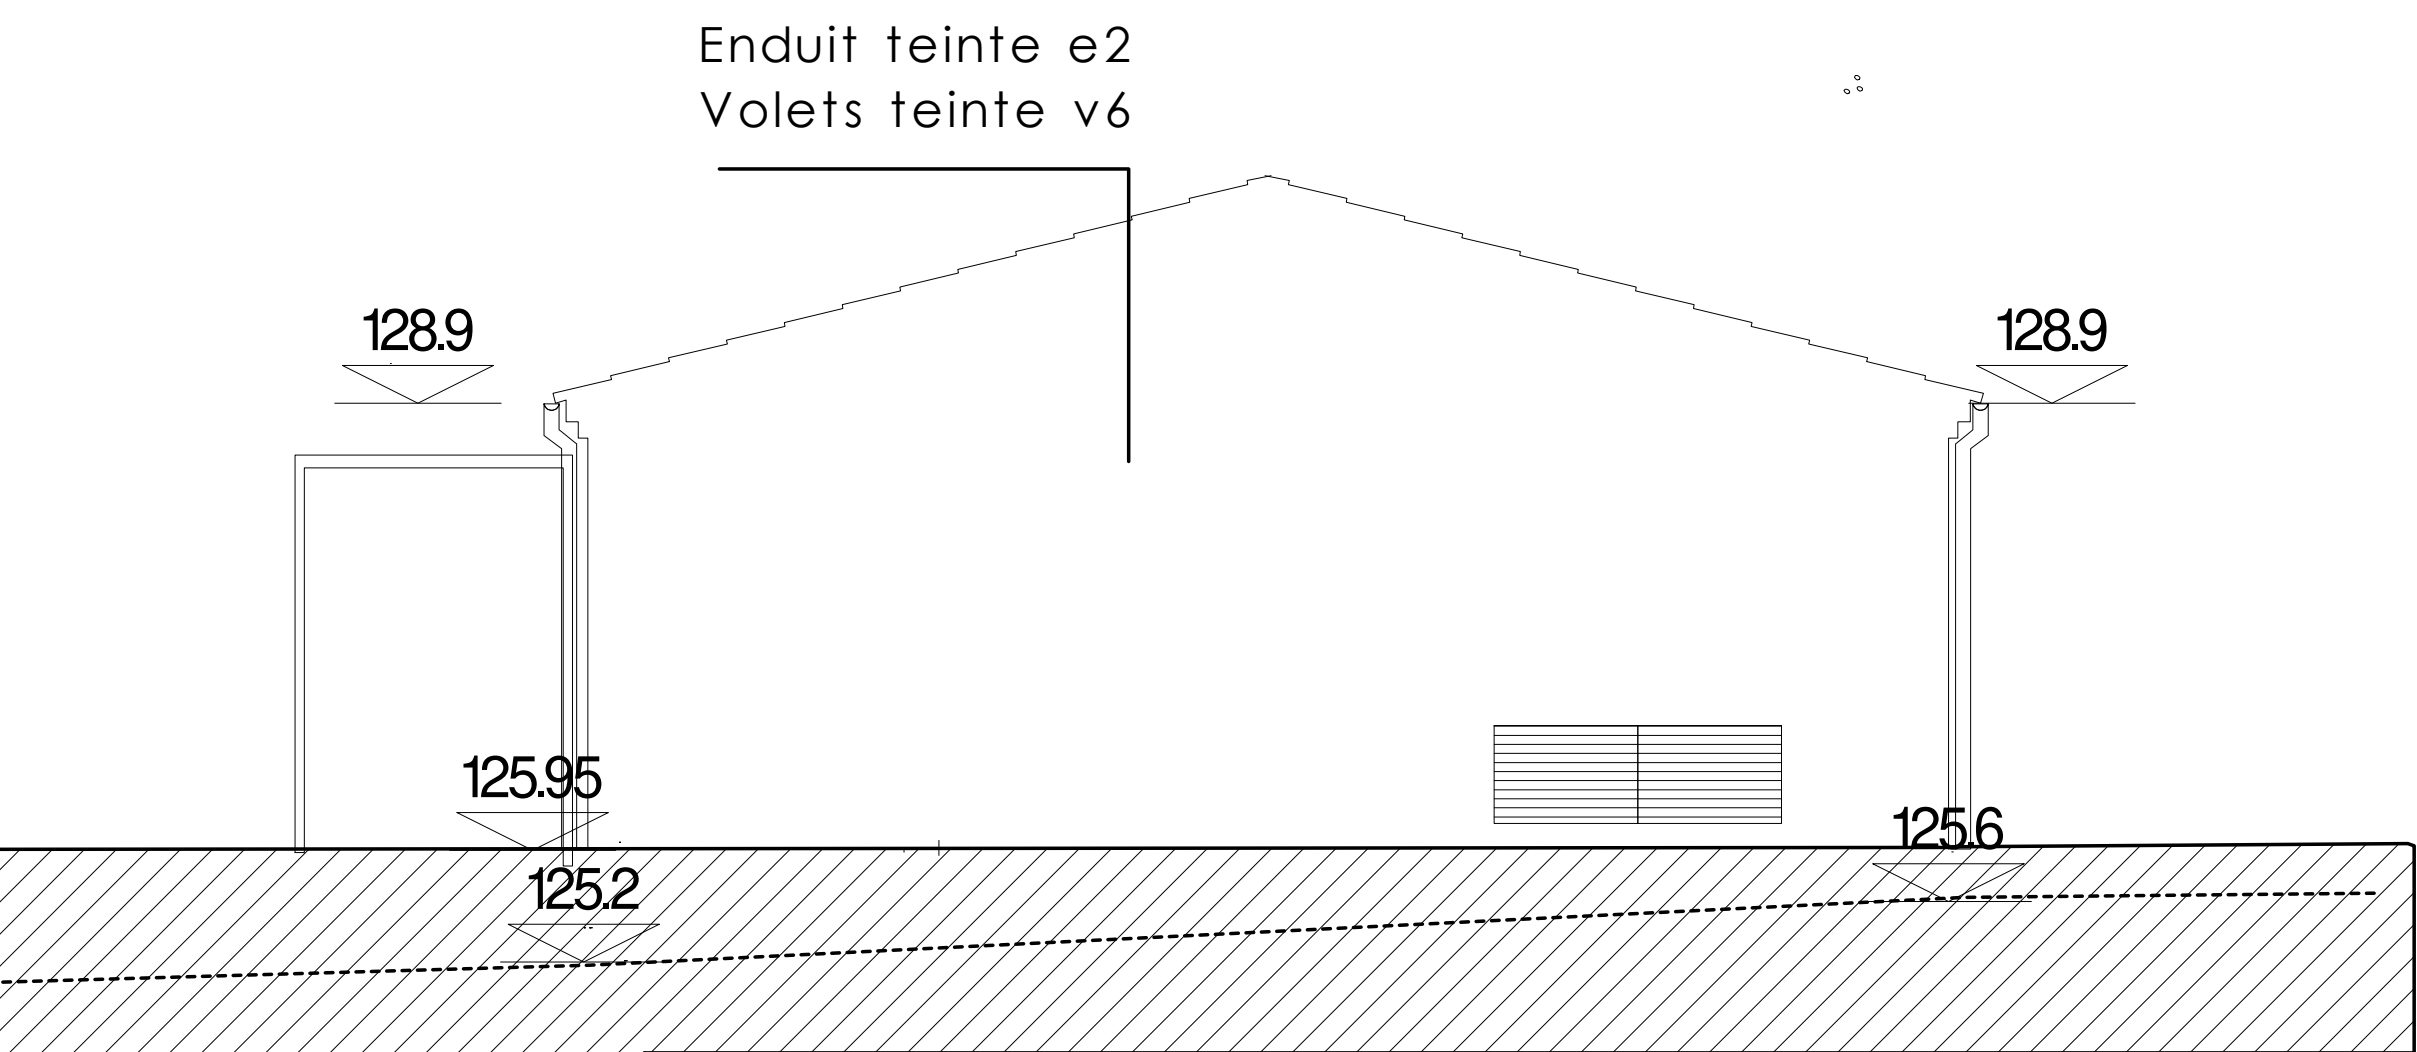


FACADE EST VILLA 17

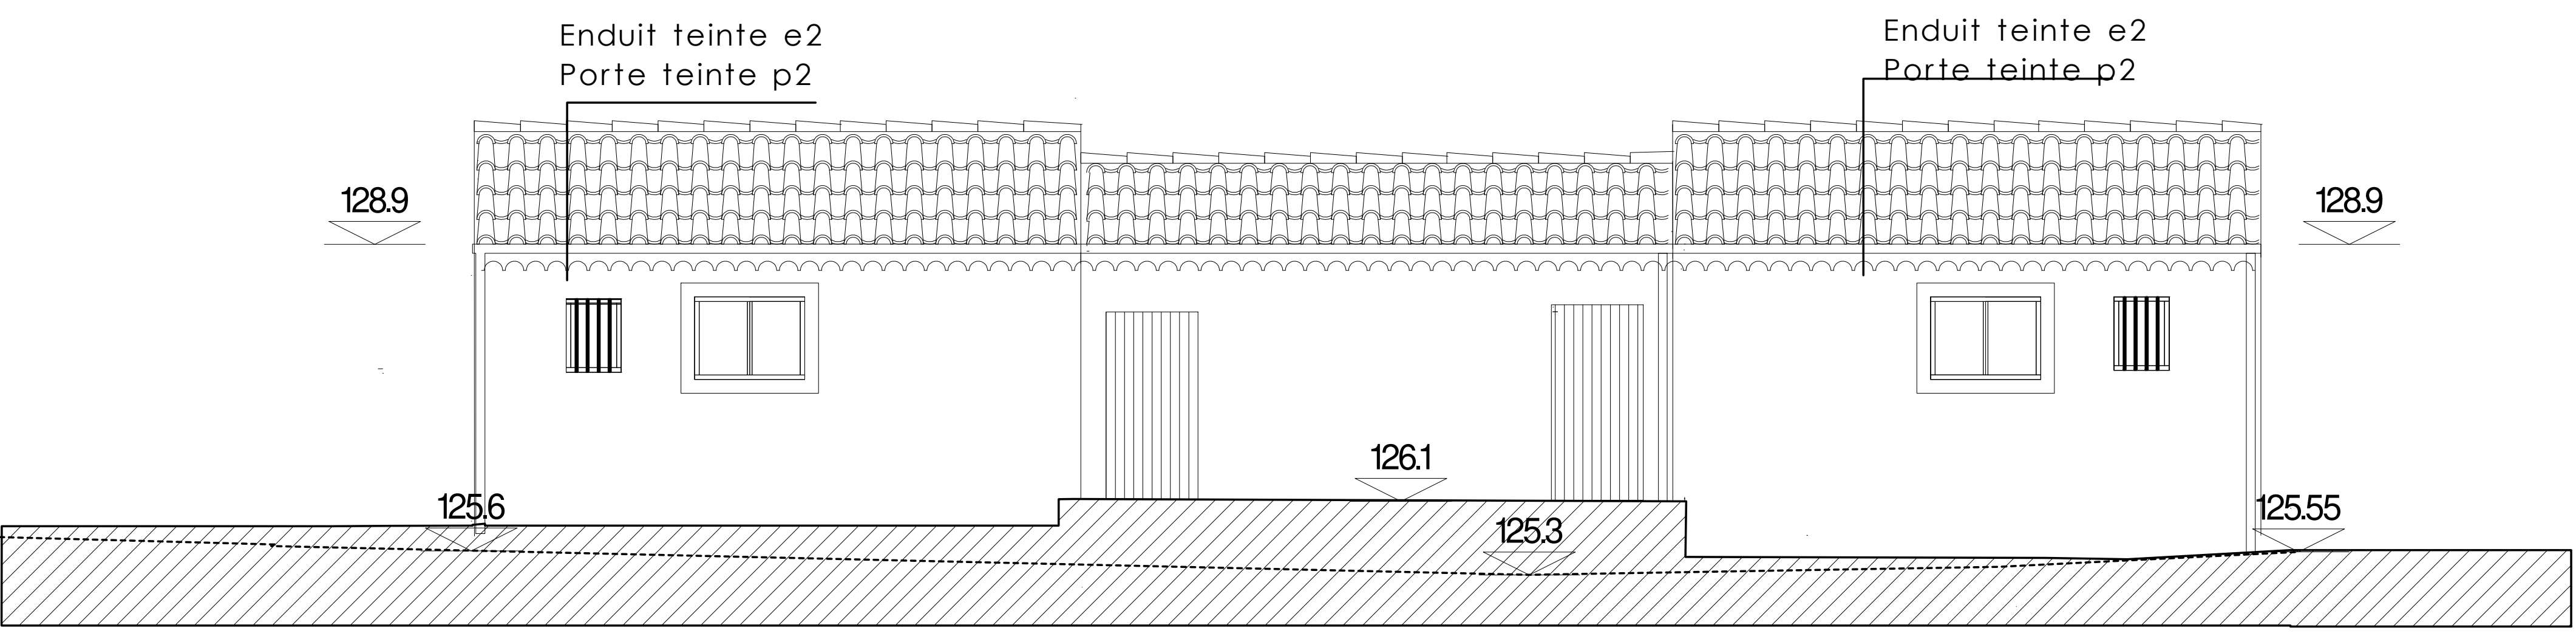


FACADES NORD VILLAS 17 ET 18




- Coffre volet roulant
- Faux plafond
- Espace de manoeuvre 220X120
devant la porte d'entrée
- Espace de manoeuvre 80X130 sanitaire
- Aire de rotation PMR
- GTL cf détail technique
- Isolant acoustique
- Cache de l'unité extérieure de climatisation
- Unités intérieure de climatisation

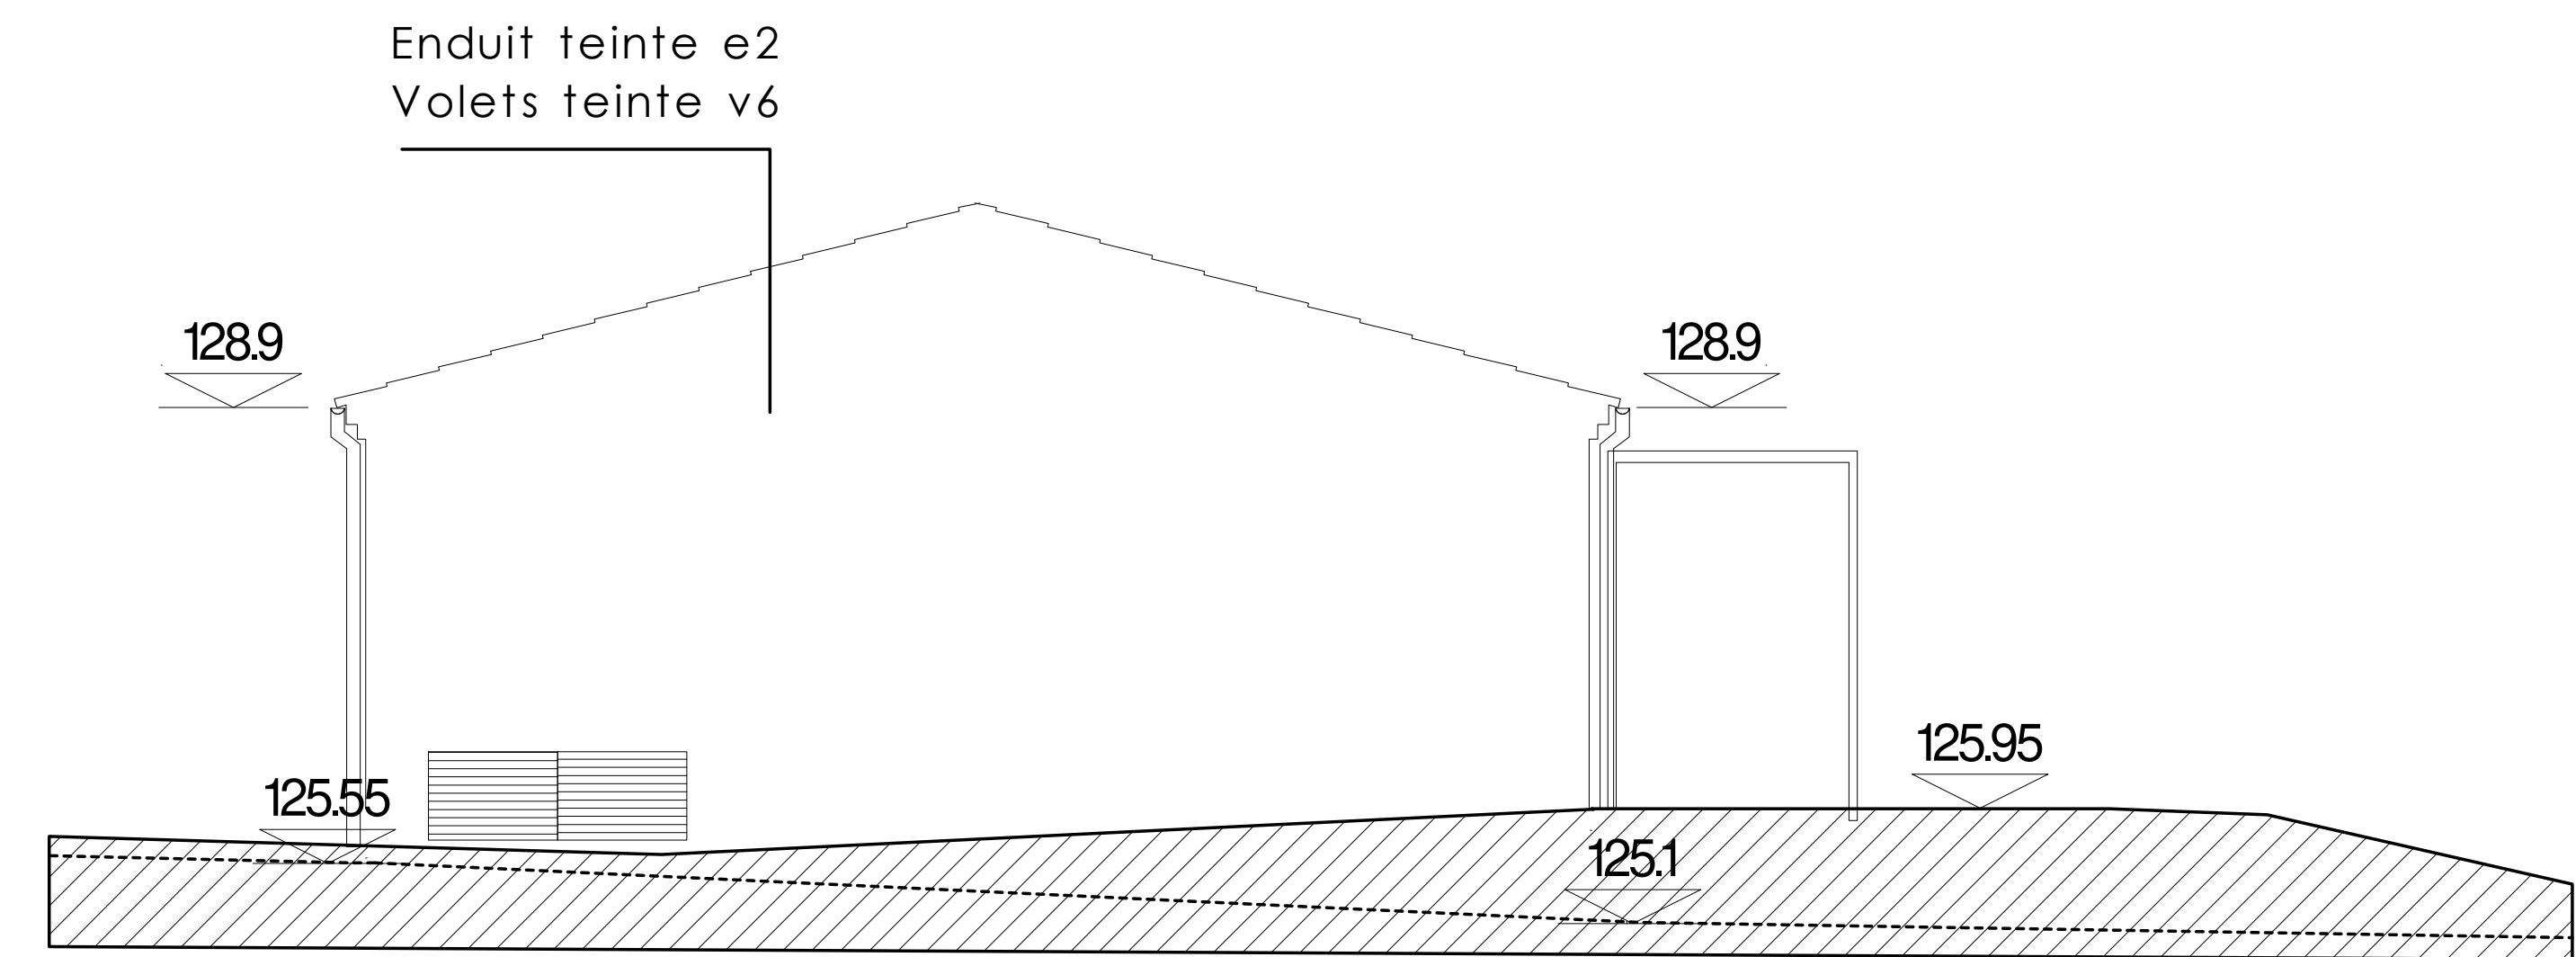

FACADE OUEST VILLA 18

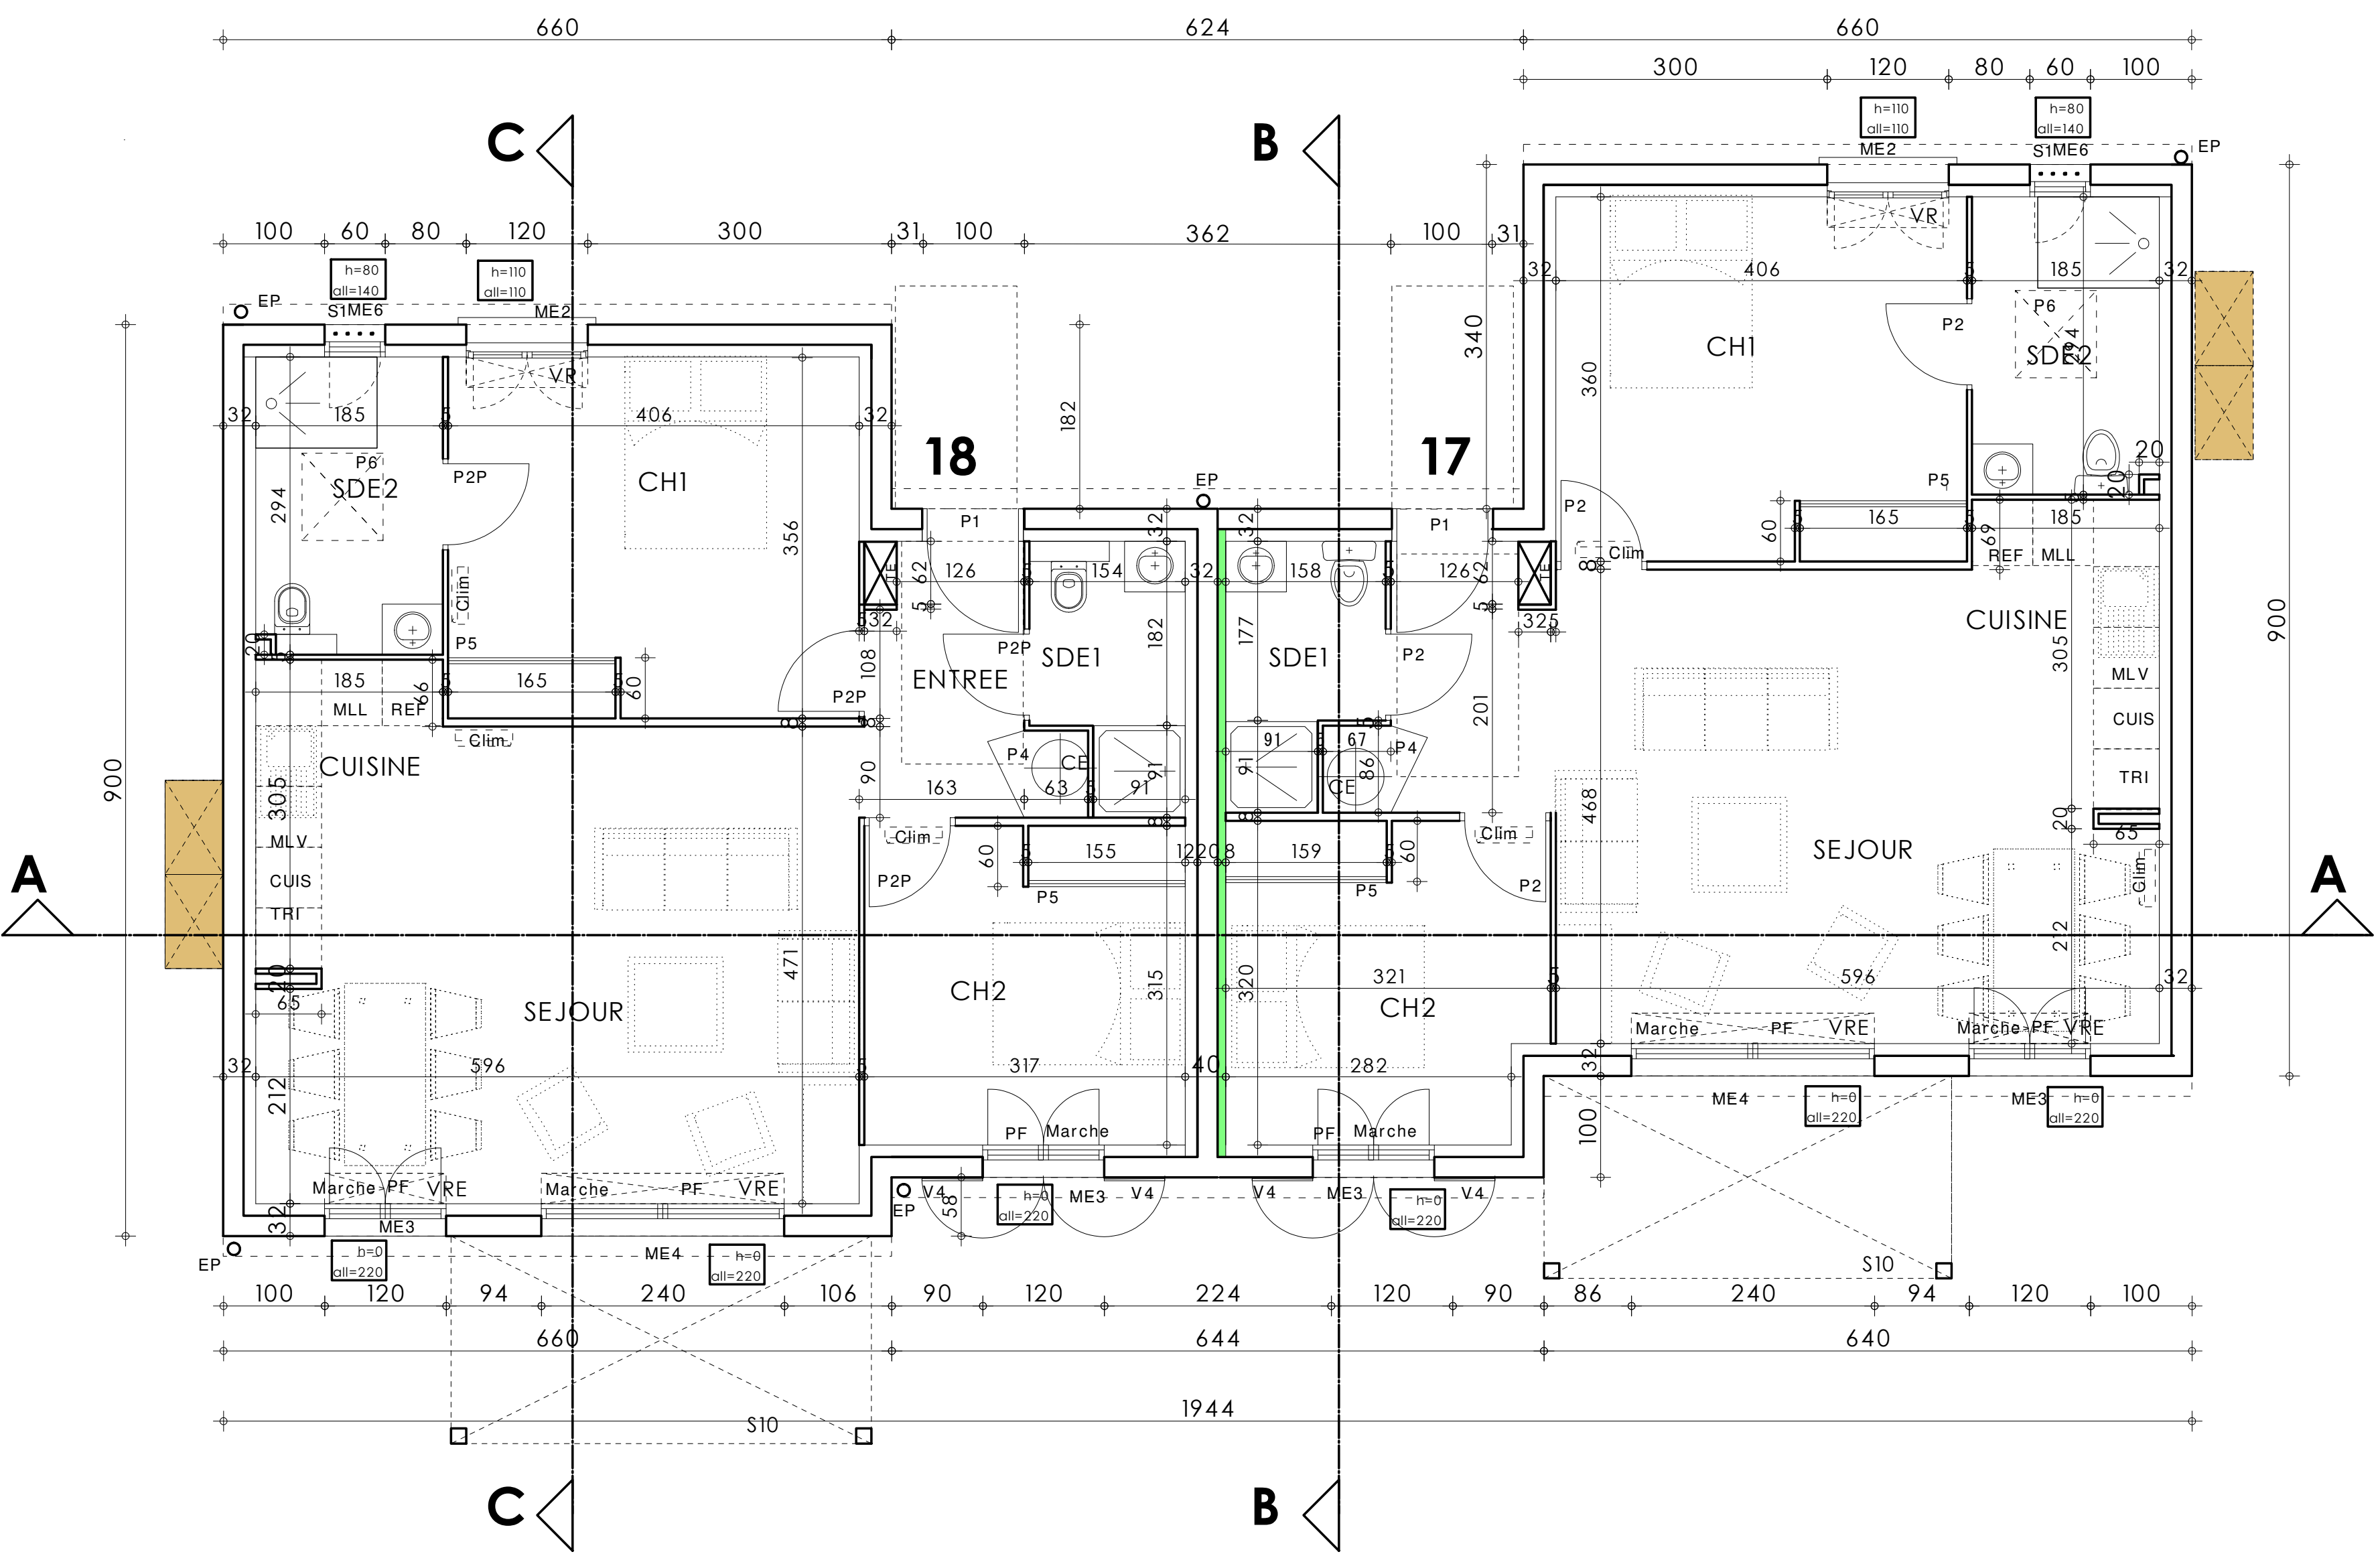

villa 18 villa 17

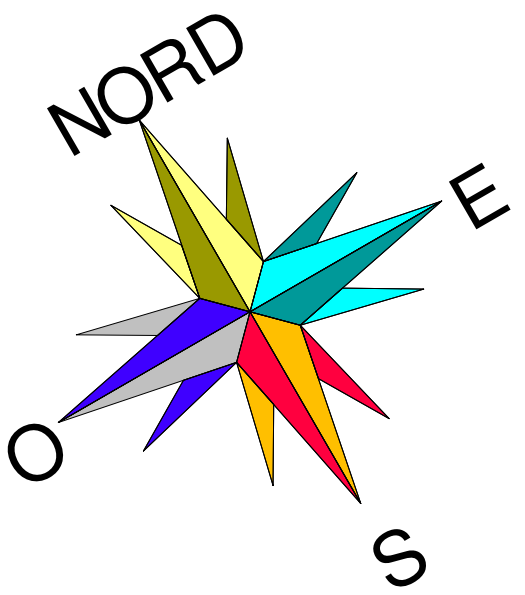

GRANDE TERRE			
INDICE	DATE	MODIFICATIONS	
A	15/04/2026	MODIFICATIONS SUITE REUNION DCE	
B	06/07/2026	MODIFICATION TE ET ISOLANT ACOUSTIQUE	
C			
D			
E			
F			
G			
H			
I			
J			
K			
L			
ARCHITECTES		MAITRE D'OUVRAGE	DATE
M. CHAUVET		SCCV GRANDE TERRE	15/04/2026
A.C. CANAZZA		(SIRET 942 743 799 R.C.S. Toulouse)	
ARCHITECTES D.P.L.G.		PROJET	1/50
Entrepreneurs Individuels		RUE NEUVE GRAND TERRE	PLANS COUPES FACADES
40 Rue FARCES 13008 MARSEILLE		13930 AUREILLE	VILLAS 17 ET 18
m.chauvet@grandterre.fr			NON PMR
bc.venet13@gmail.com			
			106