
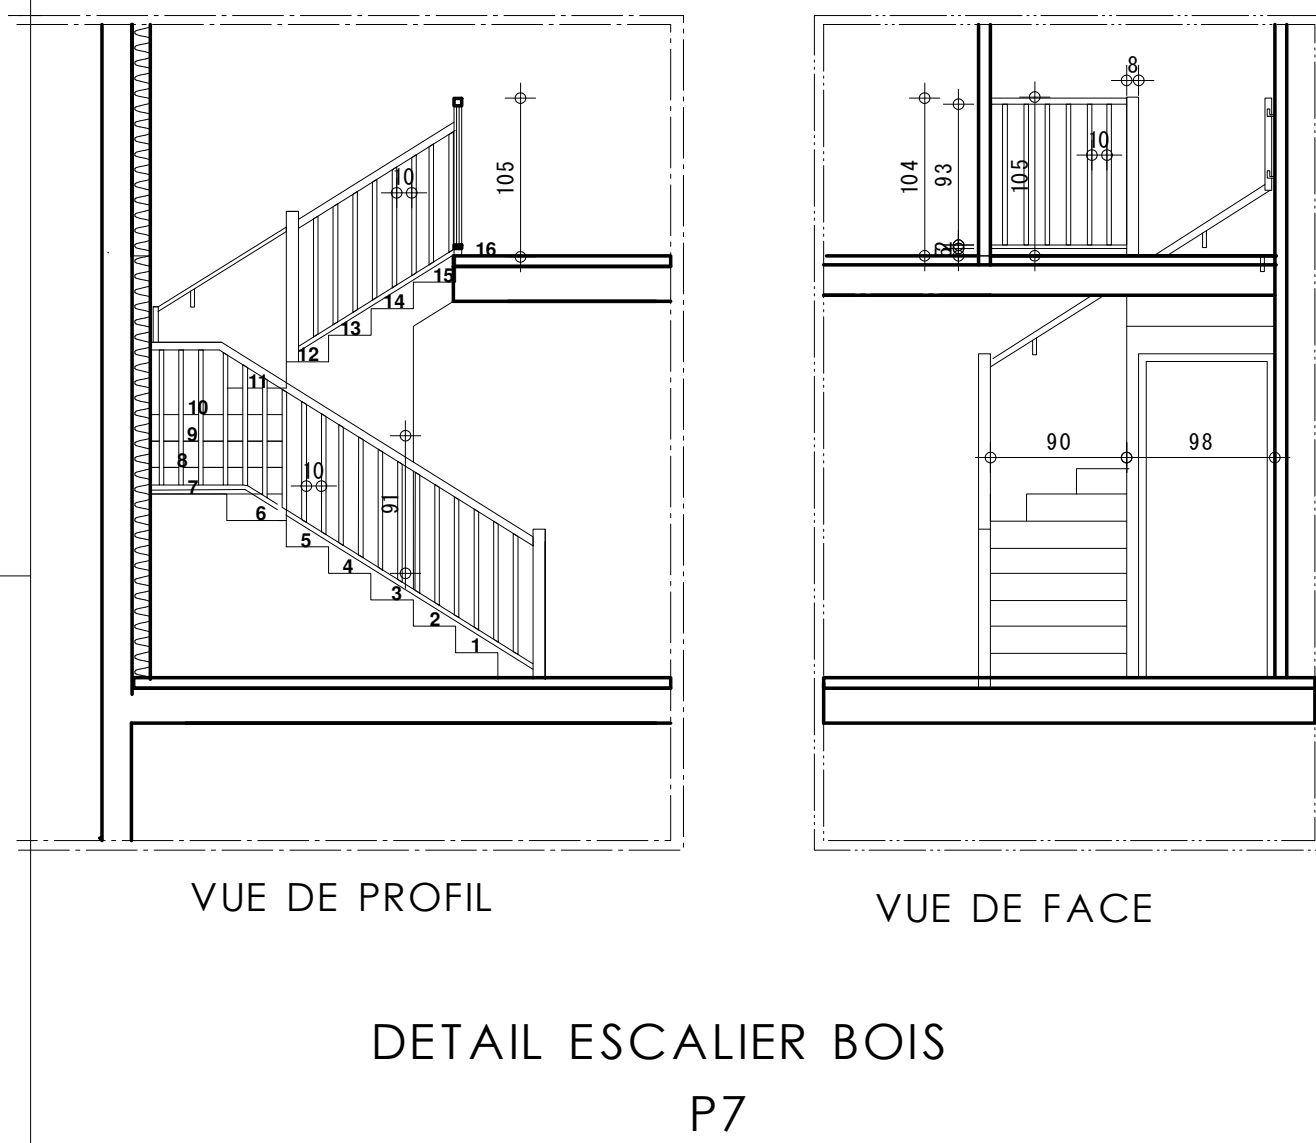
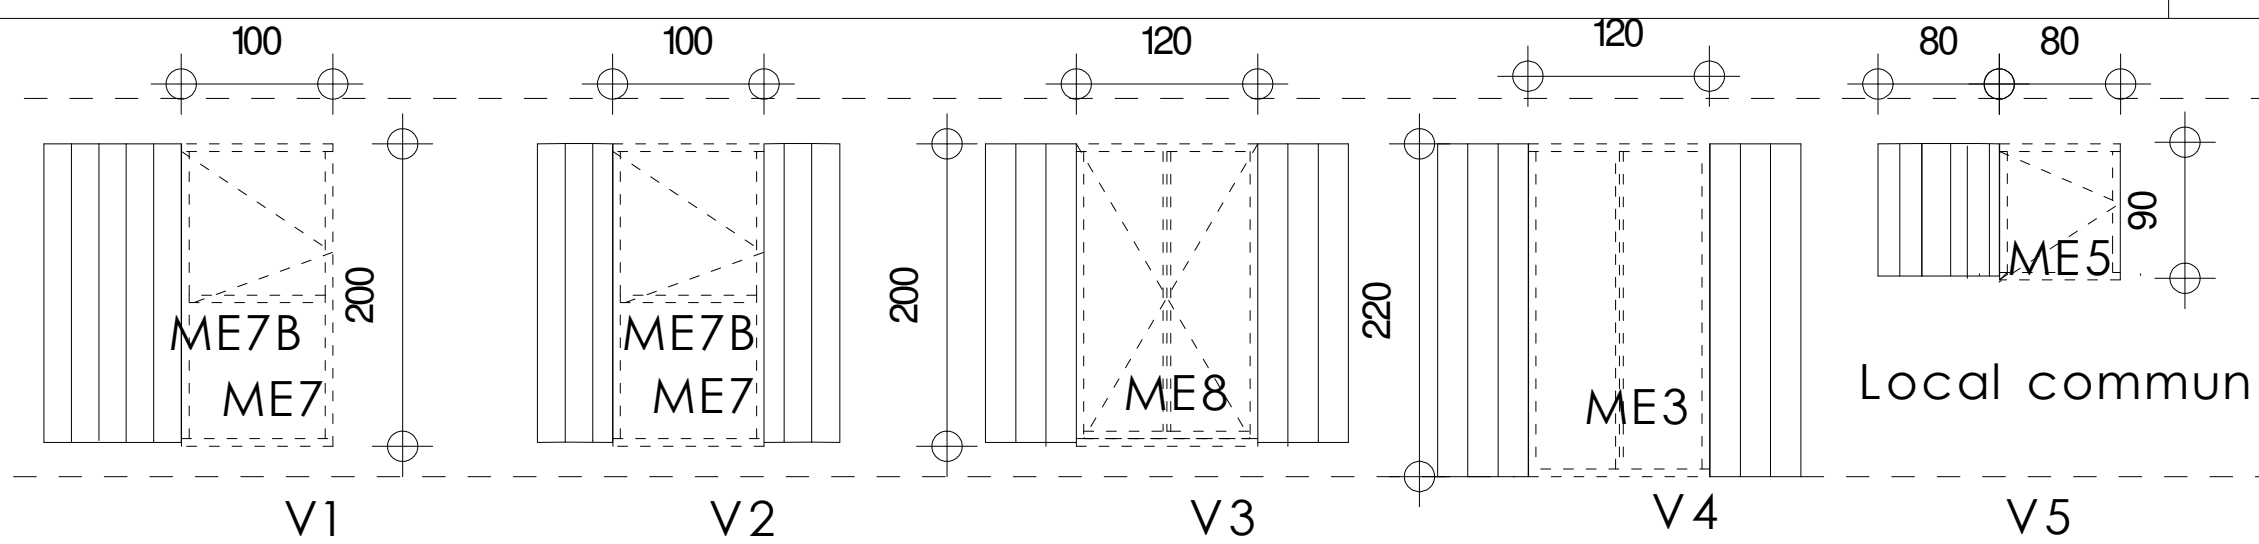
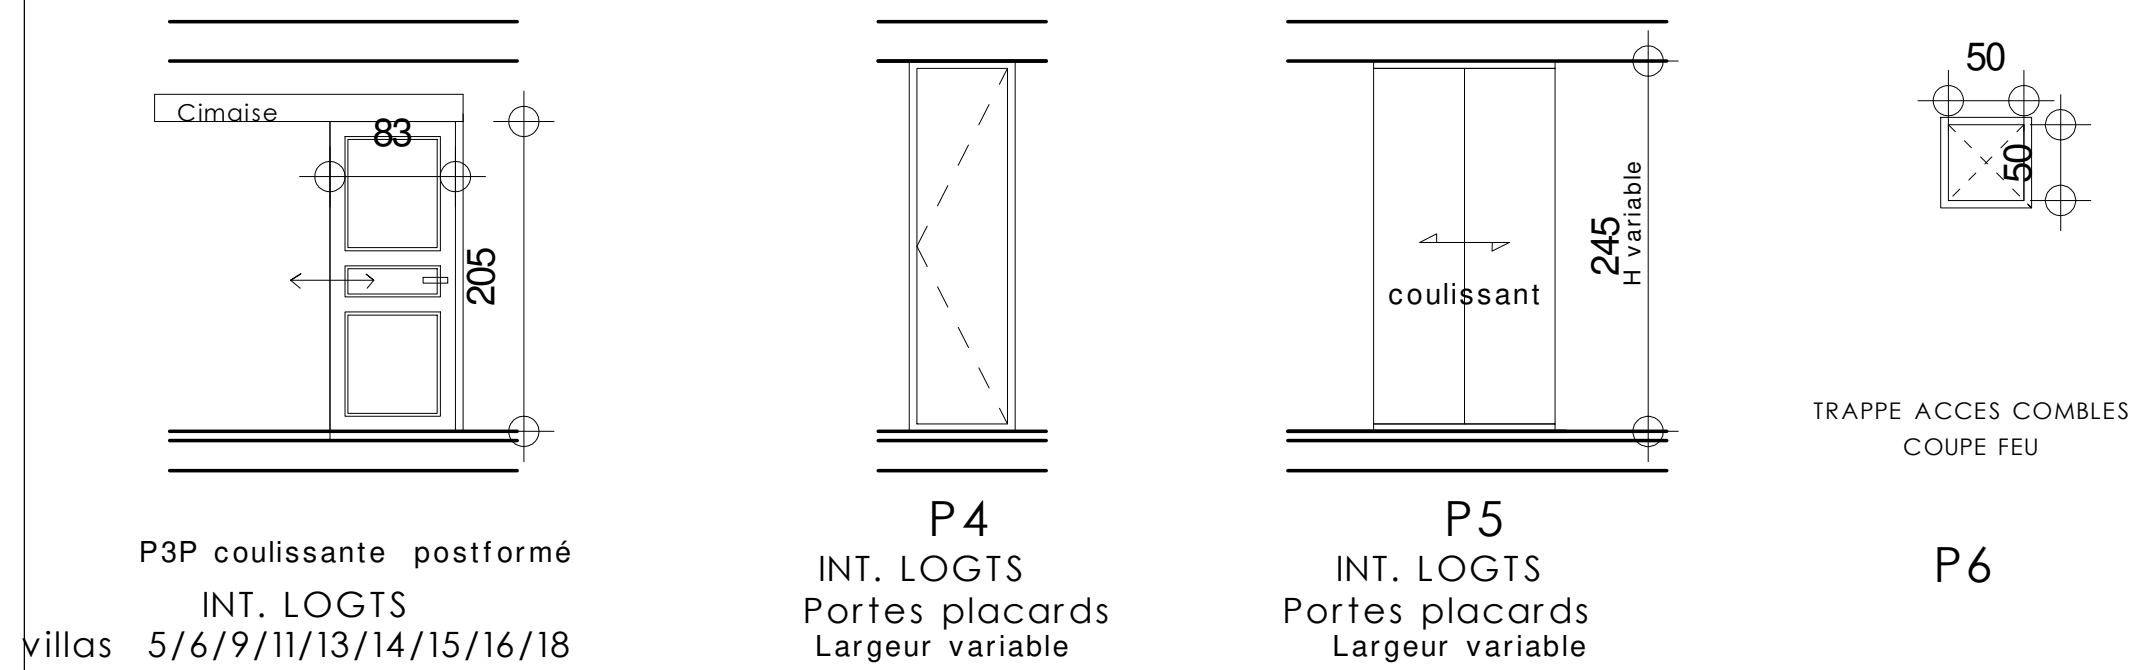


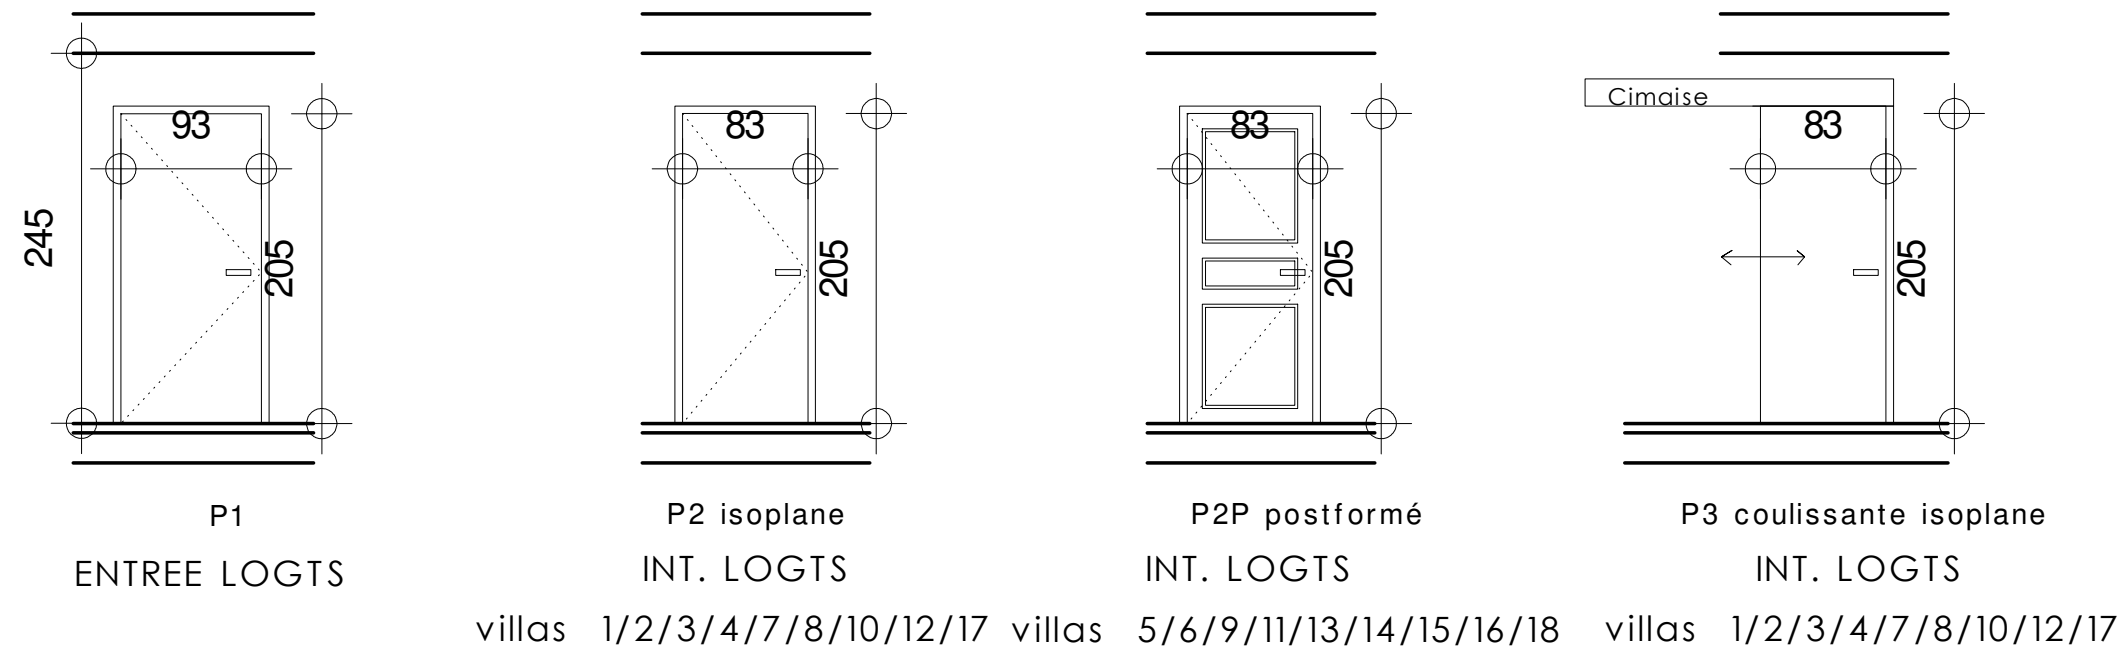

| INDICE | DATE       | MODIFICATIONS                 |
|--------|------------|-------------------------------|
| A      | 15/06/2026 | mise à jour suite reunion dce |
| B      |            |                               |
| C      |            |                               |
| D      |            |                               |
| E      |            |                               |
| F      |            |                               |
| G      |            |                               |
| H      |            |                               |
| I      |            |                               |
| J      |            |                               |
| K      |            |                               |
| L      |            |                               |

|   |   |                                         |            |                                      |         |
|---|---|-----------------------------------------|------------|--------------------------------------|---------|
| <div>ARCHITECTES</div> <div>M. CHAUVET<br/>A.C. CARNAZZA<br/>ARCHITECTES D.P.I.G.</div> <div>Entrepreneurs individuels</div> <div>40 Rue FARGES 13008 MARSEILLE</div> <div>ml.chauvet@wanadoo.fr<br/>ac.vernell1@gmail.com</div> | <div>MAITRE D'OUVRAGE</div> <div>SCCV GRANDE TERRE</div> <div>(SIRET 942 743 709 R.C.S. Toulon)</div> | DATE                                    | 15/04/2026 | A.P.S.                               |         |
|   |   | EGHELLE                                 | 1/50       | P.C.                                 |         |
|   |   | OPERATION                               |            | TITRE DU PLAN                        | MARCHES |
|   |   | RUE NEUVE GRAND TERRE<br>13930 AUREILLE |            | MENUISERIES<br>INTERIEURES<br>VOLETS | 300     |