


9 dimensions de menuiseries

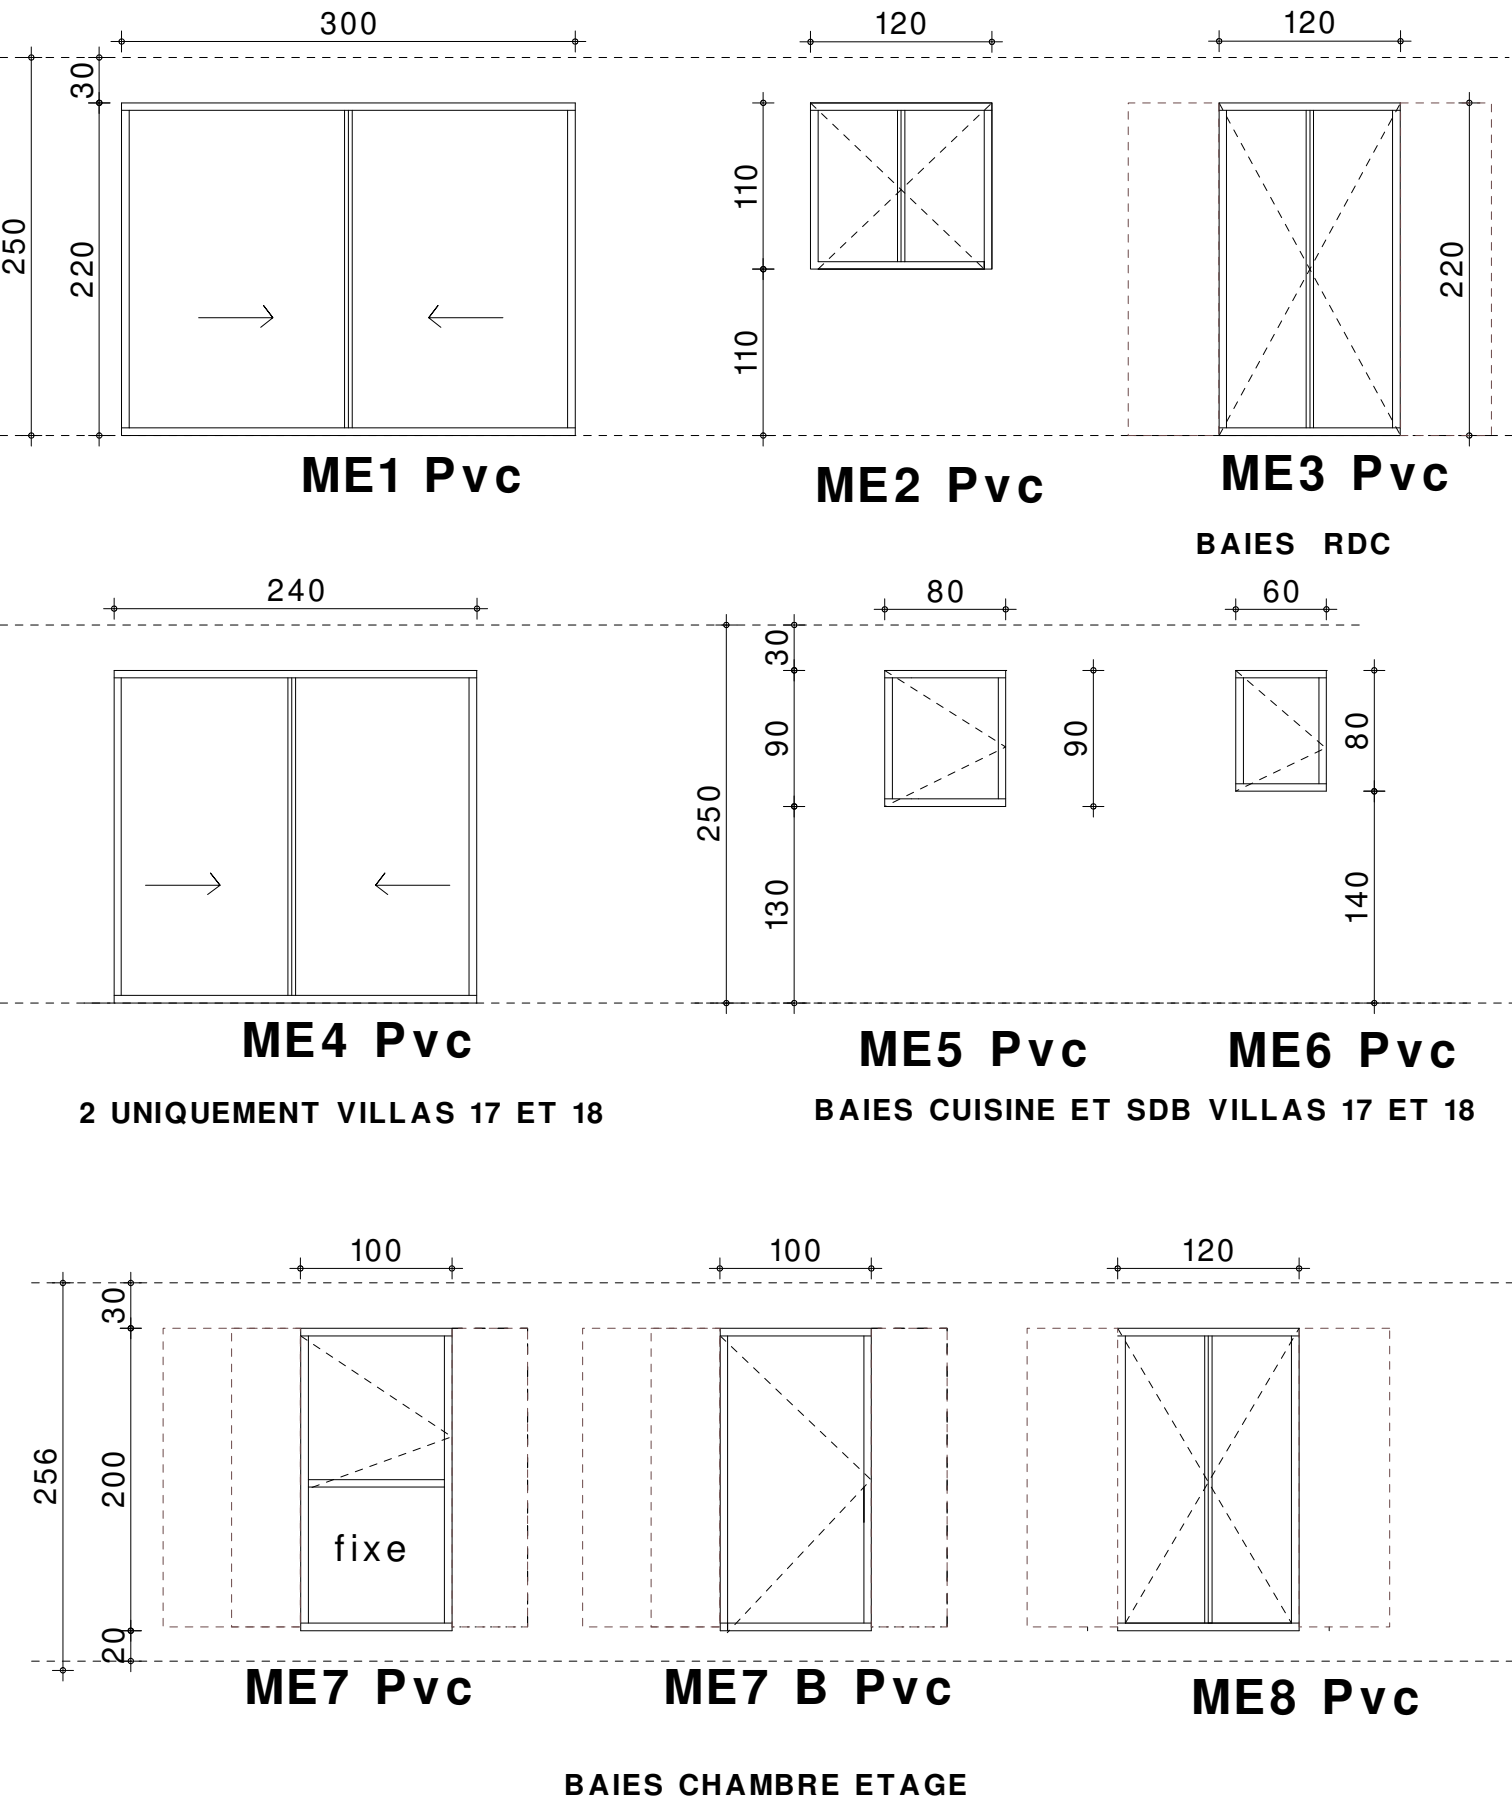

INDICE	DATE	MODIFICATIONS
A	15/06/2026	mise à jour suite reunion dce
B		
C		
D		
E		
F		
G		
H		
I		
J		
K		
L		

ARCHITECTES M.CHAUVET A.C. CARNAZZA ARCHITECTES D.P.L.G. Entrepreneurs Individuels 40 Rue FARGES 13008 MARSEILLE mi.chauvet@wanadoo.fr ac.vernet13@gmail.com	MAITRE D'OUVRAGE		DATE	15/04/2026	A.P.S.
	SCCV GRANDE TERRE (SIRET 942 743 709 R.C.S. Toulon)		ECHELLE	1/50	P.C.
	OPERATION		TITRE DU PLAN	MENUISERIES EXTERIEURES	D.C.E.
	RUE NEUVE GRAND TERRE 13930 AUREILLE				MARCHES
					301