

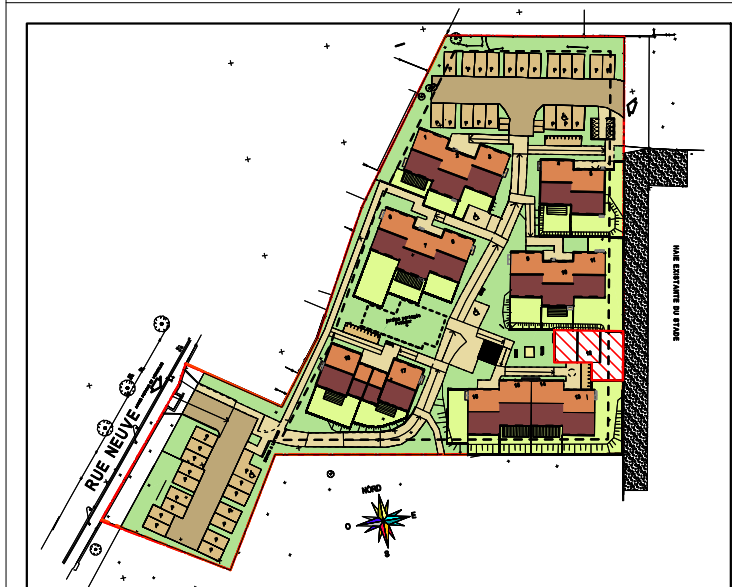
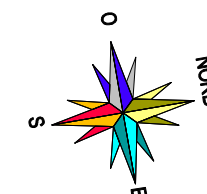


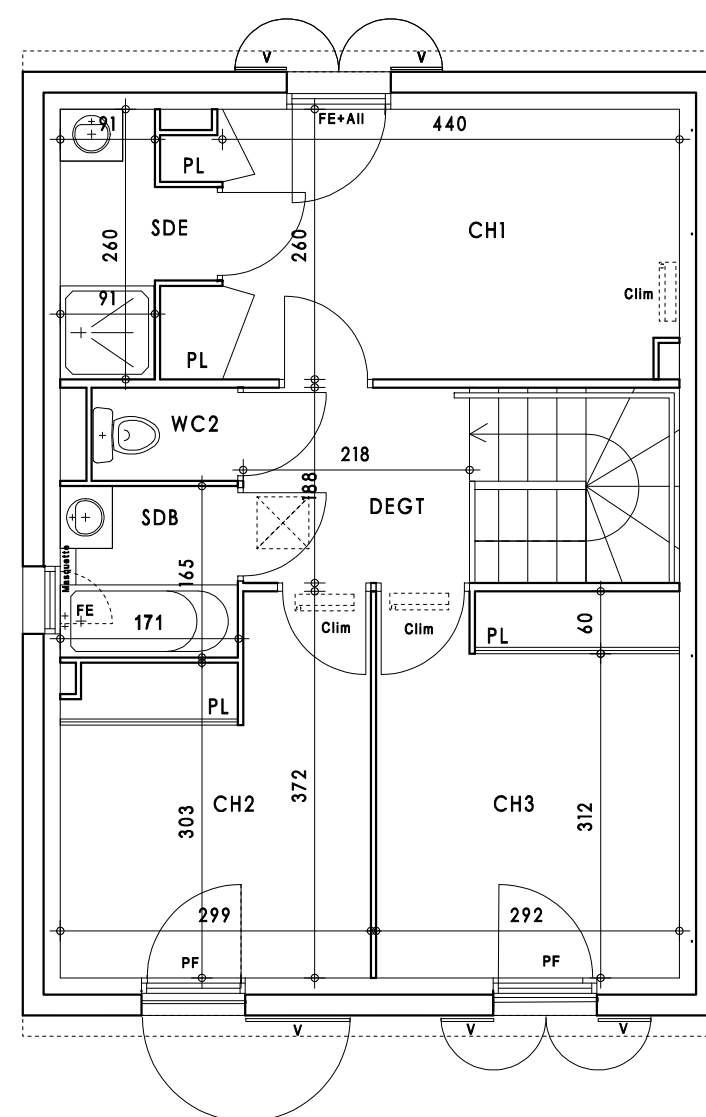

Villa N°	12
type	T4
Surface habitable	89.37 m²
Jardin	56.22 m²


séjour-entrée +pl	32.21 m²
cuisine	6.82 m²
chambre 1+pl	12.30 m²
chambre 2+pl	9.91 m²
chambre 3+pl	10.83 m²
cellier	4.95 m²
salle de bain	2.82 m²
salle d'eau	2.91 m²
wc 1	1.25 m²
wc 2	1.27 m²
dégagement	4.10 m²

12

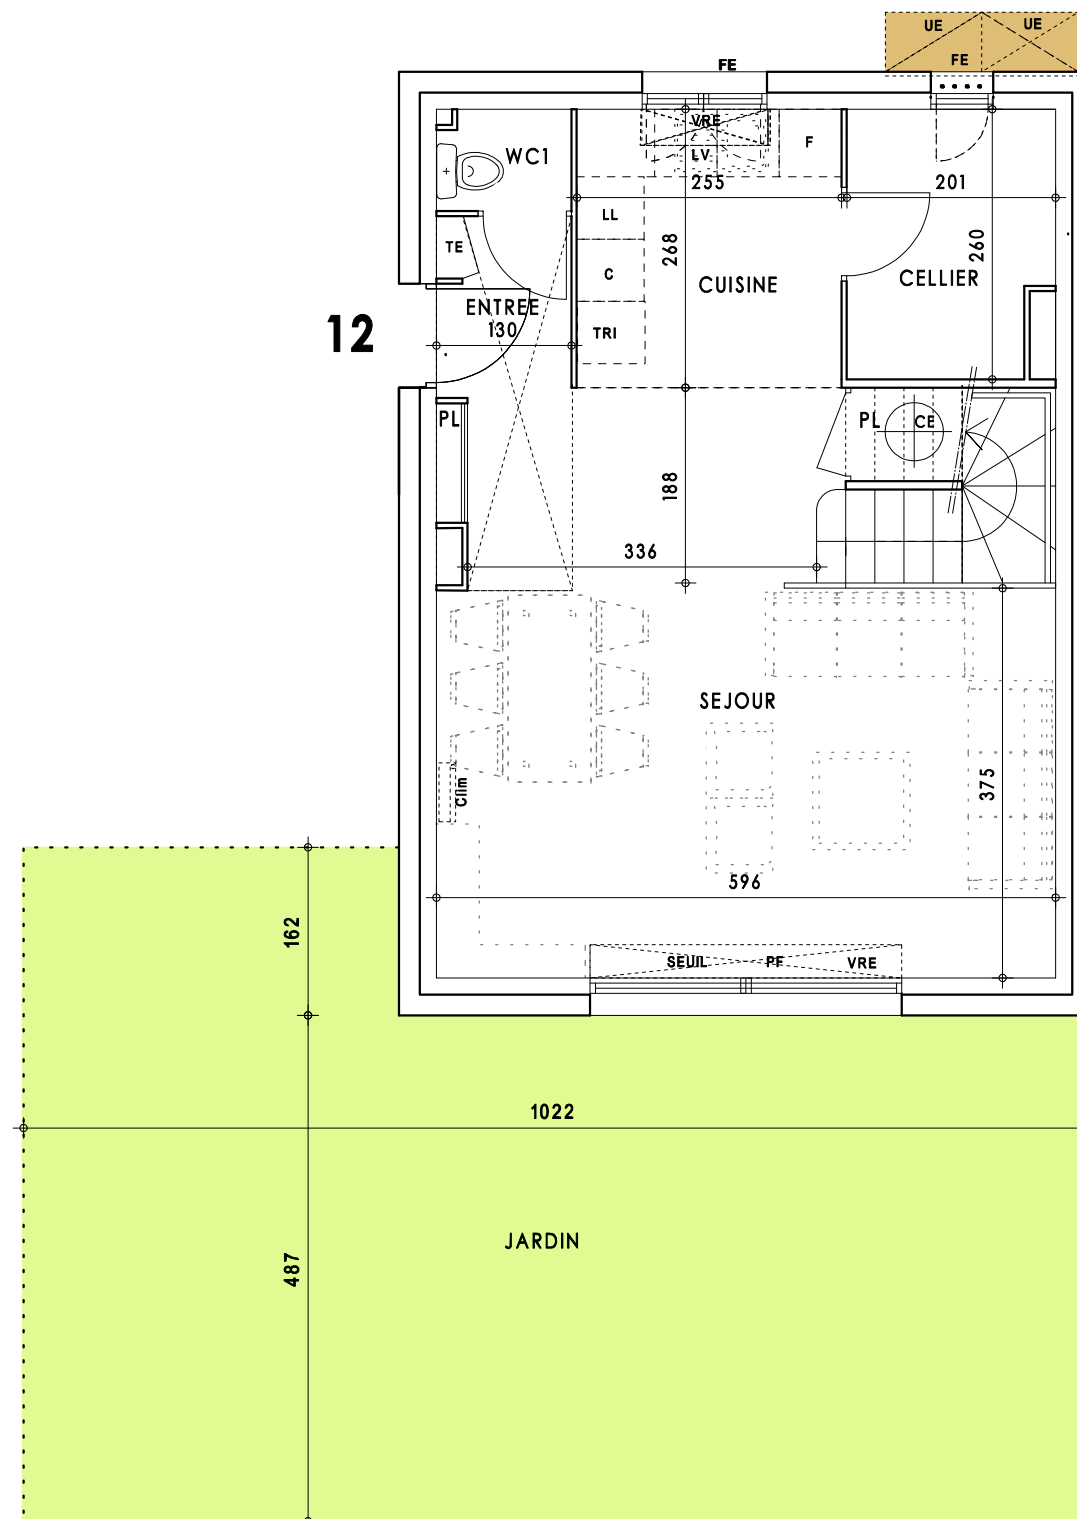

0 M 5 M

Observations:
Ce plan pourra subir des modifications de détails ou de cotations résultant des impératifs de construction.
Les surfaces, retombées, soffites et canalisations sont données à titre indicatif.

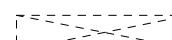 Soffite / Faux-Plafond  Clôture grillagée h = 1,40 m maille 15x15

Légende :	FE	fenêtre	SDE	salle d'eau	
CE	cumulus électrique	V	volet	DEGT	dégagement
UE	unité extérieure climatisation	LL	lave linge	PL	placard
TE	tableau électrique	LV	lave vaisselle		cloison sur carrelage
PF	porte fenêtre	C	cuisson		unité intérieure de climatisation
VR	volet roulant	F	réfrigérateur	clim	
VRE	volet roulant électrique	CH	chambre		
FE+All	fenêtre avec allège vitrée	SDB	salle de bain		

DATE : 18/06/2026
INDICE 2

SCCV GRANDE TERRE 837bis Allée de PARIS
83500 LA SEYNE SUR MER