




**Légende : Électricité CFO**

DCL

DCL

Type : DCL plafond / DCL étanche plafond

DCL

DCL

Type : DCL applique / DCL étanche applique

Type : Applique extérieure

Commande volet roulant

Télérupteur

Interrupteur va et vient

Interrupteur simple allumage

Interrupteur simple allumage à voyant

Interrupteur va et vient à voyant

Interrupteur double allumage

Simple prise de courant 2P+T 10/16A

Simple prise de courant 2P+T 10/16A étanche

Prise de Courant sur circuit dédié

E.T.E.L.

Espace Technique Electrique du Logement

SG

Tableau Electrique Services Généraux (Communs)

Fourreau ELEC

Alimentation électrique

**Légende : Électricité CFA**

Prise RJ45

Détecteur de fumée

Sonnette

Carillon

CONSTRUCTION DE 18 LOGEMENTS  
RUE NEUVE GRAND TERRE  
13930 AUREILLE

VILLAS 1 - 2 - 3

MAITRISE D'OUVRAGE

SCCV GRANDE TERRE  
837 BIS ALLEE DE PARIS  
LA SEYNE SUR MER

MAITRISE D'OEUVRE

AXXION  
41 Rue Ribas  
13770 VENELLES

BET FLUIDES CVC

AXIO INGENIERIE  
393 Rue Etторе BUGATTI  
66000 PERPIGNAN  
axio.ingenierie@gmail.com



LOT ELECTRICITE  
PLAN DES COMBLES

| Ind | Date       | Modifications        | Dessiné par: | Vérifié par: |
|-----|------------|----------------------|--------------|--------------|
| 0   | 06/07/2026 | Création du document | EB           | LG           |
| A   |            |                      | Date:        | Echelle:     |
| B   |            |                      | 06/07/2026   | 1:25         |
| C   |            |                      | Visa:        |              |
| D   |            |                      |              |              |

| NIVEAU | LOT  | DOSSIER | PHASE | N° DOCUMENT | INDICE |
|--------|------|---------|-------|-------------|--------|
| TOIT   | ELEC |         | DCE   | 721         | 0      |