


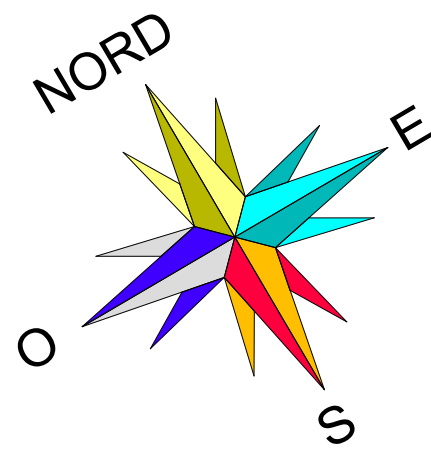


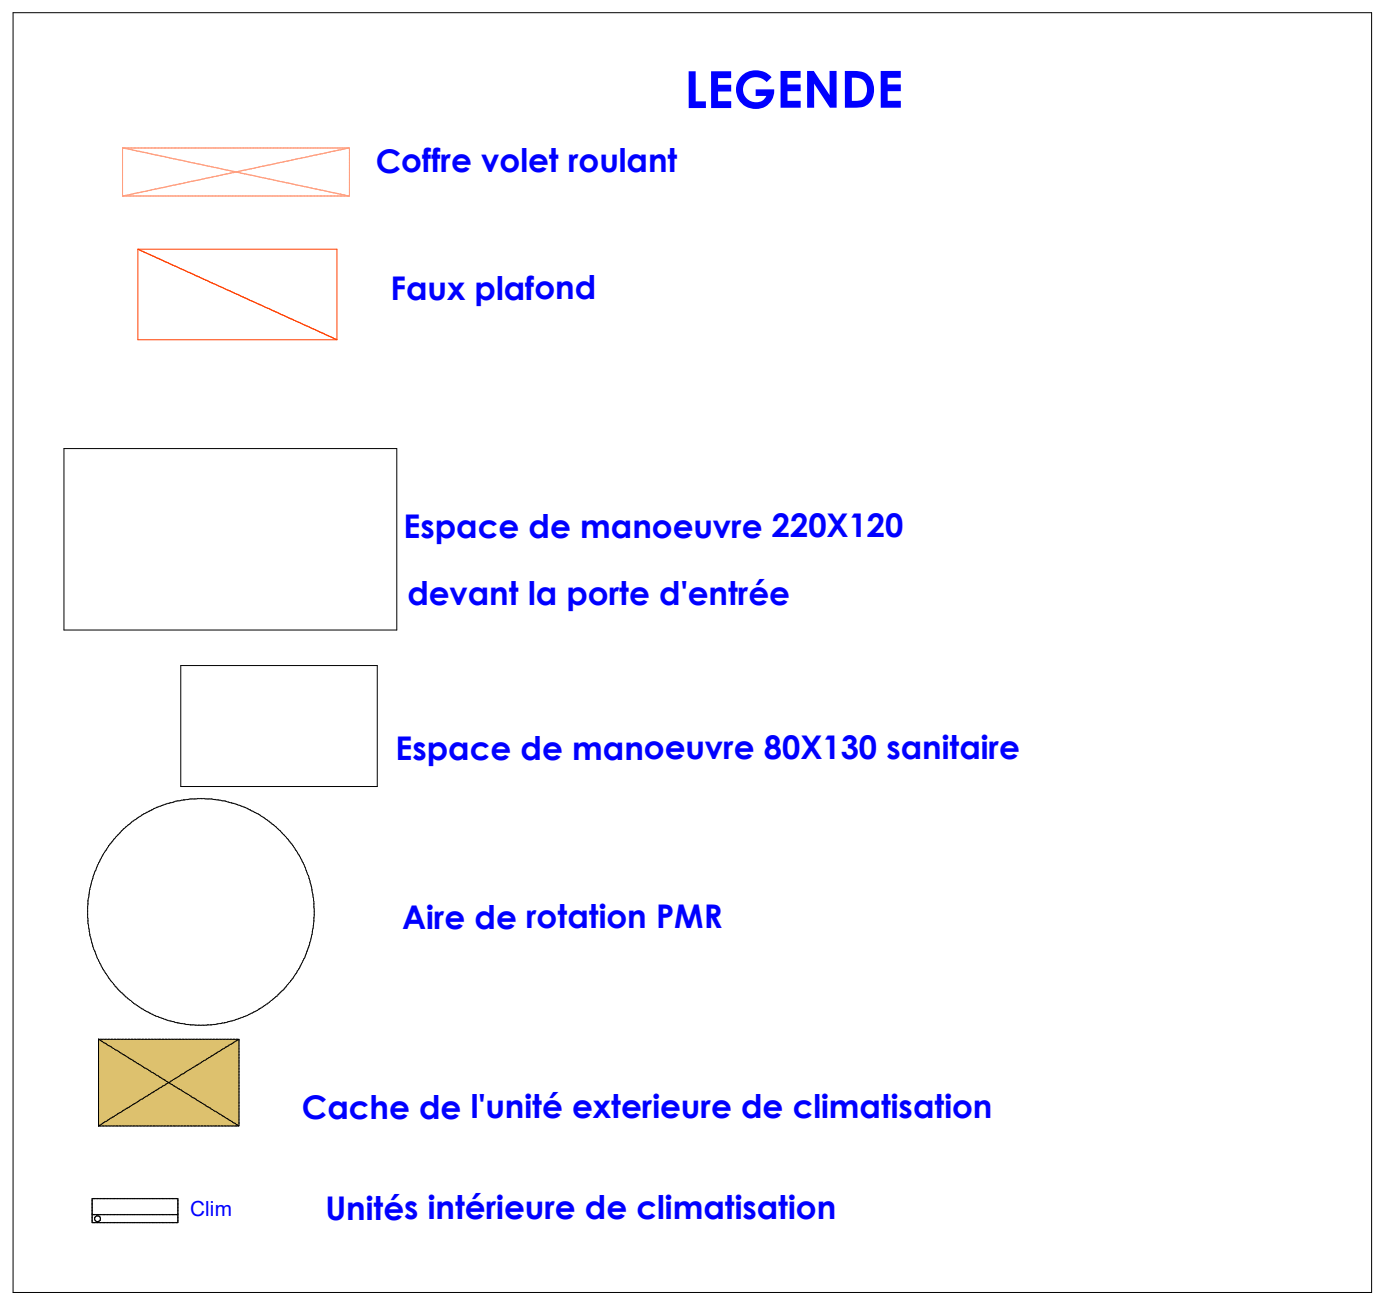

villa 12

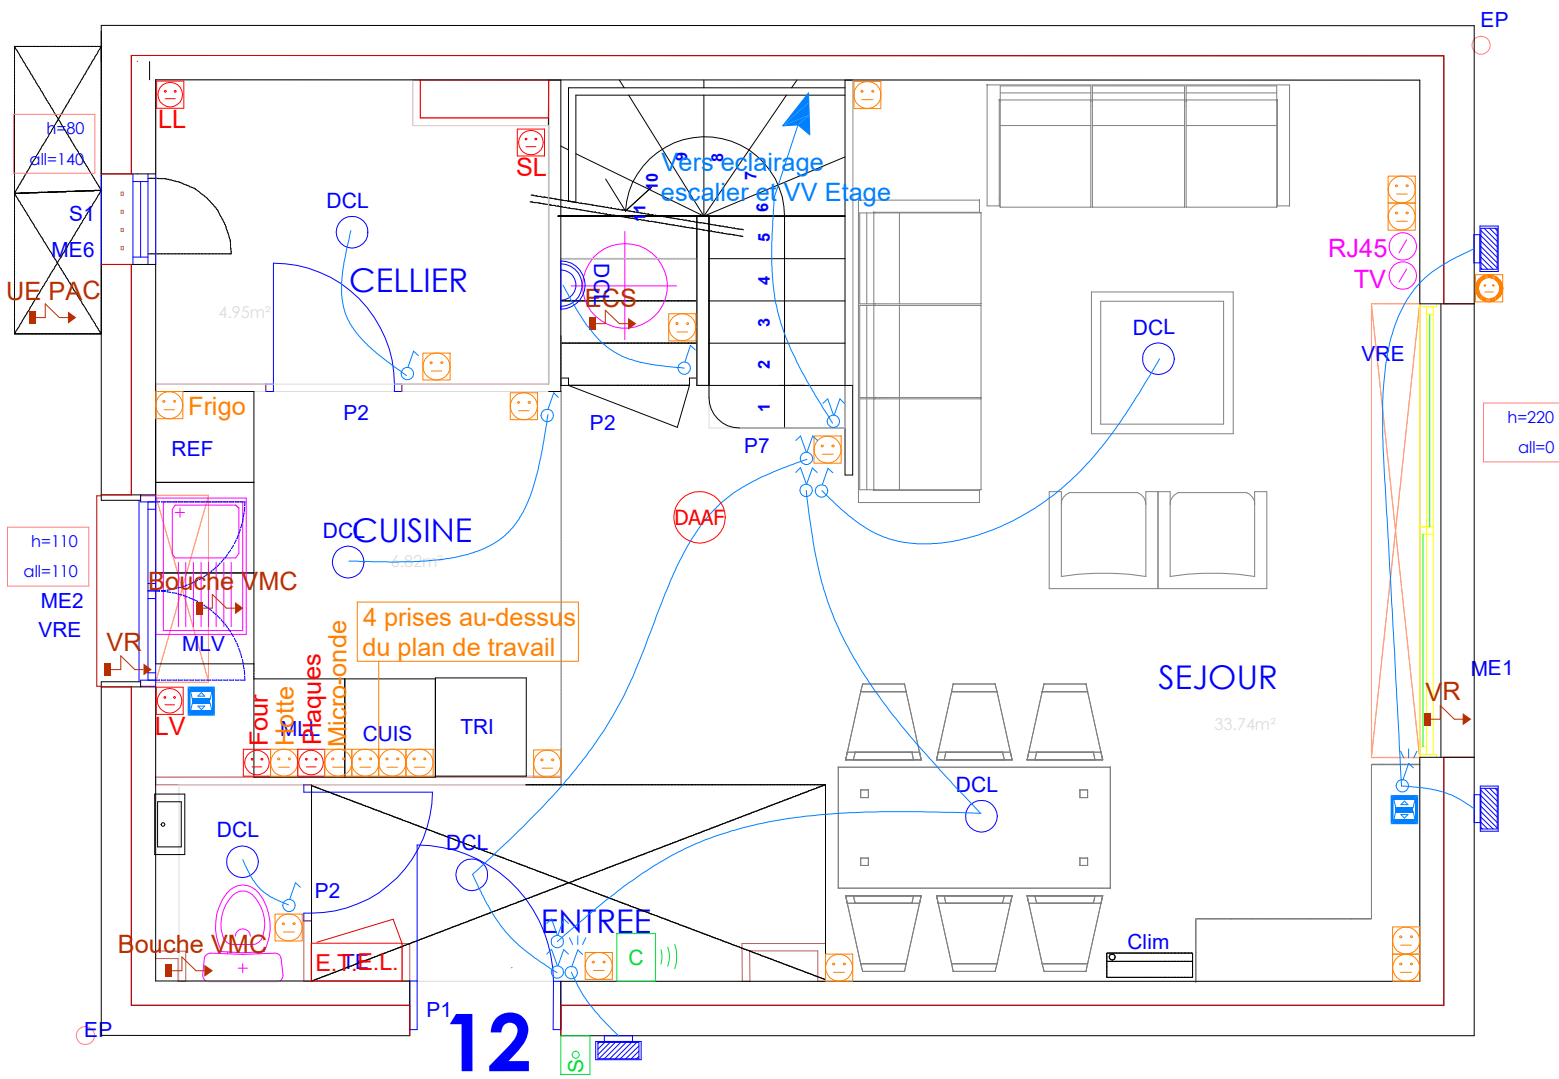

- Légende : Électricité CFO**
- DCL DCL Type : DCL plafond / DCL étanche plafond
 - DCL DCL Type : DCL applique / DCL étanche applique
 - Type : Applique extérieure
 - Commande volet roulant
 - Télerupteur
 - Interrupteur va et vient
 - Interrupteur simple allumage
 - Interrupteur simple allumage à voyant
 - Interrupteur va et vient à voyant
 - Interrupteur double allumage
 - Simple prise de courant 2P+T 10/16A
 - Simple prise de courant 2P+T 10/16A étanche
 - Prise de Courant sur circuit dédié
 - E.T.E.L. Espace Technique Electrique du Logement
 - SG Tableau Electrique Services Généraux (Communs)
 - Fourreau ELEC
 - Alimentation électrique
- Légende : Électricité CFA**
- Prise RJ45
 - Détecteur de fumée
 - Sonnette
 - Carillon

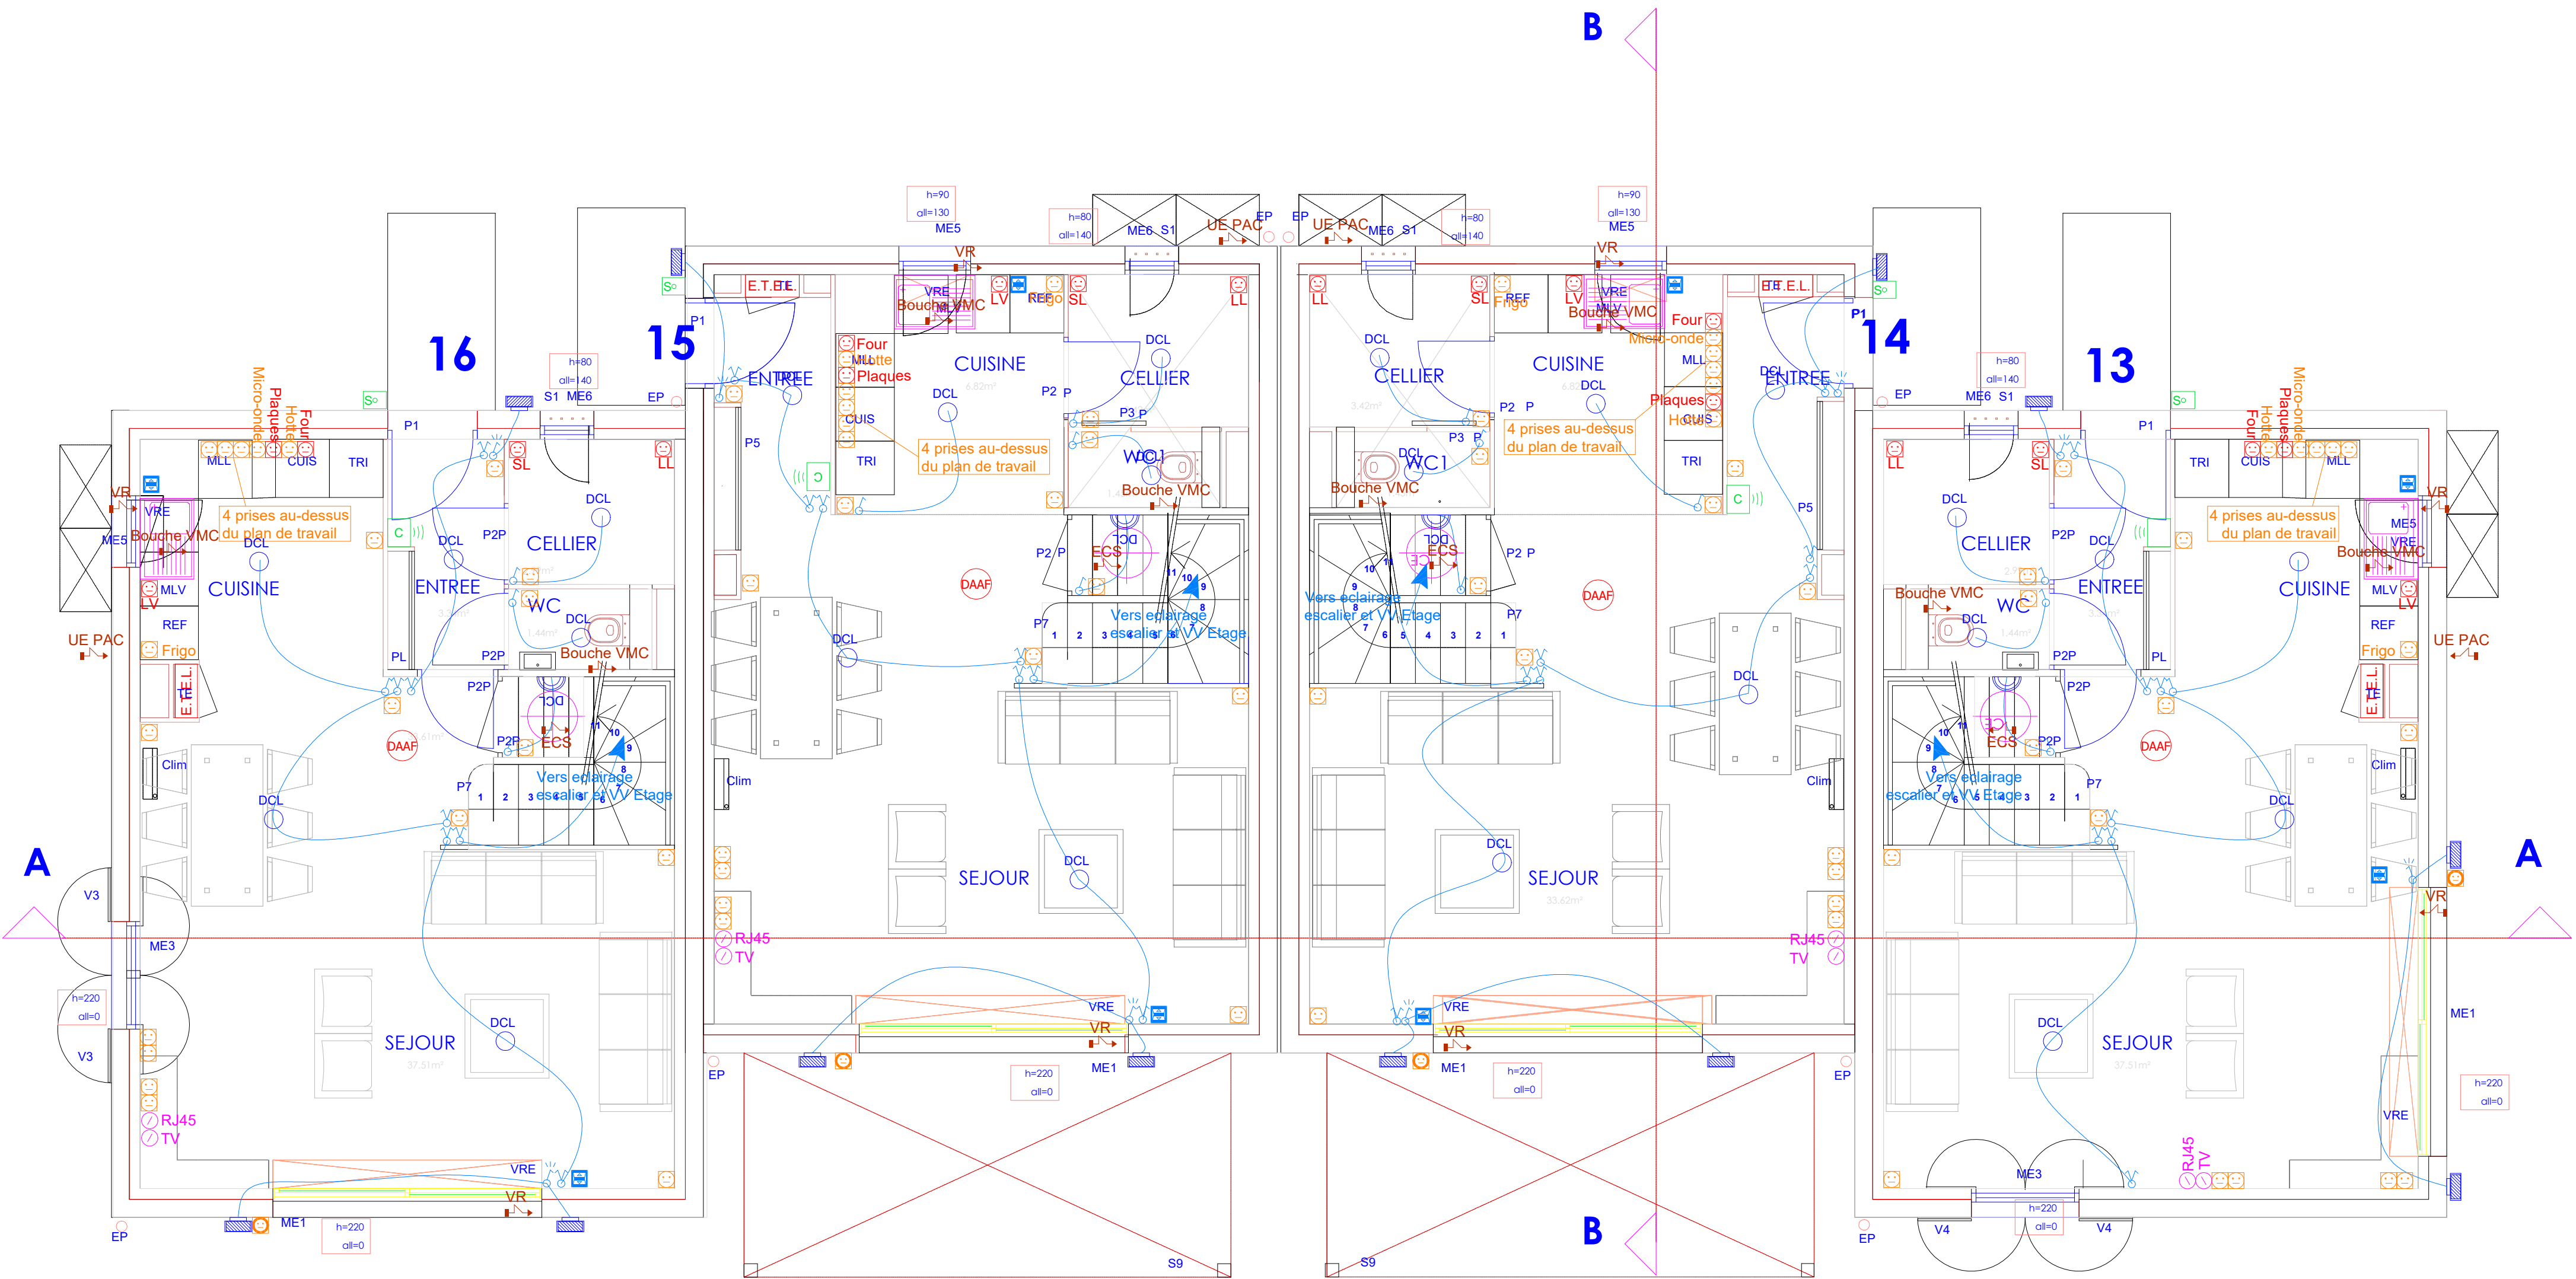

villa 16

villa 15

villa 14

villa 13

REZ DE CHAUSSEE

CONSTRUCTION DE 18 LOGEMENTS
RUE NEUVE GRAND TERRE
13930 AUREILLE

VILLAS 12 - 13 - 14 - 15 - 16

MAITRISE D'OUVRAGE
SCCV GRANDE TERRE
837 BIS ALLEE DE PARIS
LA SEYNE SUR MER

MAITRISE D'OEUVRE
AXXION
41 Rue Ribas
13770 VENELLES

BET FLUIDES CVC
AXIO INGENIERIE
393 Rue Ettore BUGATTI
66000 PERPIGNAN
axio.ingenierie@gmail.com

LOT ELECTRICITE
PLAN D'IMPLANTATION RDC

Ind	Date	Modifications	Dessiné par:	Vérifié par:
0	06/07/2026	Création du document	EB	LG
A			Date:	Echelle:
B			06/07/2026	1:25
C			Visa :	
D				

NIVEAU	LOT	DOSSIER	PHASE	N° DOCUMENT	INDICE
R0	ELEC		DCE	701	0