


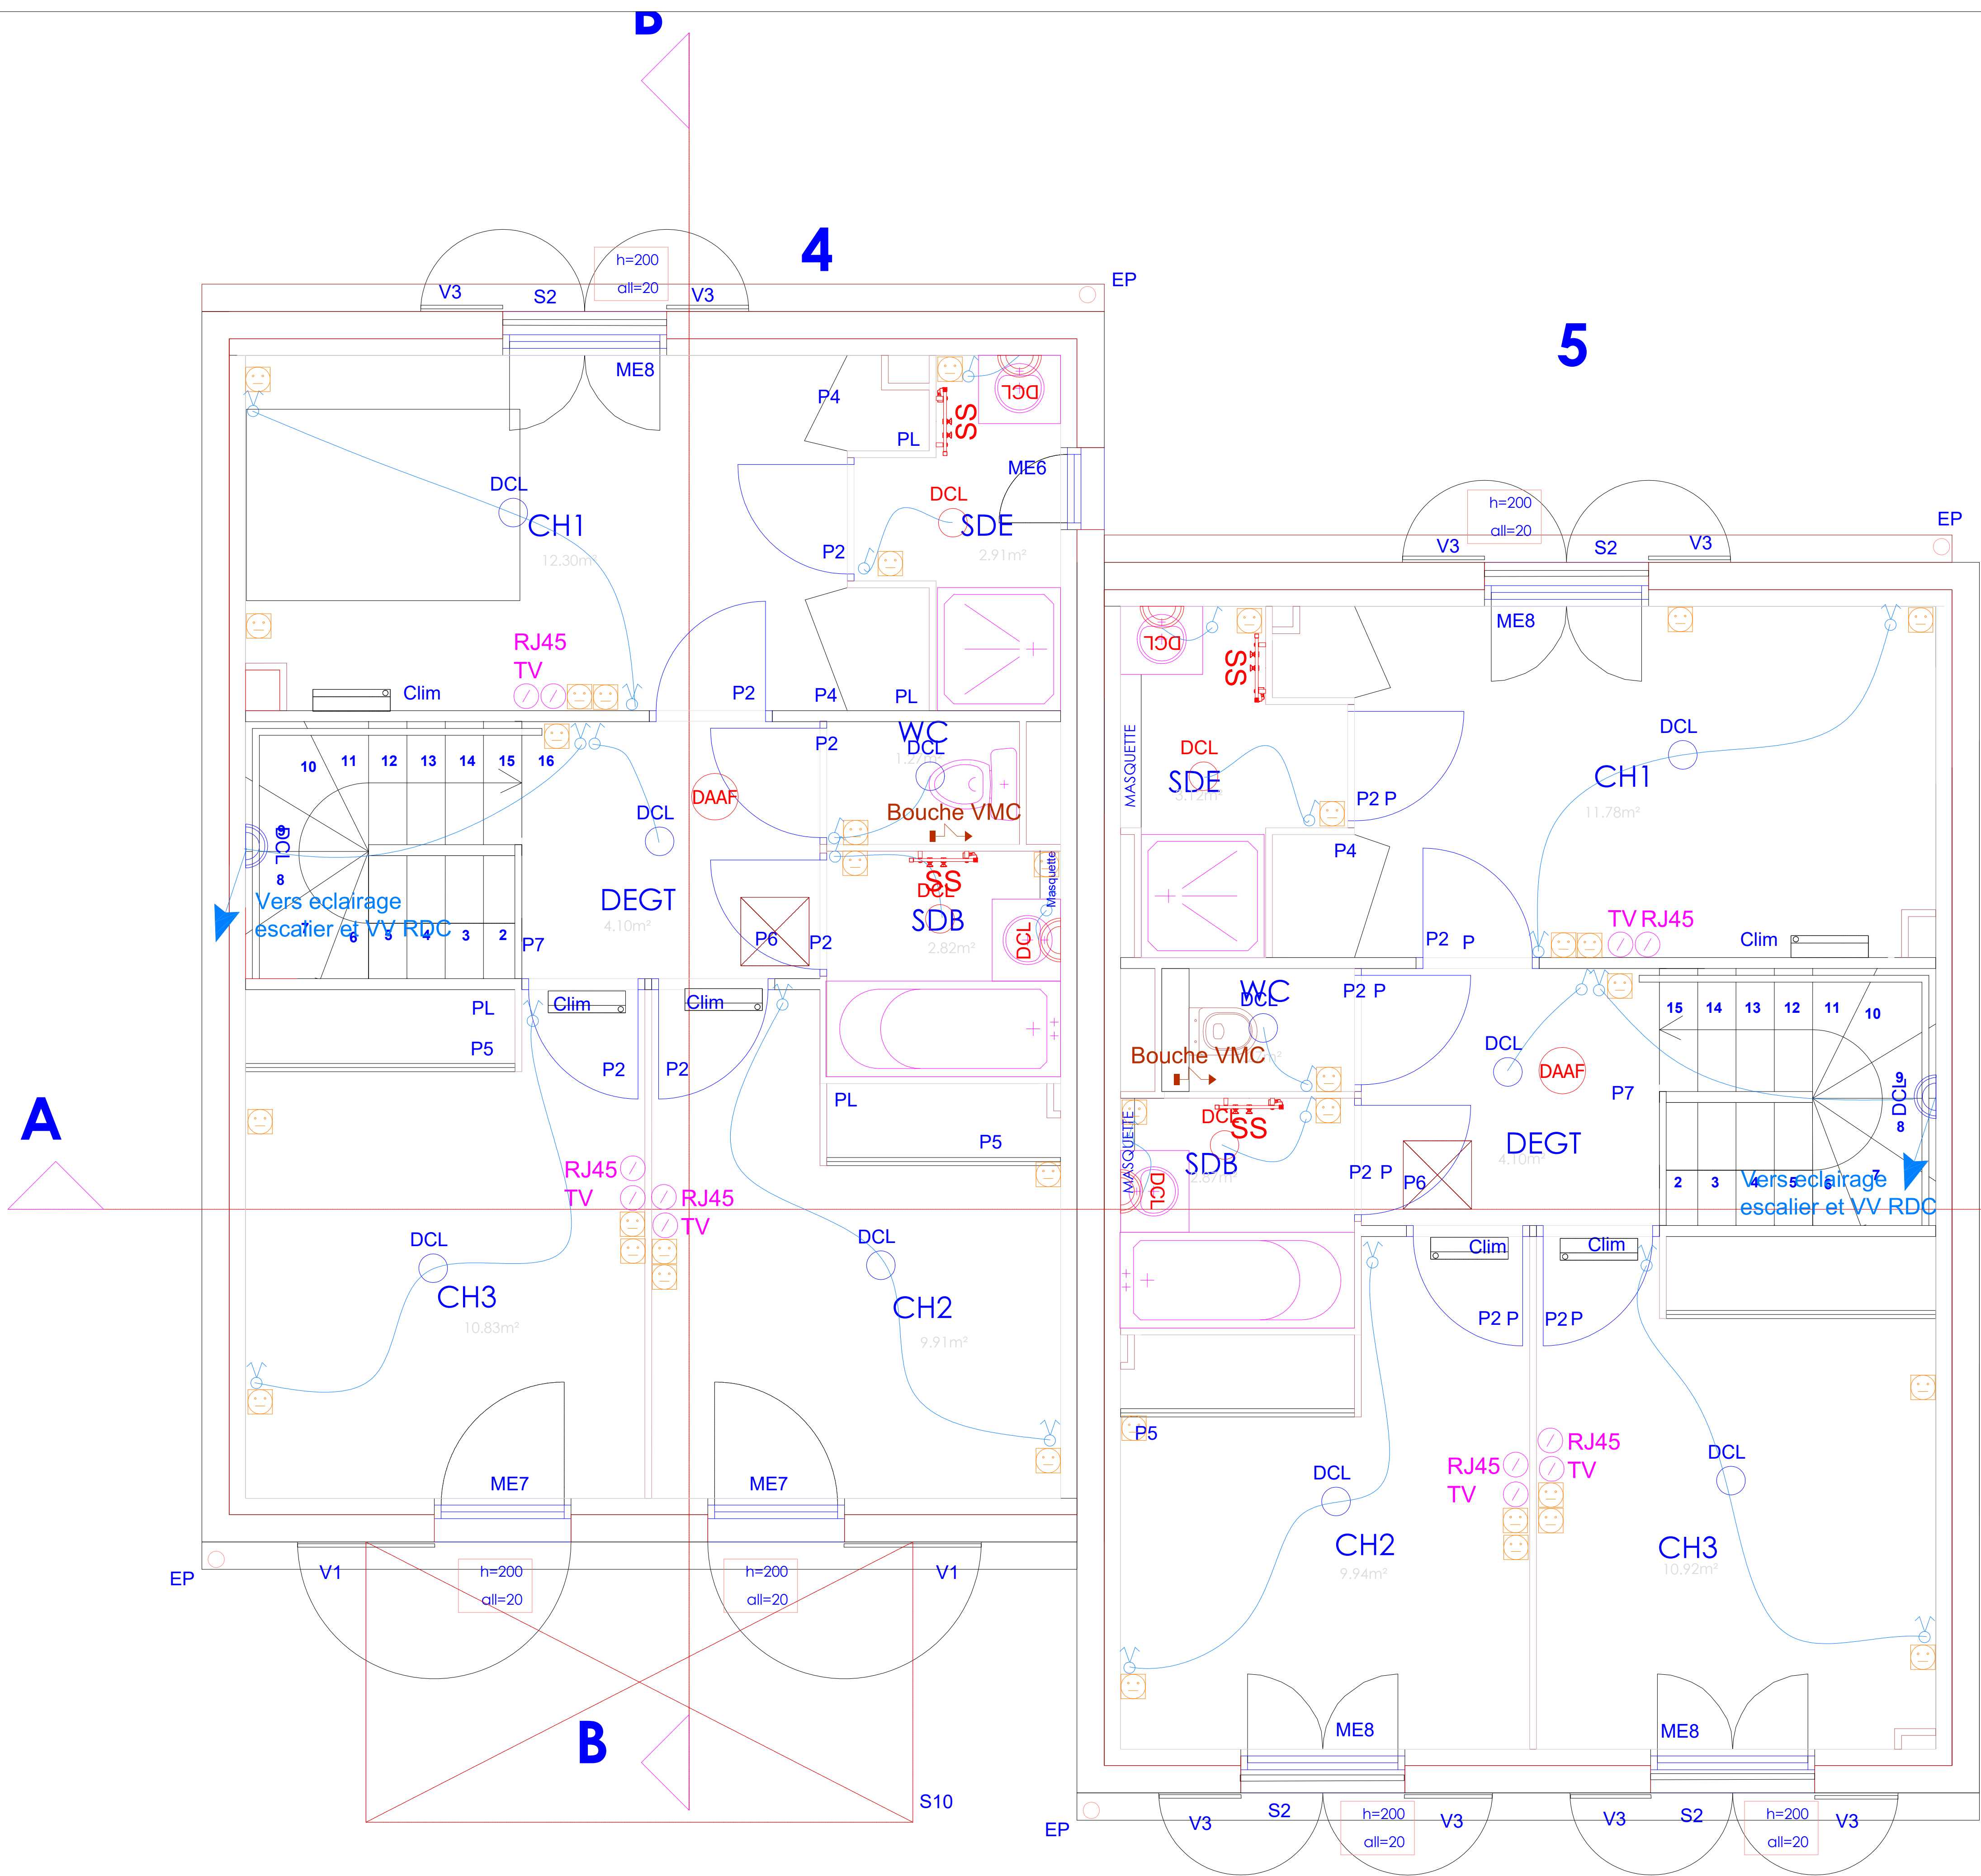

Légende : Électricité CFO

DCL

DCL

Type : DCL plafond / DCL étanche plafond

DCL

DCL

Type : DCL applique / DCL étanche applique

Type : Applique extérieure

Commande volet roulant

Télérupteur

Interrupteur va et vient

Interrupteur simple allumage

Interrupteur simple allumage à voyant

Interrupteur va et vient à voyant

Interrupteur double allumage

Simple prise de courant 2P+T 10/16A

Simple prise de courant 2P+T 10/16A étanche

Prise de Courant sur circuit dédié

E.T.E.L.

Espace Technique Electrique du Logement

SG

Tableau Electrique Services Généraux (Communs)

Fourreau ELEC

Alimentation électrique

Légende : Électricité CFAPrise RJ45Détecteur de fuméeSonnetteCarillon

CONSTRUCTION DE 18 LOGEMENTS
RUE NEUVE GRAND TERRE
13930 AUREILLE

VILLAS 4 - 5

MAITRISE D'OUVRAGE

SCCV GRANDE TERRE
837 BIS ALLEE DE PARIS
LA SEYNE SUR MER

MAITRISE D'OEUVRE

AXXION
41 Rue Ribas
13770 VENELLES

BET FLUIDES CVC
AXIO INGENIERIE
393 Rue Ettore BUGATTI
66000 PERPIGNAN
axio.ingenierie@gmail.com



LOT ELECTRICITE
PLAN D'IMPLANTATION R+1

Ind	Date	Modifications	Dessiné par:	Vérifié par:
0	06/07/2026	Création du document	EB	LG
A			Date:	Echelle:
B			06/07/2026	1:25
C			Visa :	
D				

NIVEAU	LOT	DOSSIER	PHASE	N° DOCUMENT	INDICE
R1	ELEC		DCE	711	0