


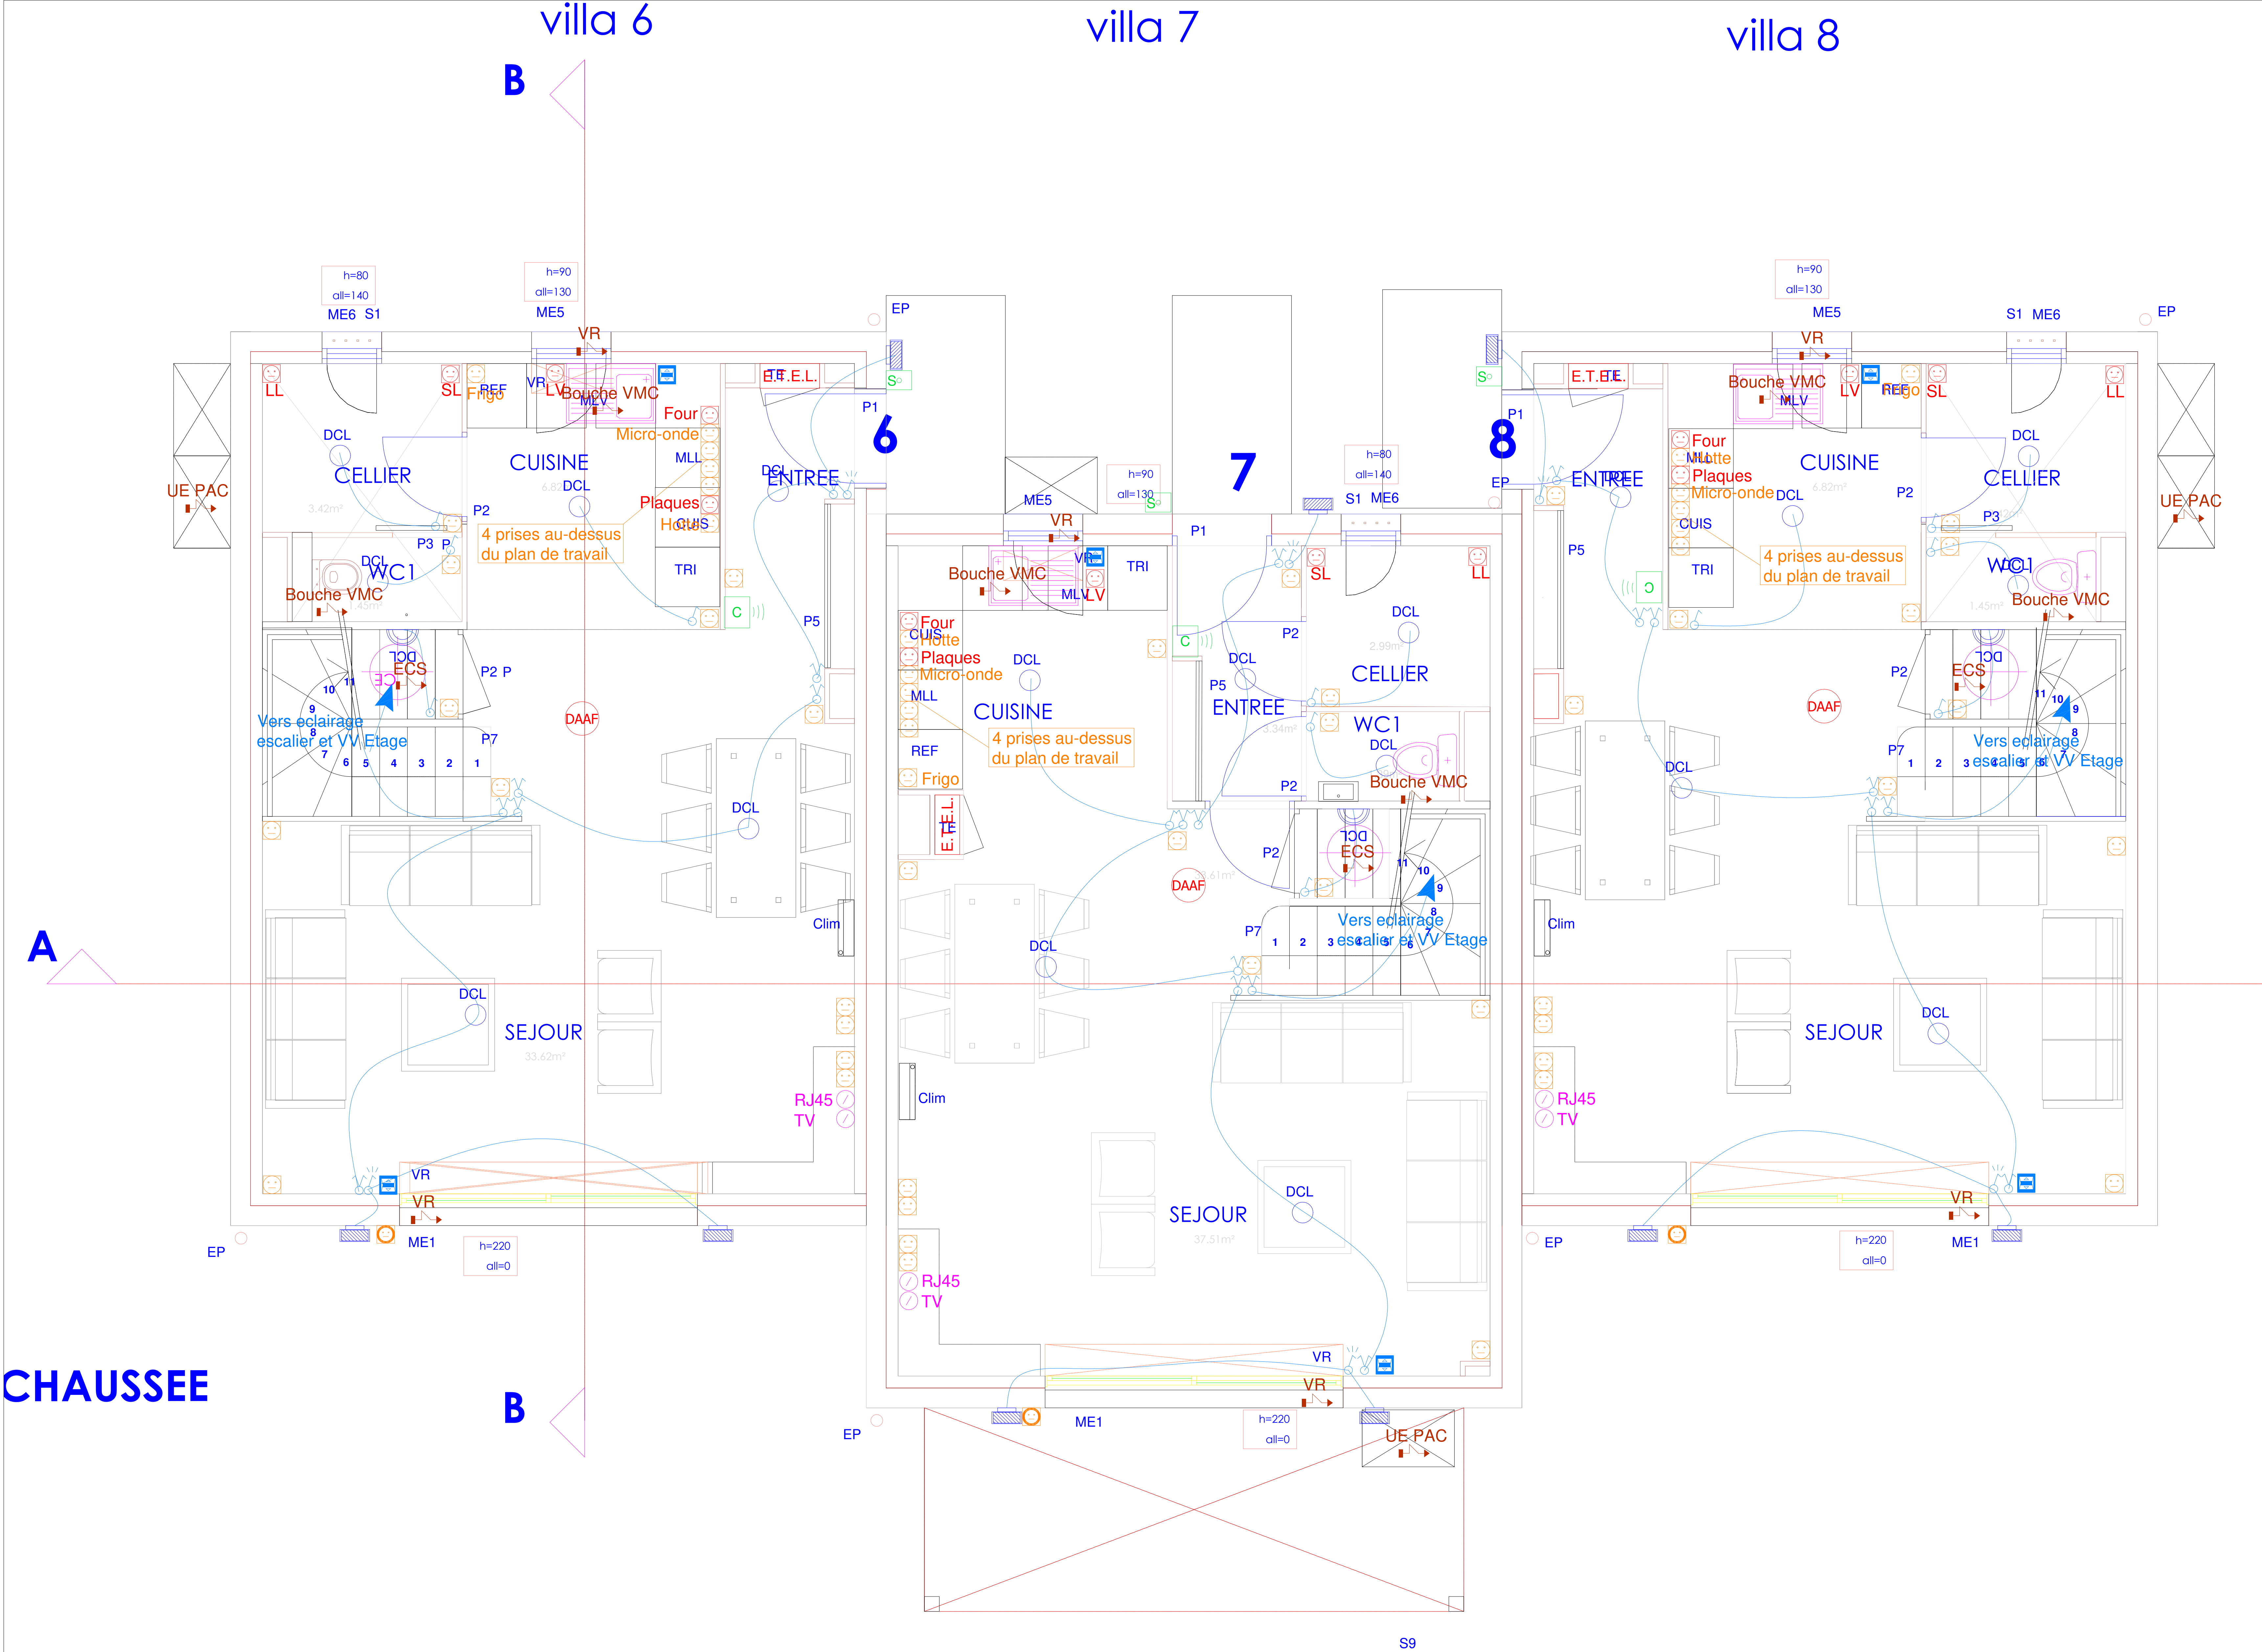

**Légende : Électricité CFO**

- Type : DCL plafond / DCL étanche plafond
- Type : DCL applique / DCL étanche applique
- Type : Applique extérieure
- Commande volet roulant
- Télérupteur
- Interrupteur va et vient
- Interrupteur simple allumage
- Interrupteur simple allumage à voyant
- Interrupteur va et vient à voyant
- Interrupteur double allumage
- Simple prise de courant 2P+T 10/16A
- Simple prise de courant 2P+T 10/16A étanche
- Prise de Courant sur circuit dédié
- Espace Technique Electrique du Logement
- Tableau Electrique Services Généraux (Communs)
- Fourreau ELEC
- Alimentation électrique

**Légende : Électricité CFA**

- Prise RJ45
- Détecteur de fumée
- Sonnette
- Carillon

CONSTRUCTION DE 18 LOGEMENTS  
RUE NEUVE GRAND TERRE  
13930 AUREILLE

VILLAS 6 - 7 - 8

MAITRISE D'OUVRAGE  
SCV GRANDE TERRE  
837 BIS ALLEE DE PARIS  
LA SEYNE SUR MER

MAITRISE D'OEUVRE  
AXION  
41 Rue Ribas  
13770 VENELLES

BET FLUIDES CVC  
AXIO INGENIERIE  
393 Rue Ettore BUGATTI  
66000 PERPIGNAN  
axio.ingenierie@gmail.com

LOT ELECTRICITE  
PLAN D'IMPLANTATION RDC

| Ind | Date       | Modifications        | Dessiné par: | Vérifié par: |
|-----|------------|----------------------|--------------|--------------|
| 0   | 06/07/2026 | Création du document | EB           | LG           |
| A   |            |                      | Date:        | Echelle:     |
| B   |            |                      | 06/07/2026   | 1:25         |
| C   |            |                      | Visa:        |              |
| D   |            |                      |              |              |

| NIVEAU | LOT  | DOSSIER | PHASE | N° DOCUMENT | INDICE |
|--------|------|---------|-------|-------------|--------|
| R0     | ELEC |         | DCE   | 701         | 0      |