


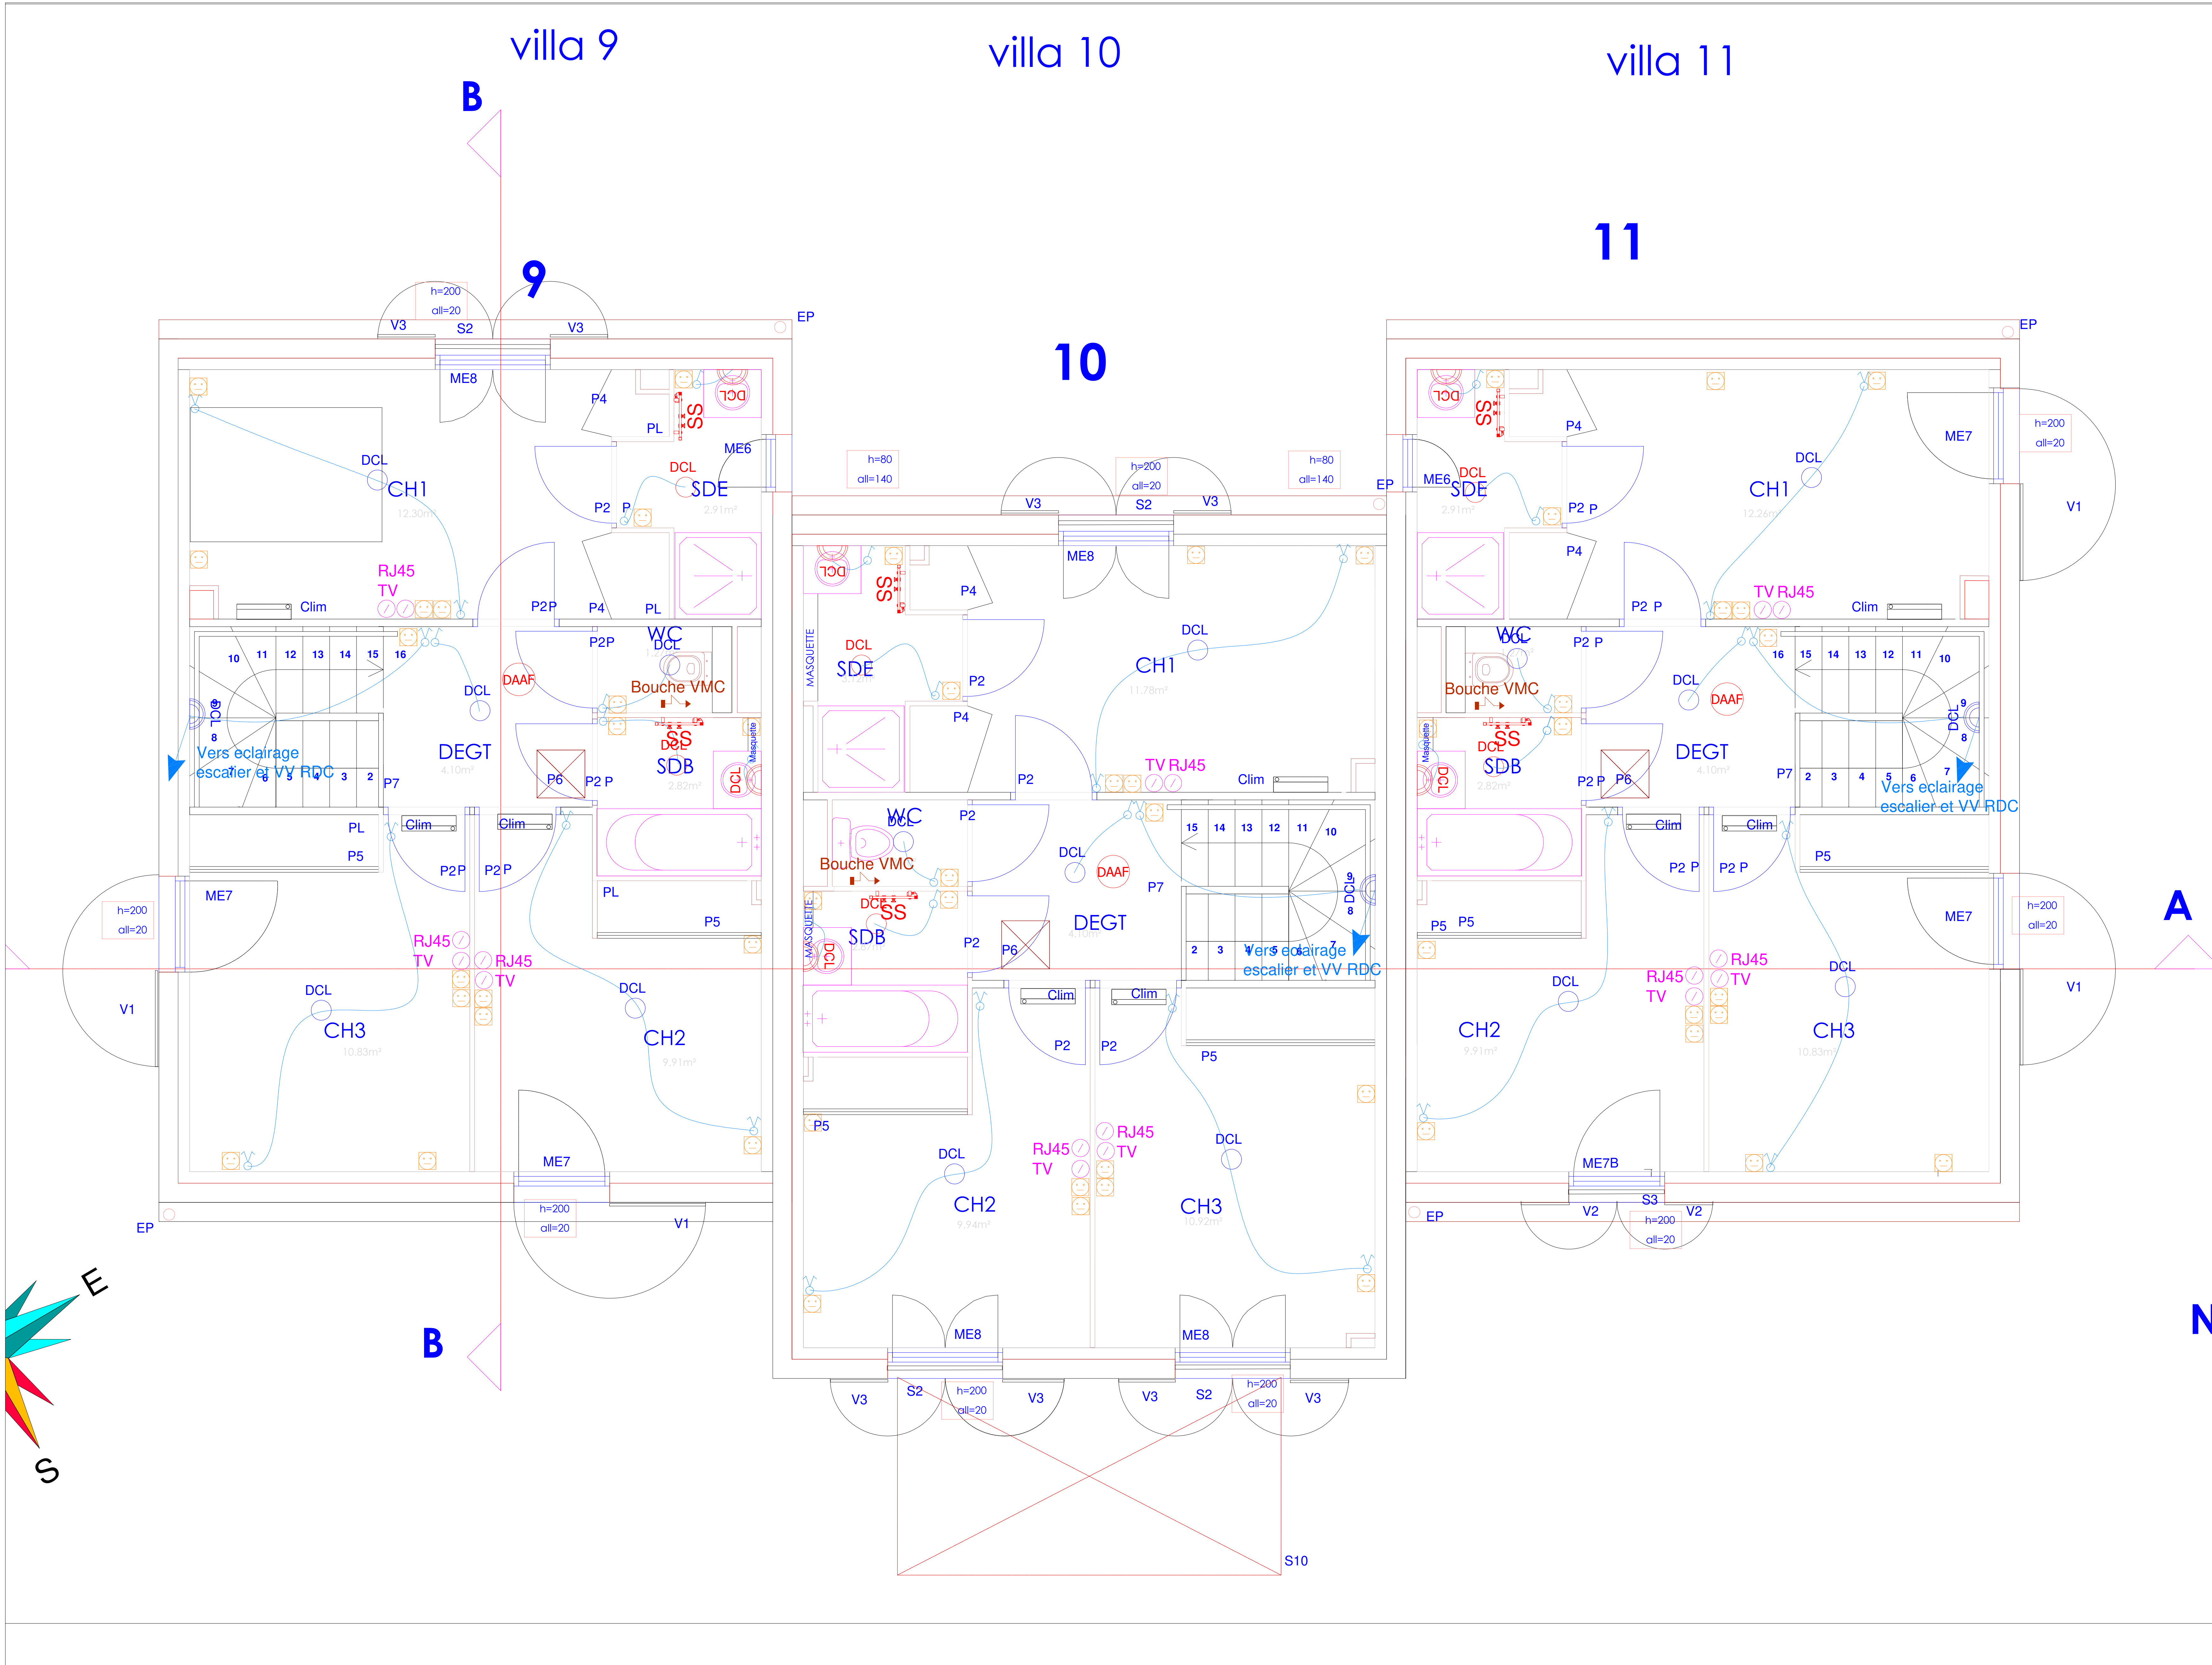

Légende : Électricité CFO

		Type : DCL plafond / DCL étanche plafond
		Type : DCL applique / DCL étanche applique
		Type : Applique extérieure
		Commande volet roulant
		Télérupteur
		Interrupteur va et vient
		Interrupteur simple allumage
		Interrupteur simple allumage à voyant
		Interrupteur va et vient à voyant
		Interrupteur double allumage
		Simple prise de courant 2P+T 10/16A
		Simple prise de courant 2P+T 10/16A étanche
		Prise de Courant sur circuit dédié
		Espace Technique Electrique du Logement
		Tableau Electrique Services Généraux (Communs)
		Fourreau ELEC
		Alimentation électrique

Légende : Électricité CFA

	Prise RJ45
	DéTECTEUR DE FUMÉE
	Sonnette
	Carillon

CONSTRUCTION DE 18 LOGEMENTS
RUE NEUVE GRAND TERRE
13930 AUREILLE

VILLAS 9 - 10 - 11

MAITRISE D'OUVRAGE
SCV GRANDE TERRE
837 BIS ALLEE DE PARIS
LA SEYNE SUR MER

MAITRISE D'OEUVRE
AXION
41 Rue Ribas
13770 VENELLES

BET FLUIDES CVC
AXIO INGENIERIE
393 Rue Ettore BUGATTI
66000 PERPIGNAN
axio.ingenierie@gmail.com



LOT ELECTRICITE
PLAN D'IMPLANTATION R+1

Ind	Date	Modifications	Dessiné par:	Vérifié par:
0	30/06/2026	Création du document	EB	LG
A			Date:	Echelle:
B			06/07/2026	1:25
C			Visa:	
D				

NIVEAU	LOT	DOSSIER	PHASE	N° DOCUMENT	INDICE
R1	ELEC		DCE	711	0