


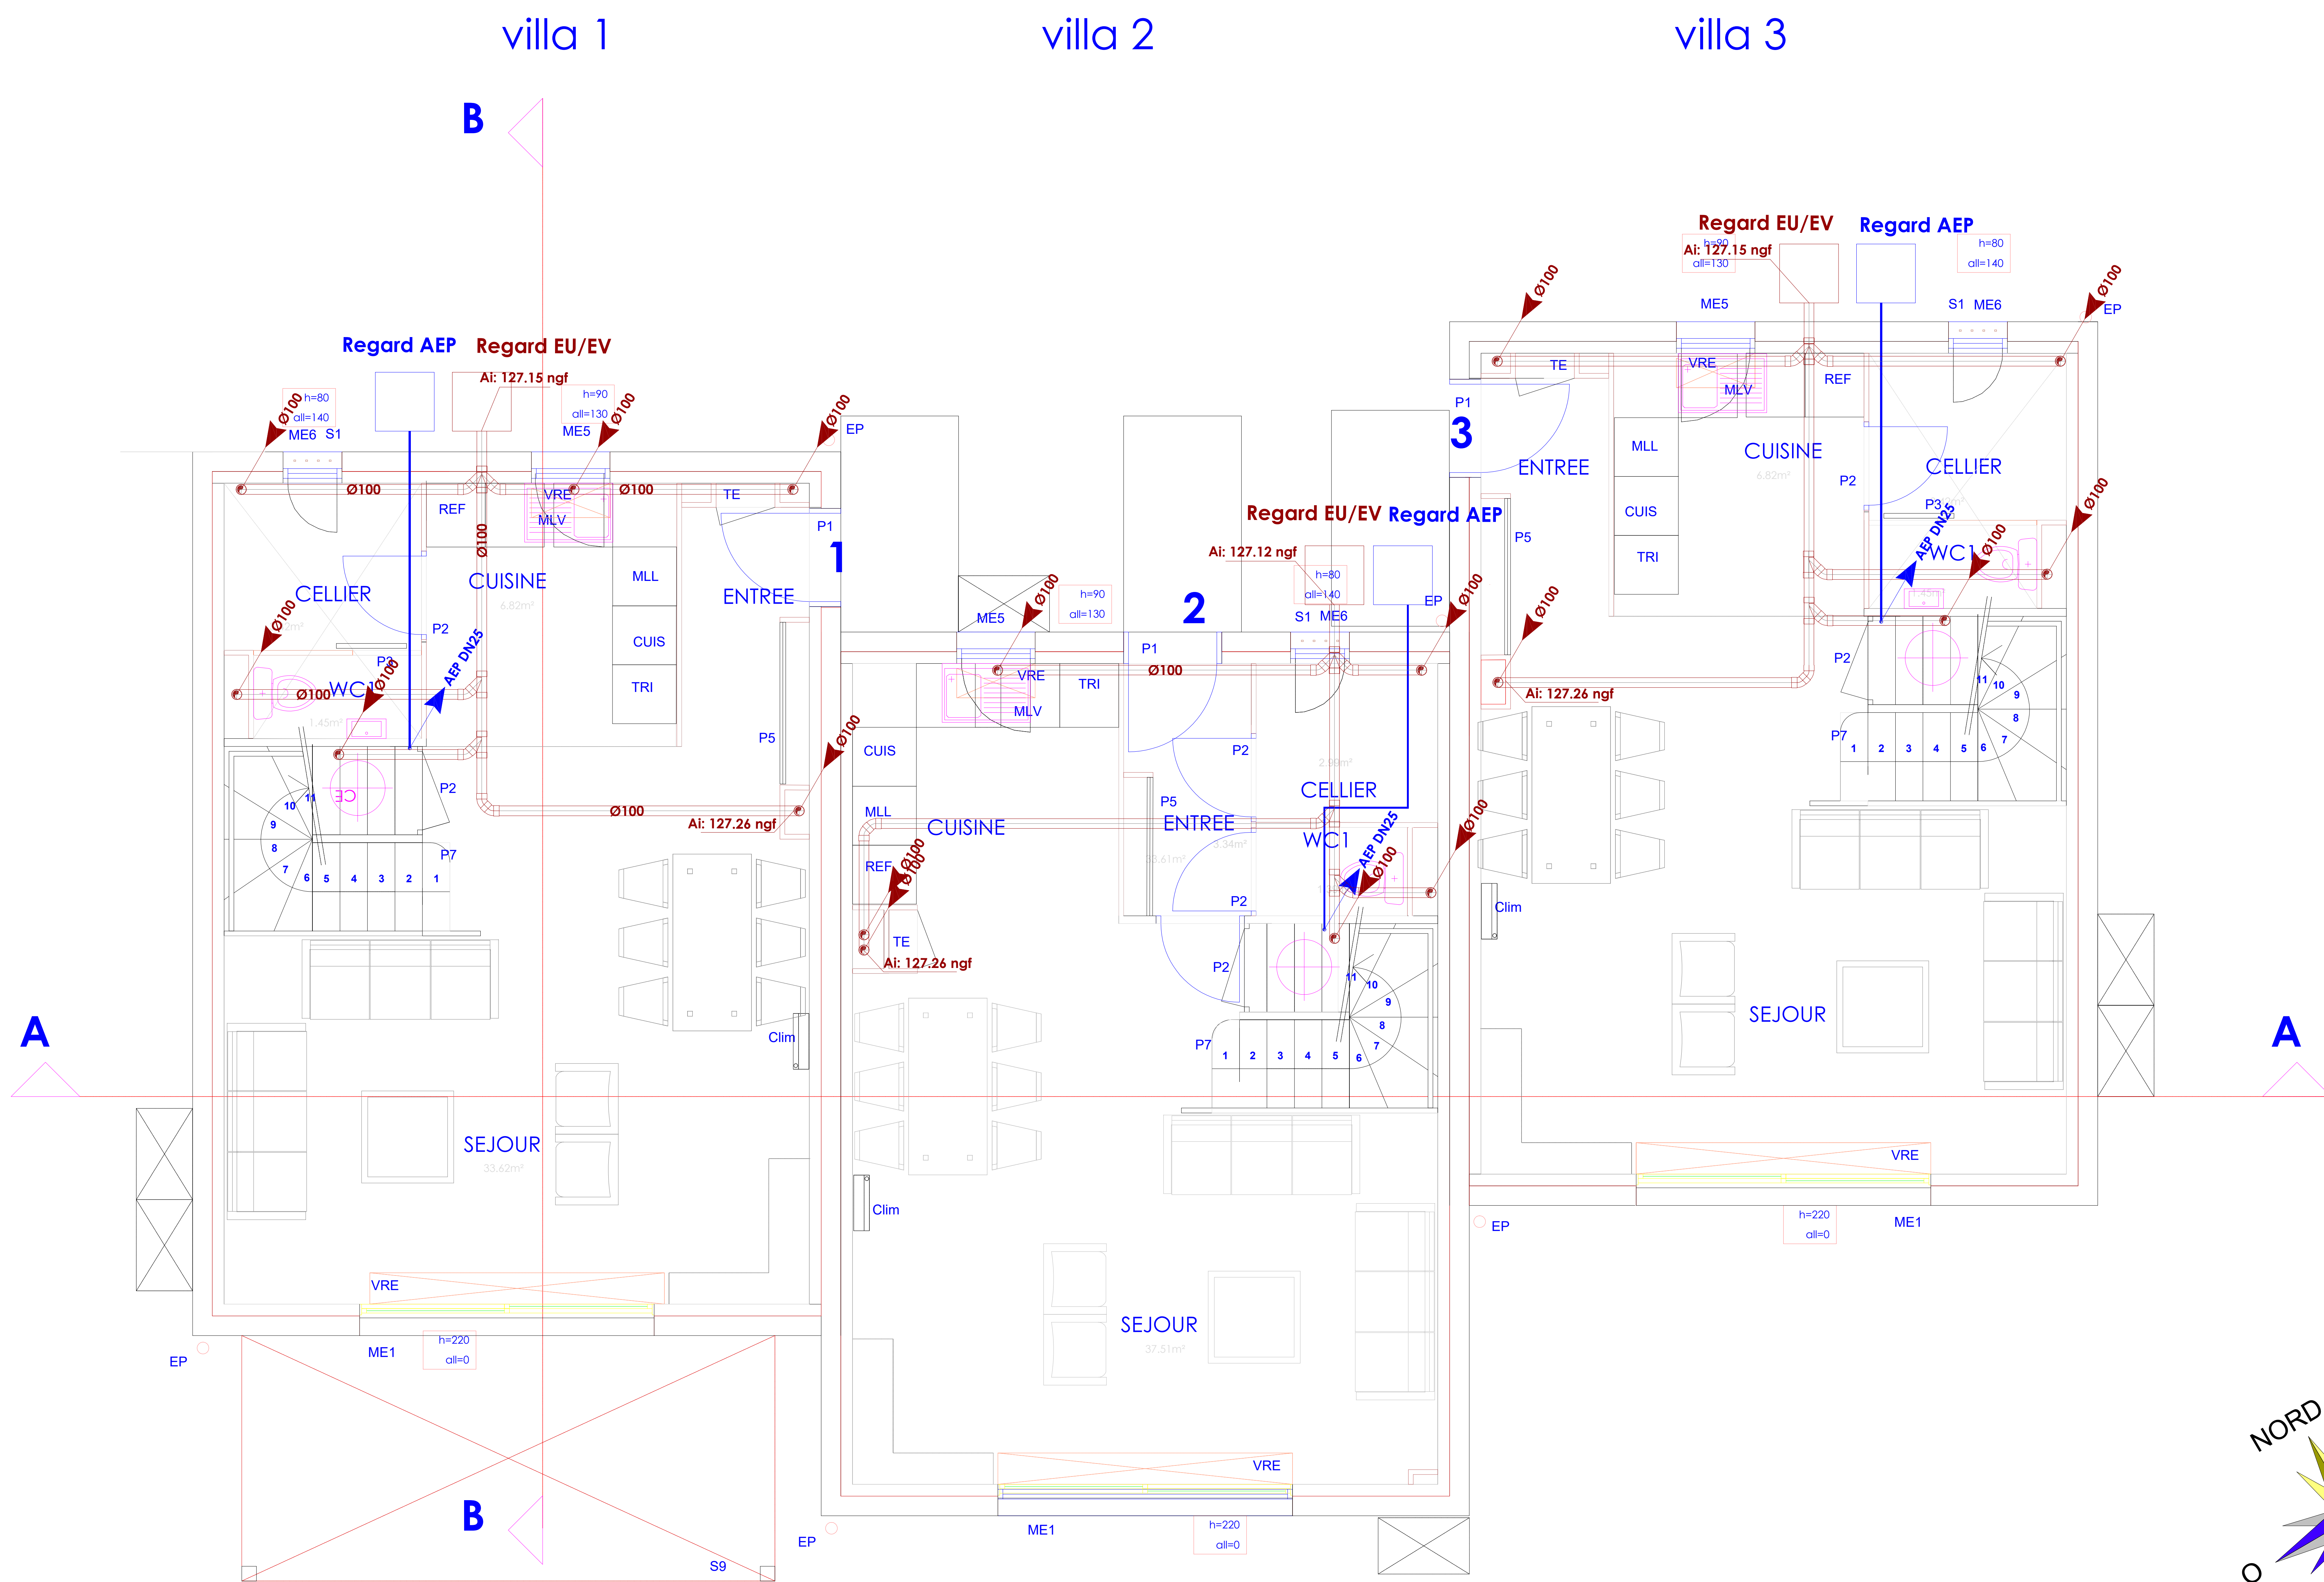

LEGENDE PLOMBERIE					
Eau froide sanitaire					
Eau chaude sanitaire					
Eaux usées					
Eaux vannes					
Condensats					
Siphon sec					
DEBIT DE BASE DES APPAREILS					
Désignation	Debit EF ECS	Quantité de	Debit EU EV	Quantité	
appareil	UA	reconnues PPS	UA	chacun	
Lavabo	0.30	10/12	0.75	40	
douche	0.30	13/16	0.5	40	
ec.	0.12	16/20	1.5	100	
Bagnoire	0.33	13/16	1.2	50	
Evier	0.20	13/16	0.75	40	
lave-vaisselle	low single	10/12	0.5	30	
rob. passage	0.33	13/16	0.5	30	
LEGENDE DIMENSIONNEMENT					
Vitesse réseau eau froide et eau chaude sanitaire : 1.5m/s en parties courbées et 3.0m/s en parties droites.					
perte EU, EV, EUS en Italie 2%					
perte EF en Italie 1.5%					

CONSTRUCTION DE 18 LOGEMENTS
RUE NEUVE GRAND TERRE
13930 AUREILLE

VILLAS 1 - 2 - 3

MAITRISE D'OUVRAGE
SCV GRANDE TERRE
837 BIS ALLÉE DE PARIS
LA SEYNE SUR MER

MAITRISE D'OEUVRE
AXXION
41 Rue Ribas
13770 VENELLES

BET FLUIDES CVC
AXIO INGENIERIE
393 Rue Etienne BUGATTI
66000 PERPIGNAN
axio.ingenierie@gmail.com



LOT PLOMBERIE, VMC & RAFFRAICHISSEMENT
PLAN VIDE SANITAIRE

Ind	Date	Modifications	Dessiné par:	Vérifié par:
0	06/07/2026	Création du document	EB	LG
A			Date:	Echelle:
B			06/07/2026	1:25
C			Visa:	
D				

NIVEAU	LOT	DOSSIER	PHASE	N° DOCUMENT	INDICE
VS	PB CVC		DCE	400	0