
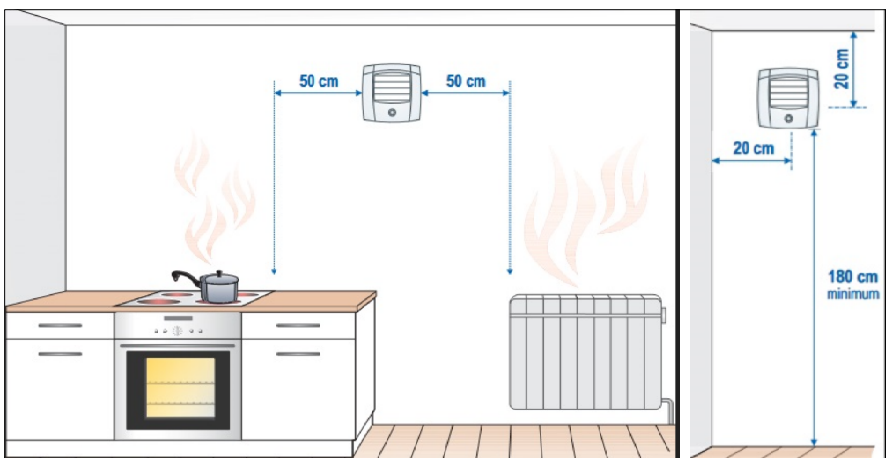


villa 1

villa 2

villa 3

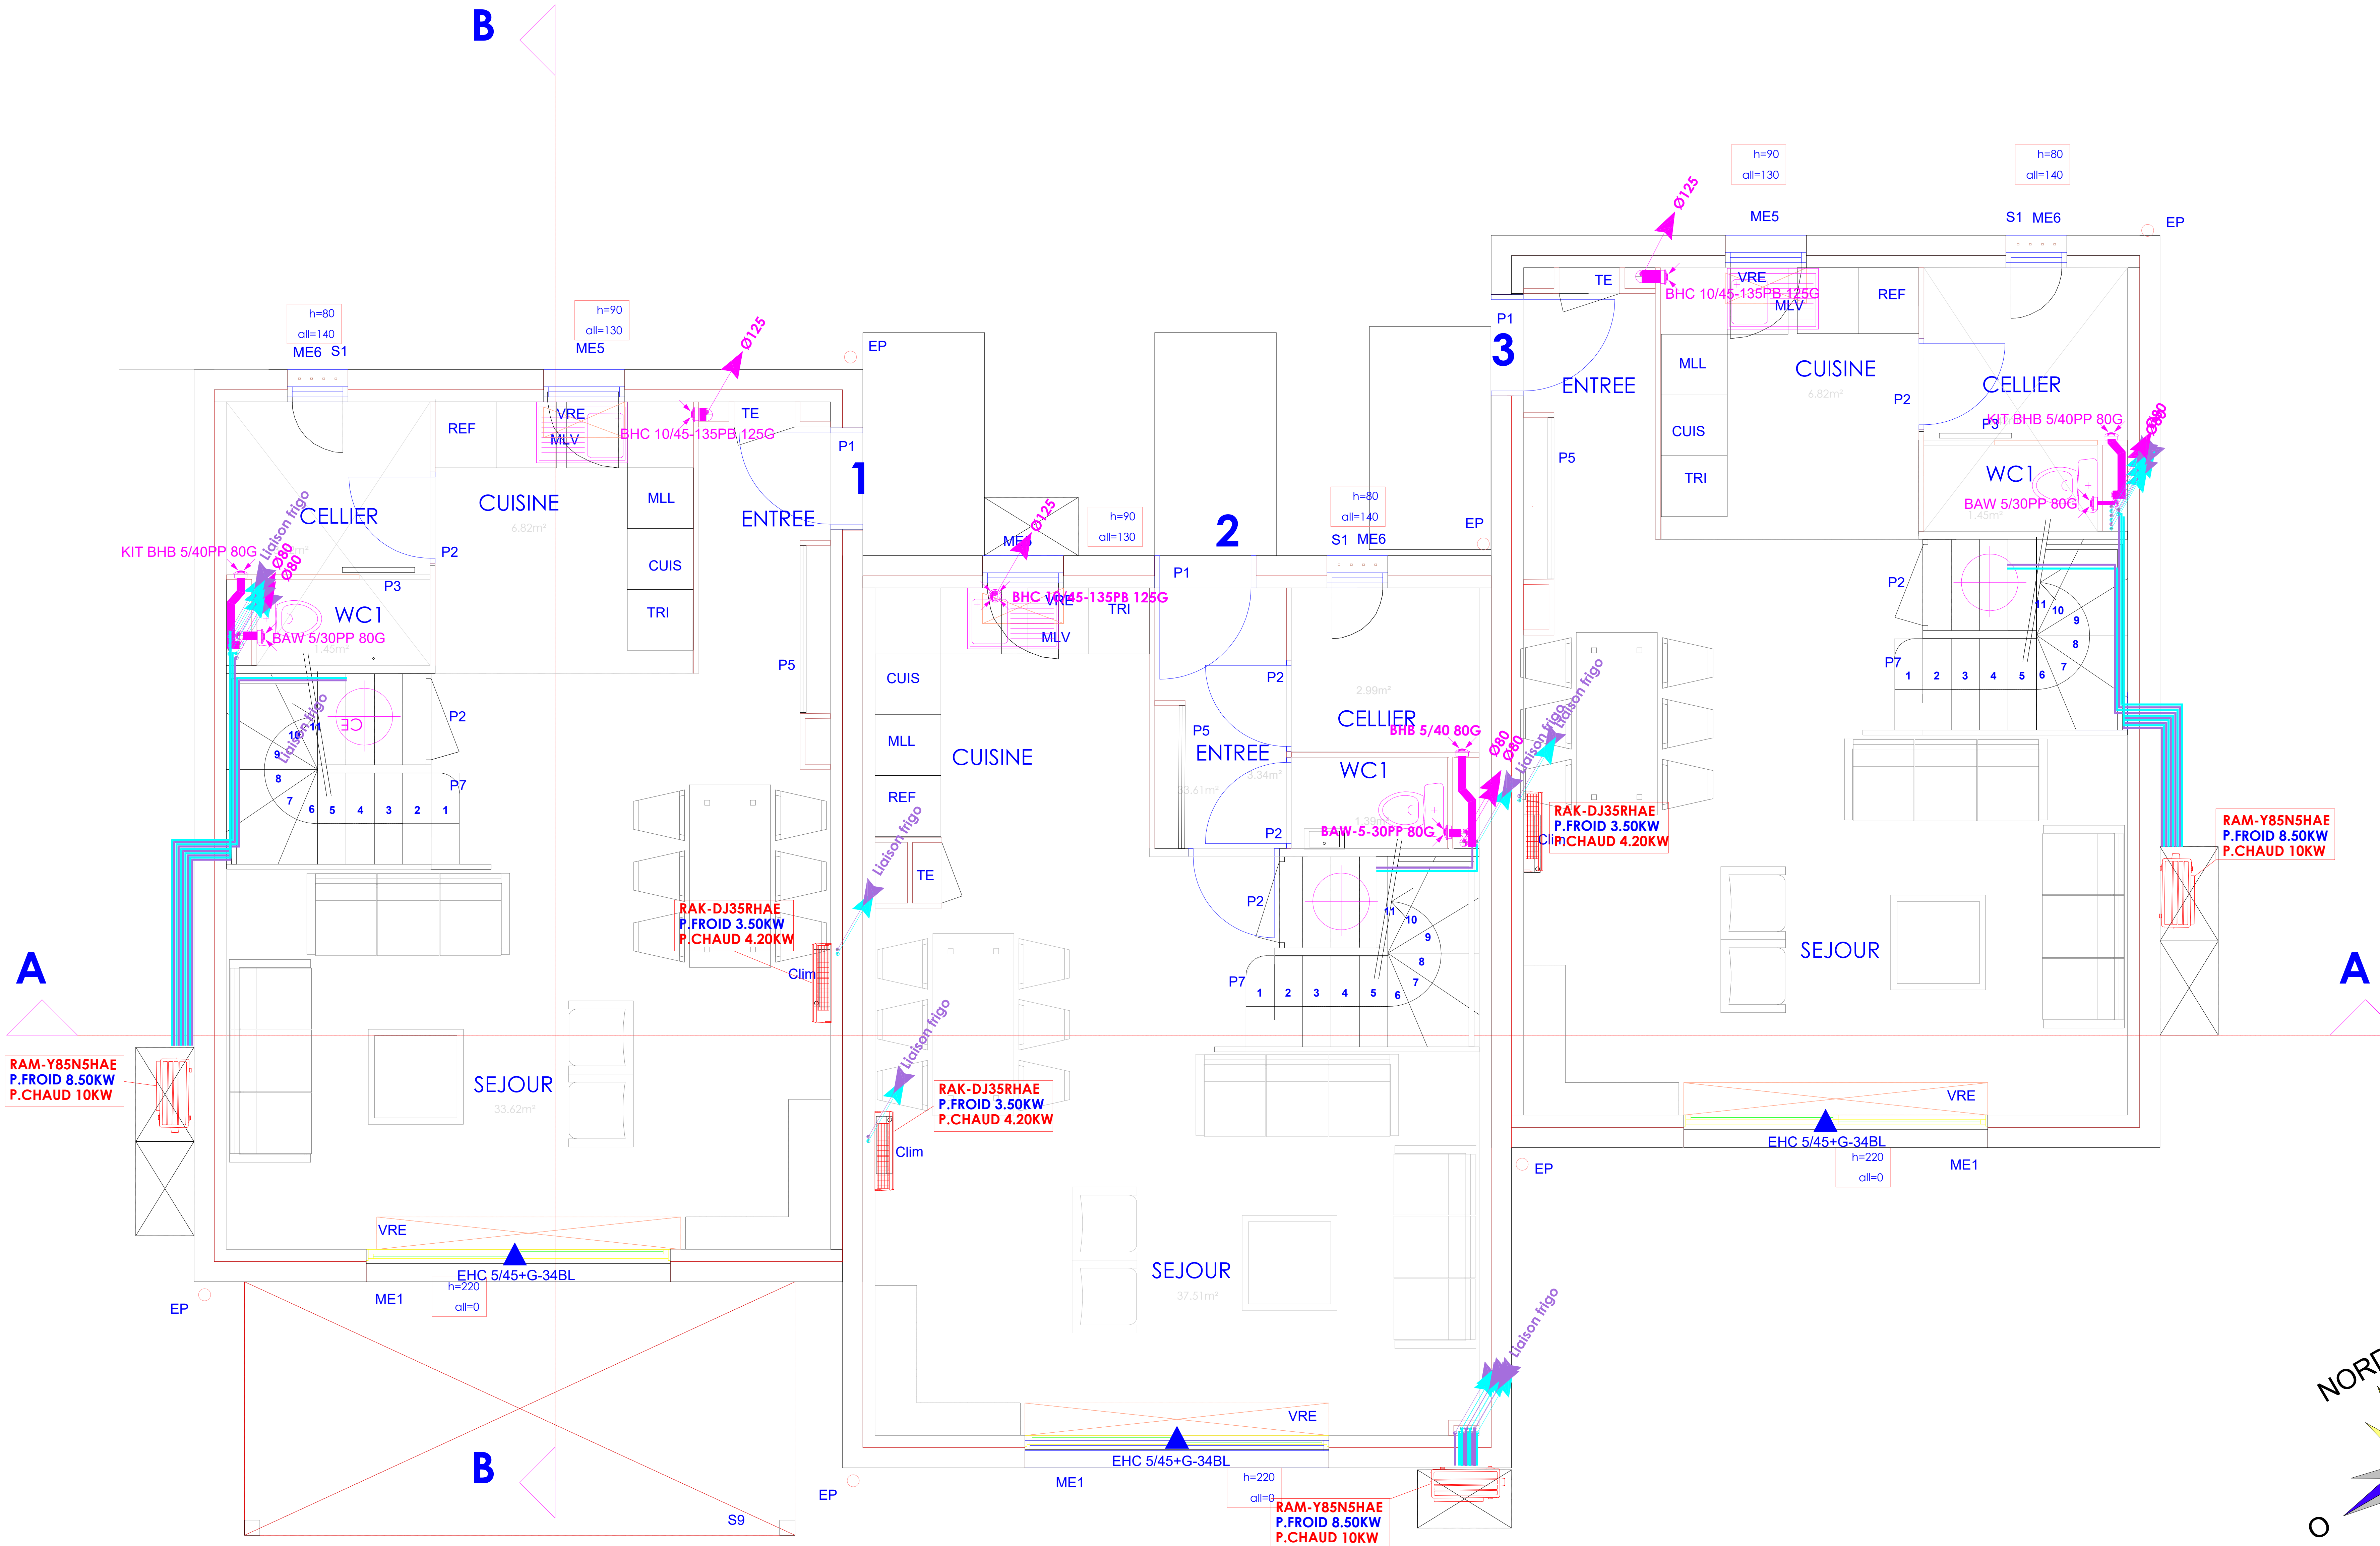

LEGENDE CHAUFFAGE

- Unité extérieure
- Unité murale
- Liaisons frigorifiques

LEGENDE VENTILATION

- Extraction VMC
- Entrée d'air
- Bouche d'extraction

CONSTRUCTION DE 18 LOGEMENTS
RUE NEUVE GRAND TERRE
13930 AUREILLE

VILLAS 1 - 2 - 3

MAITRISE D'OUVRAGE
SCV GRANDE TERRE
837 BIS ALLEE DE PARIS
LA SEYNE SUR MER

MAITRISE D'OEUVRE
AXXION
41 Rue Ribas
13770 VENELLES

BET FLUIDES CVC
AXIO INGENIERIE
393 Rue Etienne BUGATTI
66000 PERPIGNAN
axio.ingenierie@gmail.com



LOT PLOMBERIE, VMC & RAFFRAICHISSEMENT
PLAN CHAUFFAGE VENTILATION RDC

Ind	Date	Modifications	Dessiné par:	Vérifié par:
0	06/07/2026	Création du document	EB	LG
A			Date:	Echelle:
B			06/07/2026	1:25
C			Visa:	
D				

NIVEAU	LOT	DOSSIER	PHASE	N° DOCUMENT	INDICE
R0	PB CVC		DCE	402	0

