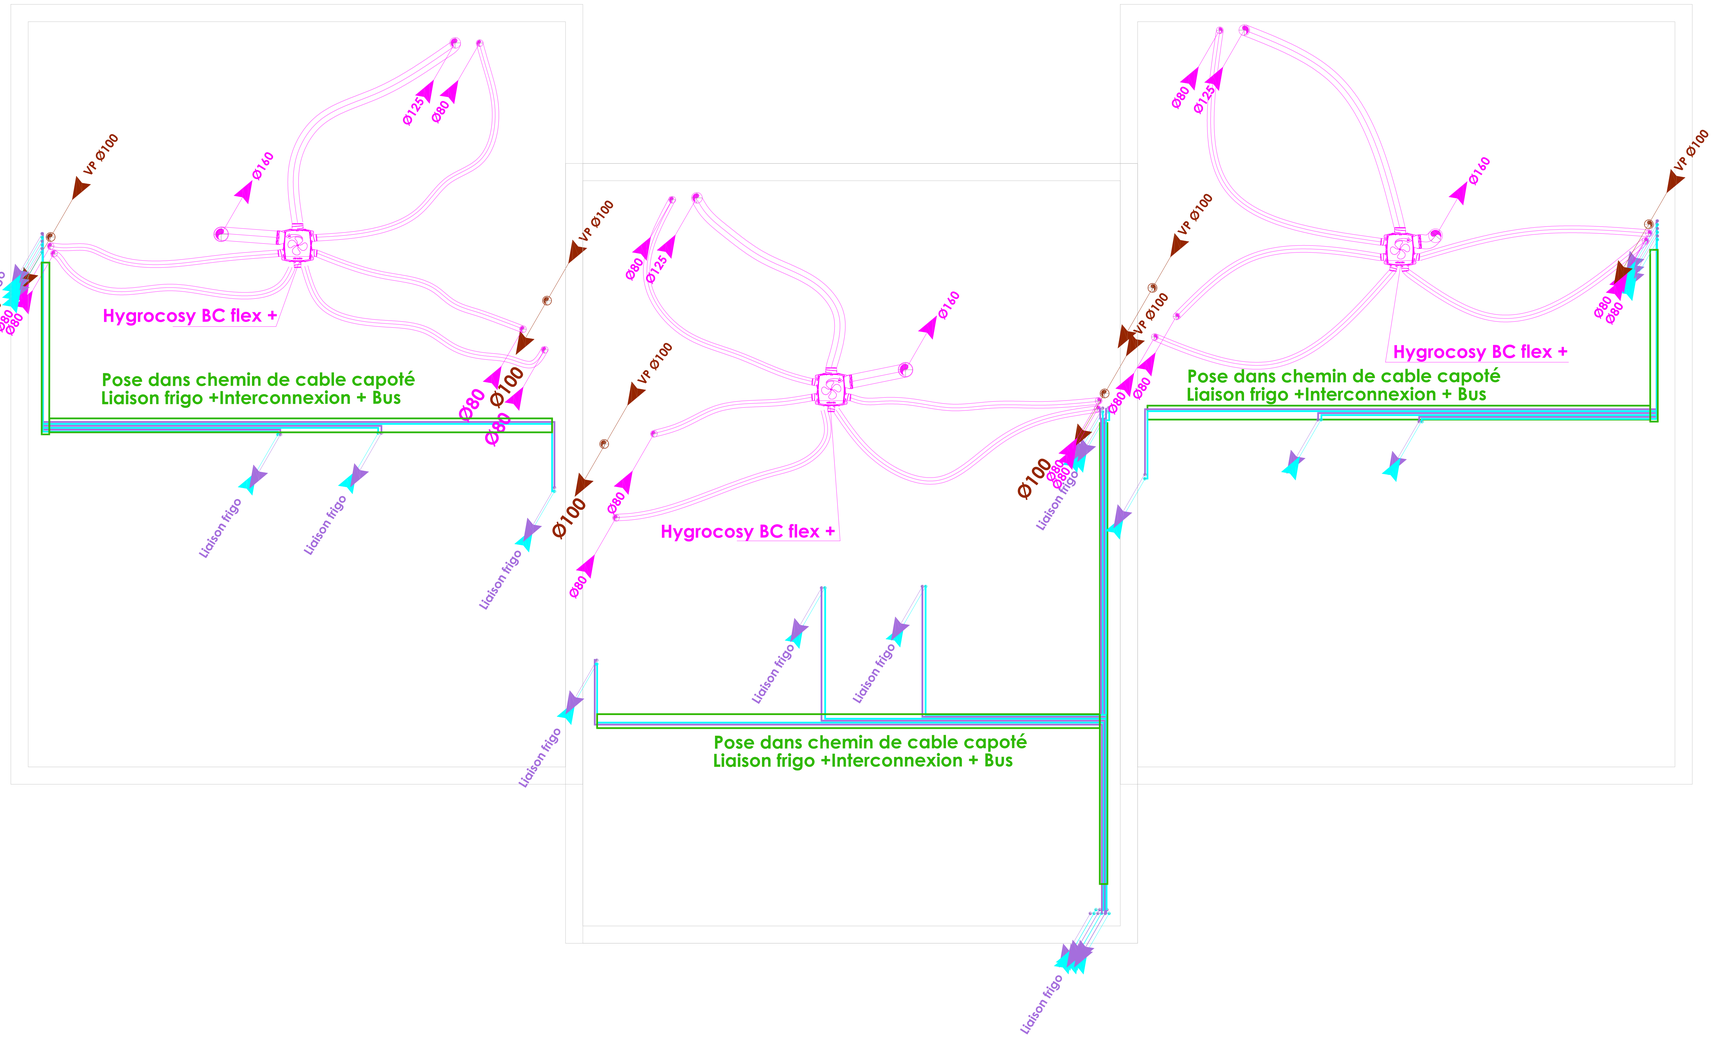

LEGENDE PLOMBERIE

- Eau froide sanitaire
- Eau chaude sanitaire
- Eaux usées
- Eaux vannes
- Condensats
- SP Siphon sec

DEBIT DE BASE DES APPAREILS

Désignation appareil	Débit EF ECS L/s	Diamètre de raccordement PER	Débit EU EV L/s	Diamètre d'évacuation (Réf. PVC)
Lavabo	0,20	10/12	0,75	40
douche	0,20	13/16	0,5	40
wc	0,12	10/12	1,5	100
Baignoire	0,33	13/16	1,2	50
Evier	0,20	13/16	0,75	40
Lave vaisselle lave linge		10/12	0,5	32
rob puisage	0,33	13/16		

LEGENDE DIMENSIONNEMENT

Vitesse réseau eau froide et eau chaude sanitaire : 1.5m/s en parties communes et sous-sol.
pente EU, EV, EUG en Rodair'2E
pente EP en Rodair 1.5%

LEGENDE CHAUFFAGE

- Unité extérieure
- Unité murale
- Liaisons frigorifiques

LEGENDE VENTILATION

- Extraction VMC
- Entrée d'air
- Bouche d'extraction

CONSTRUCTION DE 18 LOGEMENTS
RUE NEUVE GRAND TERRE
13930 AUREILLE

VILLAS 1 - 2 - 3

MAITRISE D'OUVRAGE
SCCV GRANDE TERRE
837 BIS ALLEE DE PARIS
LA SEYNE SUR MER

MAITRISE D'OEUVRE
AXXION
41 Rue Ribas
13770 VENELLES

BET FLUIDES CVC
AXIO INGENIERIE
393 Rue Ettore BUGATTI
66000 PERPIGNAN
axio.ingenierie@gmail.com

LOT PLOMBERIE,VMC & RAFRAICHISSEMENT
PLAN DES COMBLES

Ind	Date	Modifications	Dessiné par:	Vérifié par:
0	06/07/2026	Création du document	EB	LG
A			Date:	Echelle:
B			06/07/2026	1:25
C			Visa :	
D				

NIVEAU	LOT	DOSSIER	PHASE	N° DOCUMENT	INDICE
TOIT	PB CVC		DCE	403	0