villa 1 villa 2 villa 3

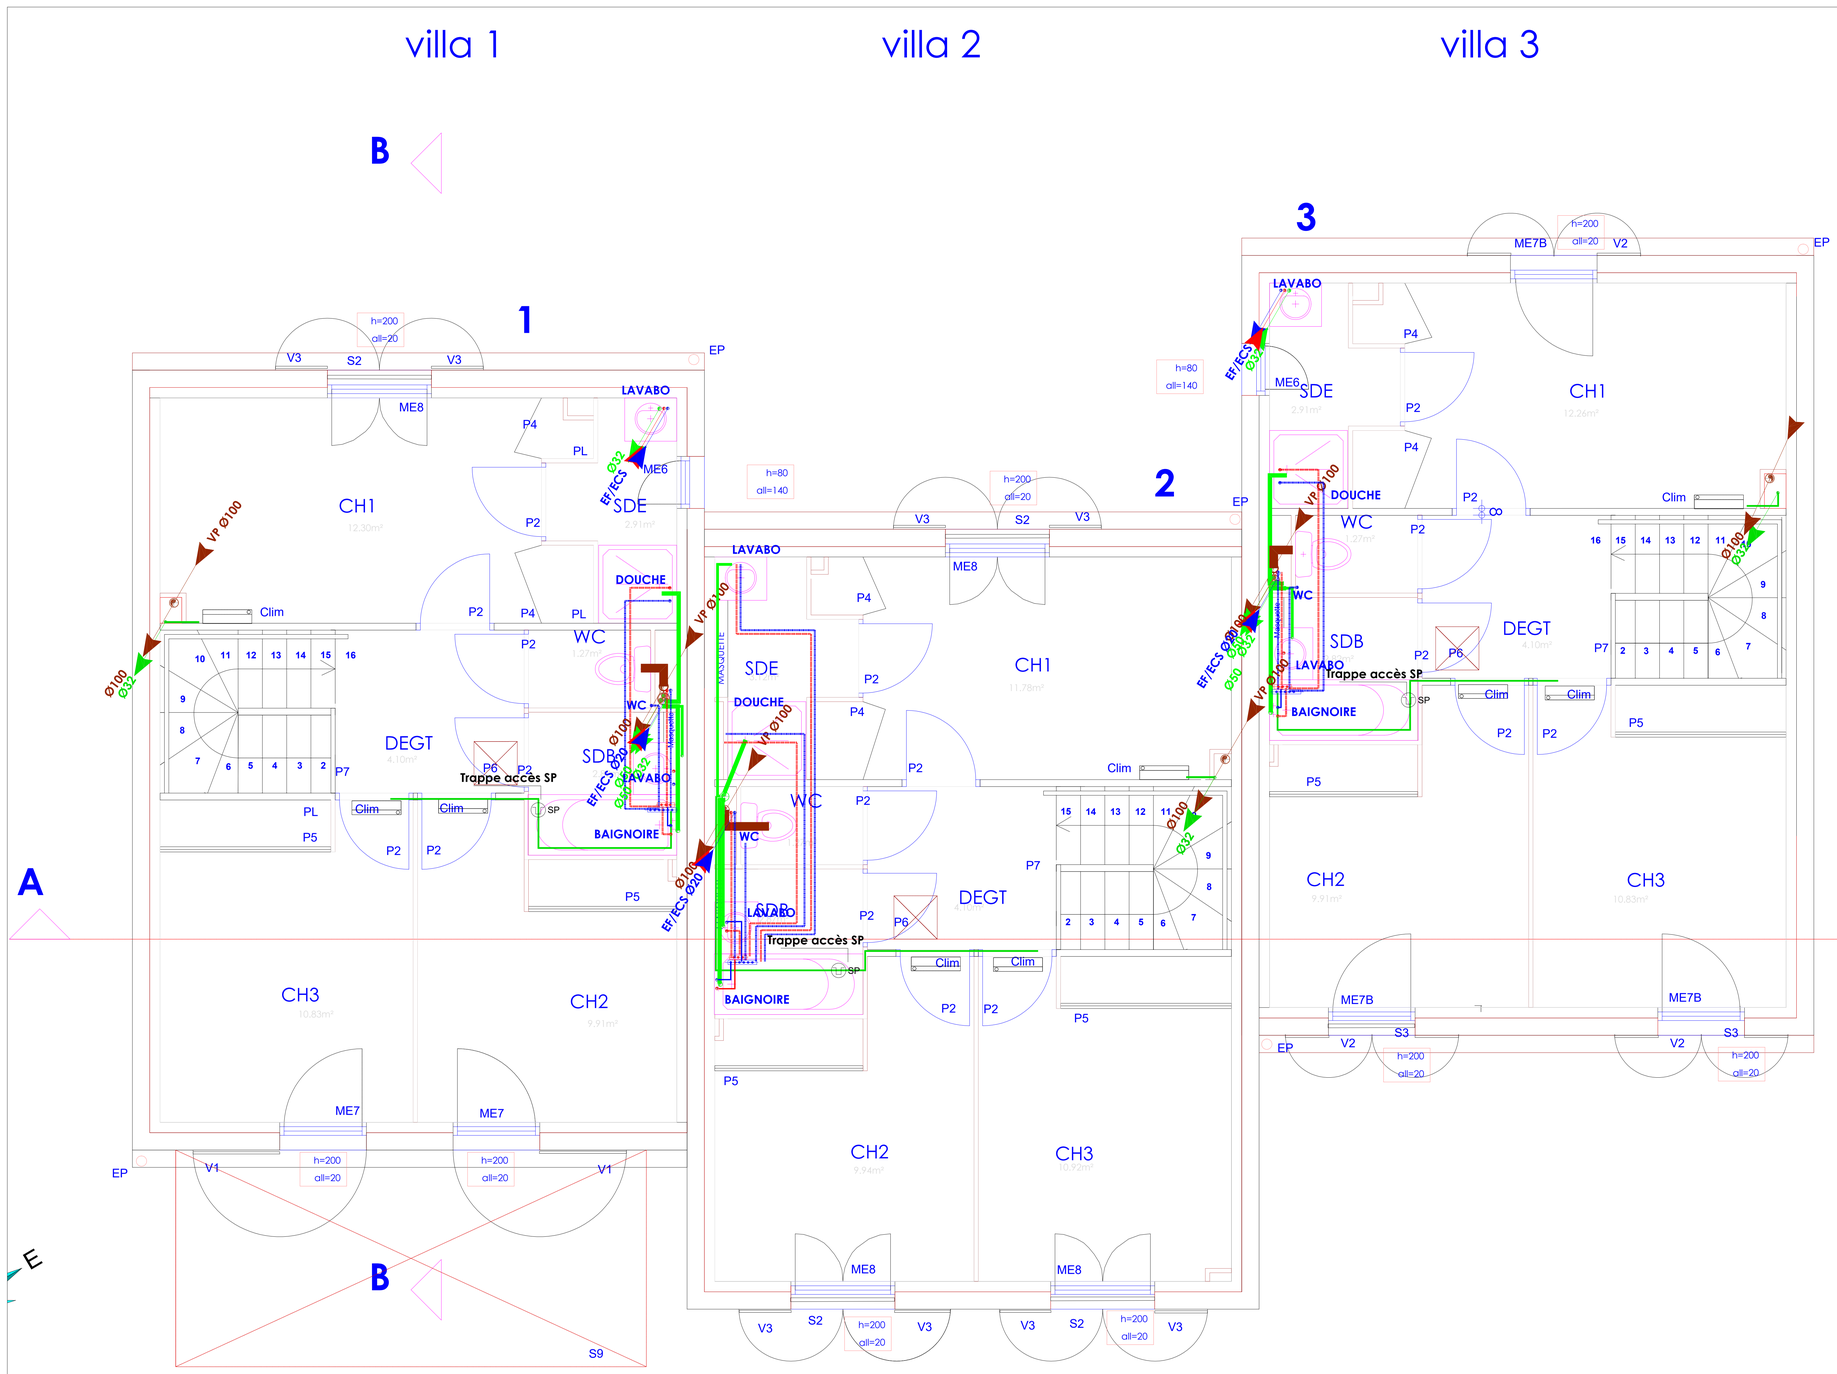

LEGENDE PLOMBERIE

- Eau froide sanitaire
- Eau chaude sanitaire
- Eaux usées
- Eaux vannes
- Condensats
- SP Siphon sec

DEBIT DE BASE DES APPAREILS

Désignation appareil	Débit EF ECS L/s	Diamètre de raccordement PER	Débit EU EV L/s	Diamètre d'évacuation (Sheet PVC)
Lavabo	0,20	10/12	0,75	40
douche	0,20	13/16	0,5	40
wc	0,12	10/12	1,5	100
Baignoire	0,33	13/16	1,2	50
Evier	0,20	13/16	0,75	40
Lave vaisselle lave linge	0,15	10/12	0,5	32
rob puisage	0,33	13/16		

LEGENDE DIMENSIONNEMENT

Vitesse réseau eau froide et eau chaude sanitaire : 1,5m/s en parties communes et sous-sol
pente EU, EV, EUC en Rodair2%
pente EP en Rodair 1,5%

CONSTRUCTION DE 18 LOGEMENTS
RUE NEUVE GRAND TERRE
13930 AUREILLE

VILLAS 1 - 2 - 3

MAITRISE D'OUVRAGE
SCCV GRANDE TERRE
837 BIS ALLEE DE PARIS
LA SEYNE SUR MER

MAITRISE D'OEUVRE
AXXION
41 Rue Ribas
13770 VENELLES

BET FLUIDES CVC
AXIO INGENIERIE
393 Rue Ettore BUGATTI
66000 PERPIGNAN
axio.ingenierie@gmail.com

LOT PLOMBERIE,VMC & RAFRAICHISSEMENT
PLAN PLOMBERIE EVACUATIONS R+1

Ind	Date	Modifications	Dessiné par:	Vérifié par:
0	06/07/2026	Création du document	EB	LG
A			Date:	Echelle:
B			06/07/2026	1:25
C			Visa :	
D				

NIVEAU	LOT	DOSSIER	PHASE	N° DOCUMENT	INDICE
R1	PB CVC		DCE	411	0