
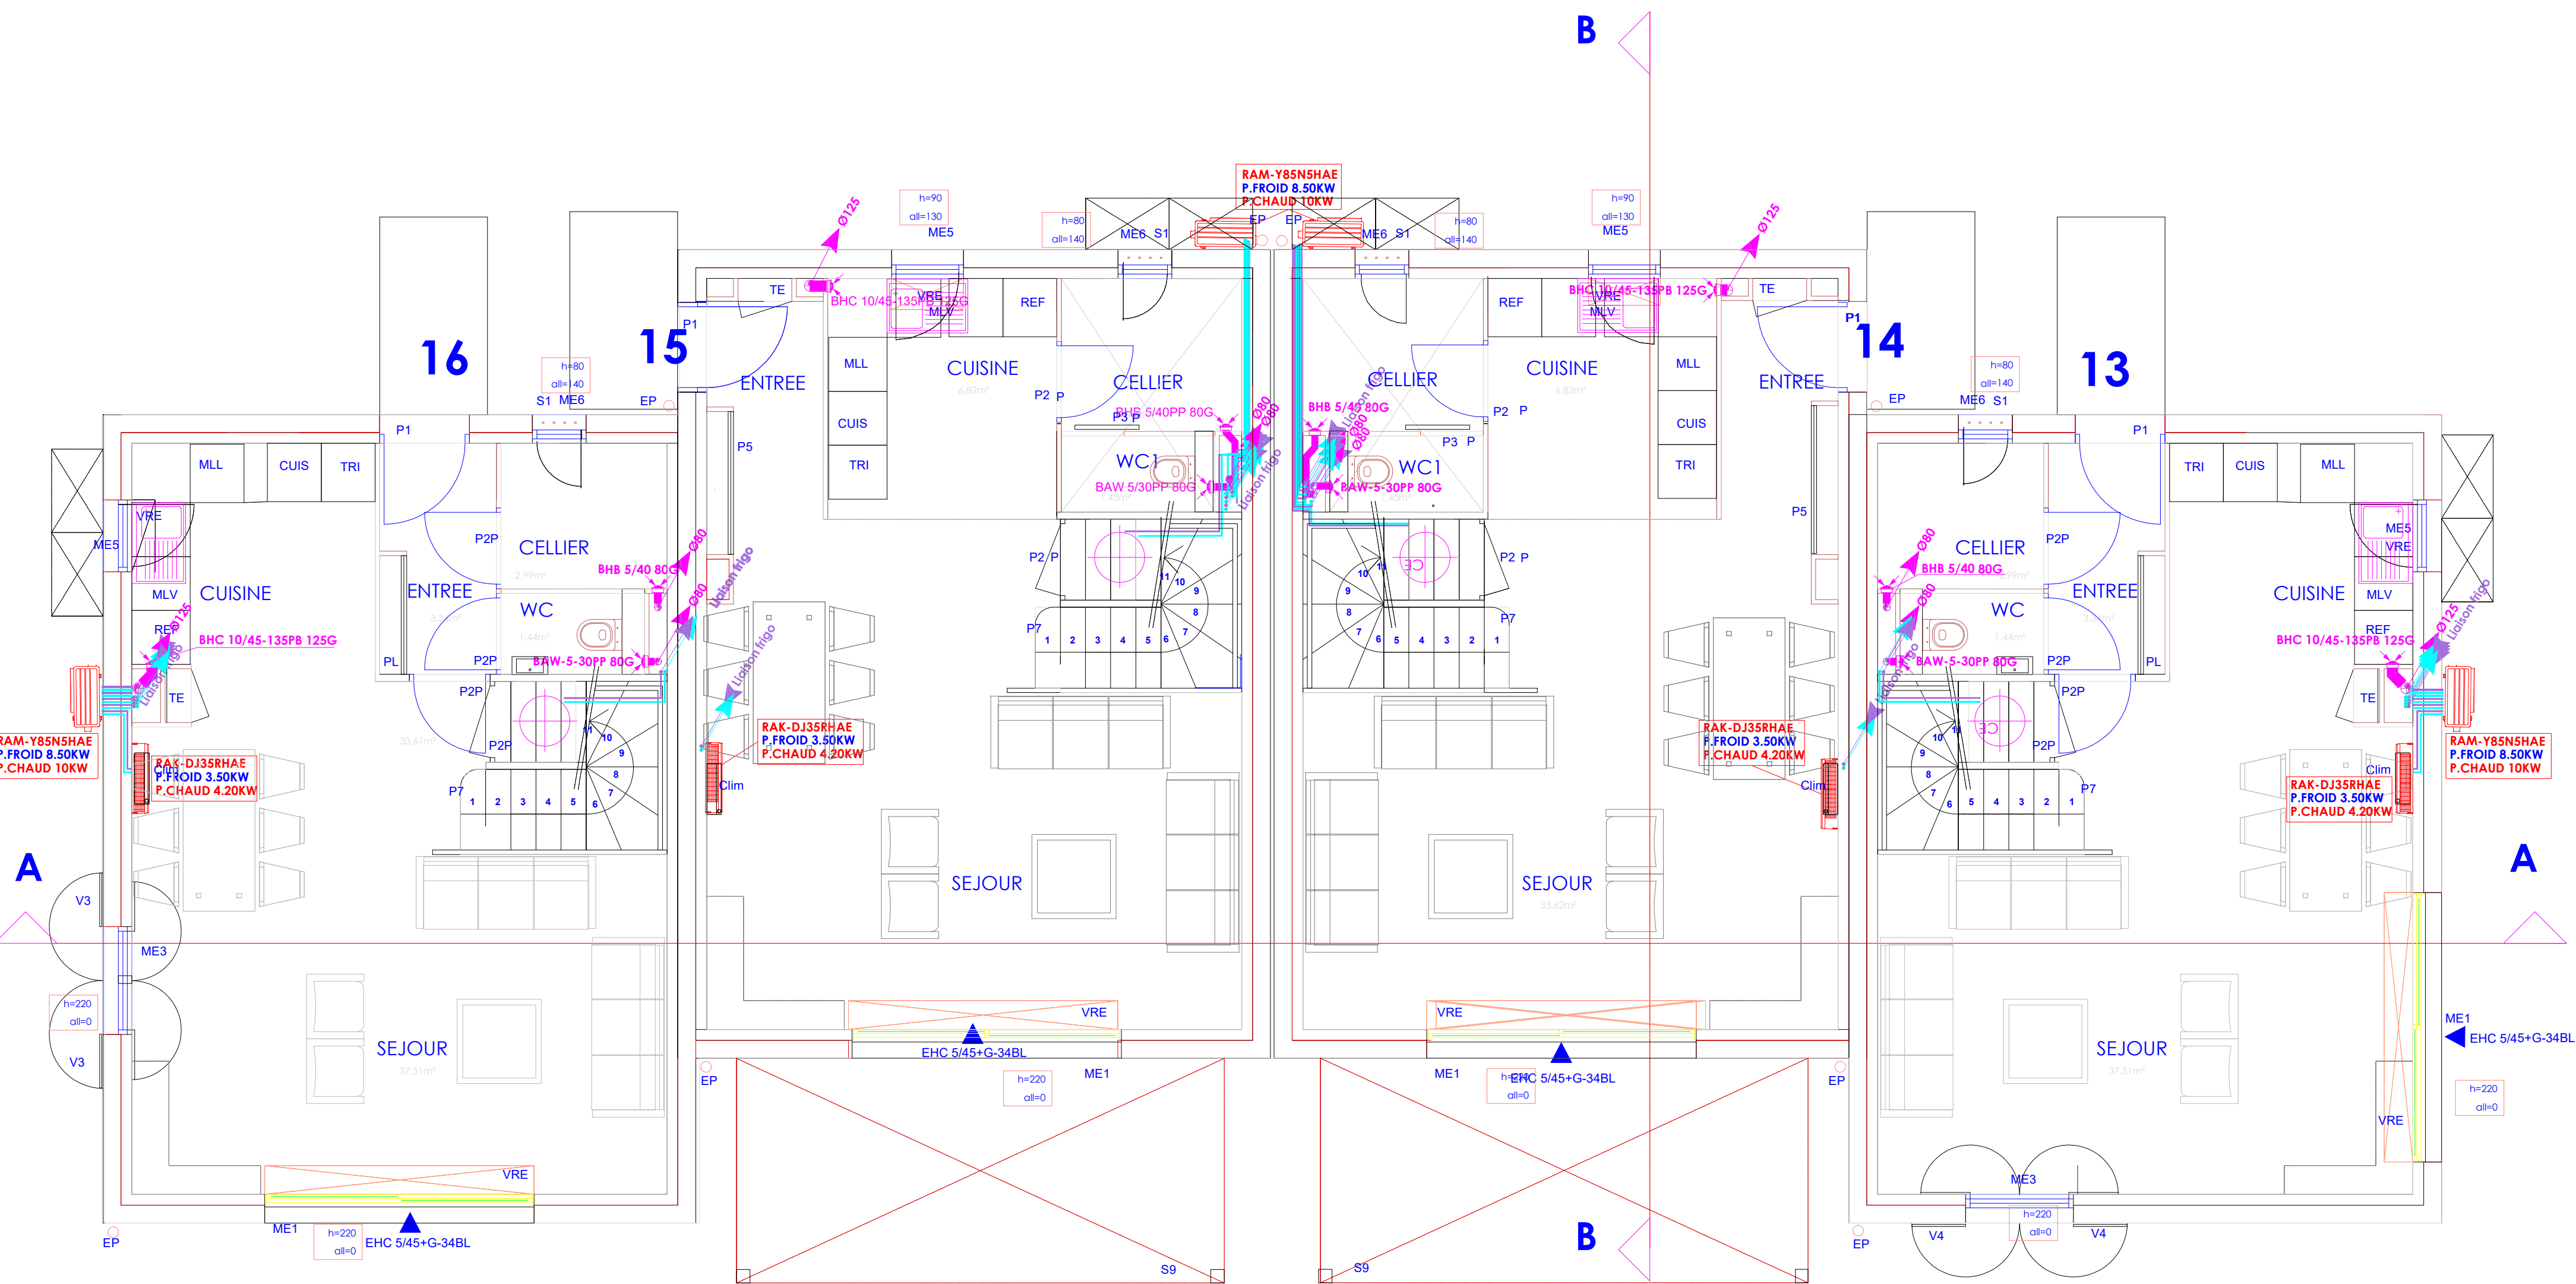
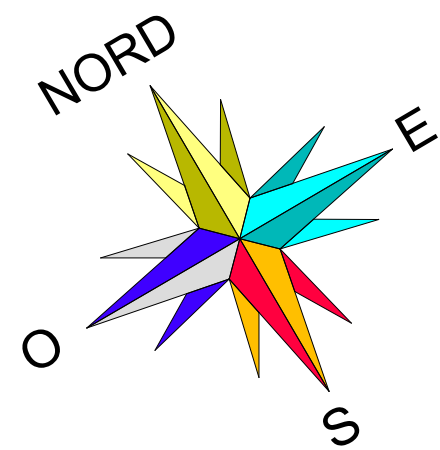


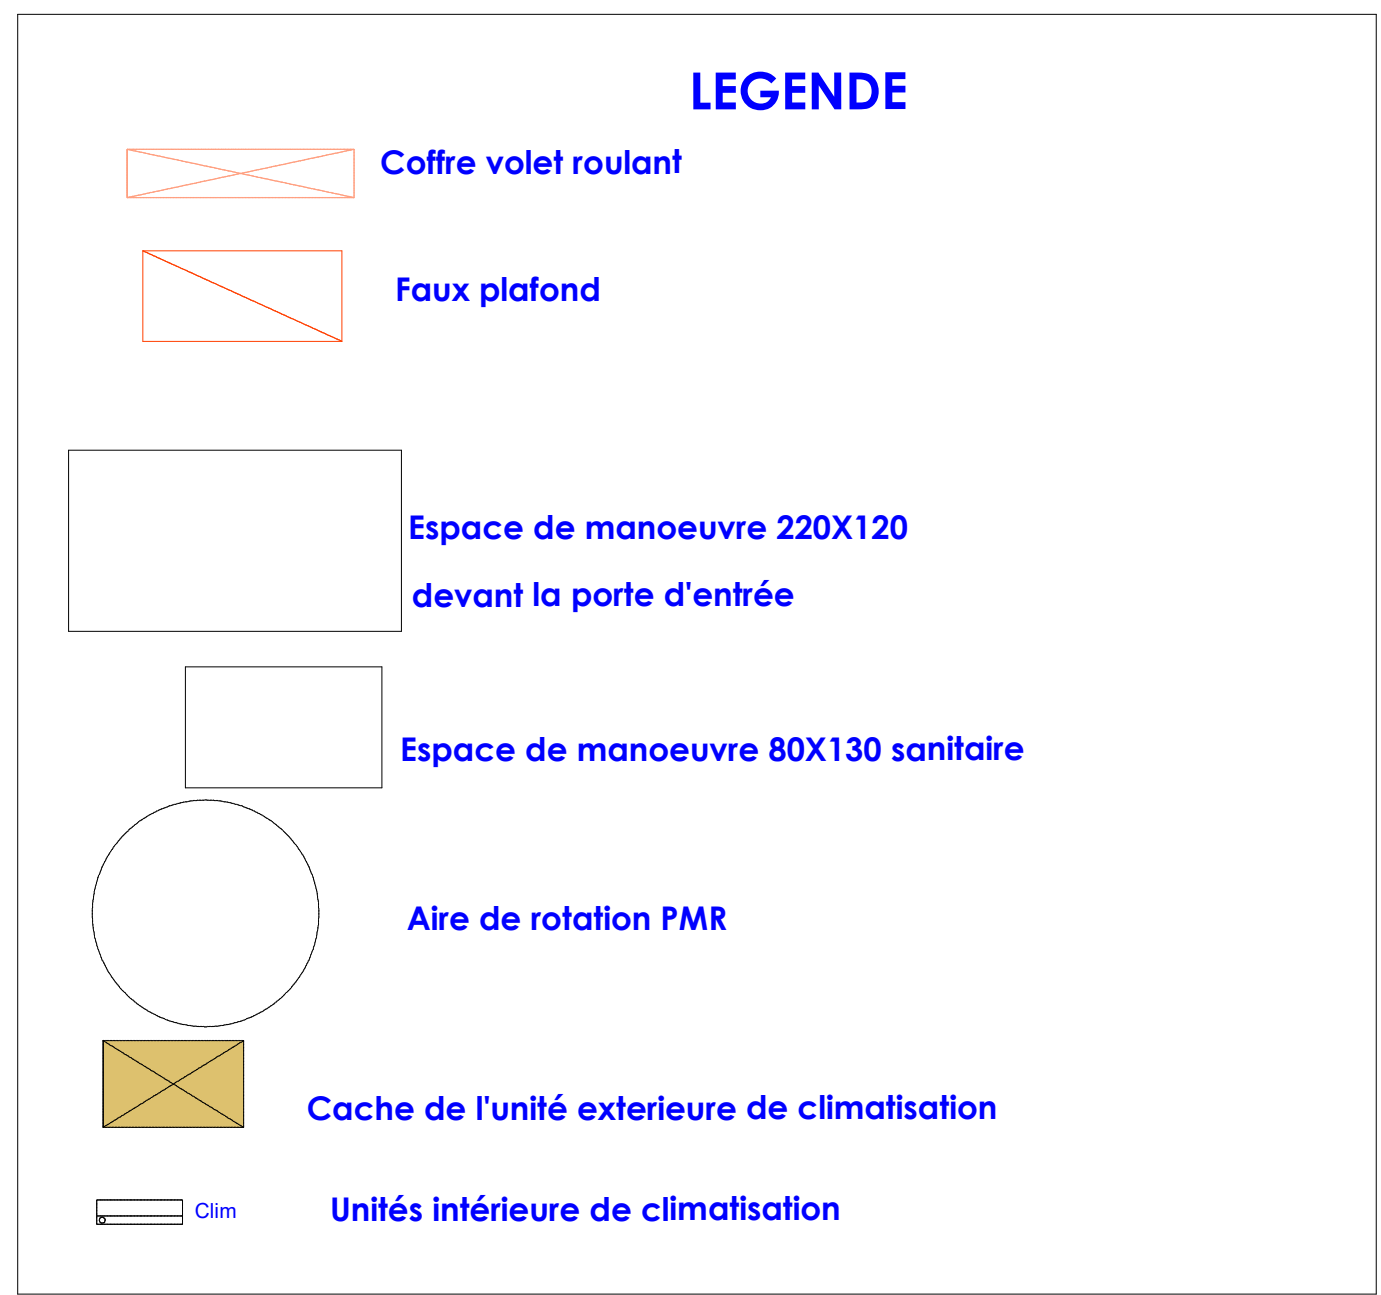

villa 16



villa 15

villa 14

villa 13

REZ DE CHAUSSEE

villa 12

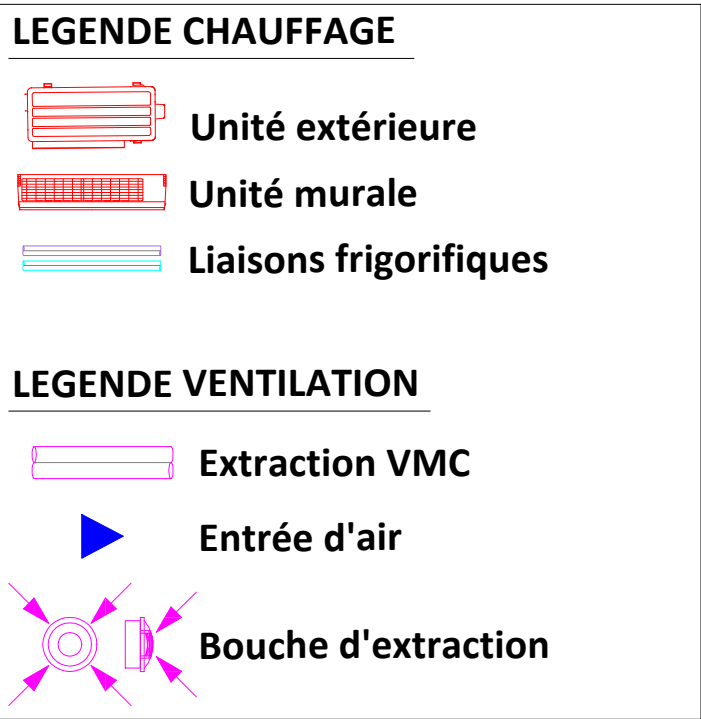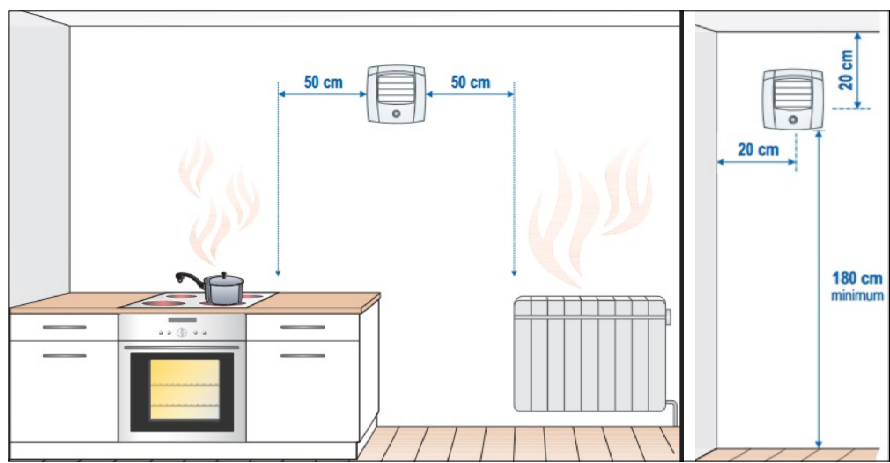

CONSTRUCTION DE 18 LOGEMENTS
RUE NEUVE GRAND TERRE
13930 AUREILLE

VILLAS 12 - 13 - 14 - 15 - 16

MAITRISE D'OUVRAGE

SCCV GRANDE TERRE
837 BIS ALLEE DE PARIS
LA SEYNE SUR MER

MAITRISE D'OEUVRE
AXXION
41 Rue Ribas
13770 VENELLES

BET FLUIDES CVC
AXIO INGENIERIE
393 Rue Ettore BUGATTI
66000 PERPIGNAN
axio.ingenierie@gmail.com



LOT PLOMBERIE, VMC & RAFFRAICHISSEMENT
PLAN CHAUFFAGE VENTILATION RDC

Ind	Date	Modifications	Dessiné par:	Vérifié par:
0	06/07/2026	Création du document	JPG	LG
A			Date:	Echelle:
B			06/07/2026	1:25
C			Visa :	
D				

NIVEAU	LOT	DOSSIER	PHASE	N° DOCUMENT	INDICE
R0	PB CVC		DCE	402	0