


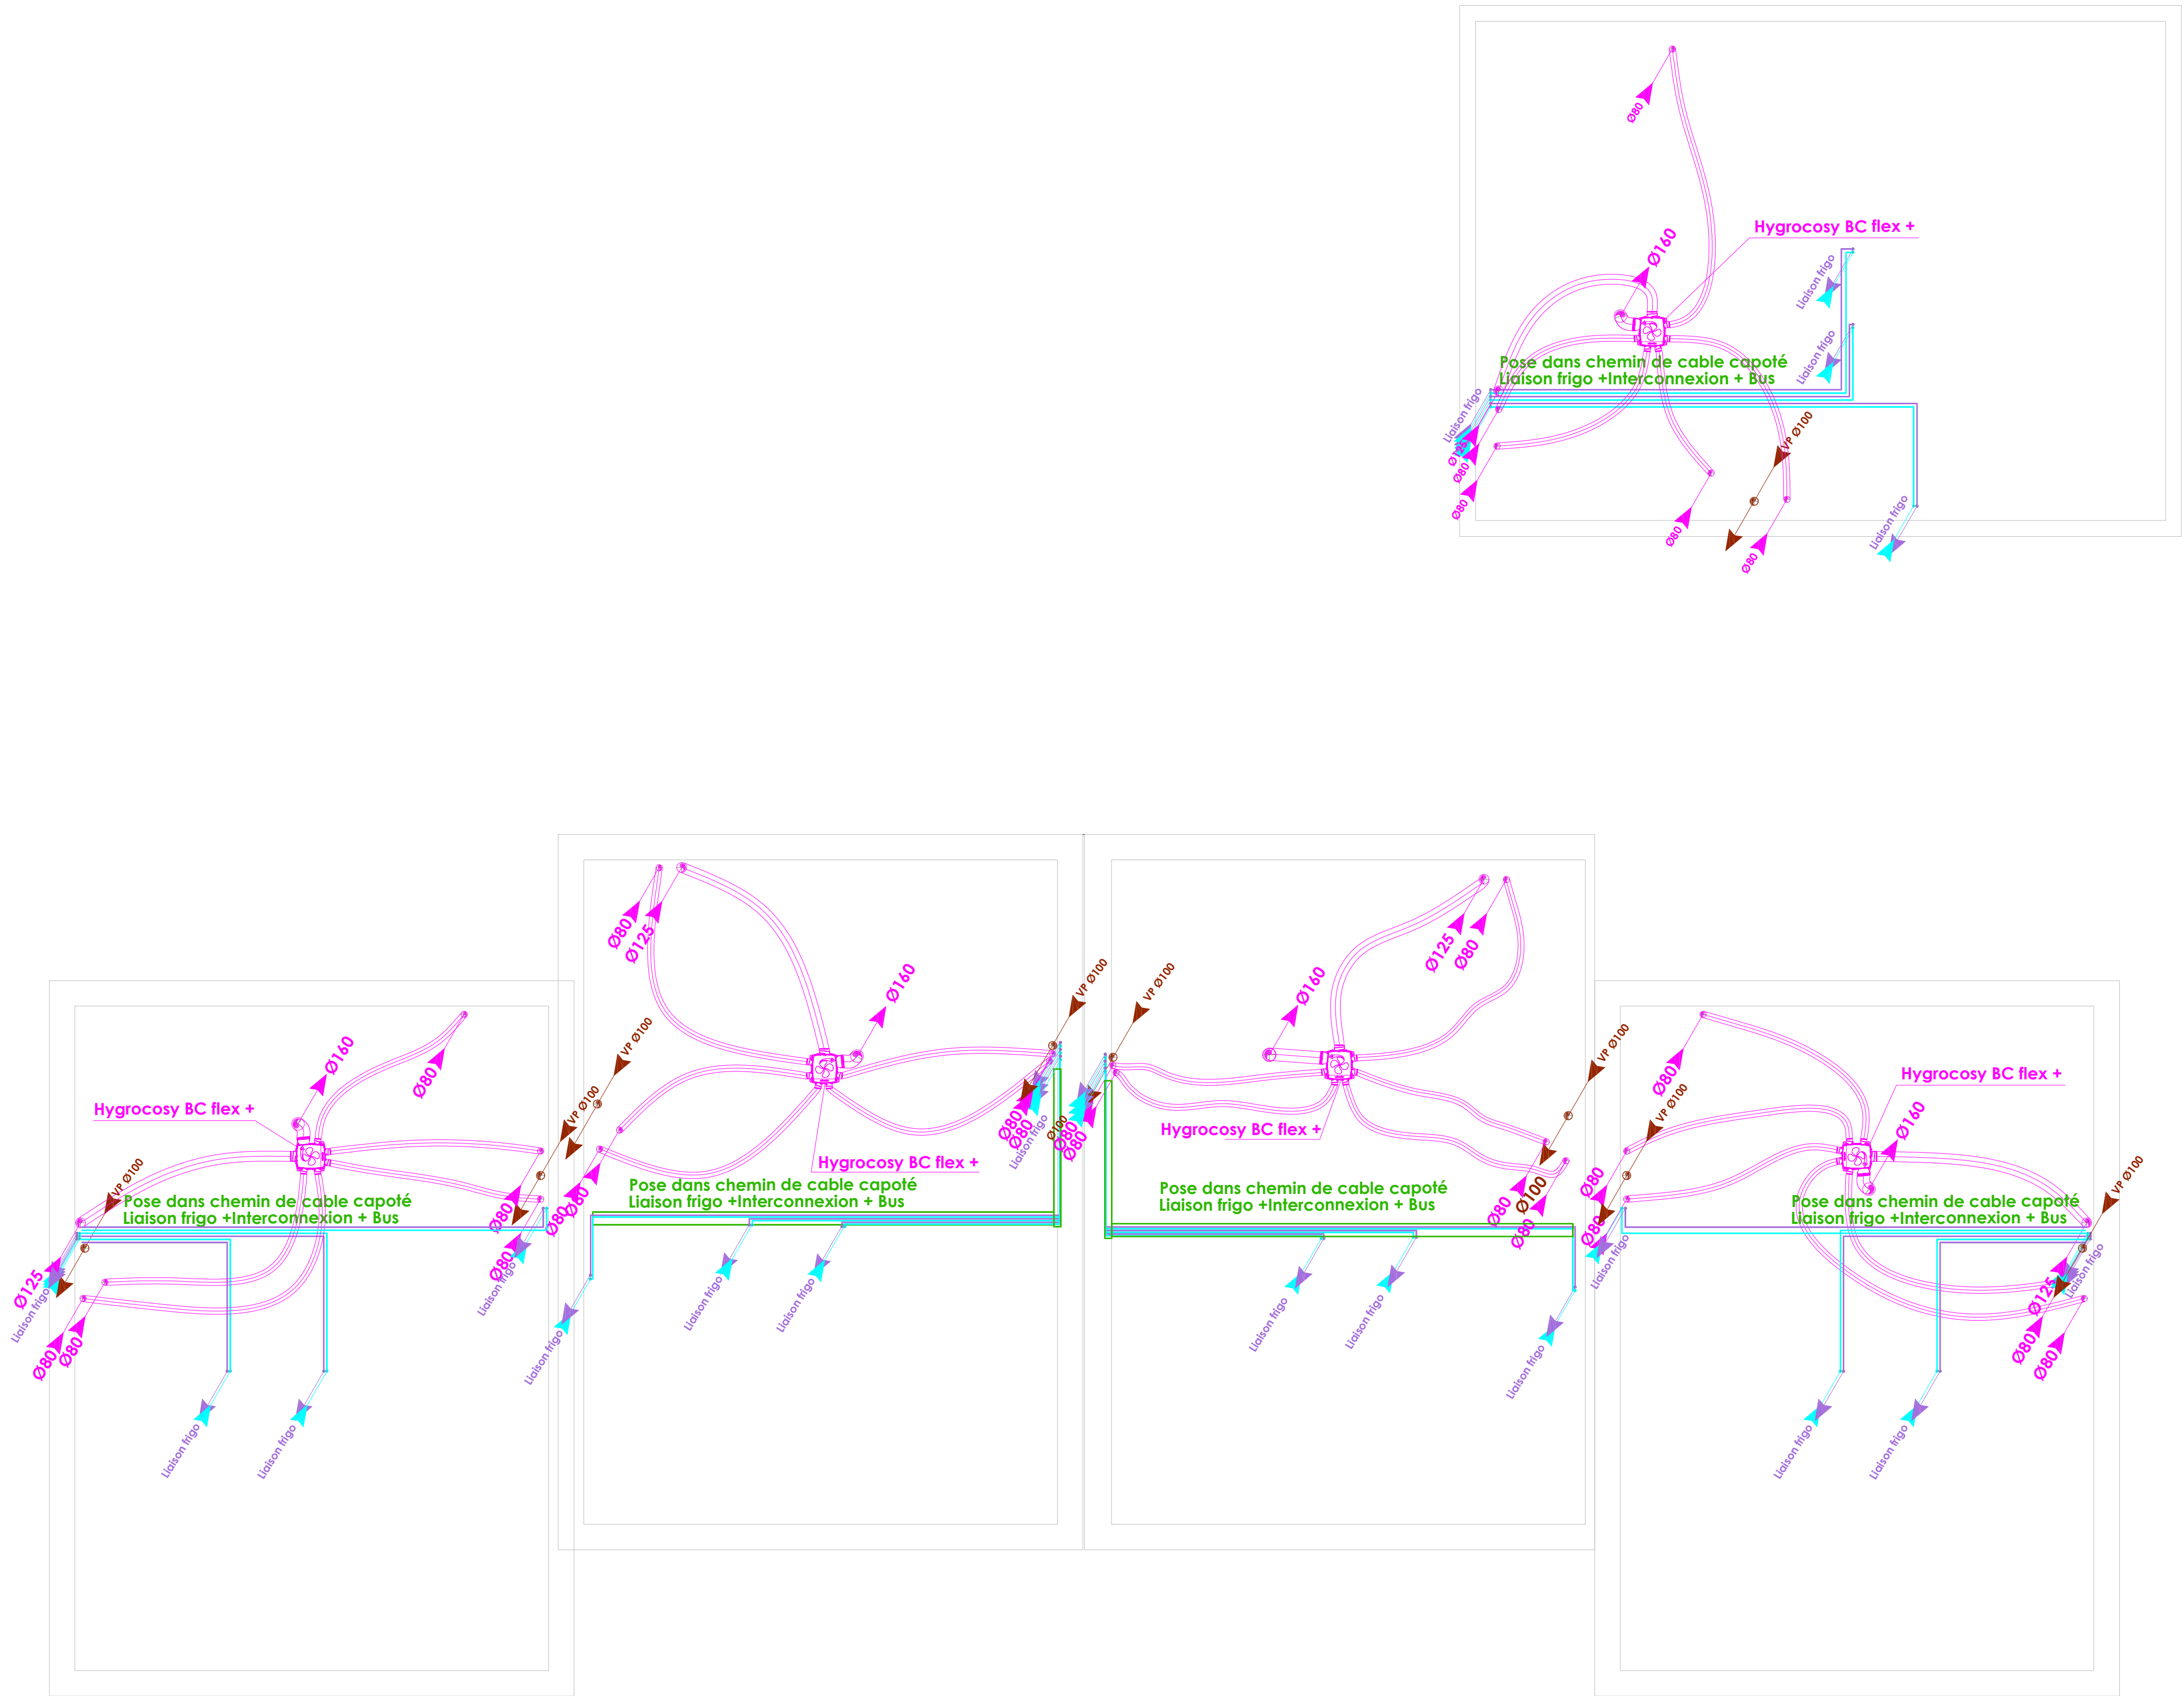

LEGENDE PLOMBERIE

Eau froide sanitaire

Eau chaude sanitaire

Eaux usées

Eaux vannes

Condensats

Siphon sec

DEBIT DE BASE DES APPAREILS				
Désignation appareil	Débit EF ECS L/s	Diamètre de raccordement PER	Débit EU EV L/s	Diamètre d'évacuation (Ext. PVC)
Lavabo	0.20	10/12	0.75	40
douche	0.20	13/16	0.5	40
wc	0.12	10/12	1.5	100
Baignoire	0.33	13/16	1.2	50
Evier	0.20	13/16	0.75	40
Lave vaisselle	0.20	10/12	0.5	32
rob puisage	0.33	13/16		

LEGENDE DIMENSIONNEMENT

Vitesse réseau eau froide et eau chaude sanitaire : 1.5m/s en portées communes et sous-sol.
pente EU, EV, EUG en Radier2%
pente EP en Radier 1.5%

LEGENDE CHAUFFAGE

Unité extérieure

Unité murale

Liaisons frigorifiques

LEGENDE VENTILATION

Extraction VMC

Entrée d'air

Bouche d'extraction

CONSTRUCTION DE 18 LOGEMENTS
RUE NEUVE GRAND TERRE
13930 AUREILLE

VILLAS 12 - 13 - 14 - 15 - 16

MAITRISE D'OUVRAGE

SCCV GRANDE TERRE
837 BIS ALLEE DE PARIS
LA SEYNE SUR MER

MAITRISE D'OEUVRE
AXXION
41 Rue Ribas
13770 VENELLES

BET FLUIDES CVC
AXIO INGENIERIE
393 Rue Ettore BUGATTI
66000 PERPIGNAN
axio.ingenierie@gmail.com

LOT PLOMBERIE,VMC & RAFFRAICHISSEMENT
PLAN DES COMBLES

Ind	Date	Modifications	Dessiné par:	Vérifié par:
0	06/07/2026	Création du document	JPG	LG
A			Date:	Echelle:
B			06/07/2026	1:25
C			Visa :	
D				

NIVEAU	LOT	DOSSIER	PHASE	N° DOCUMENT	INDICE
TOIT	PB CVC		DCE	403	0