


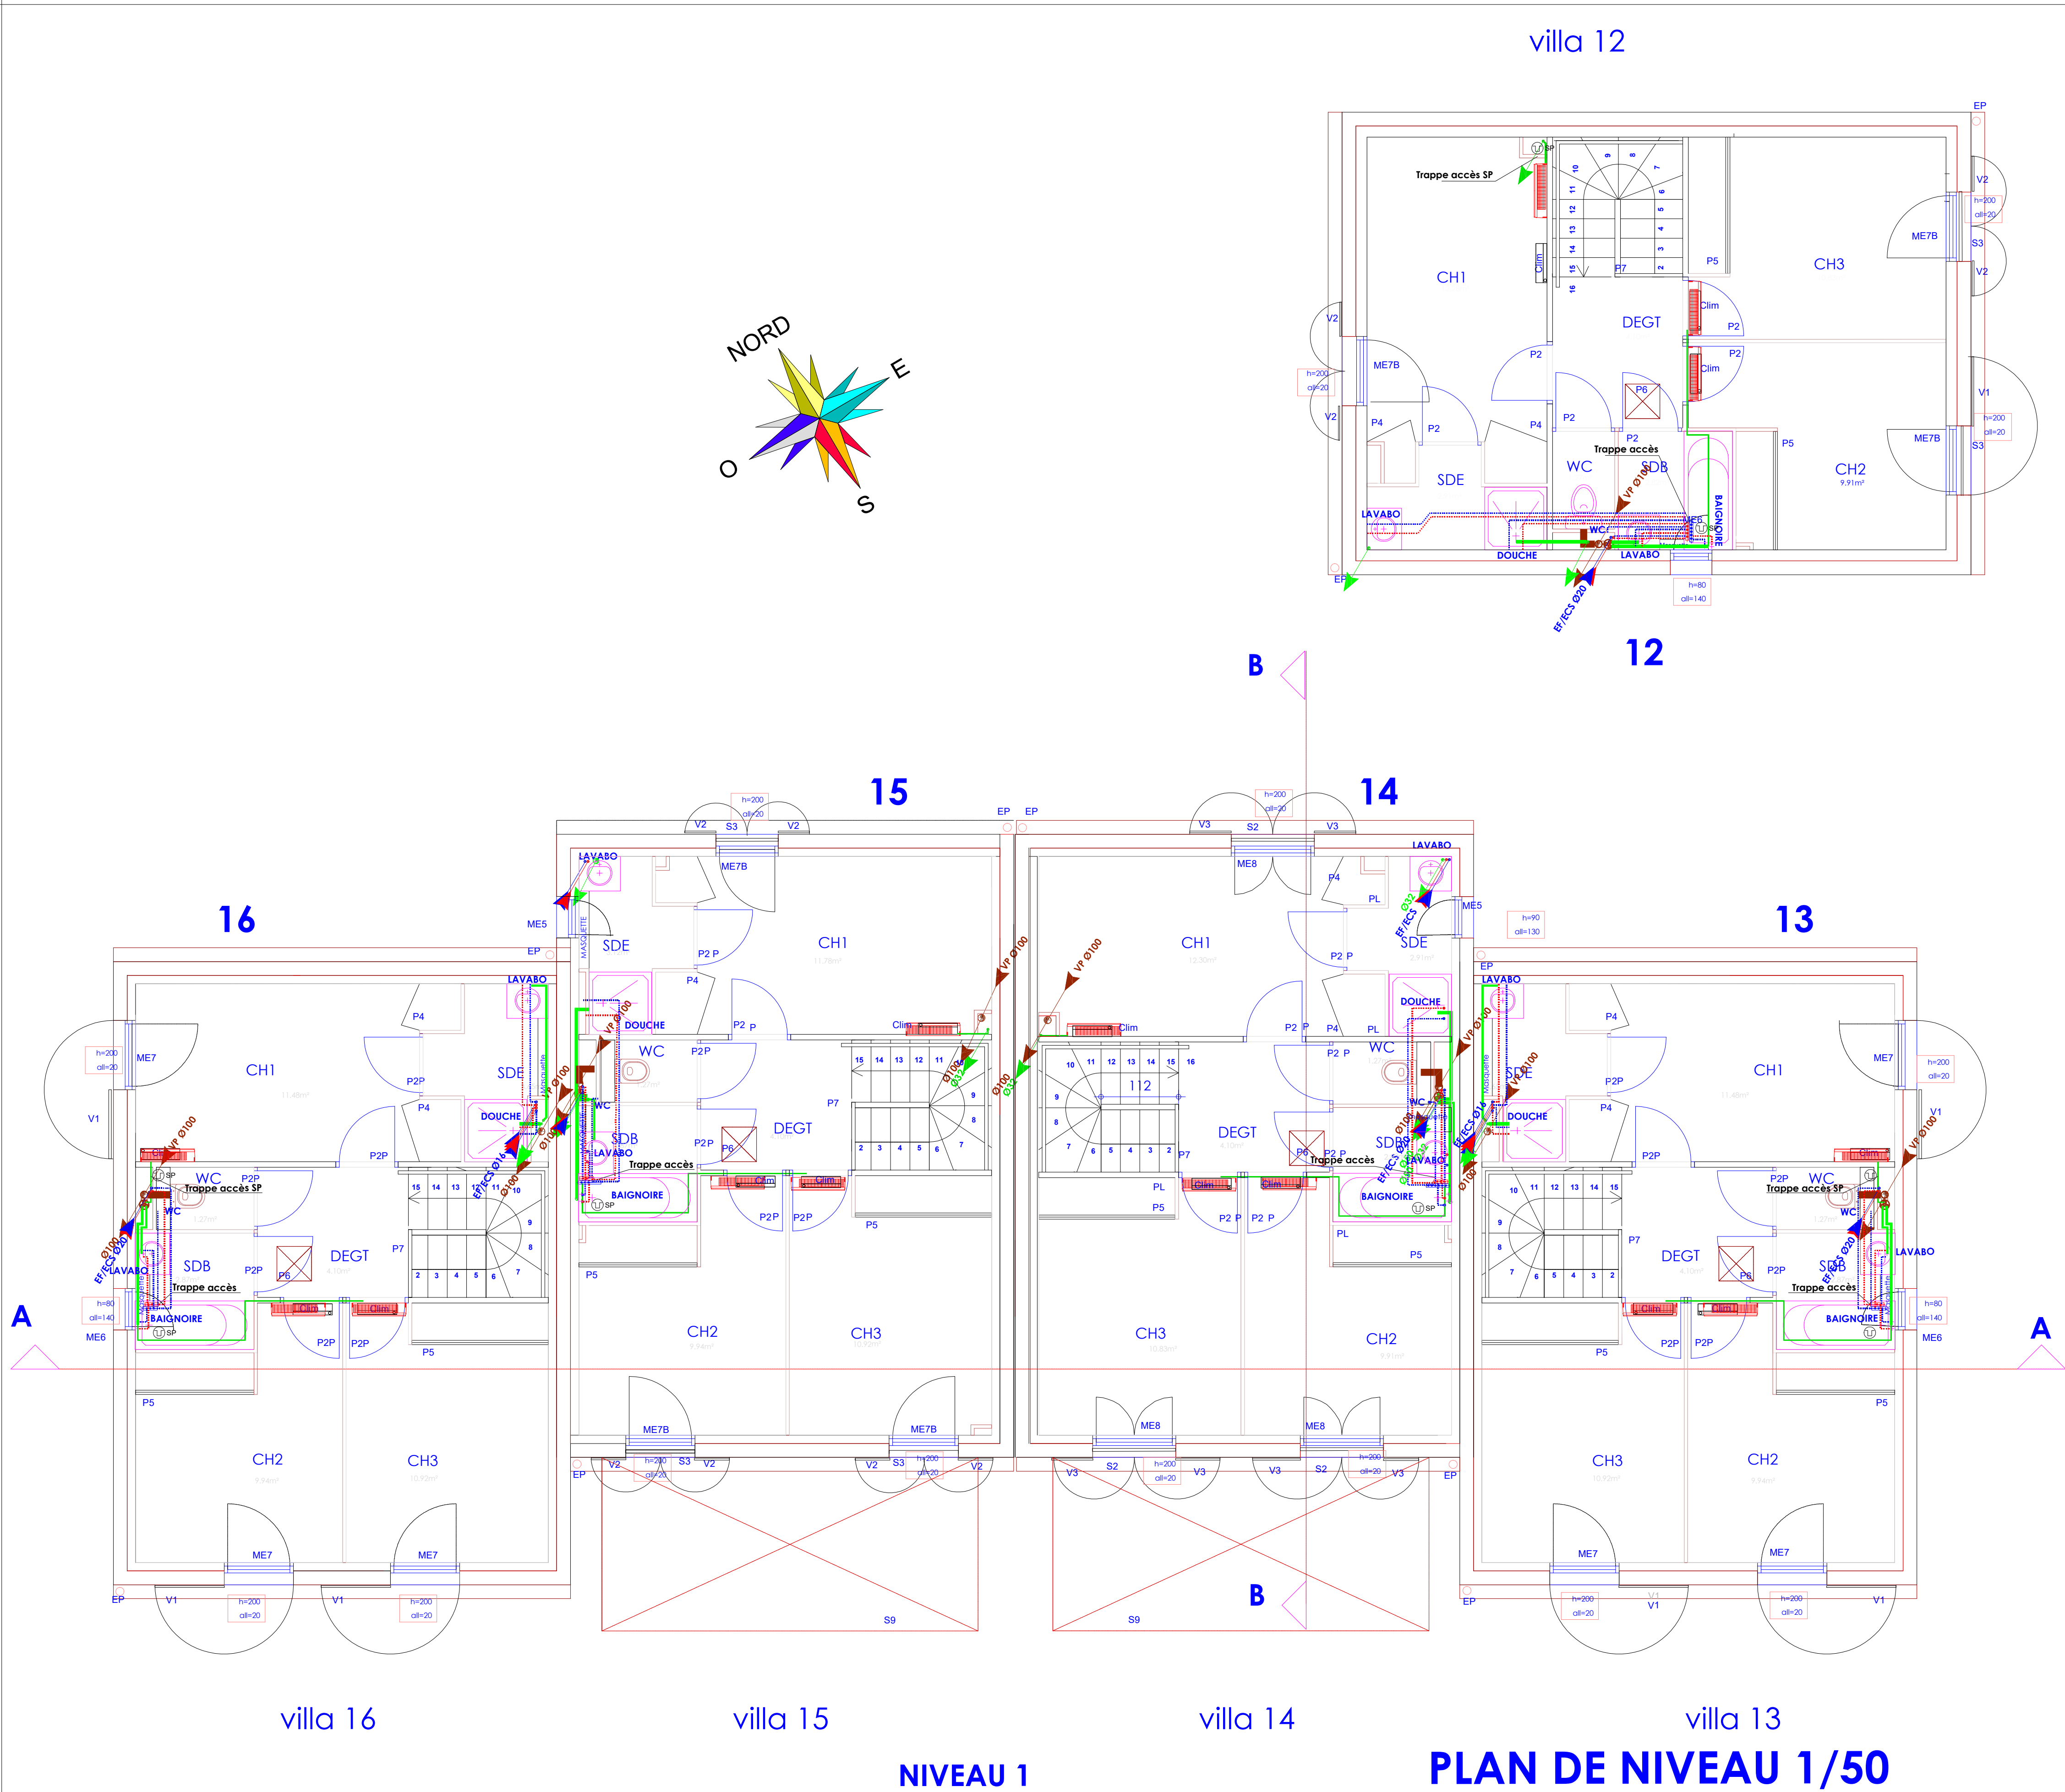

CONSTRUCTION DE 18 LOGEMENTS
RUE NEUVE GRAND TERRE
13930 AUREILLE

VILLAS 12 - 13 - 14 - 15 - 16

MAITRISE D'OUVRAGE

SCCV GRANDE TERRE
837 BIS ALLEE DE PARIS
LA SEYNE SUR MER

MAITRISE D'OEUVRE

AXXION
41 Rue Ribas
13770 VENELLES

BET FLUIDES CVC

AXIO INGENIERIE
393 Rue Ettore BUGATTI
66000 PERPIGNAN
axio.ingenierie@gmail.com

LOT PLOMBERIE,VMC & RAFFRAICHISSEMENT

PLAN PLOMBERIE EVACUATIONS R+1

Ind	Date	Modifications	Dessiné par:	Vérifié par:
0	06/07/2026	Création du document	JPG	LG
A			Date:	Echelle:
B			06/07/2026	1:25
C			Visa :	
D				

NIVEAU	LOT	DOSSIER	PHASE	N° DOCUMENT	INDICE
R1	PB CVC		DCE	411	0