


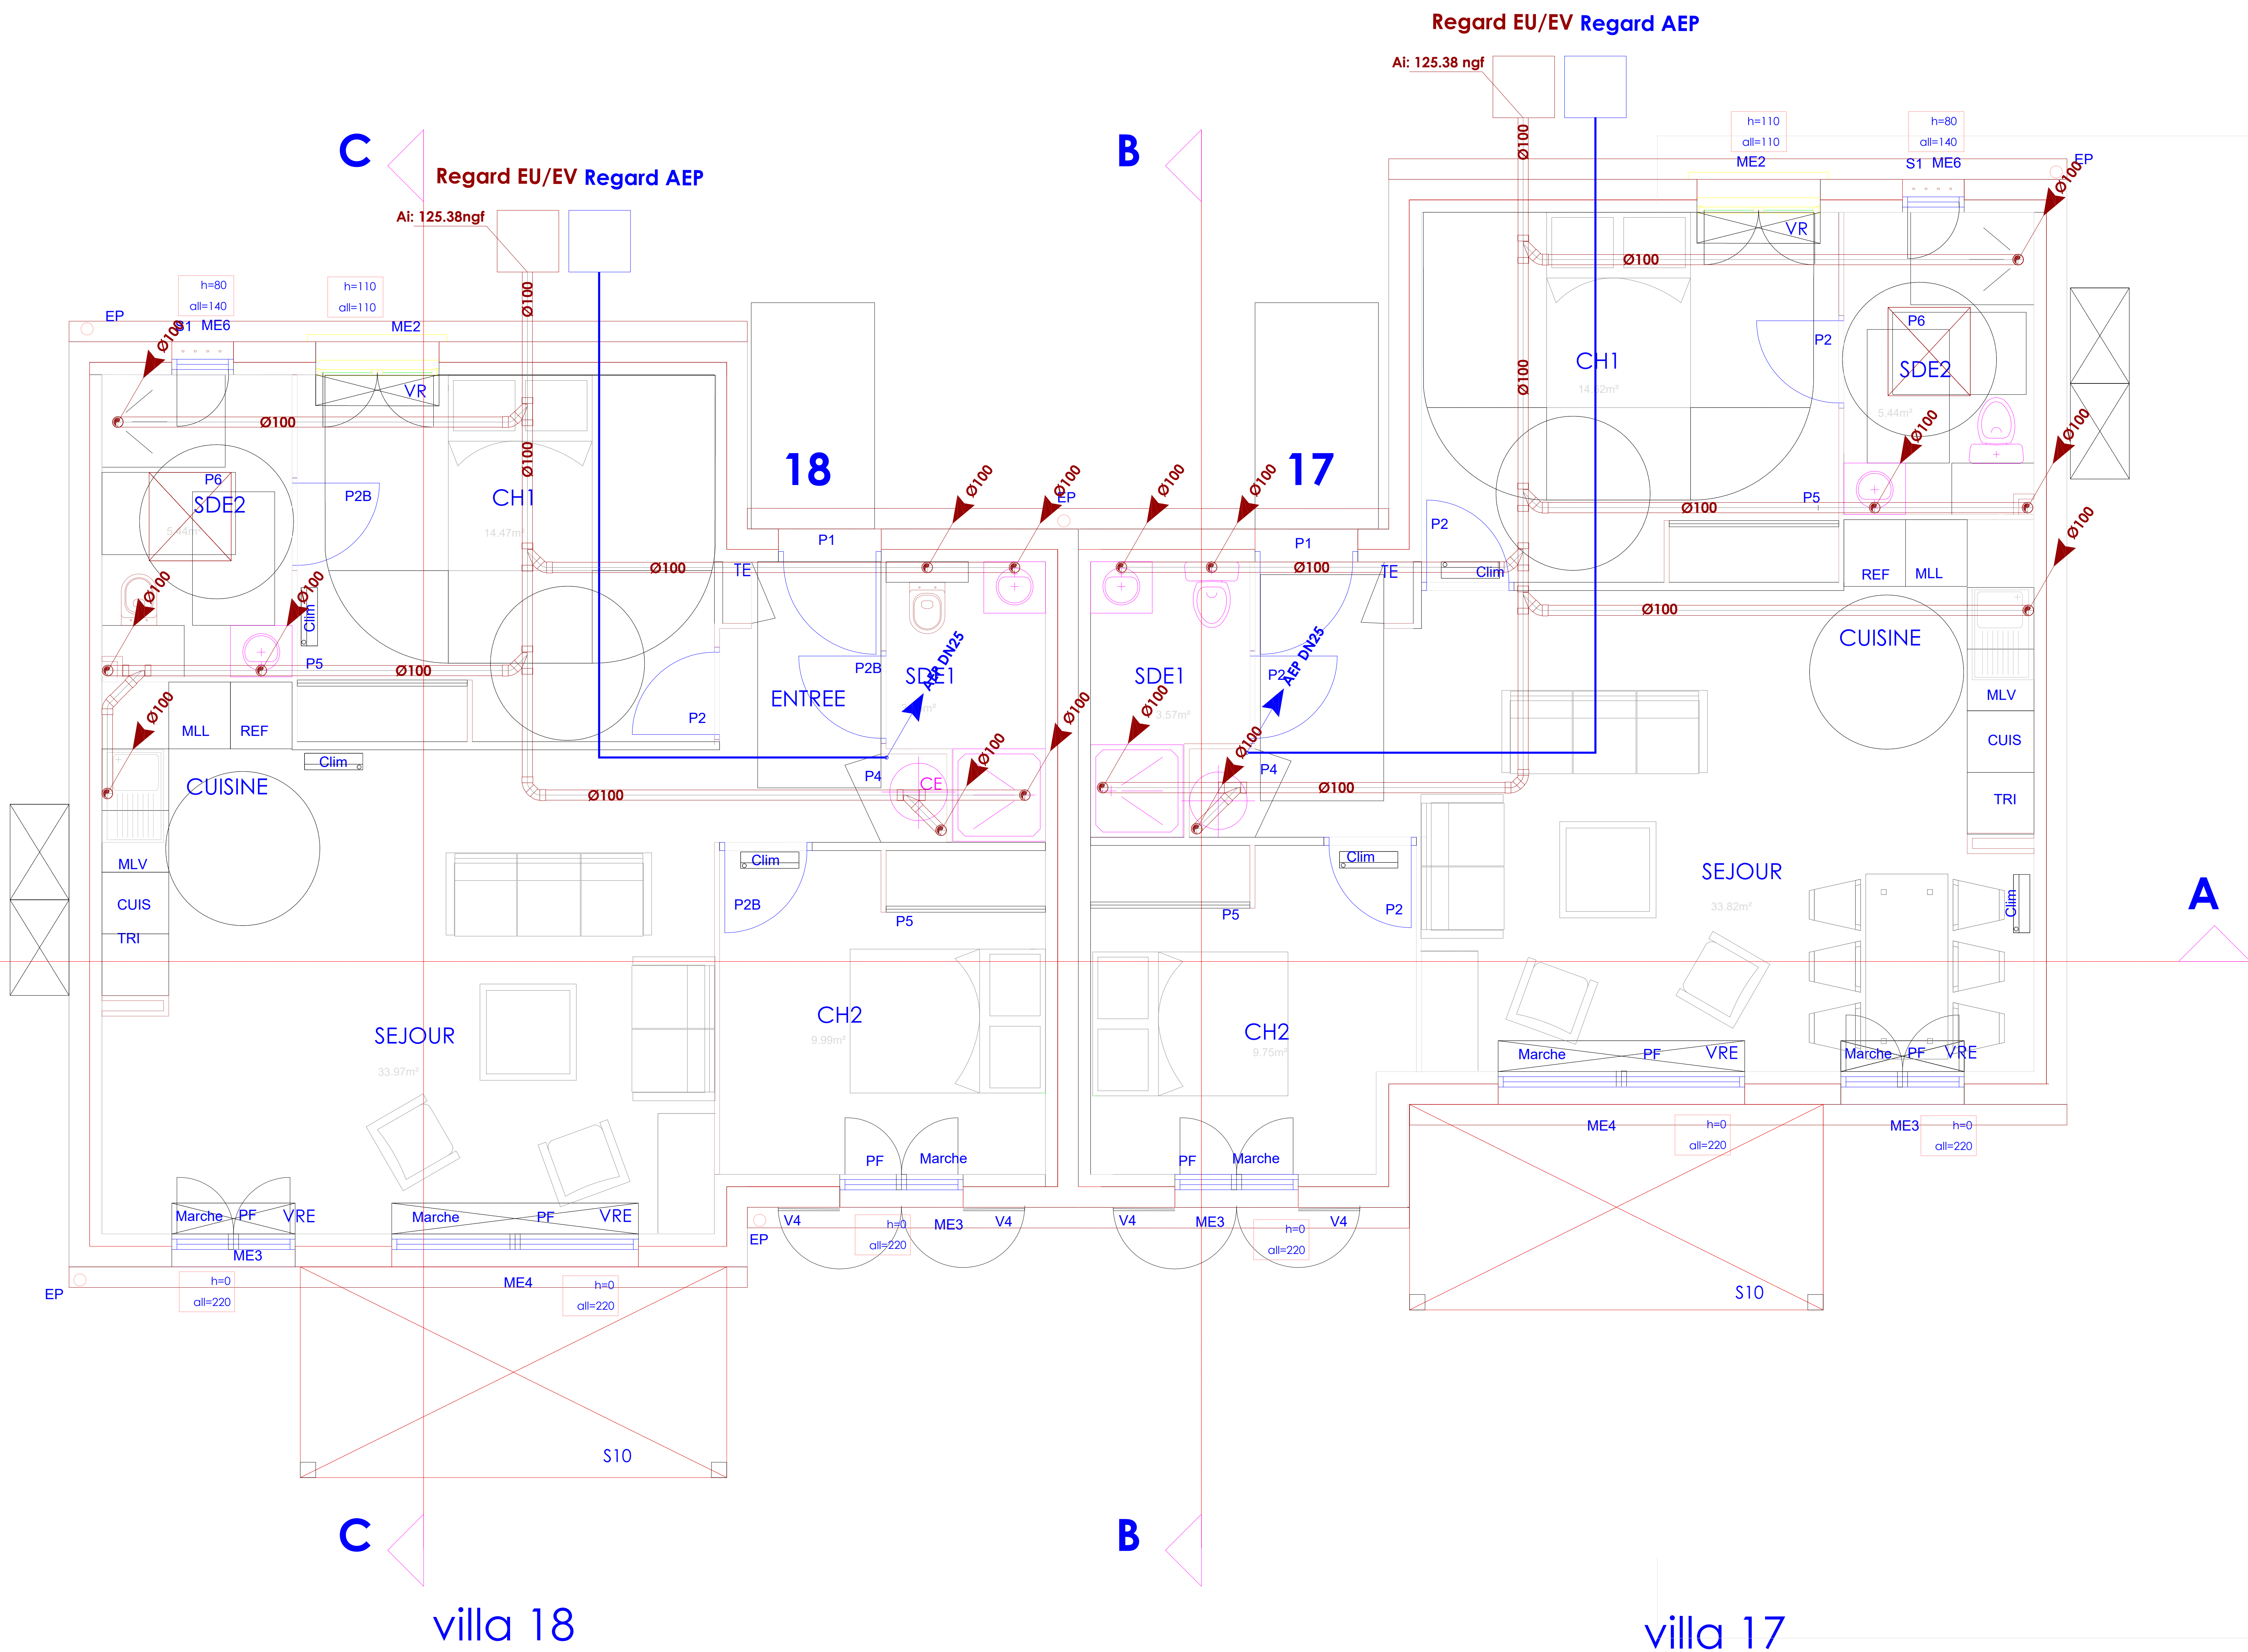

DEBIT DE BASE DES APPAREILS				
Designation	Debit EF ECS	Debit de	Debit EU EV	Quantite
ajusté	L/s	compteur PPR	L/s	Plancher (Bât. PPS)
Lavabo	0.20	10/12	0.75	40
douche	0.20	13/16	0.5	40
WC	0.13	10/12	1.5	100
Boisserie	0.33	13/16	1.2	50
Evier	0.20	13/16	0.75	40
Line vaisselle lave linge	10/12	0.5	30	
rob. puitage	0.33	13/16	1.5	100

LEGENDE DIMENSIONNEMENT				
Vitesse réseau eau froide et eau chaude sanitaire : 1.5m/s en parties souterraines et sous-sol				
pente EU, DV, EV, en Bâti 2%				
pente EP en Bâti 1.5%				

CONSTRUCTION DE 18 LOGEMENTS
RUE NEUVE GRAND TERRE
13930 AUREILLE

VILLAS 17 - 18

MAITRISE D'OUVRAGE

SCV GRANDE TERRE
837 BIS ALLEE DE PARIS
LA SEYNE SUR MER

MAITRISE D'OEUVRE

AXXION
41 Rue Ribas
13770 VENELLES

BET FLUIDES CVC

AXIO INGENIERIE
393 Rue Etienne BUGATTI
66000 PERPIGNAN
axio.ingenierie@gmail.com

LOT PLOMBERIE,VMC & RAFFRAICHISSEMENT

PLAN VIDE SANITAIRE

Ind	Date	Modifications	Dessiné par:	Vérifié par:
0	07/07/2026	Création du document	EB	LG
A			Date:	Echelle:
B			07/07/2026	1:25
C			Visé:	
D				

NIVEAU	LOT	DOSSIER	PHASE	N° DOCUMENT	INDICE
VS	PB CVC		DCE	400	0