


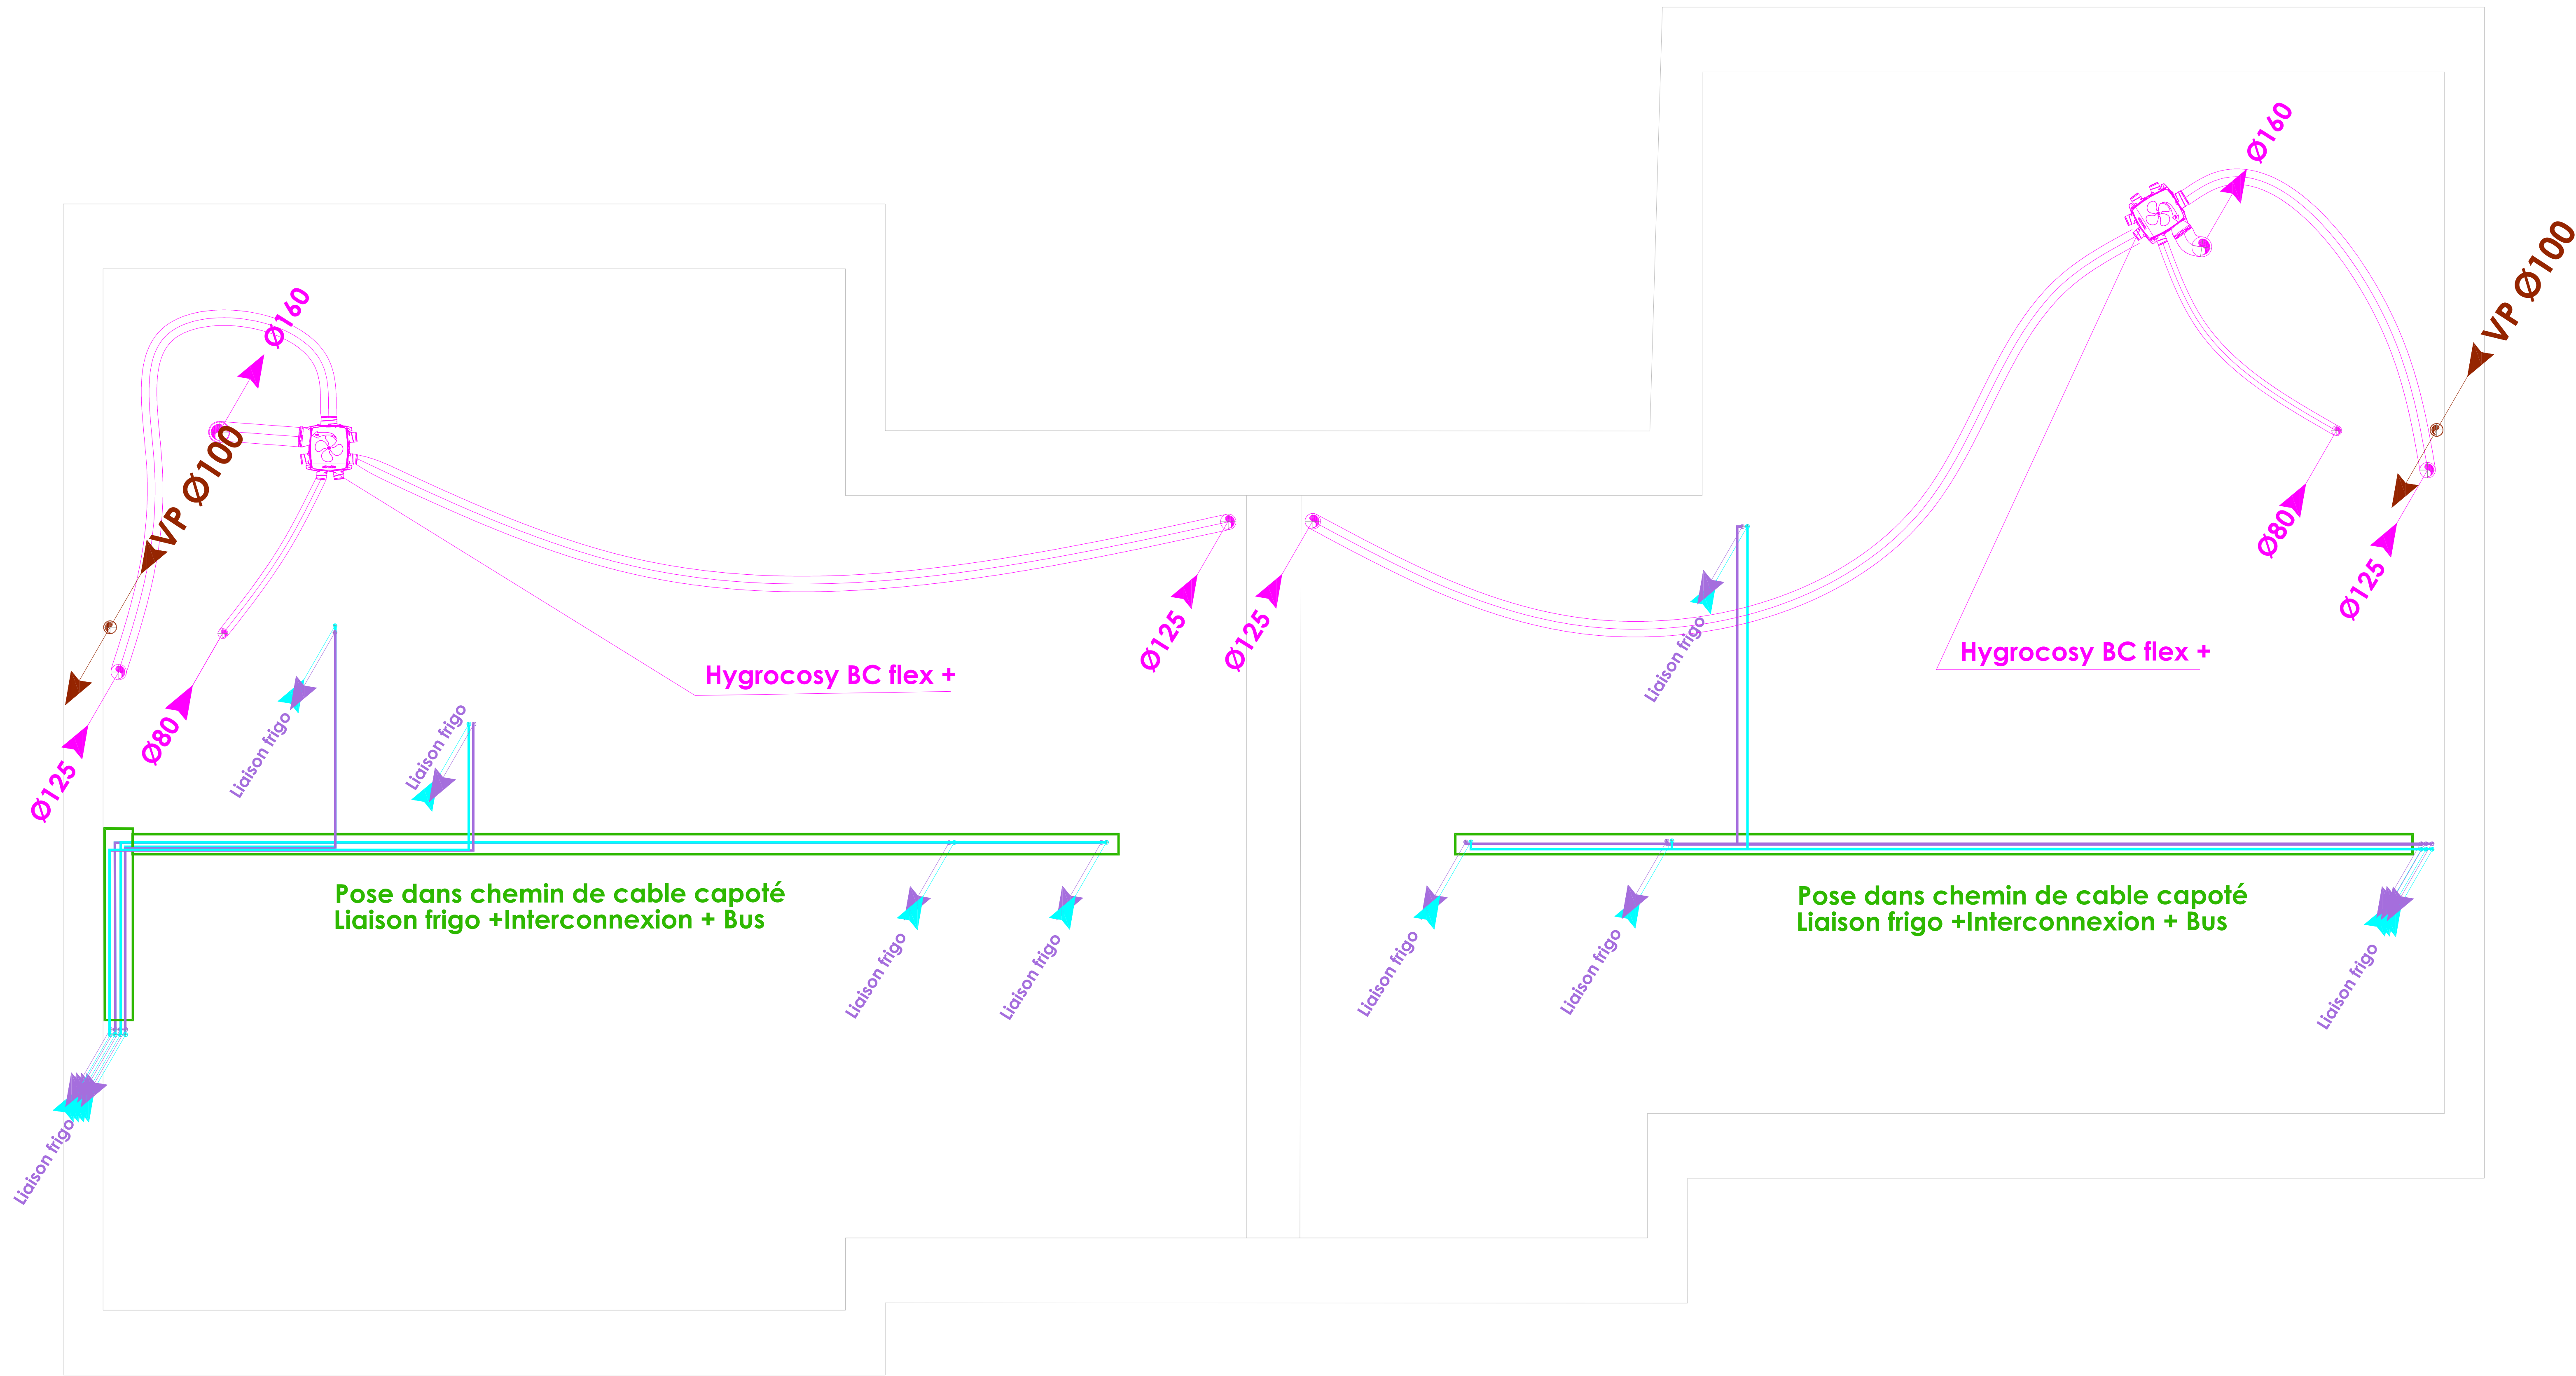

LEGENDE PLOMBERIE

- Eau froide sanitaire
- Eau chaude sanitaire
- Eaux usées
- Eaux vannes
- Condensats
- Siphon sec

DEBIT DE BASE DES APPAREILS

Désignation appareil	Debit EF ECS L/s	Diametre de raccordement PER	Debit EU EV L/s	Quantité d'installation (voir P.V.C.)
Lavabo	0,20	10/12	0,75	40
douche	0,20	13/16	0,5	40
WC	0,12	10/12	1,5	100
W.C. broyeur	0,33	13/16	1,7	50
Evier	0,20	13/16	0,75	40
Ligne nationale 1ère ligne	10/12	0,5	30	
rob. puisage	0,33	13/16		

LEGENDE DIMENSIONNEMENT

Vitesse d'écoulement des fluides et des fluides sanitaires : 1.5m/s en parties communes et sous-sol.
pente 10° en 10m en 10m.
pente 12° en 10m en 10m.
pente 15° en 10m en 10m.

LEGENDE CHAUFFAGE

- Unité extérieure
- Unité murale
- Liaisons frigorifiques

LEGENDE VENTILATION

- Extraction VMC
- Entrée d'air
- Bouche d'extraction

CONSTRUCTION DE 18 LOGEMENTS
RUE NEUVE GRAND TERRE
13930 AUREILLE

VILLAS 17 - 18

MAITRISE D'OUVRAGE

SCCV GRANDE TERRE
837 BIS ALLÉE DE PARIS
LA SEYNE SUR MER

MAITRISE D'OEUVRE
AXXION
41 Rue Ribas
13770 VENELLES

BET FLUIDES CVC
AXIO INGENIERIE
393 Rue Etienne BUGATTI
66000 PERPIGNAN
axio.ingenierie@gmail.com

LOT PLOMBERIE,VMC & RAFFRAICHISSEMENT
PLAN DES COMBLES

Ind	Date	Modifications	Dessiné par:	Vérifié par:
0	07/07/2026	Création du document	EB	LG
A			Date:	Echelle:
B			07/07/2026	1:25
C			Visa	
D				

NIVEAU	LOT	DOSSIER	PHASE	N° DOCUMENT	INDICE
TOIT	PB CVC		DCE	403	0