


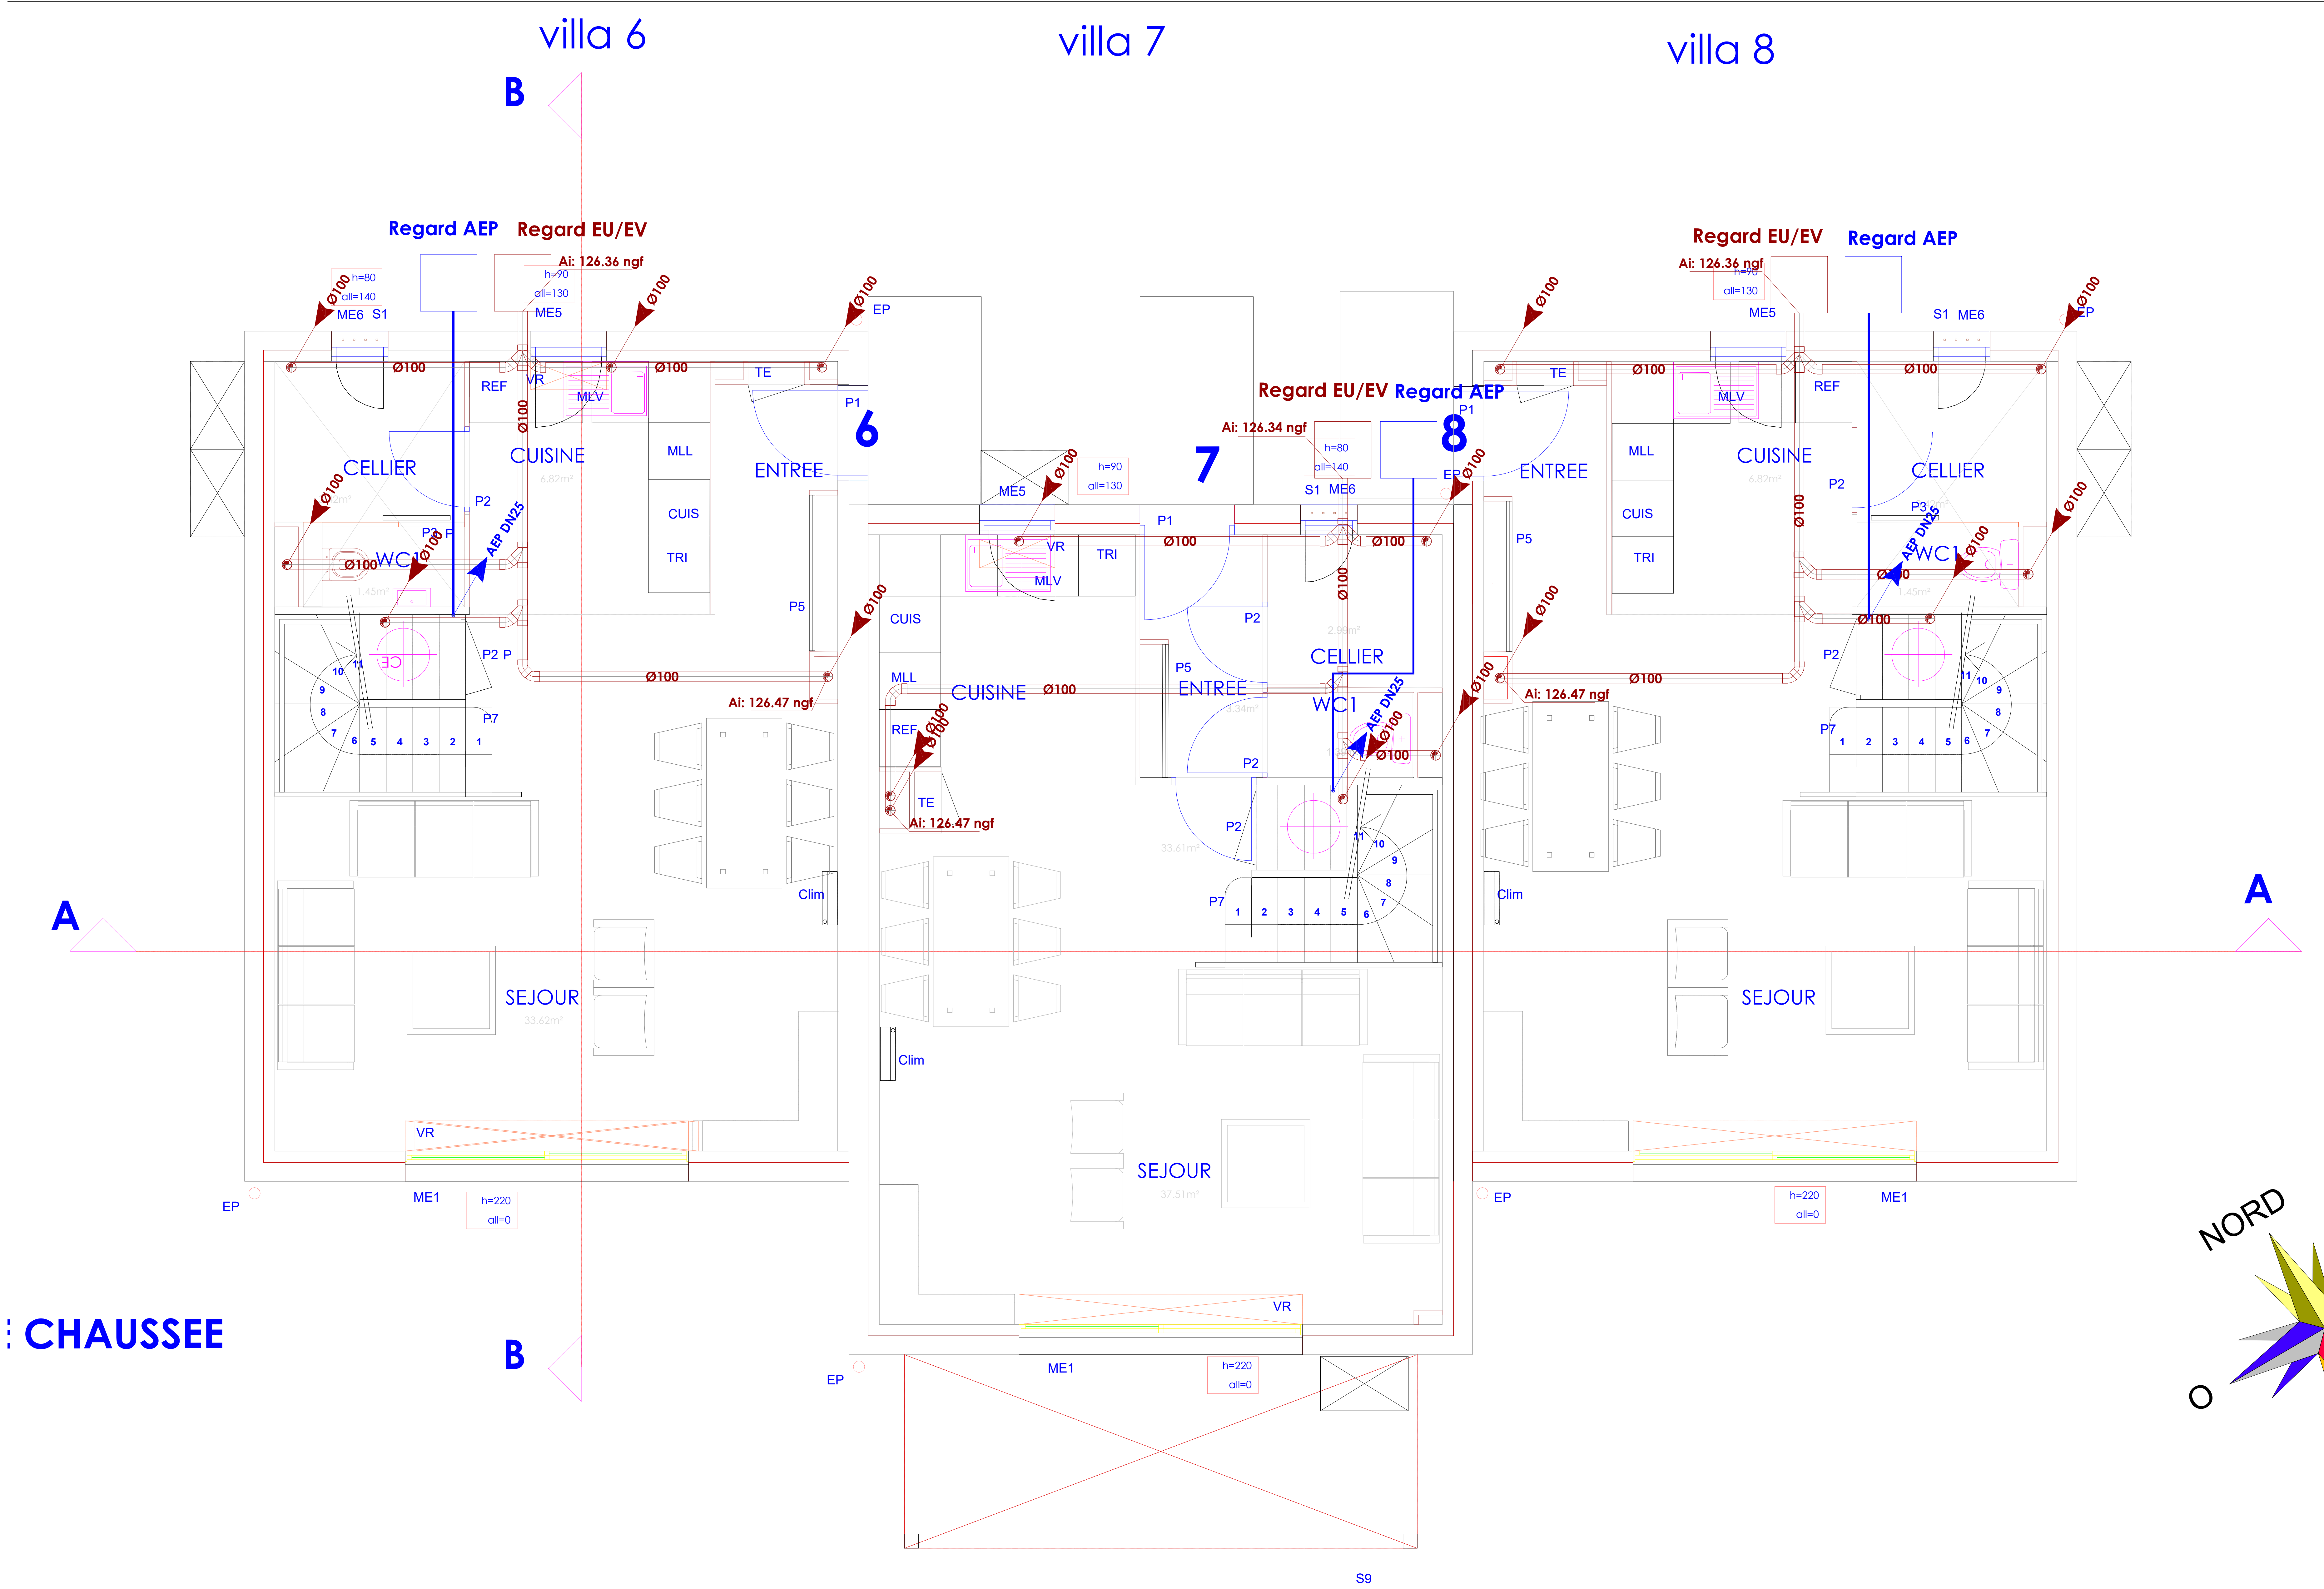

LEGENDE PLOMBERIE

- Eau froide sanitaire
- Eau chaude sanitaire
- Eaux usées
- Eaux vannes
- Condensats
- Siphon sec

DEBIT DE BASE DES APPAREILS

Désignation	Debit EF ECS	Debit de	Debit EU EV	Quantité
ajouté	Us	compteur/PER	Us	Évacuation
Lavabo	0.20	10/12	0.75	40
douche	0.20	13/16	0.5	40
WC	0.13	10/12	1.5	100
Baignoire	0.33	13/16	1.2	50
Évier	0.20	13/16	0.75	40
Line vaisselle lave linge	10/12	0.5	30	
rob. puitage	0.33	13/16		

LEGENDE DIMENSIONNEMENT

Vitesse réseau eau froide et eau chaude sanitaire : 1.5m/s en parties courantes et 1.0m/s en parties droites

peste EU, DV, EV, en 80/20

peste EP en 10/10

CONSTRUCTION DE 18 LOGEMENTS
RUE NEUVE GRAND TERRE
13930 AUREILLE

VILLAS 6 - 7 - 8

MAITRISE D'OUVRAGE
SCV GRANDE TERRE
837 BIS ALLEE DE PARIS
LA SEYNE SUR MER

MAITRISE D'OEUVRE
AXXION
41 Rue Ribas
13770 VENELLES

BET FLUIDES CVC
AXIO INGENIERIE
393 Rue Etienne BUGATTI
66000 PERPIGNAN
axio.ingenierie@gmail.com



LOT PLOMBERIE,VMC & RAFFRAICHISSEMENT
PLAN VIDE SANITAIRE

Ind	Date	Modifications	Dessiné par:	Vérifié par:
0	06/07/2026	Création du document	EB	LG
A			Date:	Echelle:
B			06/07/2026	1:25
C			Visa:	
D				

NIVEAU	LOT	DOSSIER	PHASE	N° DOCUMENT	INDICE
VS	PB CVC		DCE	400	0