


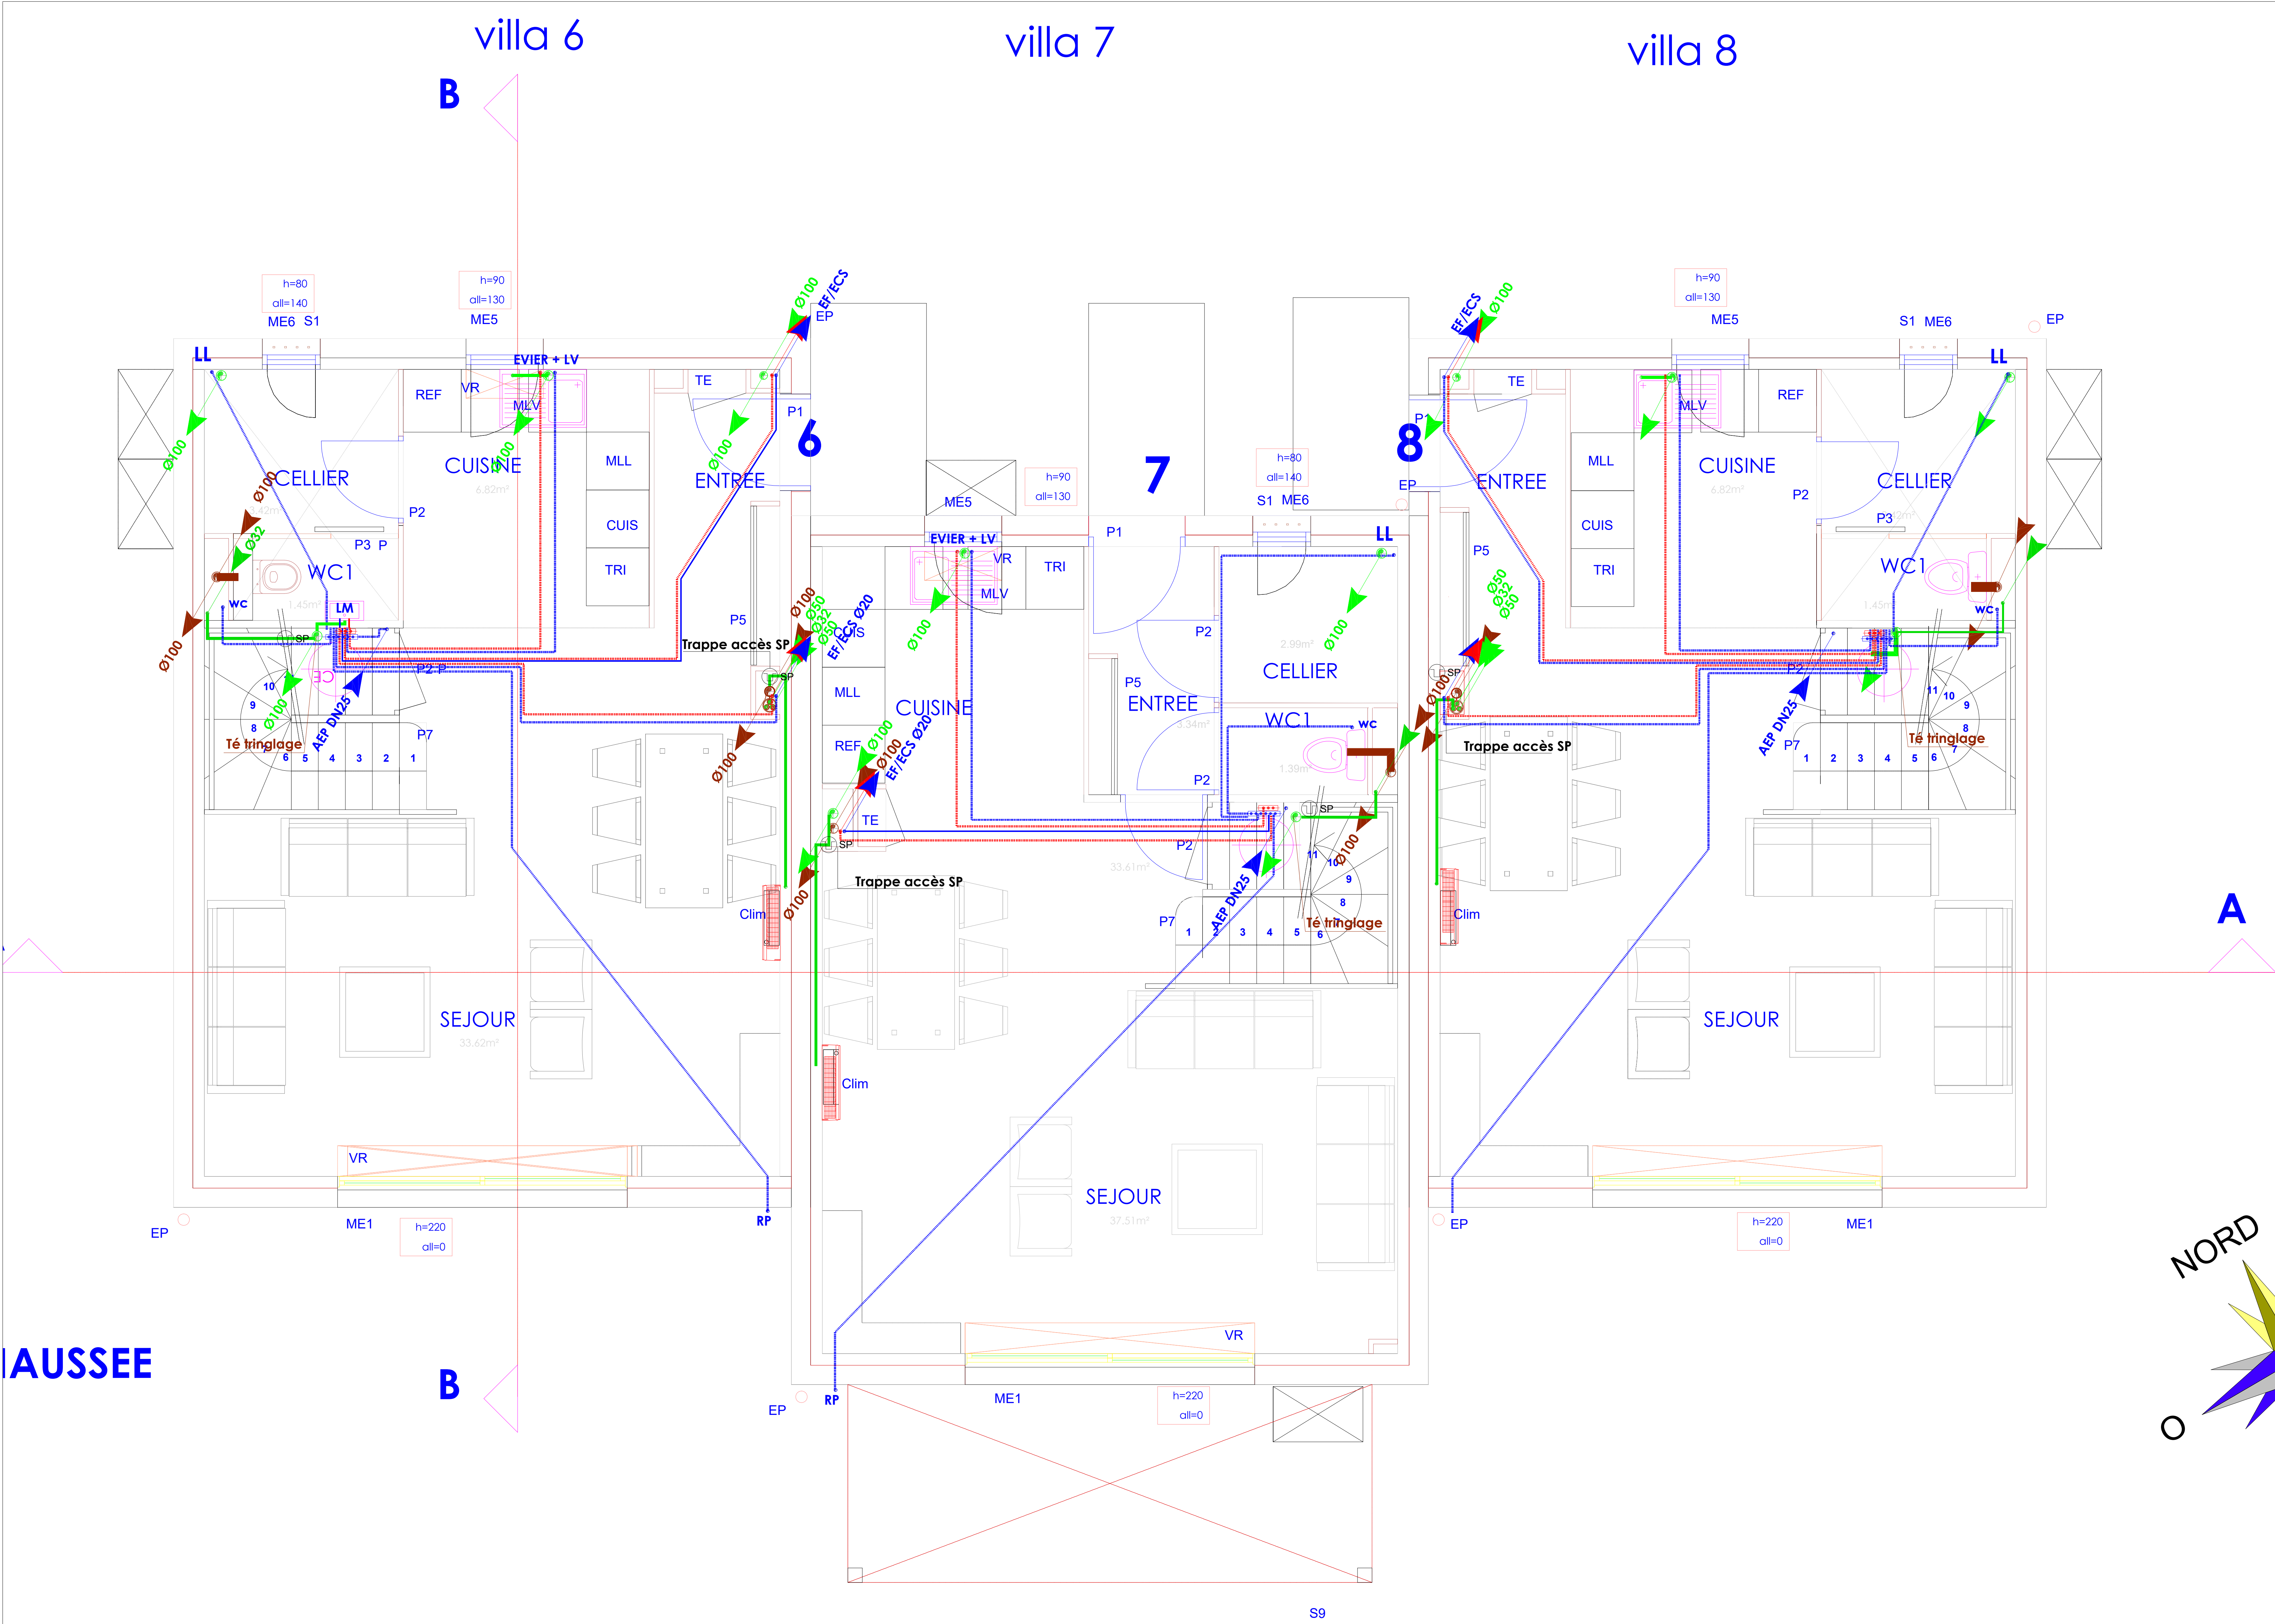

LEGENDE PLOMBERIE

- Eau froide sanitaire
- Eau chaude sanitaire
- Eaux usées
- Eaux vannes
- Condensats
- Siphon sec

DEBIT DE BASE DES APPAREILS

Désignation	Debit EF ECS	Diamètre de raccordement PPR	Debit EU EV	Quantité
Lavabo	0.30	10/12	0.75	40
Douche	0.30	13/16	0.5	40
WC	0.12	10/12	1.5	100
Baignoire	0.33	13/16	1.2	50
Evier	0.20	13/16	0.75	40
Lave-vaisselle	0.12	10/12	0.5	30
rob. passage	0.33	13/16		

LEGENDE DIMENSIONNEMENT

Vitesse réseau eau froide et eau chaude sanitaire : 1.5m/s en parties courbées et 3.0m/s en parties droites.

perte EU, EV, EUS en PPR 20°

perte EF en PPR 1.5°

CONSTRUCTION DE 18 LOGEMENTS
RUE NEUVE GRAND TERRE
13930 AUREILLE

VILLAS 6 - 7 - 8

MAITRISE D'OUVRAGE

SCV GRANDE TERRE
837 BIS ALLÉE DE PARIS
LA SEYNE SUR MER

MAITRISE D'OEUVRE

AXXION
41 Rue Ribas
13770 VENELLES

BET FLUIDES CVC

AXIO INGENIERIE
393 Rue Etienne BUGATTI
66000 PERPIGNAN
axio.ingenierie@gmail.com

LOT PLOMBERIE,VMC & RAFFRAICHISSEMENT

PLAN PLOMBERIE EVACUATIONS RDC

Ind	Date	Modifications	Dessiné par:	Vérifié par:
0	06/07/2026	Création du document	EB	LG
A			Date:	Echelle:
B			06/07/2026	1:25
C			Visa:	
D				

NIVEAU	LOT	DOSSIER	PHASE	N° DOCUMENT	INDICE
R0	PB CVC		DCE	401	0