


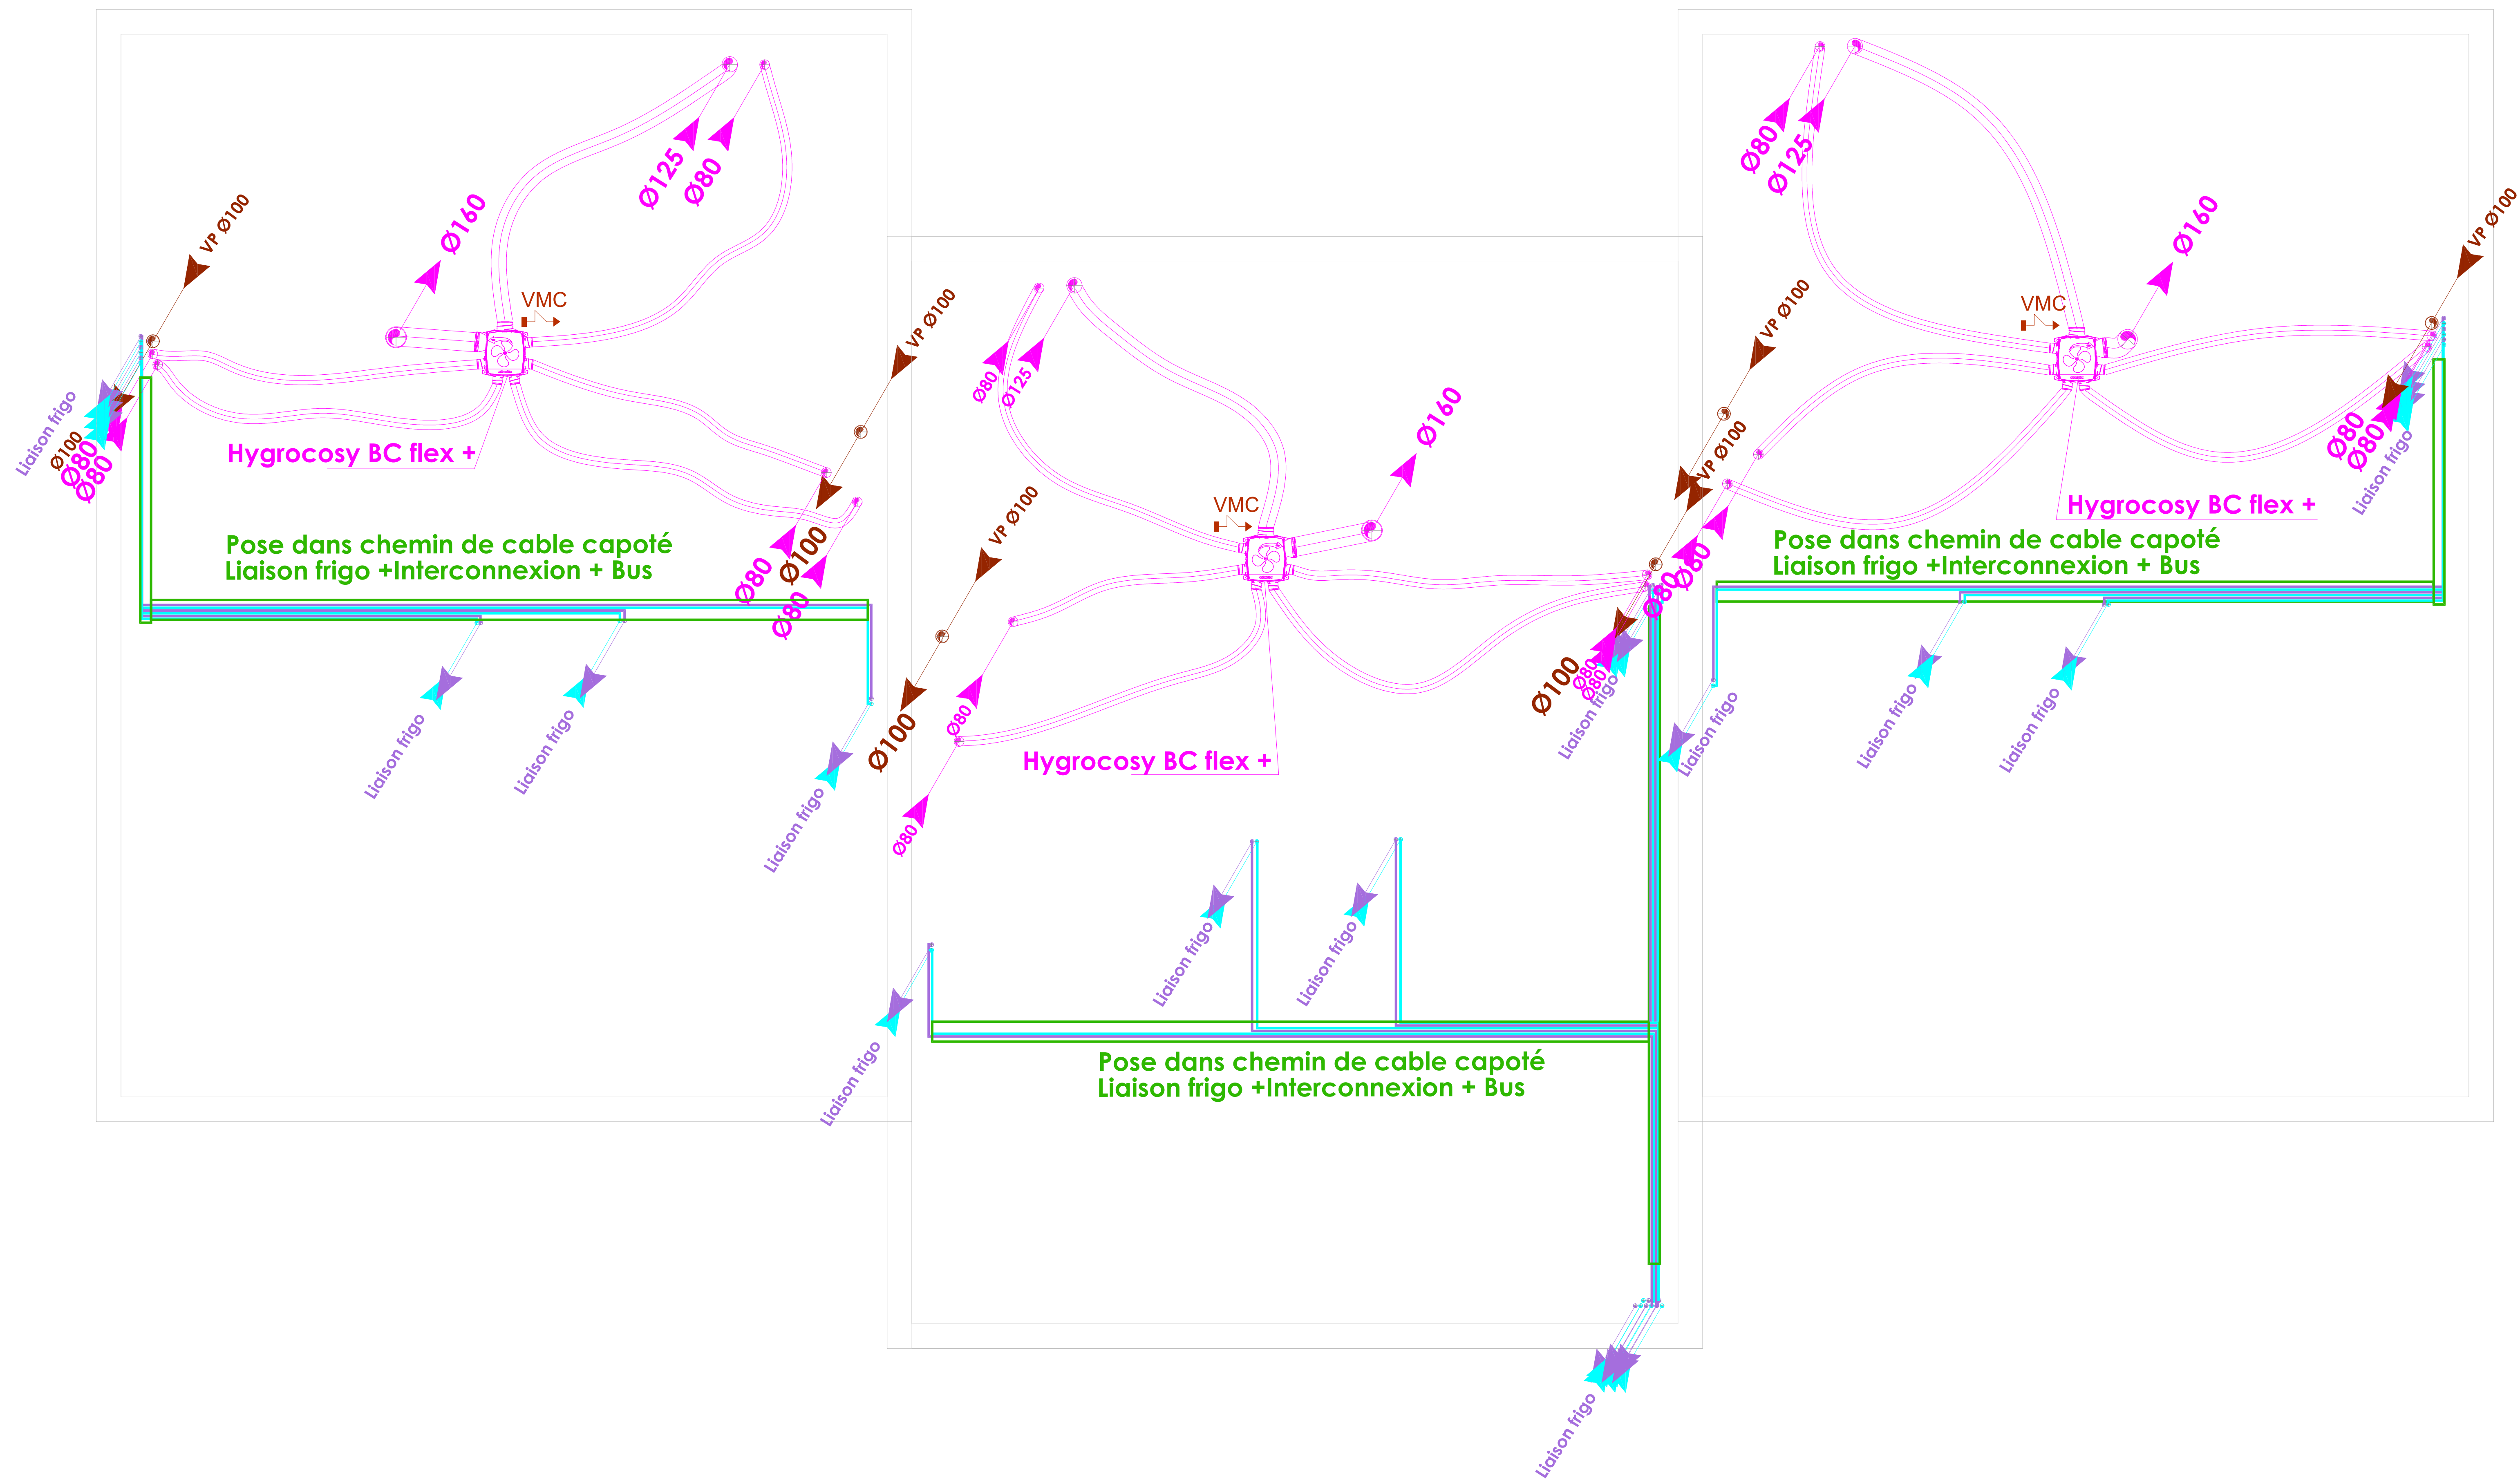

LEGENDE PLOMBERIE

- Eau froide sanitaire
- Eau chaude sanitaire
- Eaux usées
- Eaux vannes
- Condensats
- Siphon sec

DEBIT DE BASE DES APPAREILS				
Designation appareil	Debit EF ECS L/s	Debit EF ECS L/s	Debit EF ECS L/s	Debit EF ECS L/s
Lavabo	0.20	1/2	0.75	40
Douche	0.20	1/2	0.75	40
WC	0.12	1/2	1.5	100
Evier	0.20	1/2	0.75	40
Bois	0.33	1/2	0.75	40
Evier	0.20	1/2	0.75	40
Lave vaisselle	0.20	1/2	0.75	40
rob. poussoir	0.33	1/2	0.75	40

LEGENDE DIMENSIONNEMENT

Vitesse fluide eau froide et eau chaude sanitaire : 1.5m/s en parties communes et sous-sol

perte ELV, EV, EVS en l'ordre

perte EP en l'ordre 1.5%

LEGENDE CHAUFFAGE

- Unité extérieure
- Unité murale
- Liaisons frigorifiques

LEGENDE VENTILATION

- Extraction VMC
- Entrée d'air
- Bouche d'extraction

CONSTRUCTION DE 18 LOGEMENTS
RUE NEUVE GRAND TERRE
13930 AUREILLE

VILLAS 6 - 7 - 8

MAITRISE D'OUVRAGE

SCCV GRANDE TERRE
837 BIS ALLÉE DE PARIS
LA SEYNE SUR MER

MAITRISE D'OEUVRE
AXXION
41 Rue Ribas
13770 VENELLES

BET FLUIDES CVC
AXIO INGENIERIE
393 Rue Ettore BUGATTI
66000 PERPIGNAN
axio.ingenierie@gmail.com



LOT PLOMBERIE, VMC & RAFFRAICHISSEMENT
PLAN DES COMBLES

Ind	Date	Modifications	Dessiné par:	Vérifié par:
0	06/07/2026	Création du document	EB	LG
A			Date:	Echelle:
B			06/07/2026	1:25
C			Visa	
D				

NIVEAU	LOT	DOSSIER	PHASE	N° DOCUMENT	INDICE
TOIT	PB CVC		DCE	403	0