


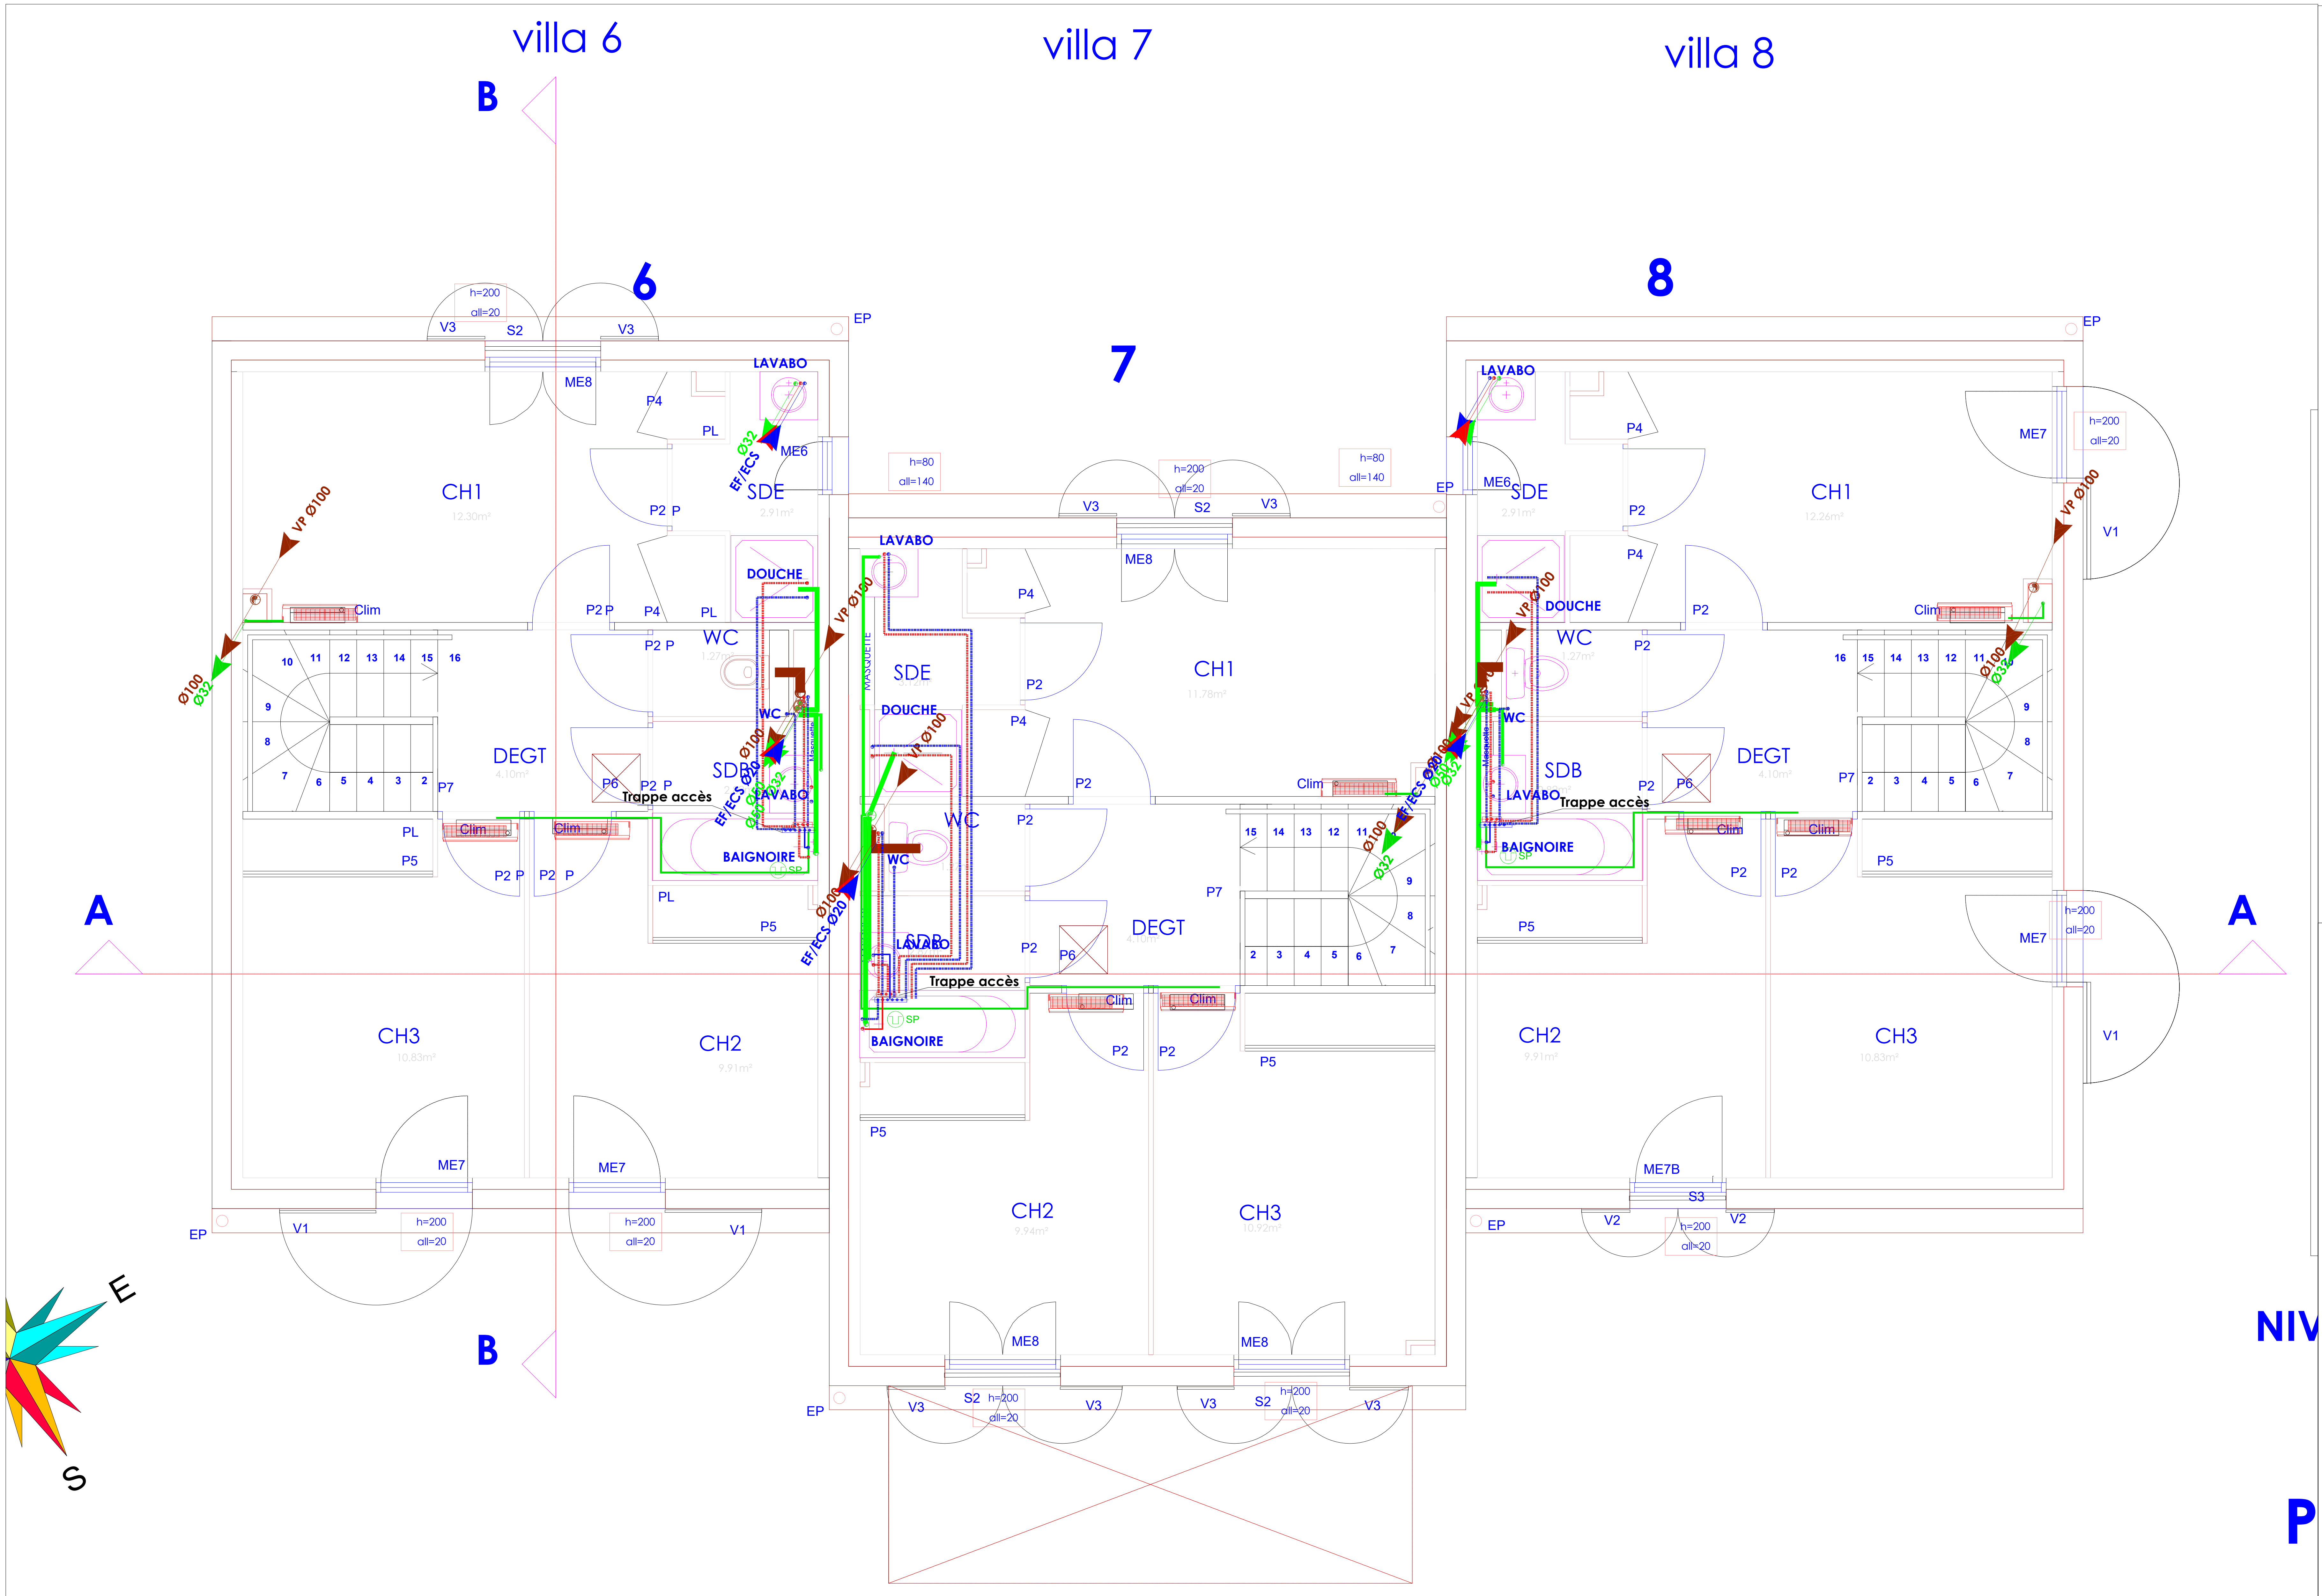

LEGENDE PLOMBERIE

- Eau froide sanitaire
- Eau chaude sanitaire
- Eaux usées
- Eaux vannes
- Condensats
- Siphon sec

DEBIT DE BASE DES APPAREILS				
Designation	Debit EF EDS	Debit de	Debit EU EV	Quantite
quantite	LA	recolement PER	LA	chauffage
Lavabo	0.25	15/12	0.75	40
douche	0.20	15/16	0.5	40
ec.	0.12	15/12	1.5	100
Baignoire	0.35	15/16	1.2	50
Evier	0.20	15/16	0.75	40
Lave-vaisselle	0.20	15/12	0.5	30
rob. passage	0.35	15/16		

LEGENDE DIMENSIONNEMENT

Vitesse réseau eau froide et eau chaude sanitaire : 1.5m/s en parties courbées et 30m/s en parties droites
perte EU, EV, EUD en Raccord
perte EP en Raccord 1.5%

CONSTRUCTION DE 18 LOGEMENTS
RUE NEUVE GRAND TERRE
13930 AUREILLE

VILLAS 6 - 7 - 8

MAITRISE D'OUVRAGE

SCV GRANDE TERRE
837 BIS ALLEE DE PARIS
LA SEYNE SUR MER

MAITRISE D'OEUVRE
AXION
41 Rue Ribas
13770 VENELLES

BET FLUIDES CVC
AXIO INGENIERIE
393 Rue Etienne BUGATTI
66000 PERPIGNAN
axio.ingenierie@gmail.com



LOT PLOMBERIE,VMC & RAFFRAICHISSEMENT
PLAN PLOMBERIE EVACUATIONS R+1

Ind	Date	Modifications	Desiné par:	Vérifié par:
0	06/07/2026	Création du document	EB	LG
A			Date:	Echelle:
B			06/07/2026	1:25
C			Visa:	
D				

NIVEAU	LOT	DOSSIER	PHASE	N° DOCUMENT	INDICE
R1	PB CVC		DCE	411	0