


villa 9

villa 10

villa 11

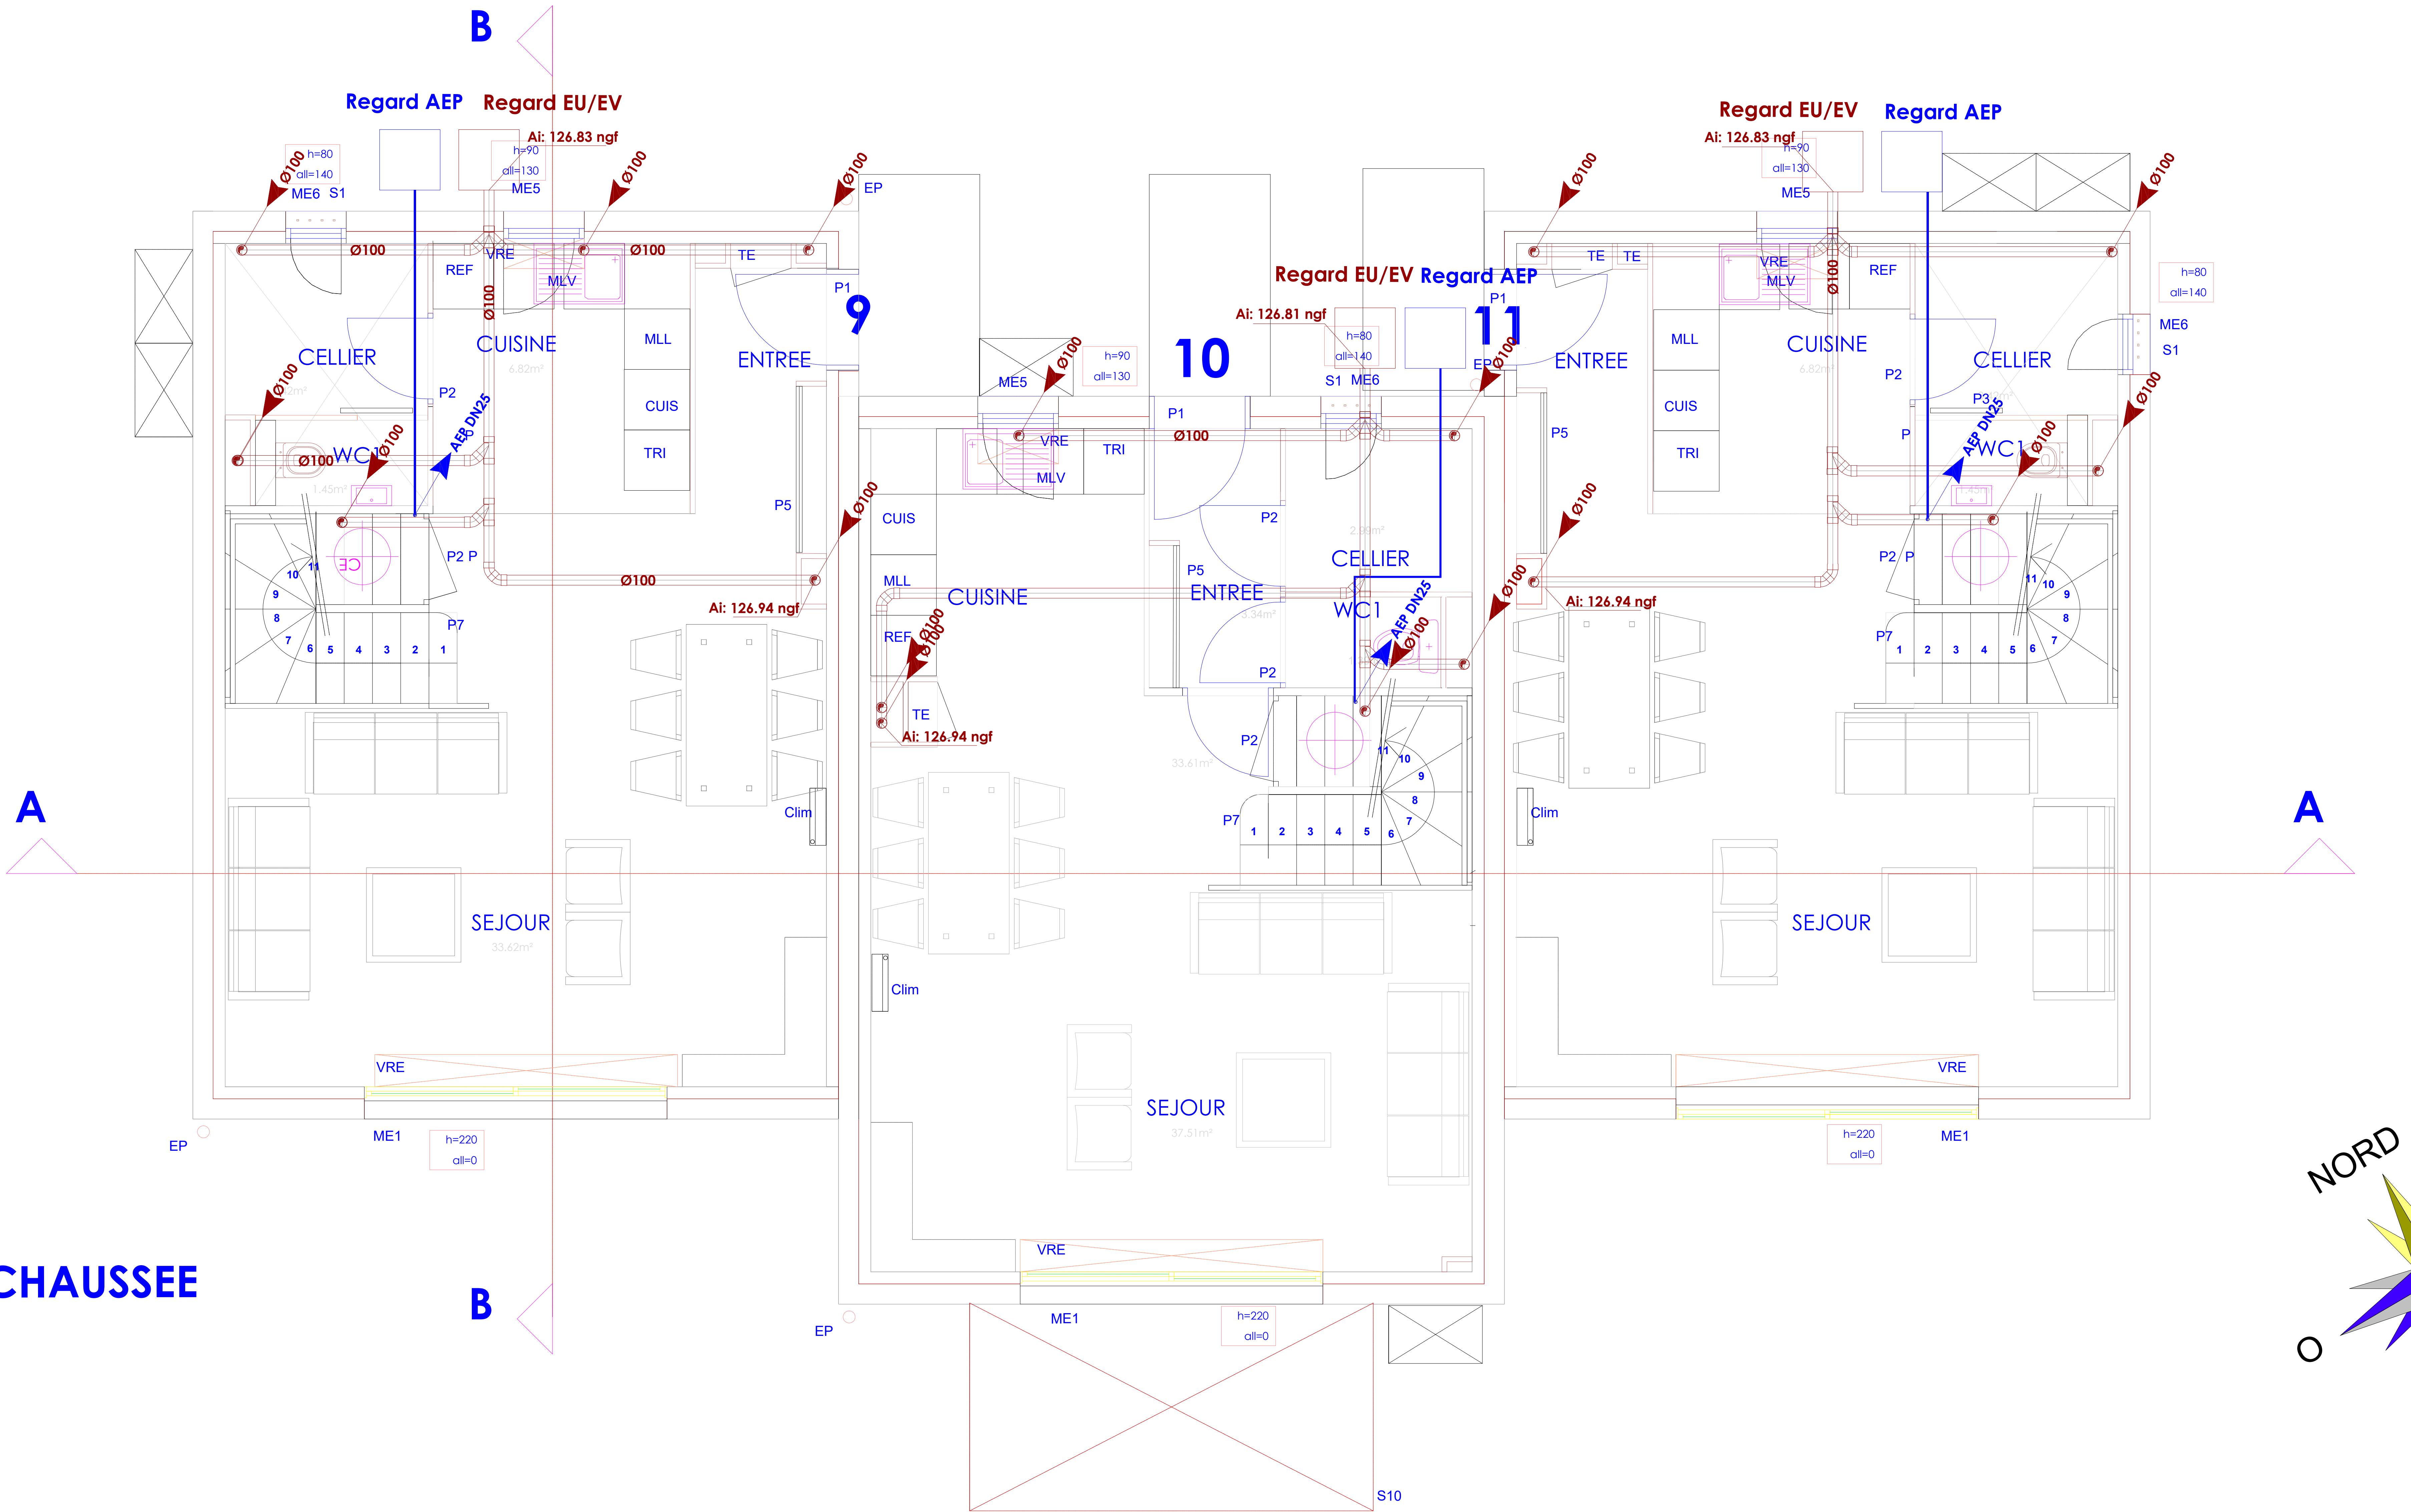

LEGENDE PLOMBERIE

- Eau froide sanitaire
- Eau chaude sanitaire
- Eaux usées
- Eaux vannes
- Condensats
- Siphon sec

DEBIT DE BASE DES APPAREILS

Désignation	Debit EF ECS	Debit EF ECS	Debit EF EV	Quantité
appareil	L/s	recommandé (P/R)	La	(Bât. P/R)
Lavabo	0.20	10/12	0.75	40
douche	0.20	13/16	0.5	40
WC	0.13	10/12	1.5	100
Baignoire	0.33	13/16	1.2	50
Evier	0.20	13/16	0.75	40
Lave vaisselle	0.20	10/12	0.5	30
rob. passage	0.33	13/16		

LEGENDE DIMENSIONNEMENT

Vitesse réseau eau froide et eau chaude sanitaire : 1.5m/s en parties horizontales et 3.0m/s en parties verticales

perte D.U. EV, D.U. en regard 2%

perte TP en regard 1.5%

CONSTRUCTION DE 18 LOGEMENTS
RUE NEUVE GRAND TERRE
13930 AUREILLE

VILLAS 9 - 10 - 11

MAITRISE D'OUVRAGE
SCV GRANDE TERRE
837 BIS ALLEE DE PARIS
LA SEYNE SUR MER

MAITRISE D'OEUVRE
AXION
41 Rue Ribas
13770 VENELLES

BET FLUIDES CVC
AXIO INGENIERIE
393 Rue Etienne BUGATTI
66000 PERPIGNAN
axio.ingenierie@gmail.com



LOT PLOMBERIE,VMC & RAFFRAICHISSEMENT
PLAN VIDE SANITAIRE

Ind	Date	Modifications	Dessiné par:	Vérifié par:
0	06/07/2026	Création du document	JPG	LG
A			Date:	Echelle:
B			06/07/2026	1:25
C			Visa:	
D				

NIVEAU	LOT	DOSSIER	PHASE	N° DOCUMENT	INDICE
VS	PB CVC		DCE	400	0