


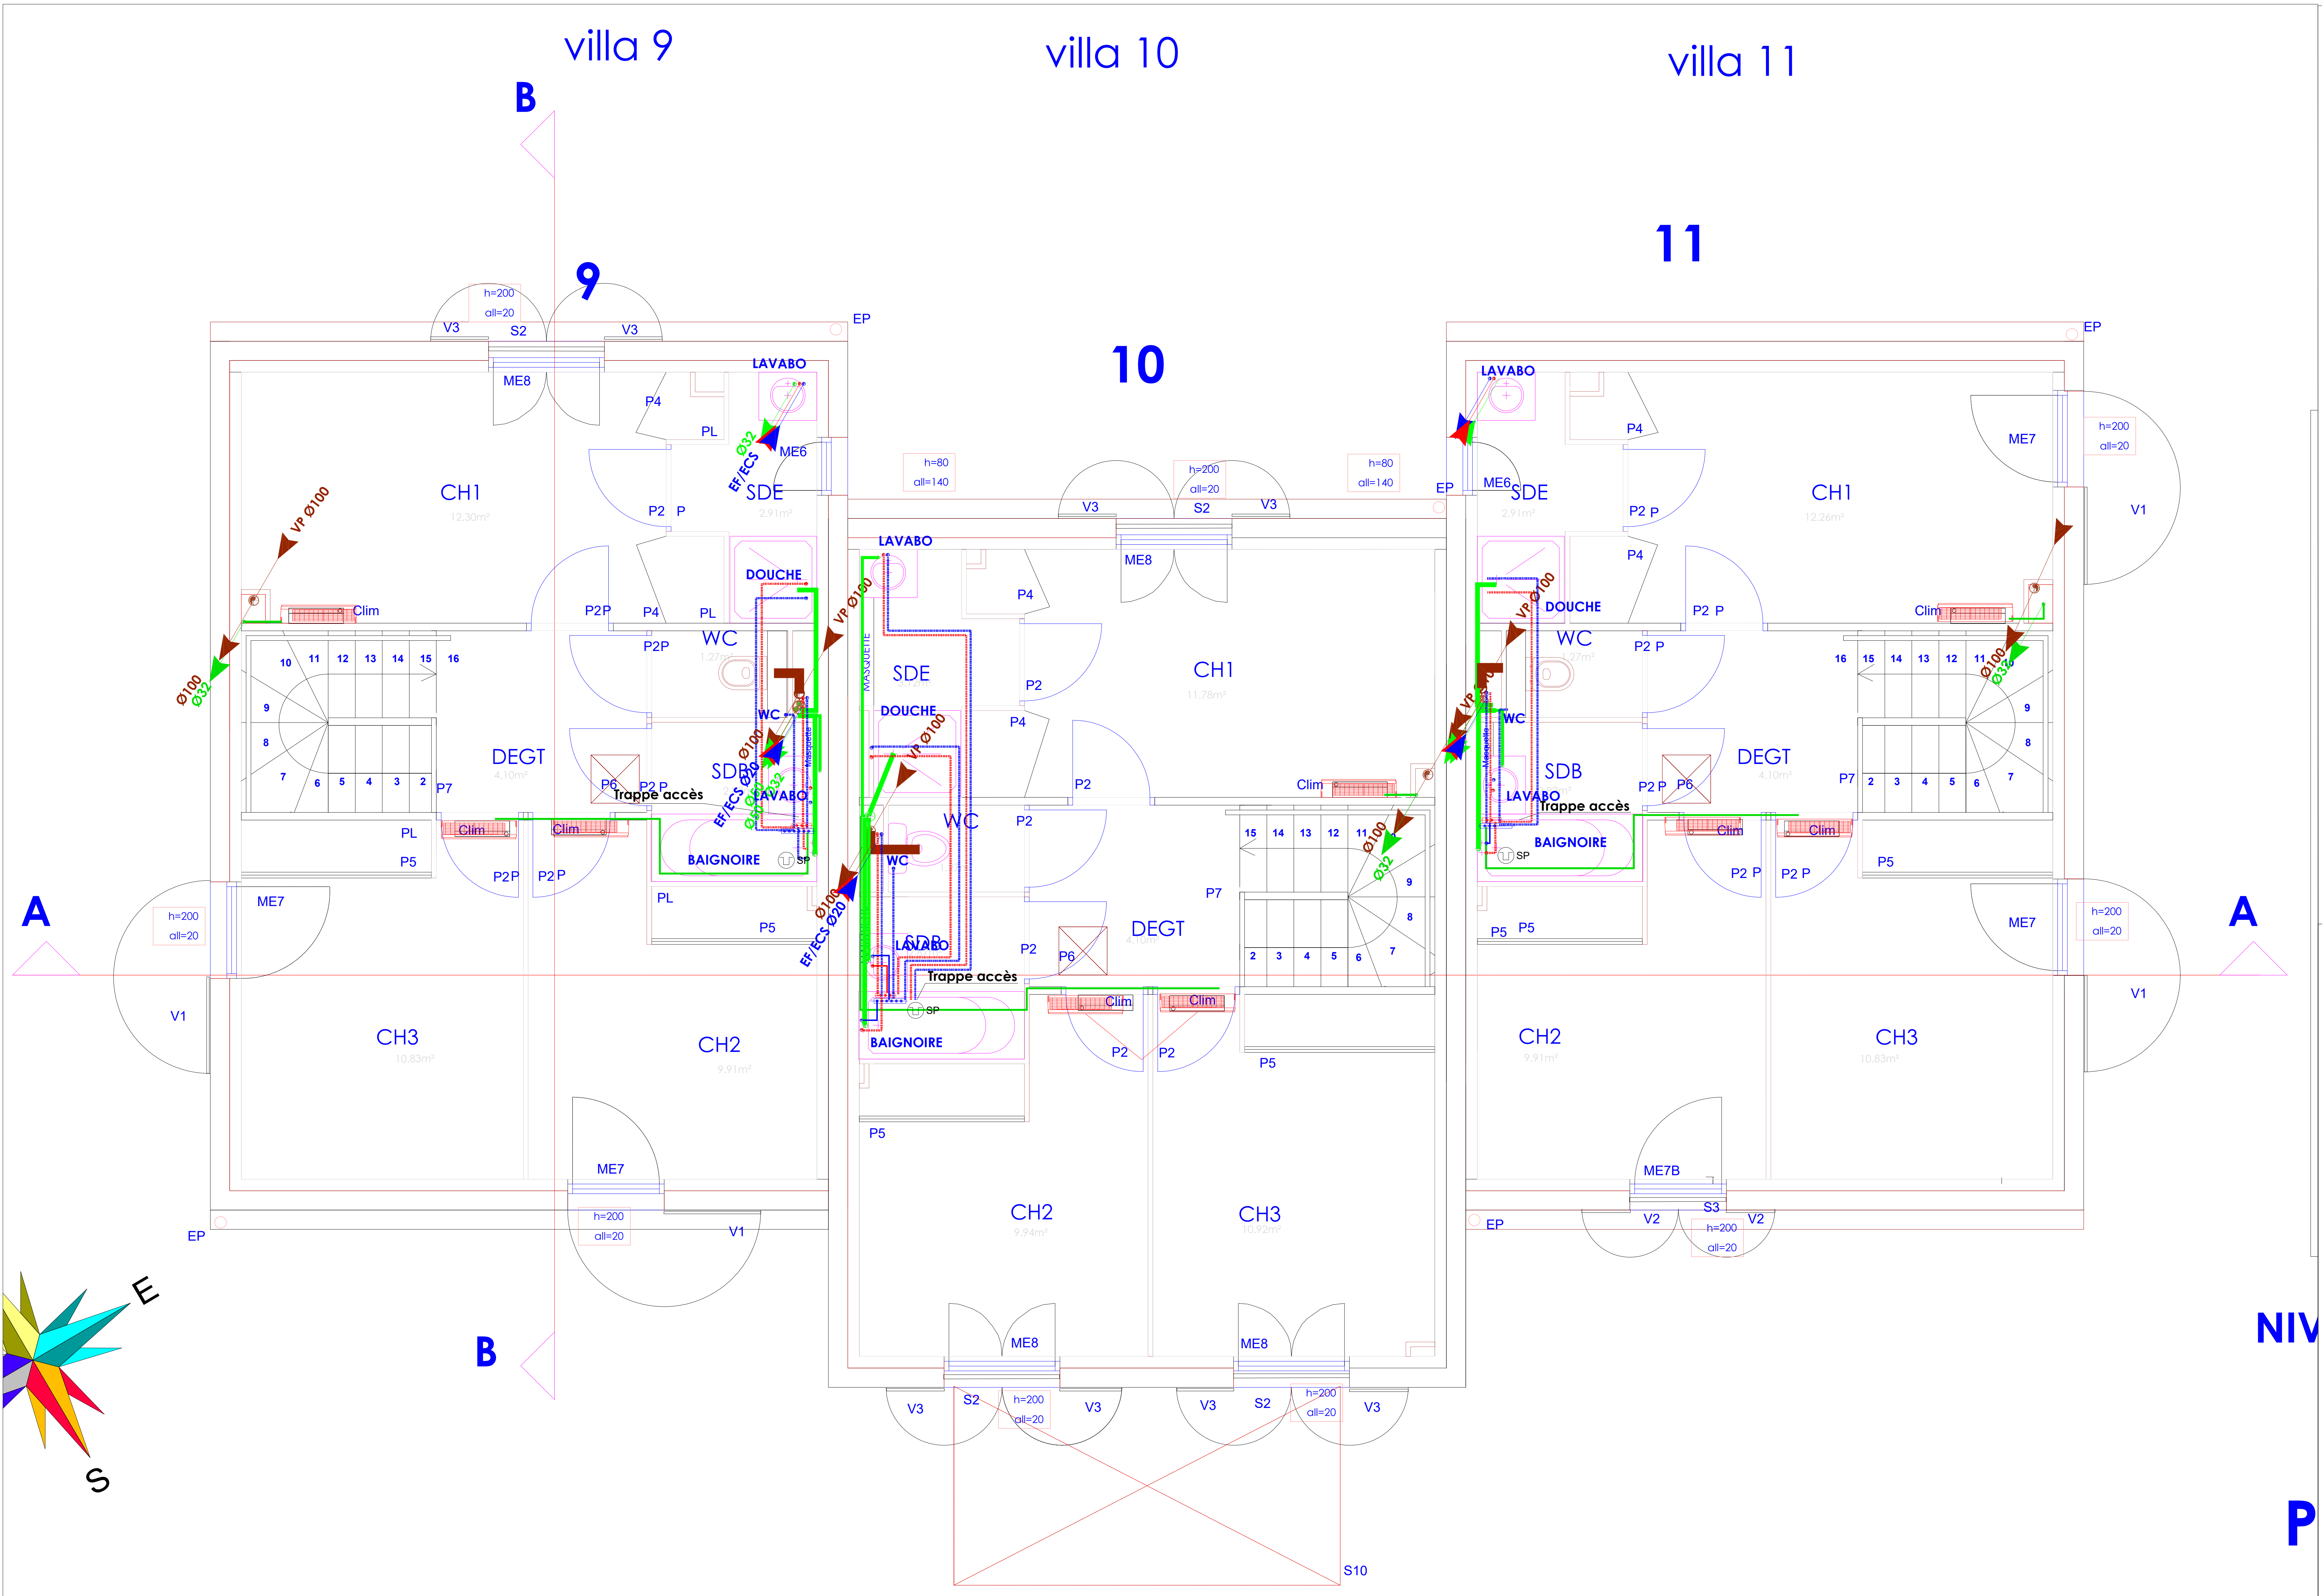

LEGENDE PLOMBERIE

- Eau froide sanitaire
- Eau chaude sanitaire
- Eaux usées
- Eaux vannes
- Condensats
- Siphon sec

DEBIT DE BASE DES APPAREILS				
Désignation	Donnée EF EDS	Quantité de	Donnée EF EV	Quantité
usager	La	reconnues PER	La	d'occupation
Lavabo	0.25	10/12	0.75	40
douche	0.20	15/16	0.5	40
WC	0.12	10/12	1.5	100
Baignoire	0.33	15/16	1.2	50
Evier	0.20	15/16	0.75	40
Low velocity flow trap	10/12	0.5	32	
rob. puisage	0.33	15/16		

Version réseau eau froide et eau chaude sanitaire : 1.5m/s en parties courantes et 300-400.
perte EU, EV, DUE en flèche 2/3
perte EP en flèche 1/3

LEGENDE DIMENSIONNEMENT

CONSTRUCTION DE 18 LOGEMENTS
RUE NEUVE GRAND TERRE
13930 AUREILLE

VILLAS 9 - 10 - 11

MAITRISE D'OUVRAGE

SCV GRANDE TERRE
837 BIS ALLEE DE PARIS
LA SEYNE SUR MER

MAITRISE D'OEUVRE
AXXION
41 Rue Ribas
13770 VENELLES

BET FLUIDES CVC
AXIO INGENIERIE
393 Rue Etienne BUGATTI
66000 PERPIGNAN
axio.ingenierie@gmail.com



LOT PLOMBERIE,VMC & RAFFRAICHISSEMENT
PLAN PLOMBERIE EVACUATIONS R+1

Ind	Date	Modifications	Dessiné par:	Vérifié par:
0	06/07/2026	Création du document	JPG	LG
A			Date:	Echelle:
B			06/07/2026	1:25
C			Visa:	
D				

NIVEAU	LOT	DOSSIER	PHASE	N° DOCUMENT	INDICE
R1	PB CVC		DCE	411	0