

LEGENDE		MENTIONS	
	Mur BA	NOM	ELEMENTS
	Mur BA de l'usage avec reprise mur BA	PI/	Poutre Voile
	Pléneur	CV	Console Voile
	Altitude dans Murs	VD	Voile Drapeau
		VS	Voile Suspens
		BN	Bande Noyée
		B	Poutre
		VSD	Voile Réglés sur Dalle
		P	Poutre


DOCUMENTS DE REFERENCES			
ORIGINE DOCUMENT	OBJET	N° DOCUMENT	DATE
-	Plan DCE	181125_DCE_02	17/11/2025
	Plan Révisions PHAS		
	Essais		
	Dossier de Révisions		
	Portes		
	Portes CO - Hds		
	Révisions		
	Dimension Porte-Pailles		

HYPOTHESES DE CALCUL (charges en daN/m²)								
CHARGES & SURCHARGES	TYPE	COURANTE	S1	S2	S3	S4	S5	S6
Charges permanentes - PP Plancher + Revet Sol	G	500 daN	-	-	-	-	-	-
Charges	G	50 daN	-	-	-	-	-	-
Surcharge Vire d'exploitation	Q	150 daN	-	-	-	-	-	-
Surcharge jardin	G	-	-	-	-	-	-	-

BETON : fck = 25 MPa (sauf mention contraire sur plan)	fcm = 28 MPa	TRELLIS SOUDÉS : (A4es) TSL 300	fyk = 500 MPa
ENROBAGE : 2,5 cm			TSH 500 fyk = 500 MPa
COUPE FEU : 1 H			S 300 (Type B) pour trappes soudés
ZONE DE SISMOTITE : ZONE 3			ADHERS : Haute Adhérence (HA) S300 - Type B) pour Ø ≤ 16 mm
CLASSE DE SOL : CLASSE A			(Type B) pour Ø > 16 mm
FONDATIONS : Contraintes admissibles = 2,5 Bars. Suivant étude GEC - GEPPO du 06/05/2026			


E					
D					
C					
B	09/06/2026	MB	MB		Mise à jour / Cour anglaise accès VS.
A	21/05/2026	MB	MB		Mise à jour suite reunion du 20/05/2026
O	08/05/2026	MB	MB		PREMIERE EMISSION
Ind	Date	Rédaction	Vérification	Approbation	MODIFICATIONS / OBSERVATIONS

COUPE TYPE FONDATIONS

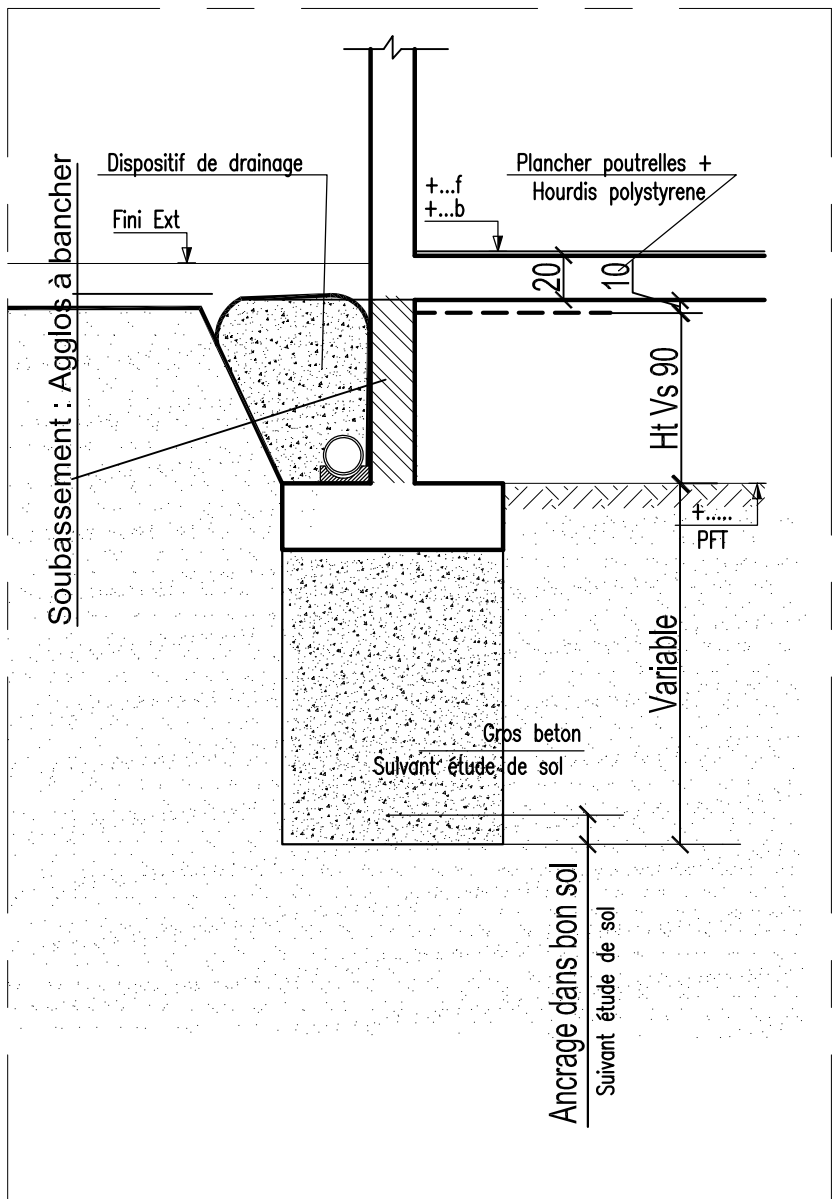

COUPE TYPE STRUCTURE

Villas 1 - 2 - 3

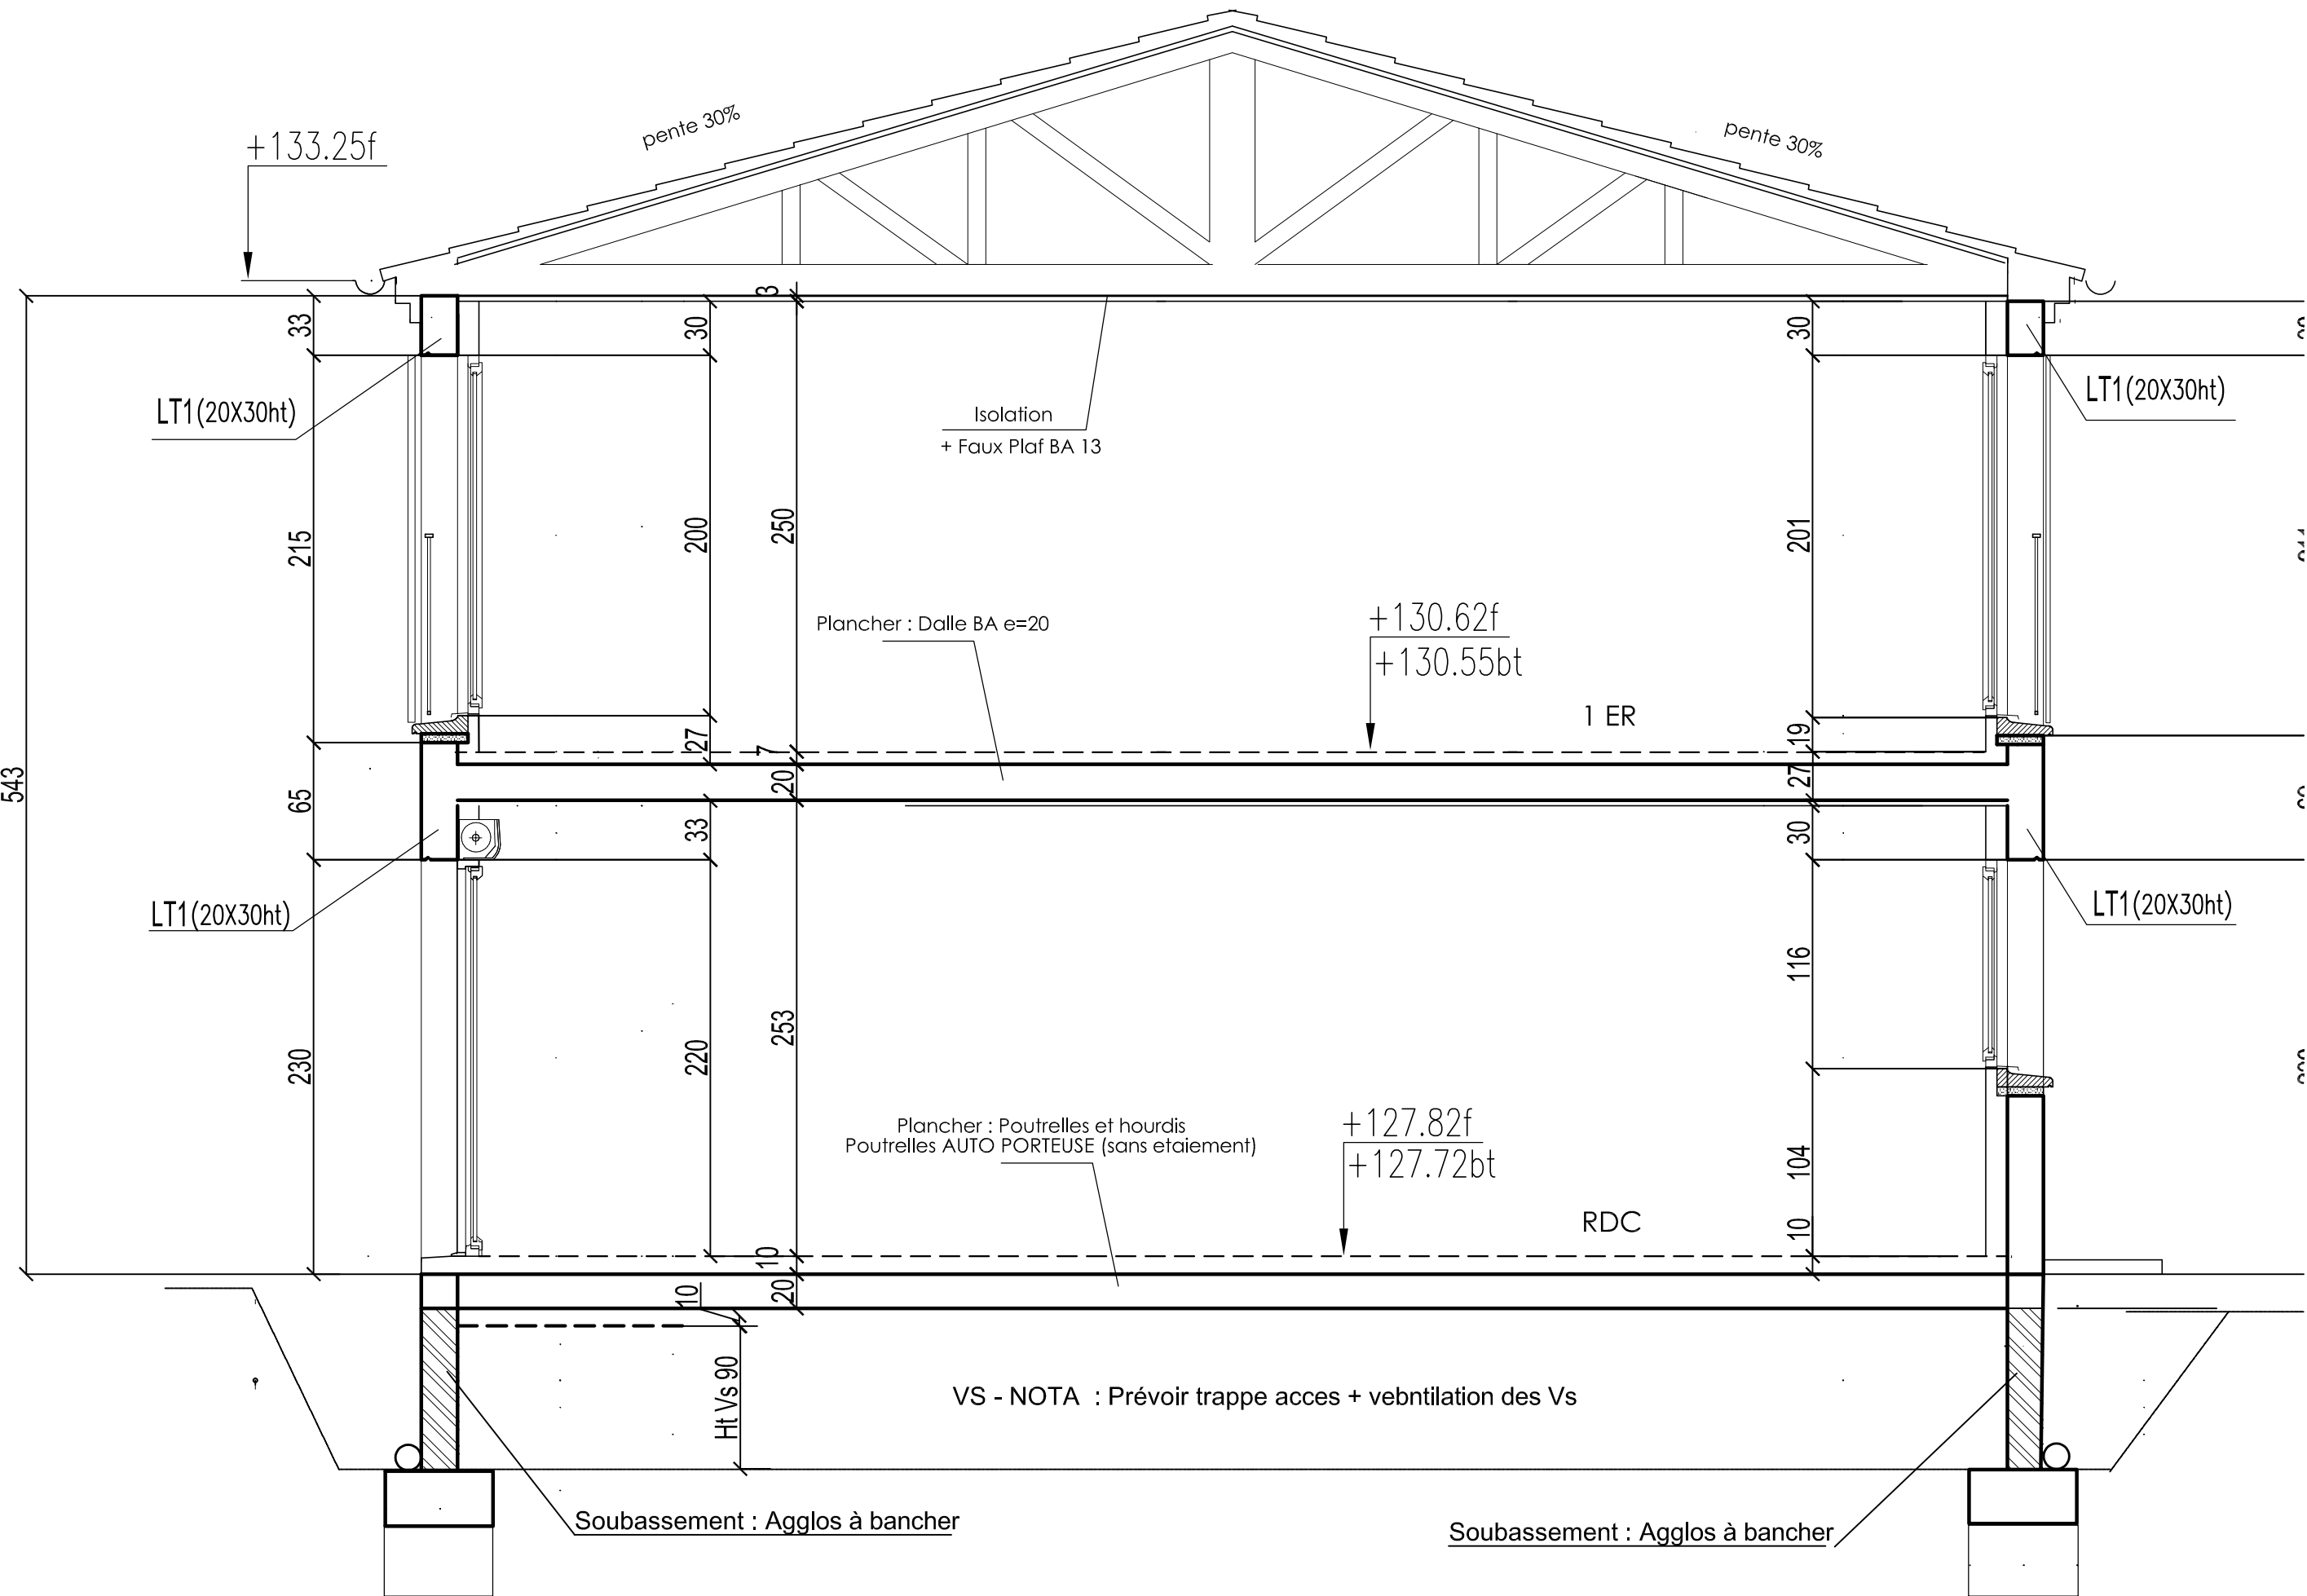

SCCV GRANDE TERRE
18 VILLAS A AUREILLE

MAITRE D'OUVRAGE

SCCV GRANDE TERRE
837 BIS AV DE PARIS
LA SEYNE SUR MER

MAITRE D'OEUVRE

AXXION
41 Rue Ribas
13770 VENELLES

ARCHITECTE

MICHEL CHAUVET &
CATHERINE CARNAZZA
ARCHITECTES

BUREAU DE CONTROLE

ALPES CONTROLES
67 Rue Ollioules
83140 SIX FOURS

ENTREPRISE

A Désigner

BET STRUCTURE

BET BMC

49 Domaine du val des pins
2 Montée Belle France
13015 MARSEILLE

VILLAS 1-2-3 & DITO POUR VILLAS 4 à 11
COFFRAGE FONDATION & HT VS
COUPES TYPES

Rédaction: E.H	Signature	Vérification: B.B	Signature	Approbation:	Signature
		Date :08-05-2026		Date :	

Echelle: 1:50					
Elaboré	Zones	Nature	Type de document	N° de document	Révisé
ECS	/	DCE	COF	0 0 1 0	/ B

Ce document est la propriété intellectuelle du BET BMC
Il ne saurait être reproduit ou communiqué à des tiers sans son autorisation .