



HT DES RDC
Murs Refends entre Logements : Agglos à bancher
villa 1 villa 2 villa 3

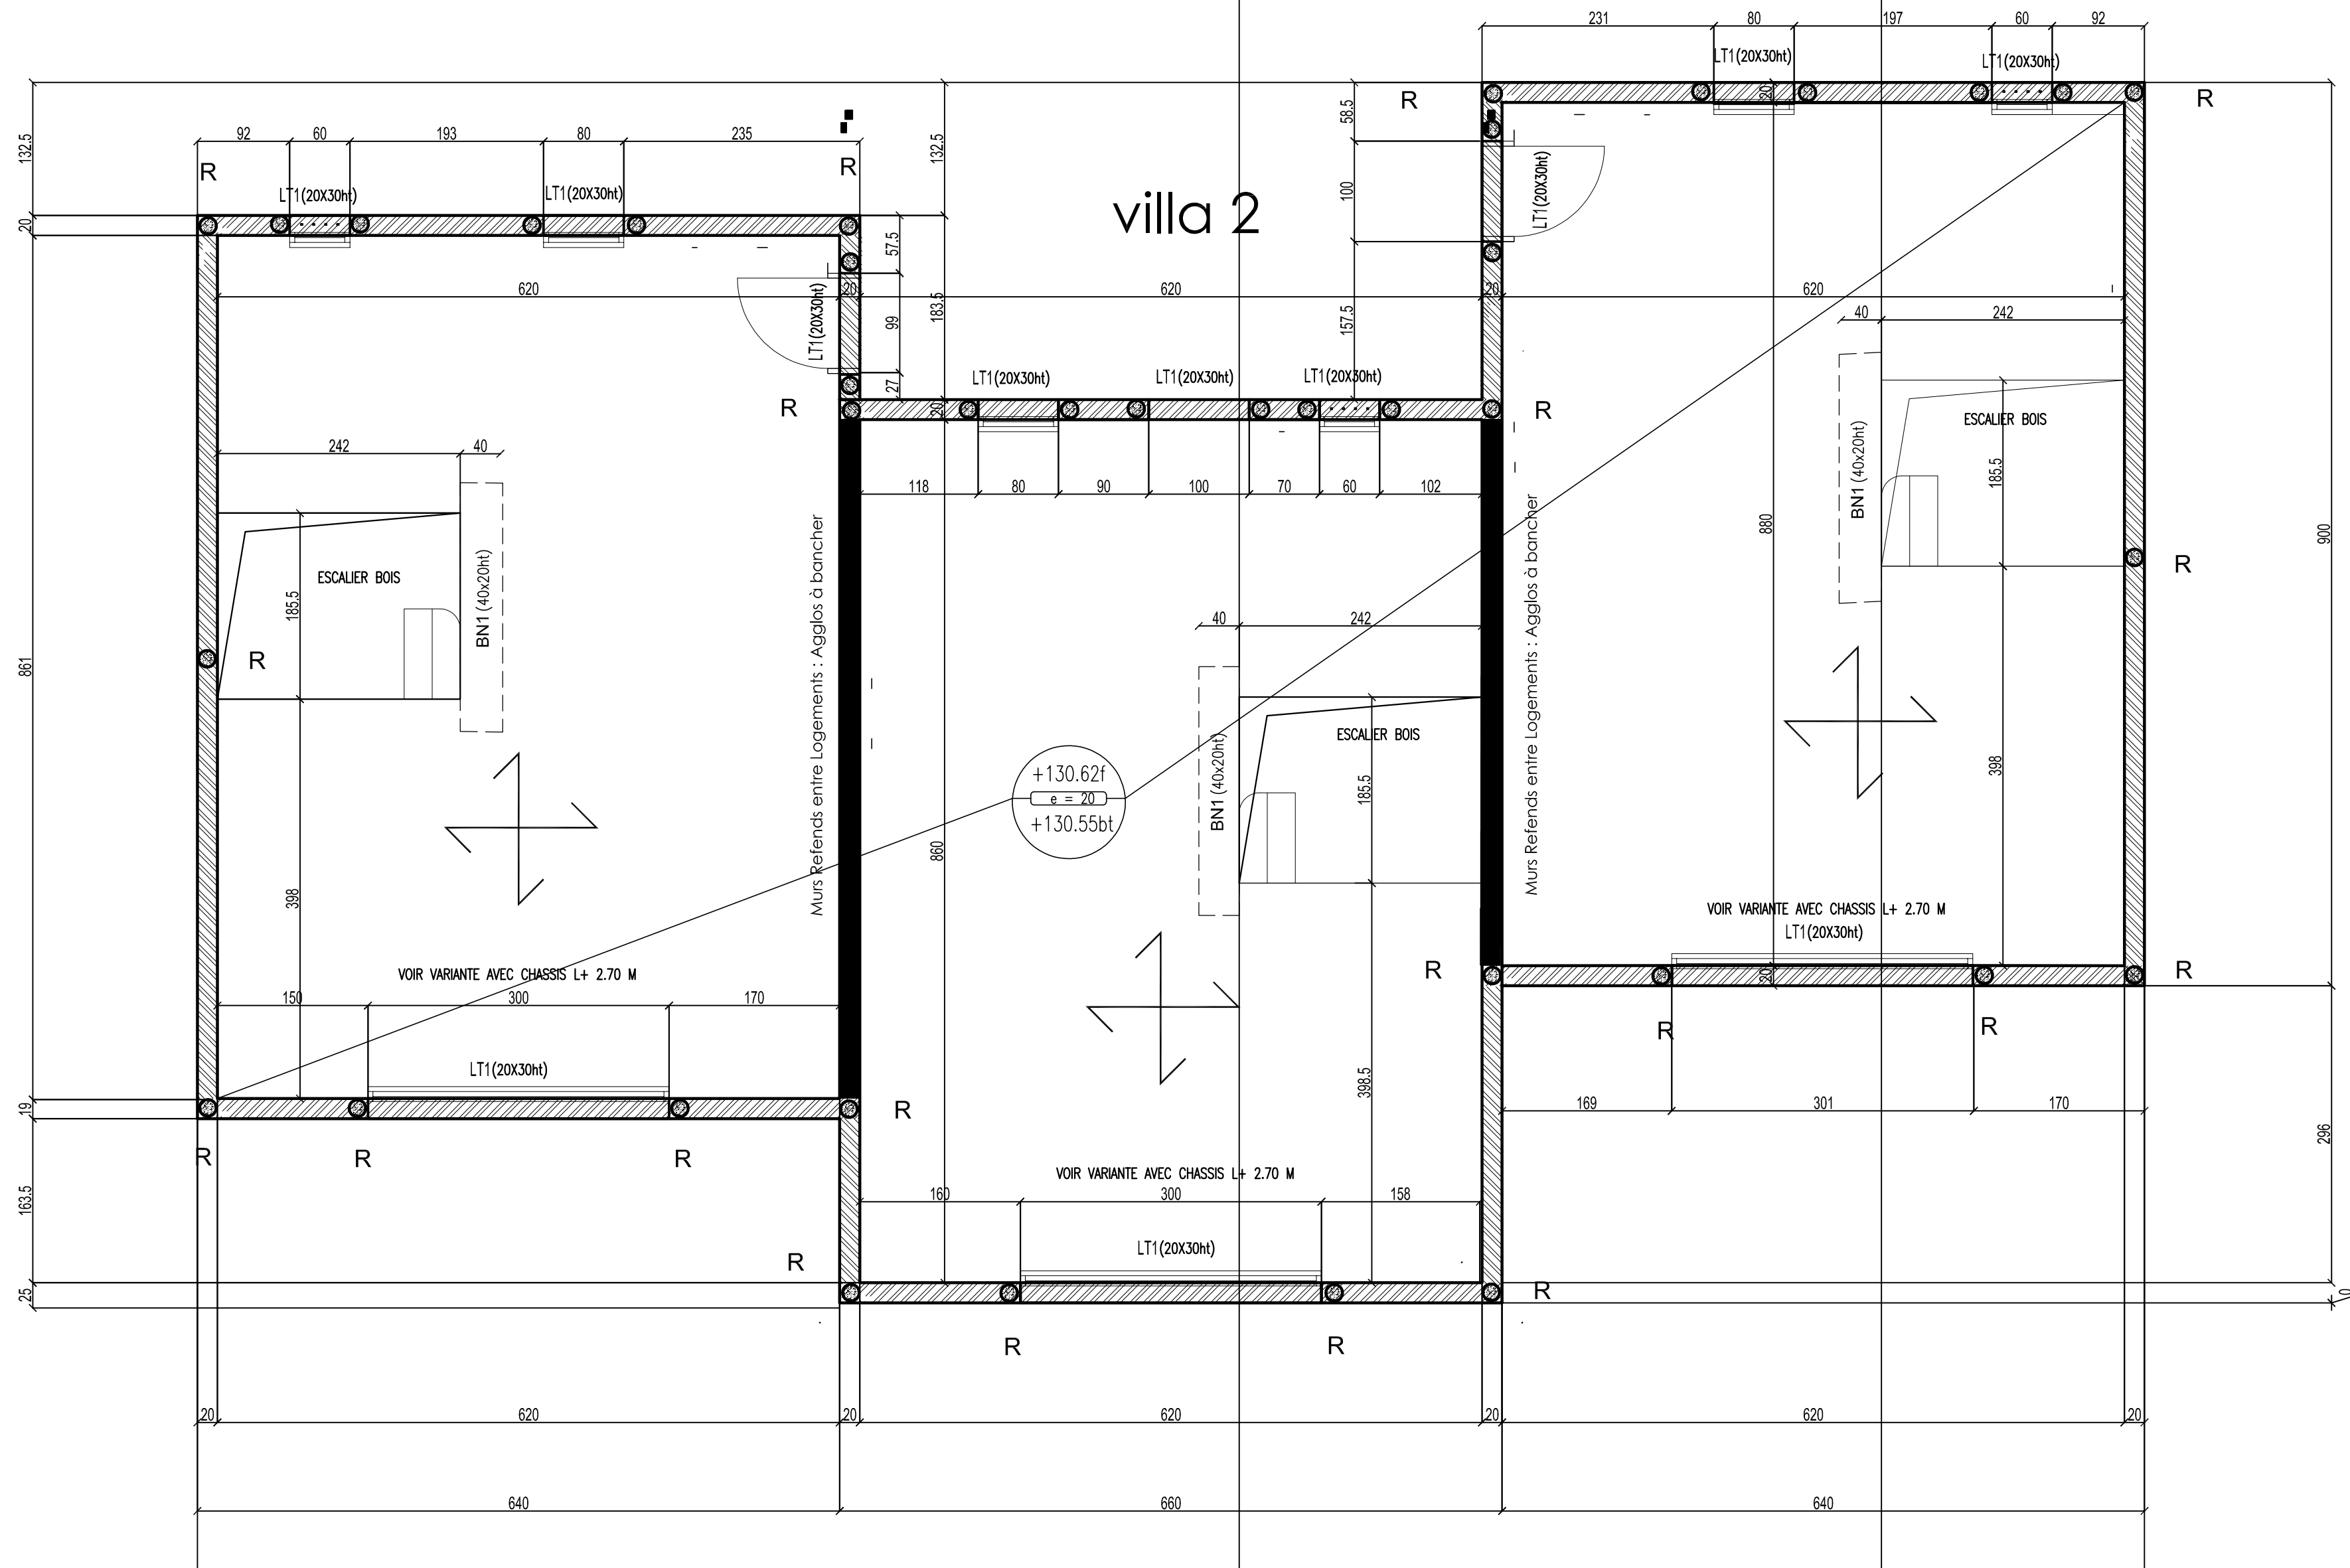

HT DES ETAGES / COMBLES
Murs Refends entre Logements : Agglos à bancher
villa 1 villa 2 villa 3

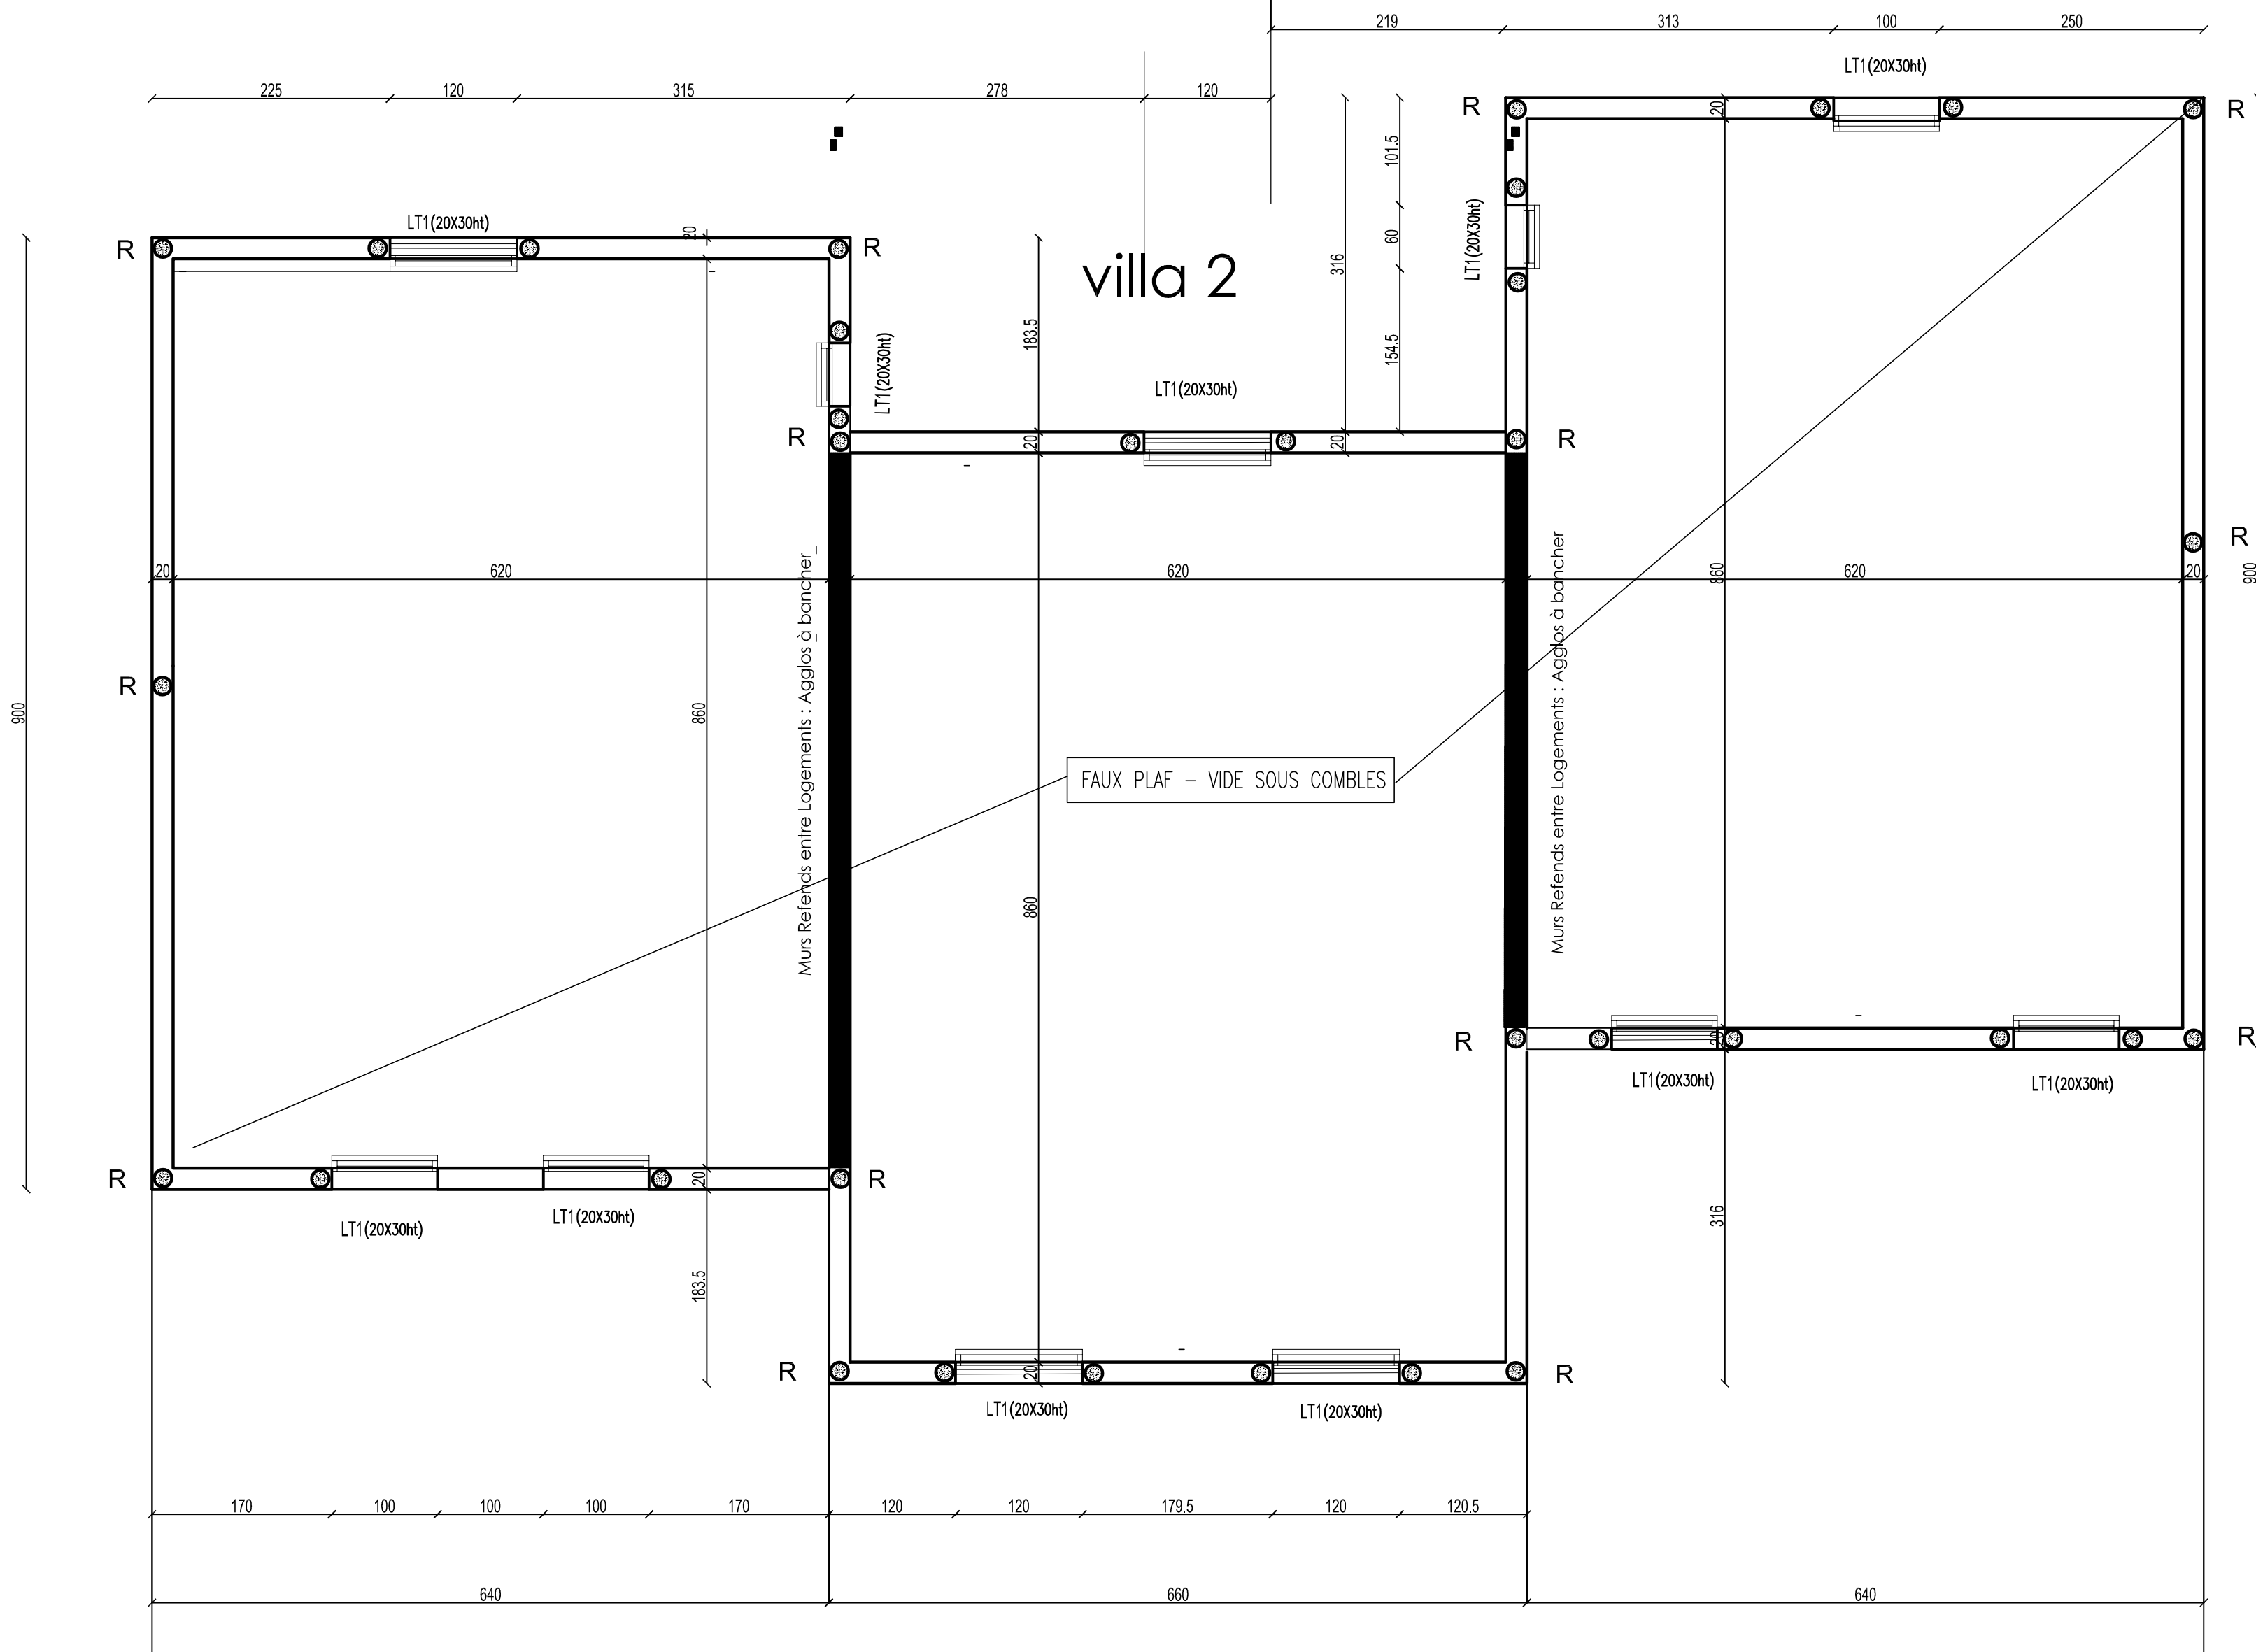


LEGENDE	MENTIONS
	NON ELEMENTS
	PI Plancher Vitré
	CV Couvre Vitré
	VS Vitré Supérieur
	BN Bords Murs
	B Plancher
	VSD Vitré Supérieur sur Dalle
	P Plancher

DOCUMENTS DE REFERENCES			
ORIGINE DOCUMENT	OBJET	N° DOCUMENT	DATE
PLANS ARCHITECTE	Plan d'Etat	18105_DCE_42	10/10/2025
	Plan d'Etat		
	Plan d'Etat		
	Plan d'Etat		
	Plan d'Etat		
	Plan d'Etat		
	Plan d'Etat		

HYPOTHESES DE CALCUL (charges en daN/m²)									
CHARGES S'Y RATTACHANT	TYPE	COLORANTE	S1	S2	S3	S4	S5	S6	S7
Charges permanentes - PP Plancher + Revet Sol	G	500 daN	.	.	.	.	.	.	.
Charges	G	50 daN	.	.	.	.	.	.	.
Surcharge d'exploitation	Q	150 daN	.	.	.	.	.	.	.
Surcharge d'impact	G	.	.	.	.	.	.	.	.

BETON: fck = 25 MPa (selon mention contraire sur plan)	fcm = 32 MPa	TRELLIS SOULEES: (A) et (B) 300	fyk = 500 MPa
PROFILAGE: 15 cm		TRELLIS SOULEES: (A) et (B) 300	fyk = 500 MPa
COUPE REU: 1 m		S 300 (Type B) pour treillis soudés	fyk = 500 MPa
ZONE DE SISMOTITE: - ZONE 3		ALCANTARA: (selon mention contraire sur plan)	fyk = 500 MPa
CLASSE DE SOL: - CLASSE 4			fyk = 500 MPa
FONDATEURS: Contraintes admissibles = 2,5 Bars - Suivant étude GEC - CSIRO du 06/02/2025			fyk = 500 MPa

COUPES PLANS ARCHITECTE

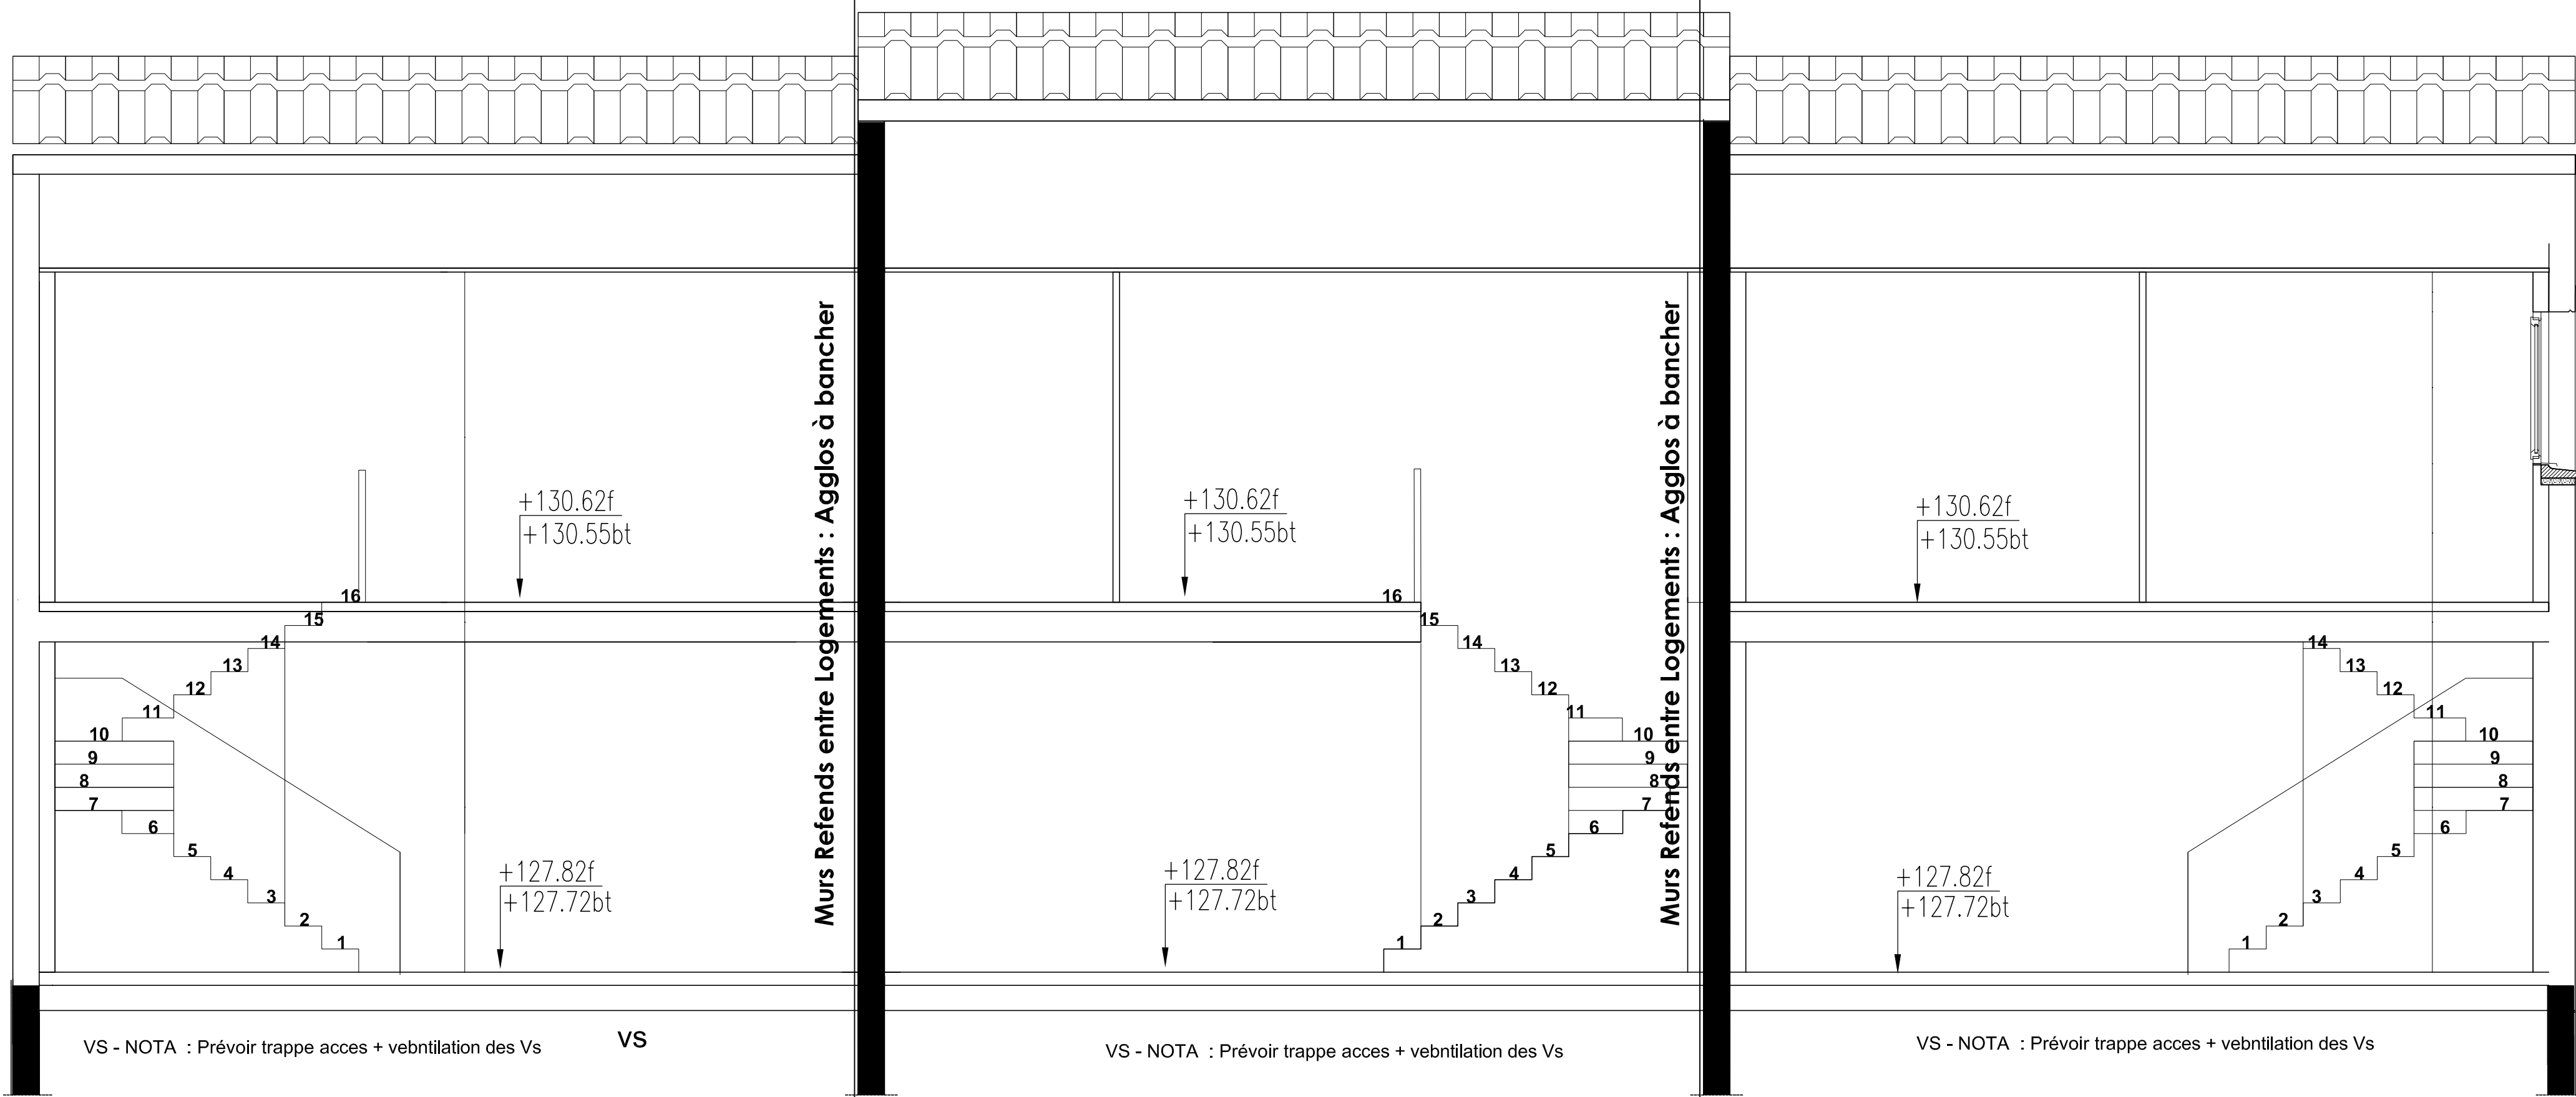


villa 1

villa 2

villa 3

COUPES PLANS ARCHITECTE

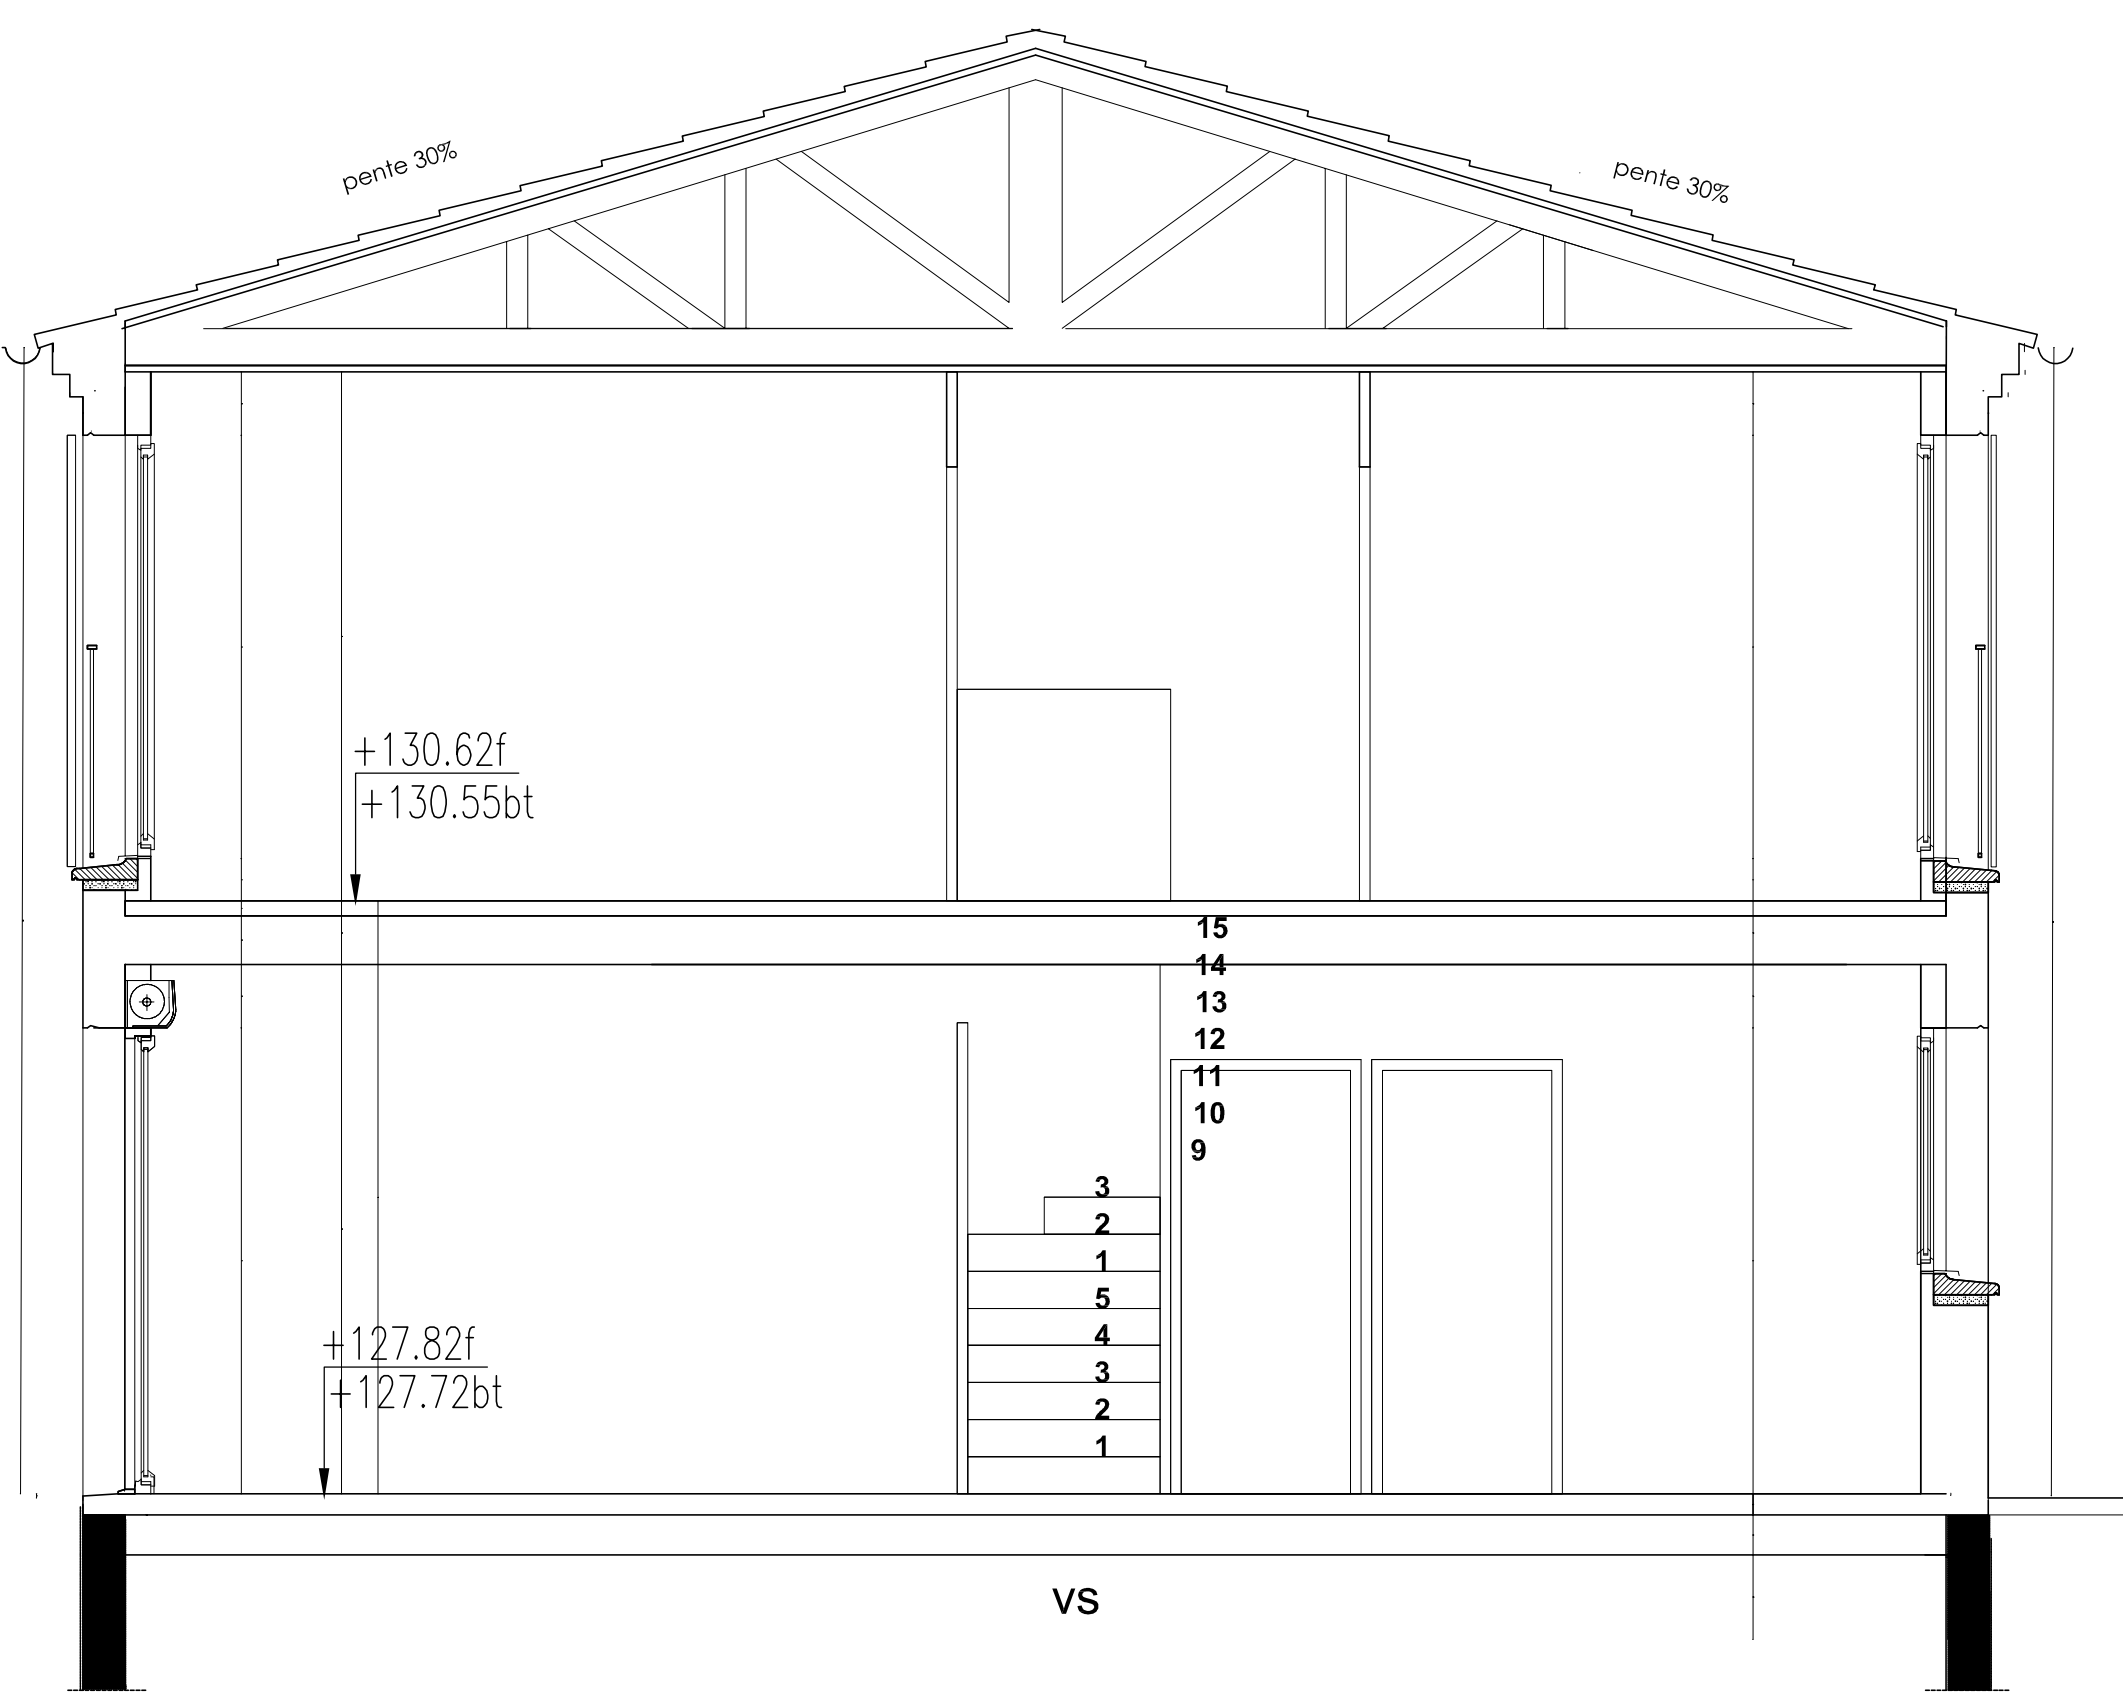

villa 1

E					
D					
C					
B	09/06/2026	MB	MB		Mise à jour / Cour anglaise accès VS.
A	21/05/2026	MB	MB		Mise à jour suite réunion du 20/05/2026
O	08/05/2026	MB	MB		PREMIERE EMISSION
Ind	Date	Rédaction	Vérification	Approbation	MODIFICATIONS / OBSERVATIONS

SCCV GRANDE TERRE
18 VILLAS A AUREILLE

MAITRE D'OUVRAGE

SCCV GRANDE TERRE
837 BIS AV DE PARIS
LA SEYNE SUR MER

MAITRE D'OEUVRE

AXXION

41 Rue Ribas
13770 VENELLES

ARCHITECTE

MICHEL CHAUVET &
CATHERINE CARNAZZA
ARCHITECTES

BUREAU DE CONTROLE

ALPES CONTROLES

67 Rue Ollioules
83140 SIX FOURS

ENTREPRISE

A Désigner

BET STRUCTURE

BET BMC

49 Domaine du val des pins
2 Montee Belle France
13015 MARSEILLE

VILLAS 1-2-3 & VILLAS 4 à 11
COFFRAGE HT RDC & HT 1 ER
COUPES ARCHI

Rédaction: E.H	Signature	Vérification: B.B	Signature	Approbation:	Signature
		Date: 08-05-2026		Date:	

Echelle: 1:50	Format: A3	Version: 1	Classe: DCE	Classe: COF	Classe: 00120	Classe: B
ECS	7	DCE	COF	00120	/	B

Ce document est la propriété intellectuelle du BET BMC
Il ne saurait être reproduit ou communiqué à des tiers sans son autorisation.