



Murs sousbassements : Agglos à bancher

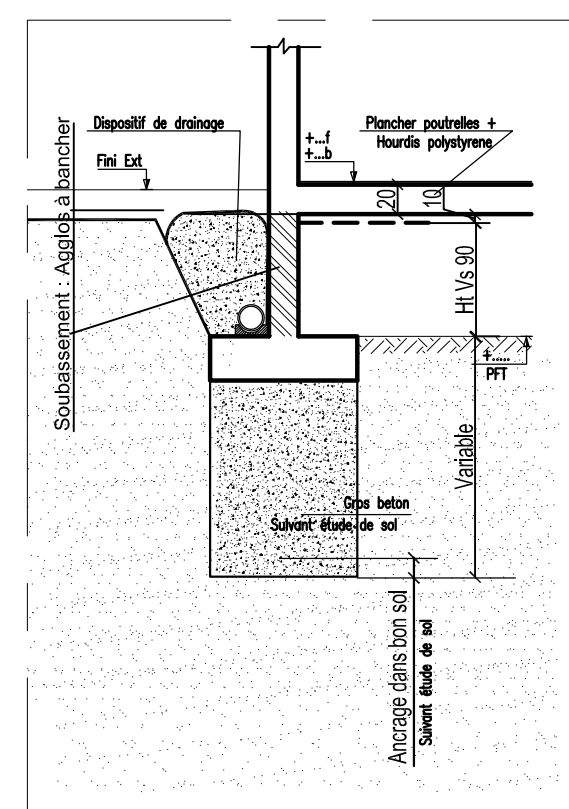

COUPE TYPE STRUCTURE

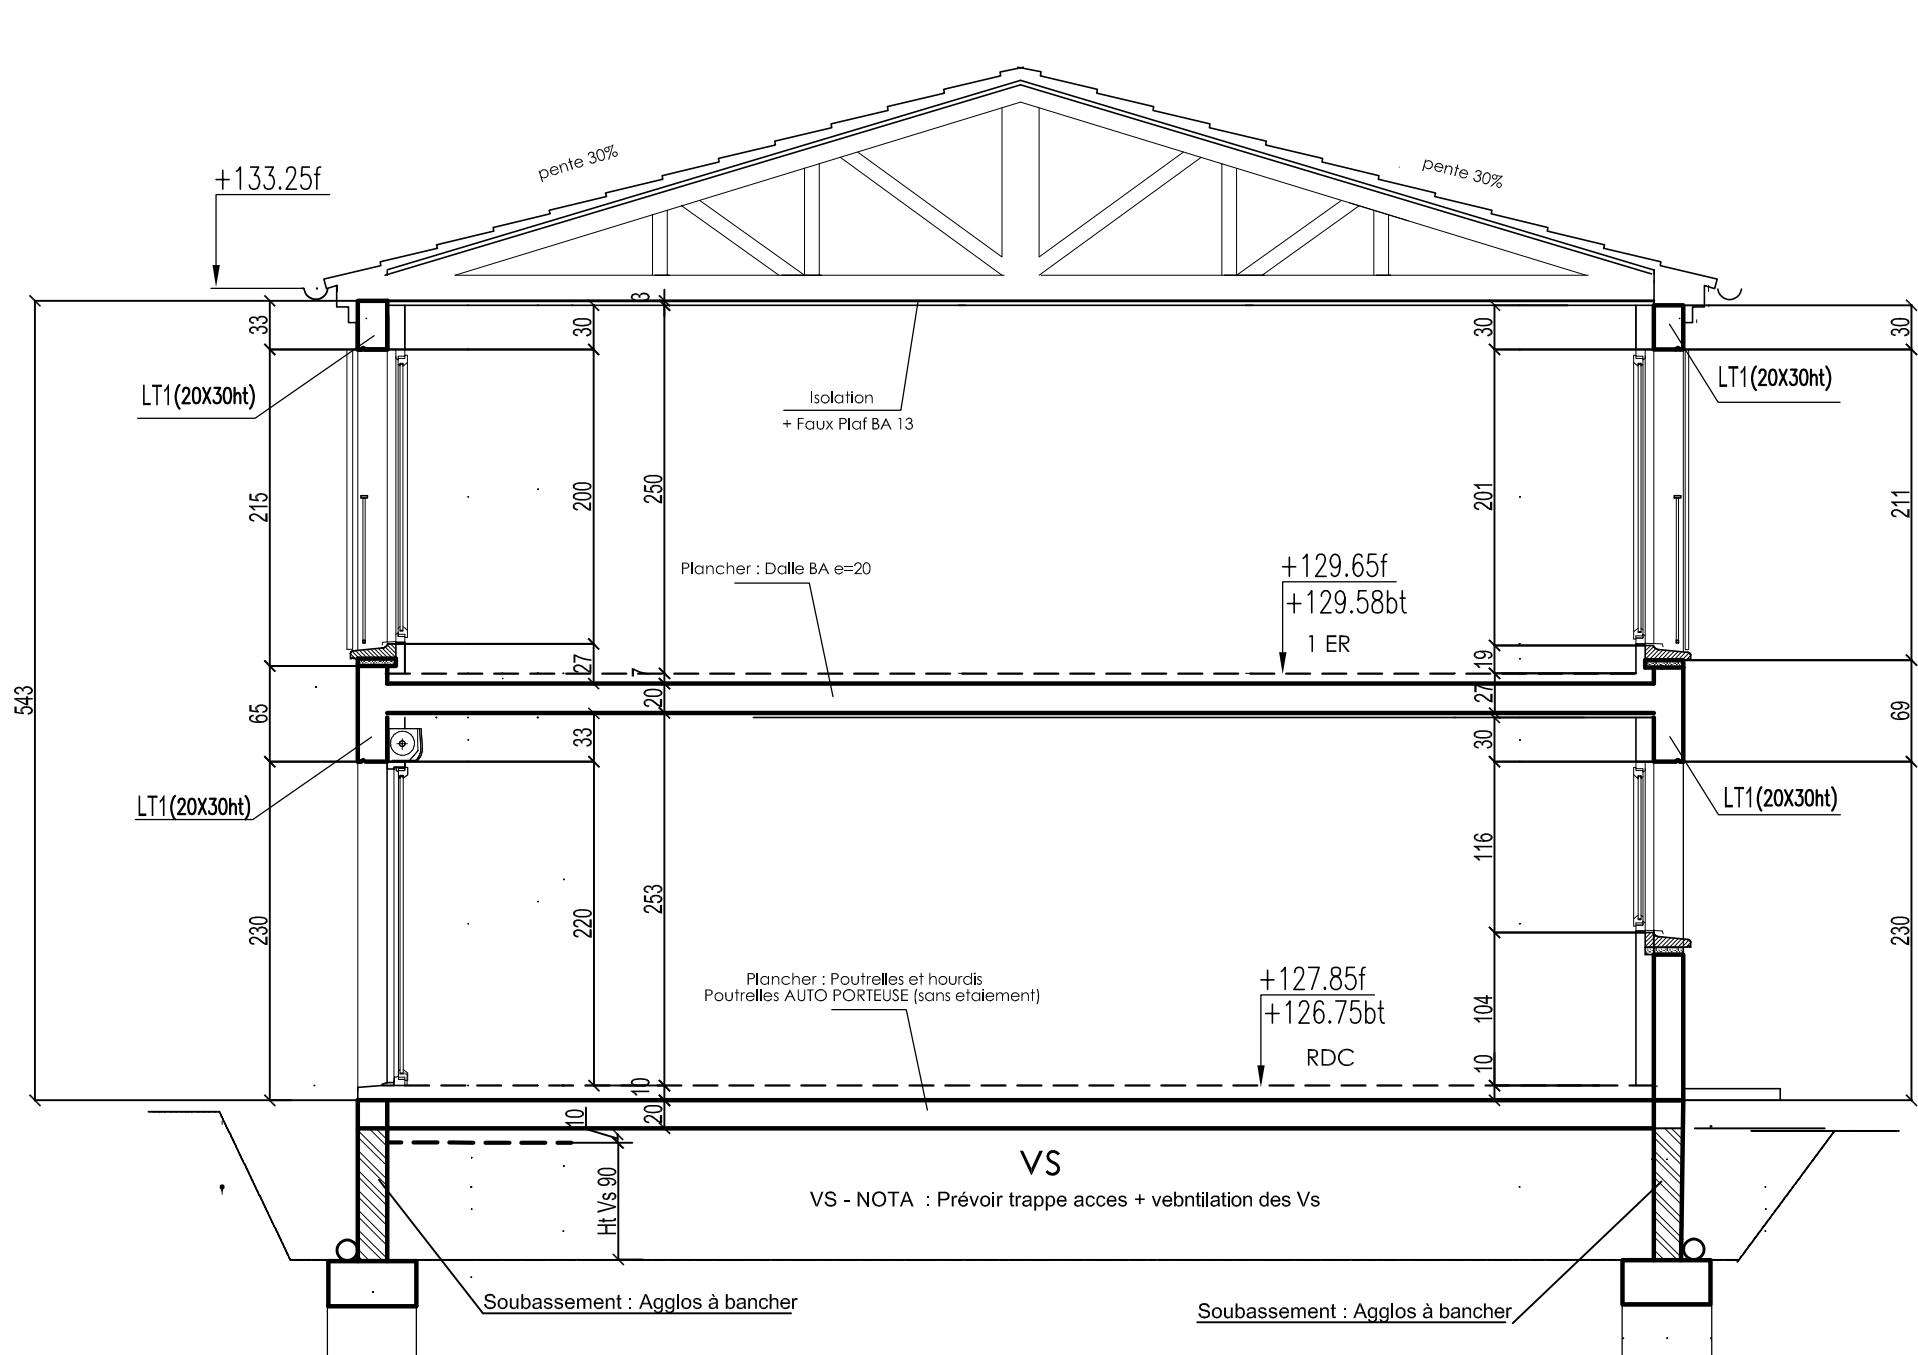

LEGENDE		MENTIONS	
	Mur BA	NON	ELEMENTS
	Mur Sd de litrage	PI	Plaque Voile
	avec option mur BA	CI	Croûte Voile
	Premur	VD	Voile Grapau
A	Atterre dans l'eau	VS	Voile Supendu
		BN	Bande Noyau
		B	Plaque
		VSD	Voile Repère sur Dalle
		P	Pierres


DOCUMENTS DE REFERENCES			
ORGANE DOCUMENT	OBJET	N° DOCUMENT	DATE
PLANS ABSTRACTES	Plan DCE	81132_DOC_02	17/11/2025
	Plan Normative PMS		
	Exercice		
	Scénario Normalisés		
	Portance		
	Forme 2D - 3D		
	Remarques		
	Dimensiones Plan-Paire		

HYPOTHESES DE CALCUL (charges en daN/m²)							
CHARGES & SURCHARGES	TYPE	COURANTE	1951	1952	1953	1954	1955
Charges permanentes - PP Plancher + Revet Sol	G	500 daN	-				
Others	G	50 daN	/				
Surcharge Evén-Exploitation	Q	150 daN	-				
Surcharge jardin	G	/					

Myrs Refends entre Logements : Agglos à bancher



Murs Refends entre Logements : Agglos à bancher

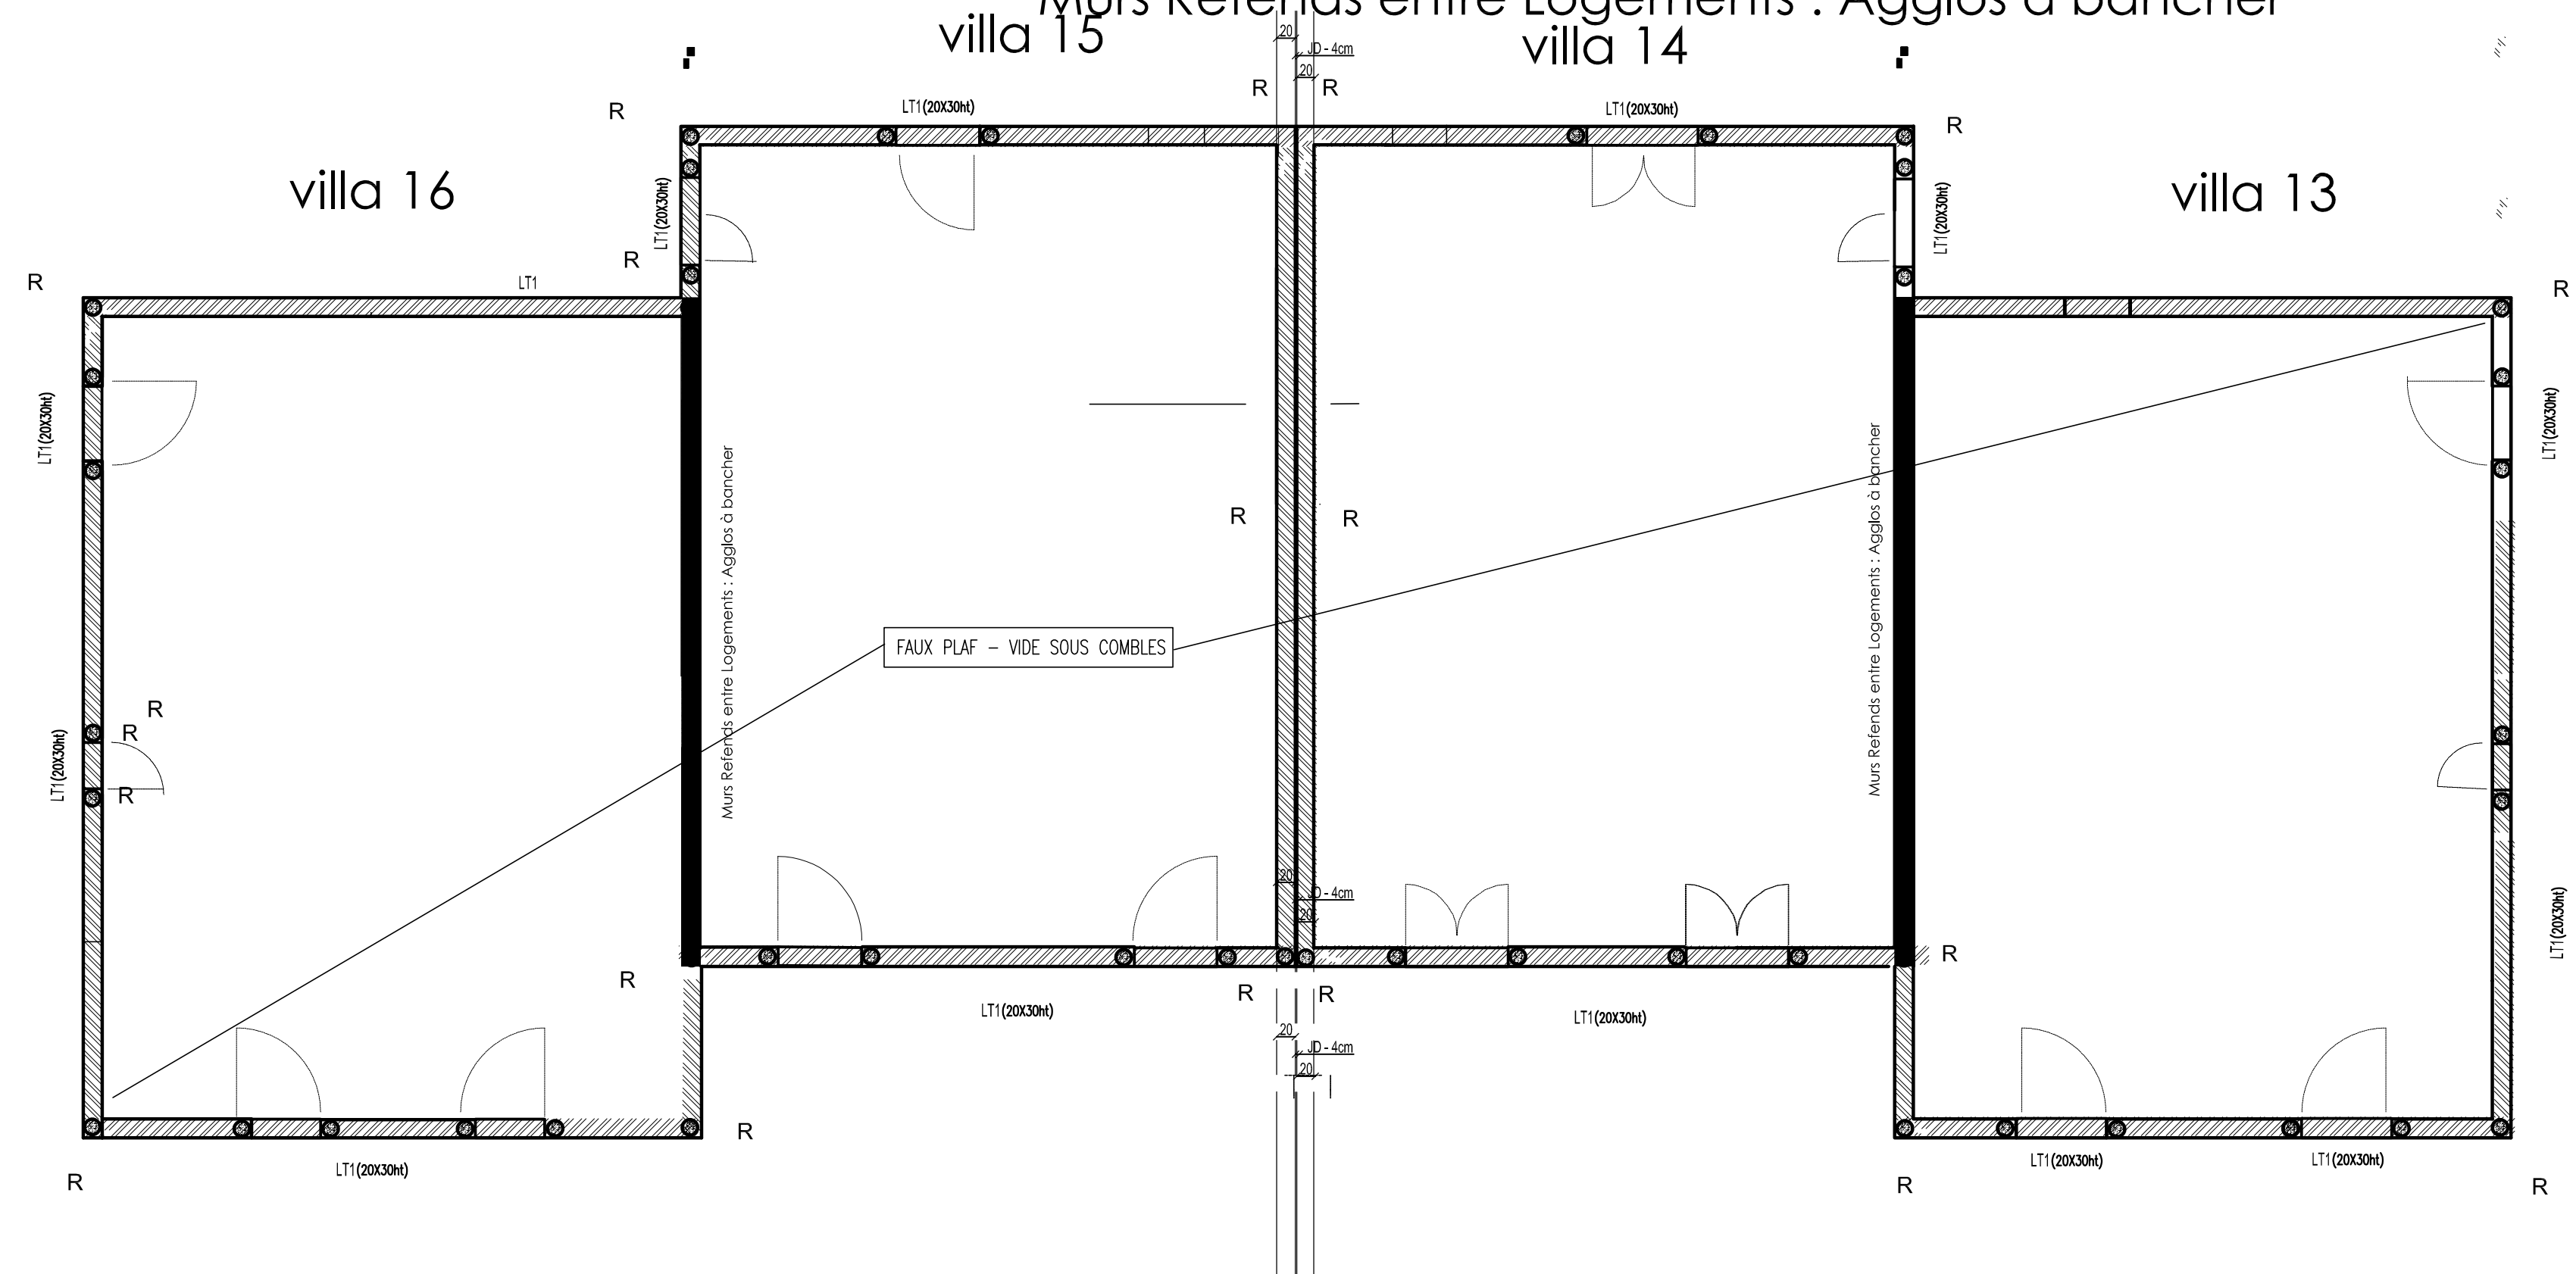[illegible]

SECTION : 10 x 25 cm (selon montage conforme au plan)	f = 20MPa	TRÉLIS SOUS-ÉPAILLAGE : (Métal) TS3, 500	14-50MPa
EMBOÎTAGE : 2,5 cm			TS4, 500 - 14-50MPa
COUPE FEU : 1h			S 500 : Type B pour trafic autorisé
ZONE DE SONNÉTTE - ZONE :			AGS25 : Heule Adhesione (M, S30 - Type B) pour 2511mm
CLASSE DE SOL - CLASSE A			(Type B) pour 20-16mm
FOUNDATIONS : Contraintes admissibles = 0,5 Bars - Solvent étuvé GEC- GIPPO à 100/60/200			

E				
D				
C				
B	09/06/2026	MB	MB	Mise à jour / Cour anglaise accès VS.
A	21/05/2026	MB	MB	Mise à jour suite reunion du 20/05/2026
0	08/05/2026	MB	MB	PREMIERE EMISSION
nd	Date	Rédaction	Vérification	Approbation
				MODIFICATIONS / OBSERVATIONS

SCCV GRANDE TERRE
18 VILLAS A AUREILLE

MAITRE D'OUVRAGE

SCCV GRANDE TERRE
837 BIS AV DE PARIS
LA SEYNE SUR MER

MAITRE D'OEUVRE

AXXION
41 Rue Ribas
13770 VENELLES

ARCHITECTE

**MICHEL CHAUVET &
CATHERINE CARNAZZA
ARCHITECTES**

BUREAU DE CONTROLE

ALPHESS CONTROLS

67 Rue Ollioules
83140 SIX FOURS

ENTREPRISE

A Désigner

BET STRUCTURE

BET BMC

49 Domaine du val des pins
2 Montee Belle France
13015 MARSEILLE

VILLAS 13 à 16
COFFRAGE FONDATIONS ET TOUS NIVEAUX
COUPES ARCHI

Rédaction: E.H	Signature	Vérification: B.B	Signature	Approbation:	Signature
		Date :06-05-2026		Date :	

Extrait		1:50									
Créateur		Zones		Nature		Type de document		N° de document		Révision	
ECS		/		DCE		COF		0 0 3 0		/ B	

**Ce document est la propriété intellectuelle du BET BMC
Il ne saurait être reproduit ou communiqué à des tiers sans son autorisation**