


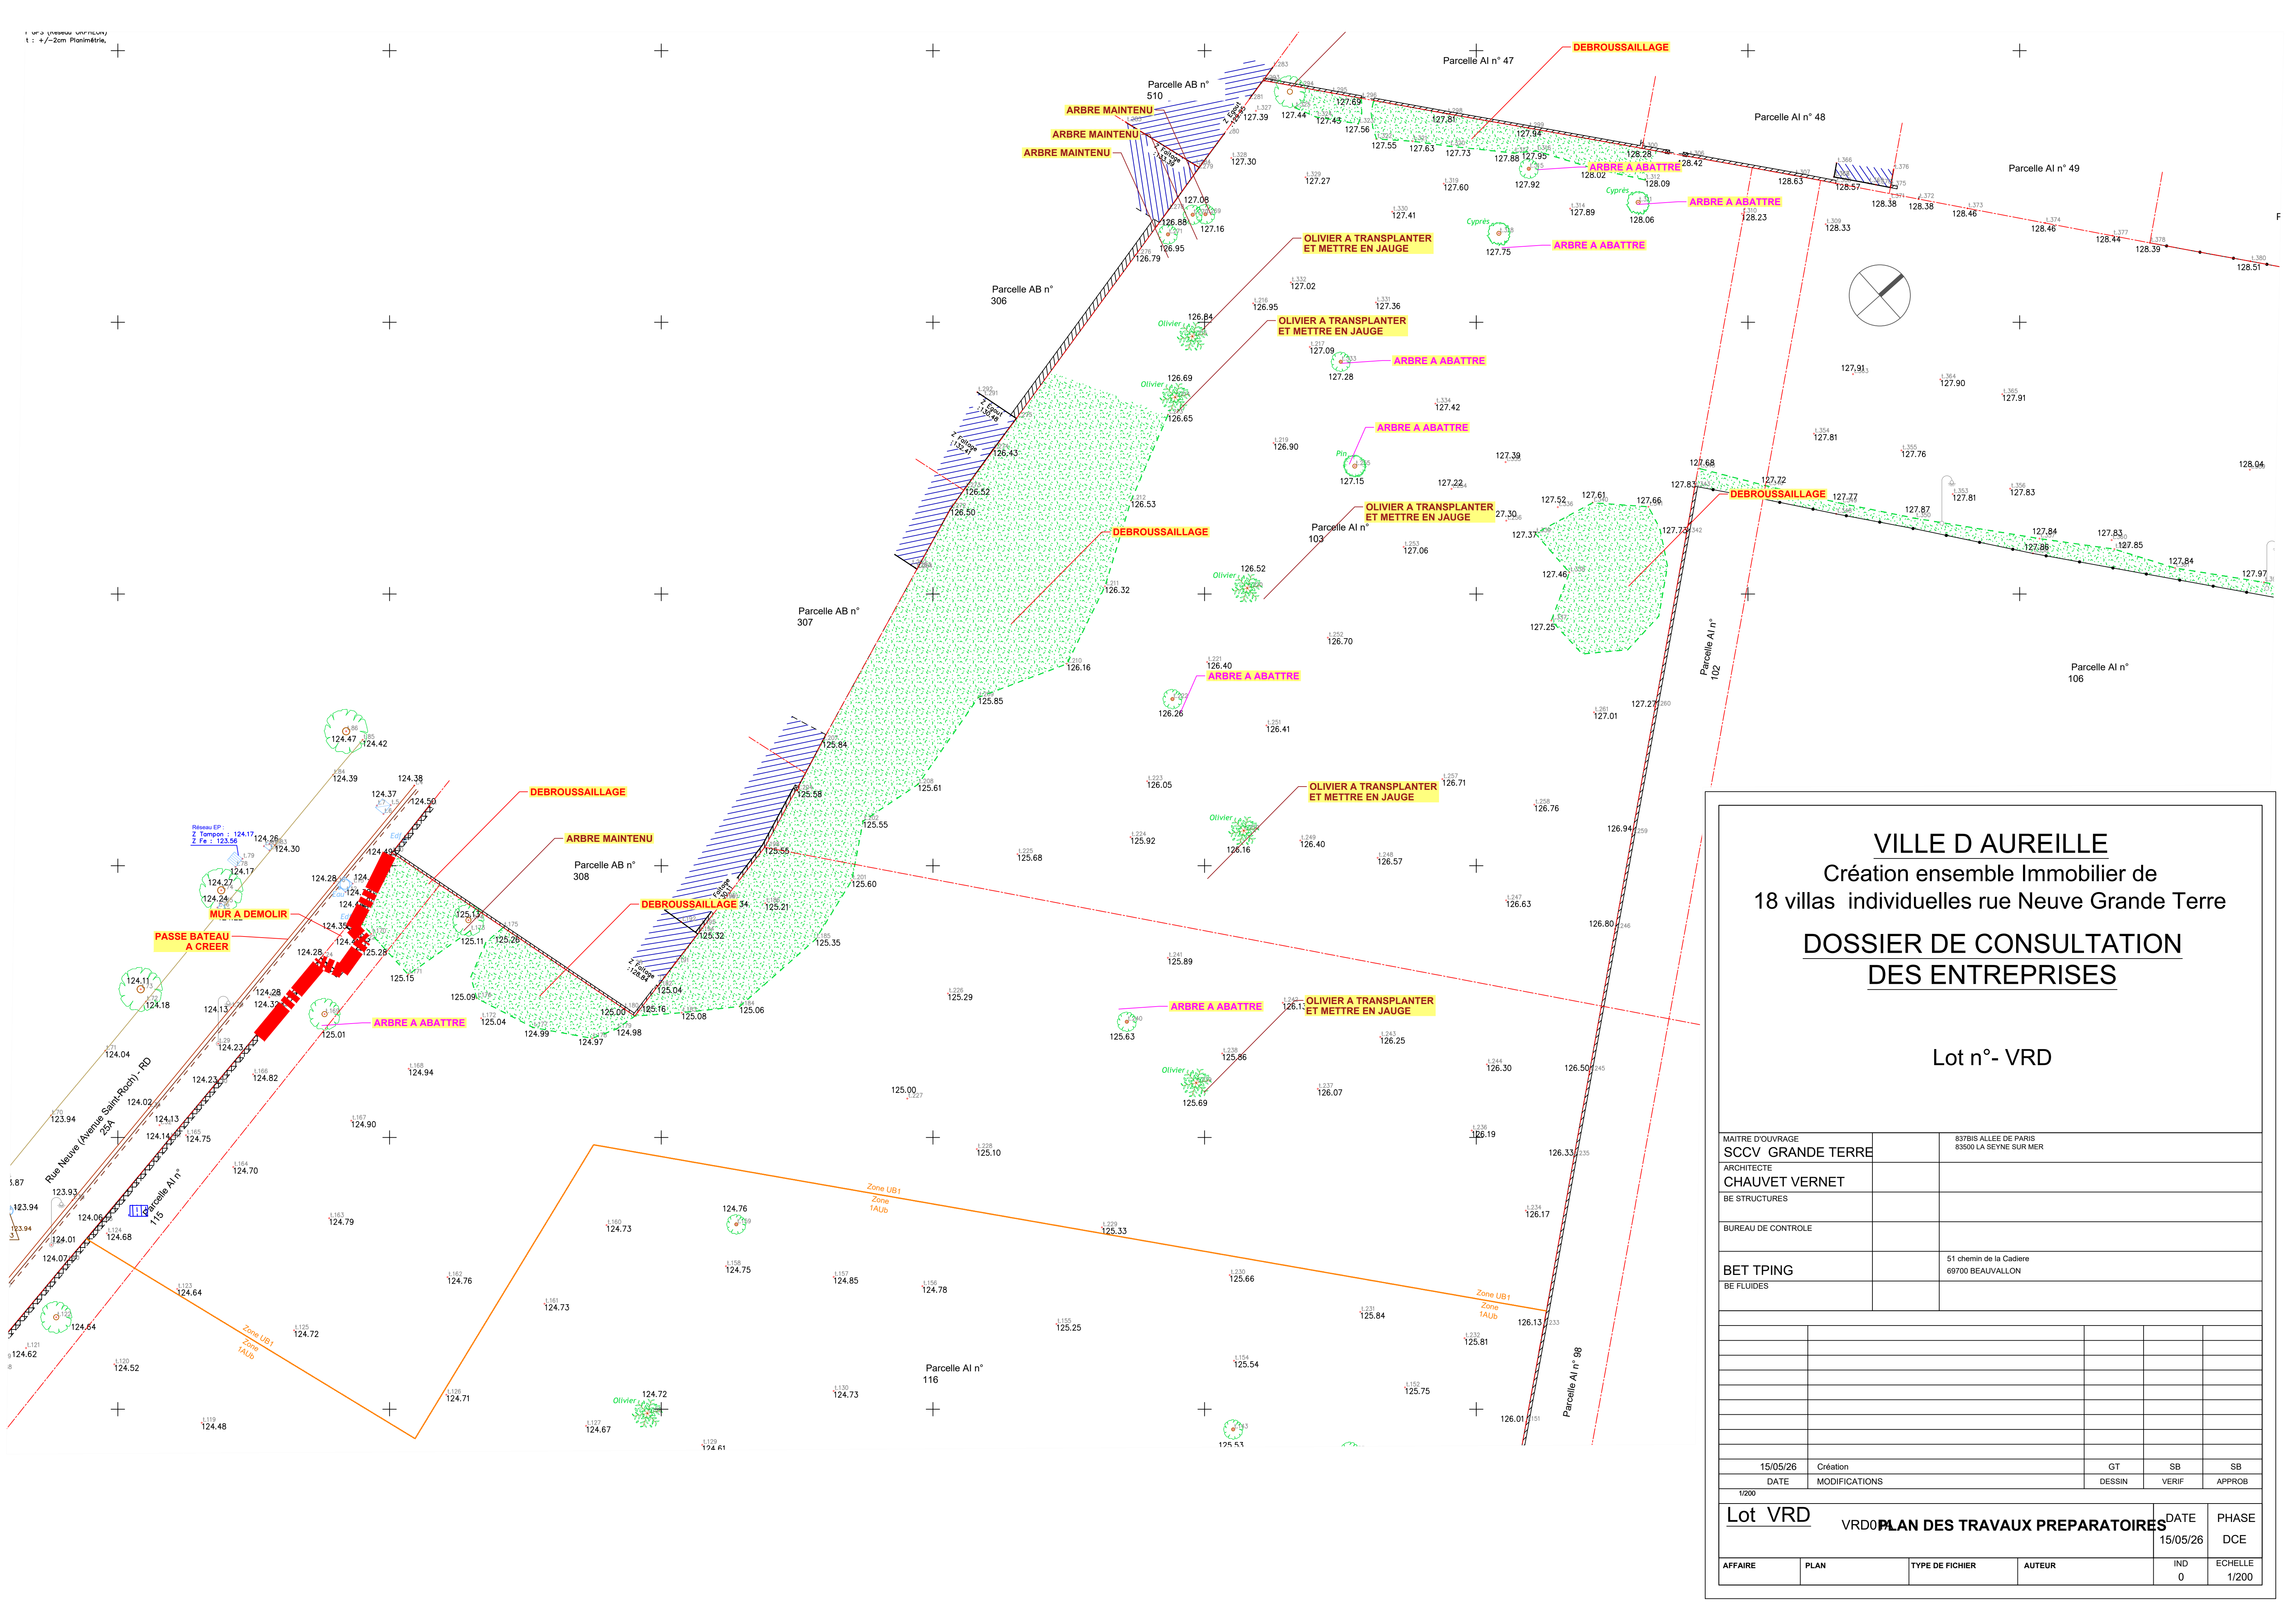

VILLE D AUREILLE

Création ensemble Immobilier de 18 villas individuelles rue Neuve Grande Terre

DOSSIER DE CONSULTATION DES ENTREPRISES

Lot n° - VRD

MAÎTRE D'OUVRAGE		837BIS ALLEE DE PARIS 83500 LA SEYNE SUR MER		
ARCHITECTE				
CHAUVET VERNET				
BE STRUCTURES				
BUREAU DE CONTROLE				
BET TPING		51 chemin de la Cadiere 69700 BEAUVALLON		
BE FLUIDES				
15/05/26	Création	GT	SB	SB
DATE	MODIFICATIONS	DESSIN	VERIF	APPROB
Lot VRD		VRD01PLAN DES TRAVAUX PREPARATOIRES		DATE 15/05/26
PHASE DCE				
AFFAIRE	PLAN	TYPE DE FICHIER	AUTEUR	IND 0
ECHELLE 1/200				