


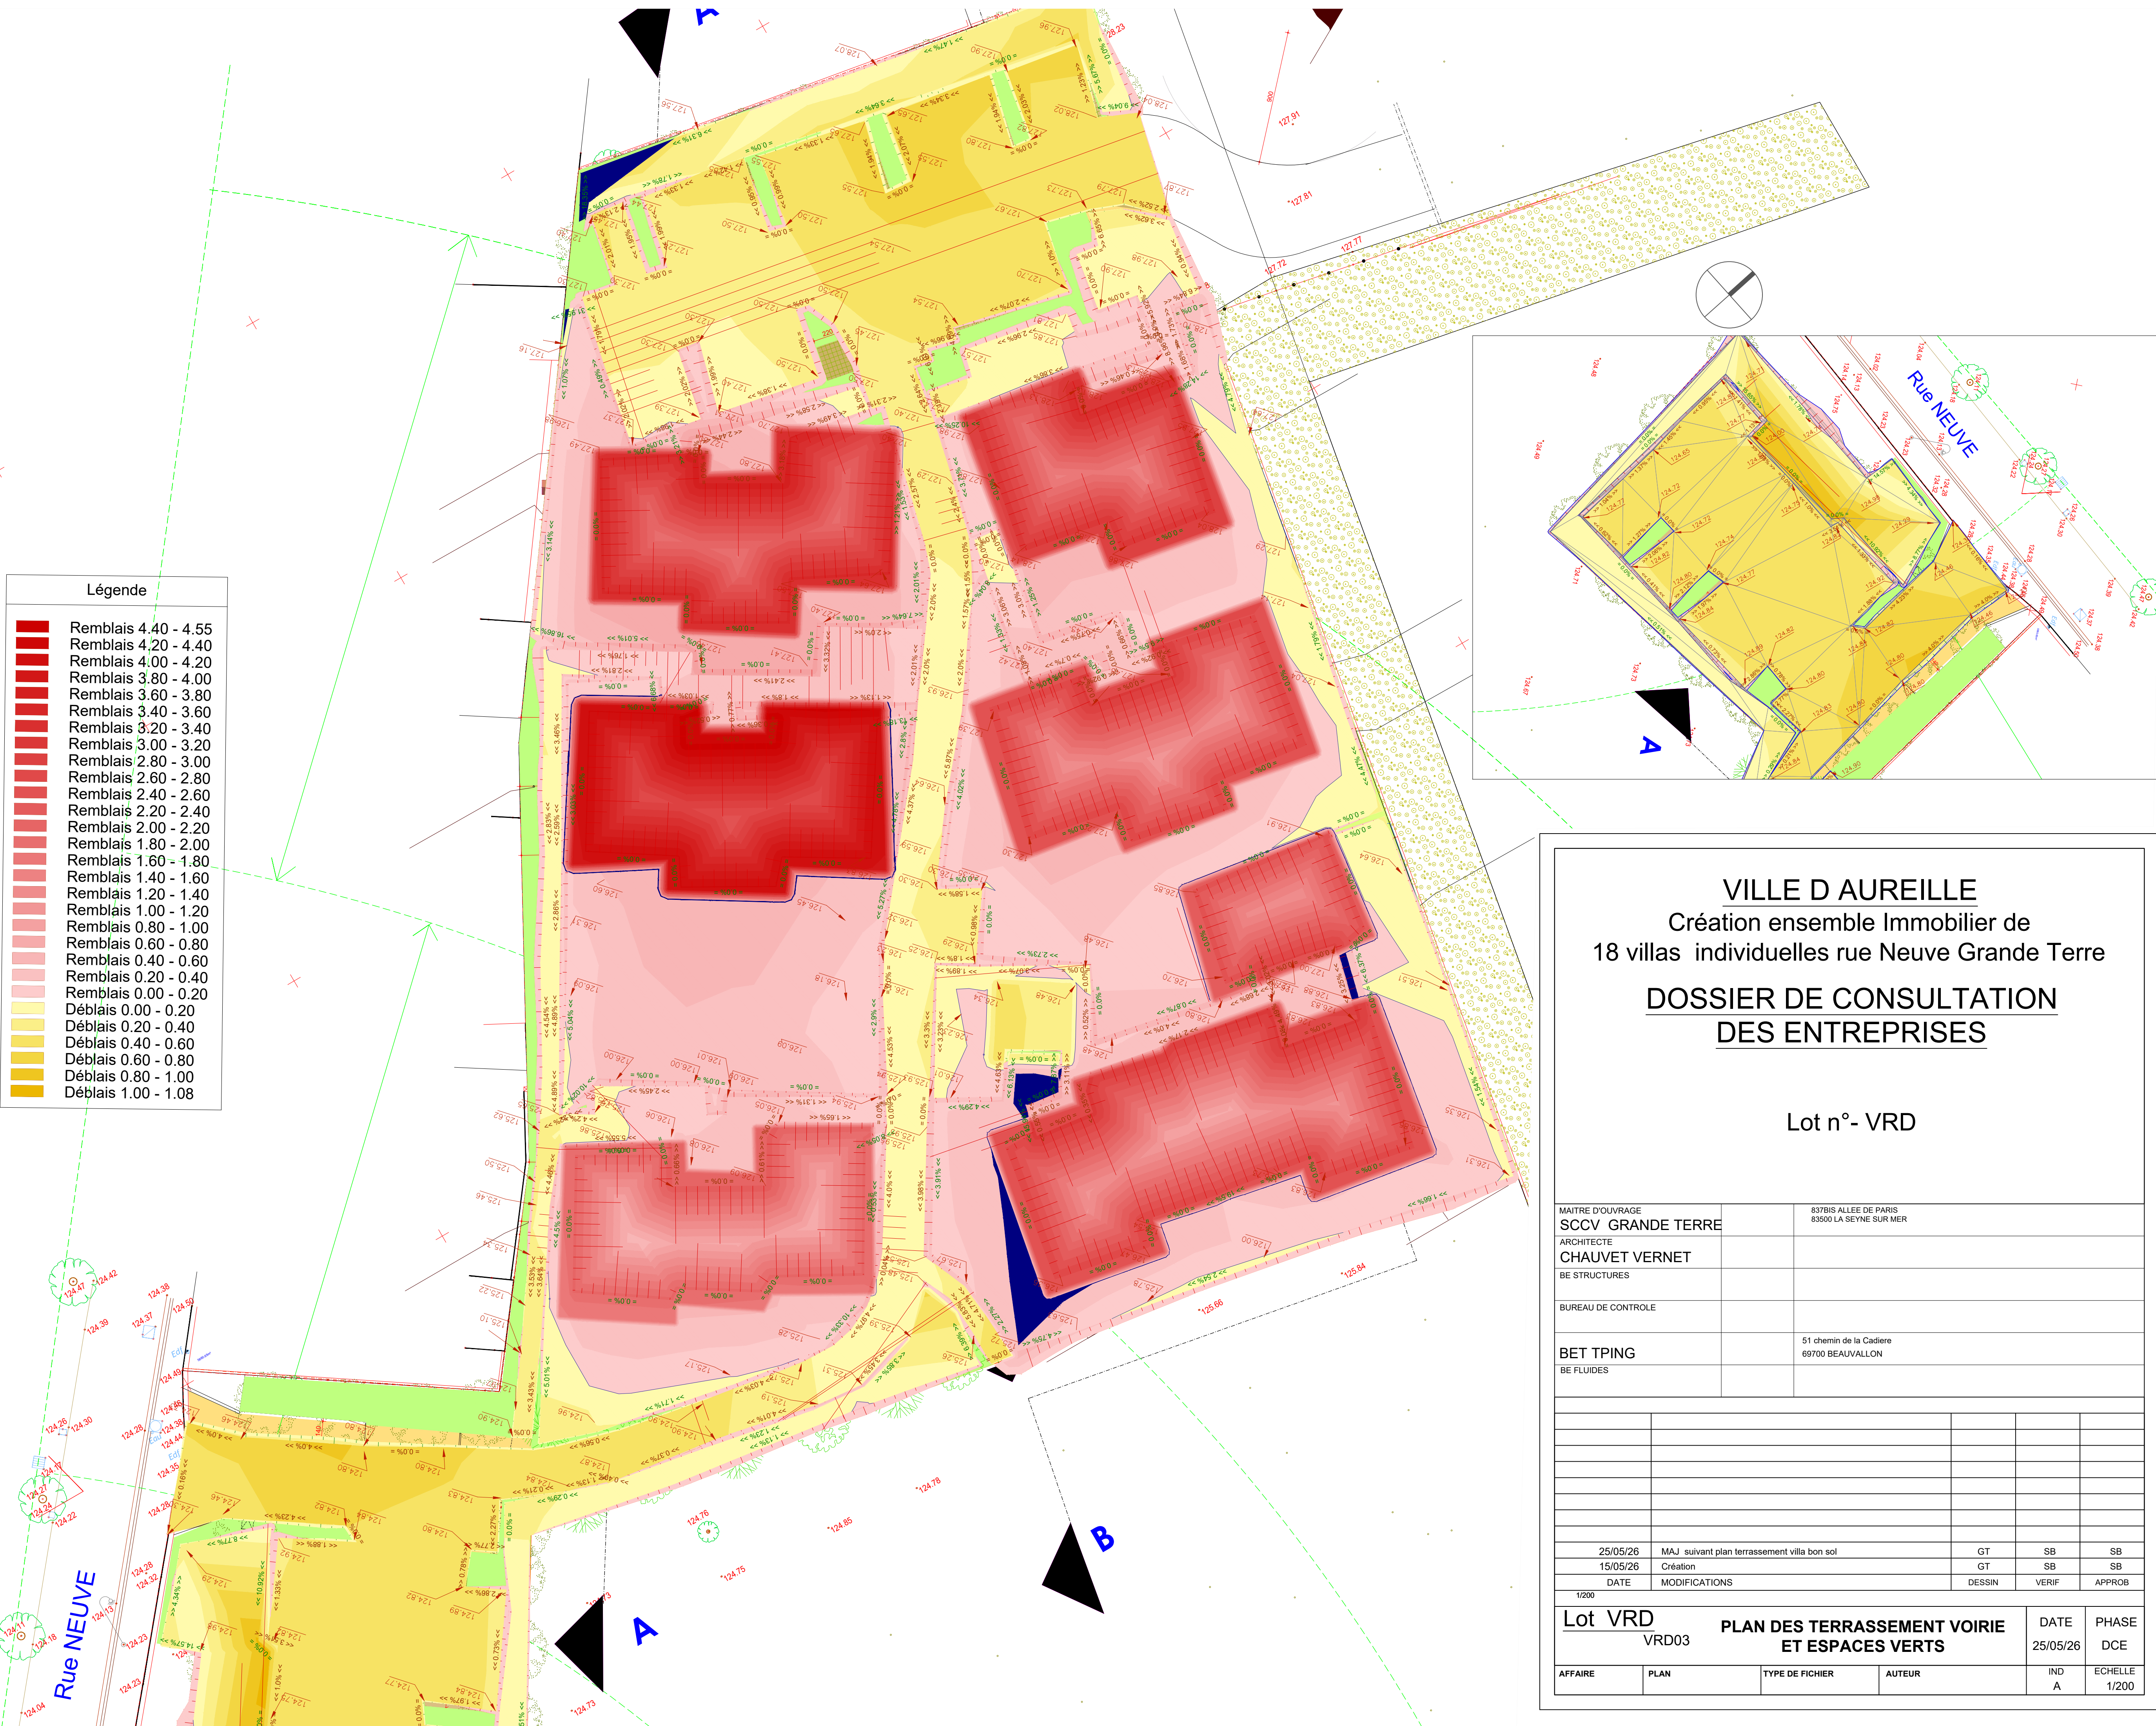

Légende

Remblais 4.40 - 4.55

Remblais 4.20 - 4.40

Remblais 4.00 - 4.20

Remblais 3.80 - 4.00

Remblais 3.60 - 3.80

Remblais 3.40 - 3.60

Remblais 3.20 - 3.40

Remblais 3.00 - 3.20

Remblais 2.80 - 3.00

Remblais 2.60 - 2.80

Remblais 2.40 - 2.60

Remblais 2.20 - 2.40

Remblais 2.00 - 2.20

Remblais 1.80 - 2.00

Remblais 1.60 - 1.80

Remblais 1.40 - 1.60

Remblais 1.20 - 1.40

Remblais 1.00 - 1.20

Remblais 0.80 - 1.00

Remblais 0.60 - 0.80

Remblais 0.40 - 0.60

Remblais 0.20 - 0.40

Remblais 0.00 - 0.20

Déblais 0.00 - 0.20


Déblais 0.20 - 0.40

Déblais 0.40 - 0.60

Déblais 0.60 - 0.80

Déblais 0.80 - 1.00

Déblais 1.00 - 1.08

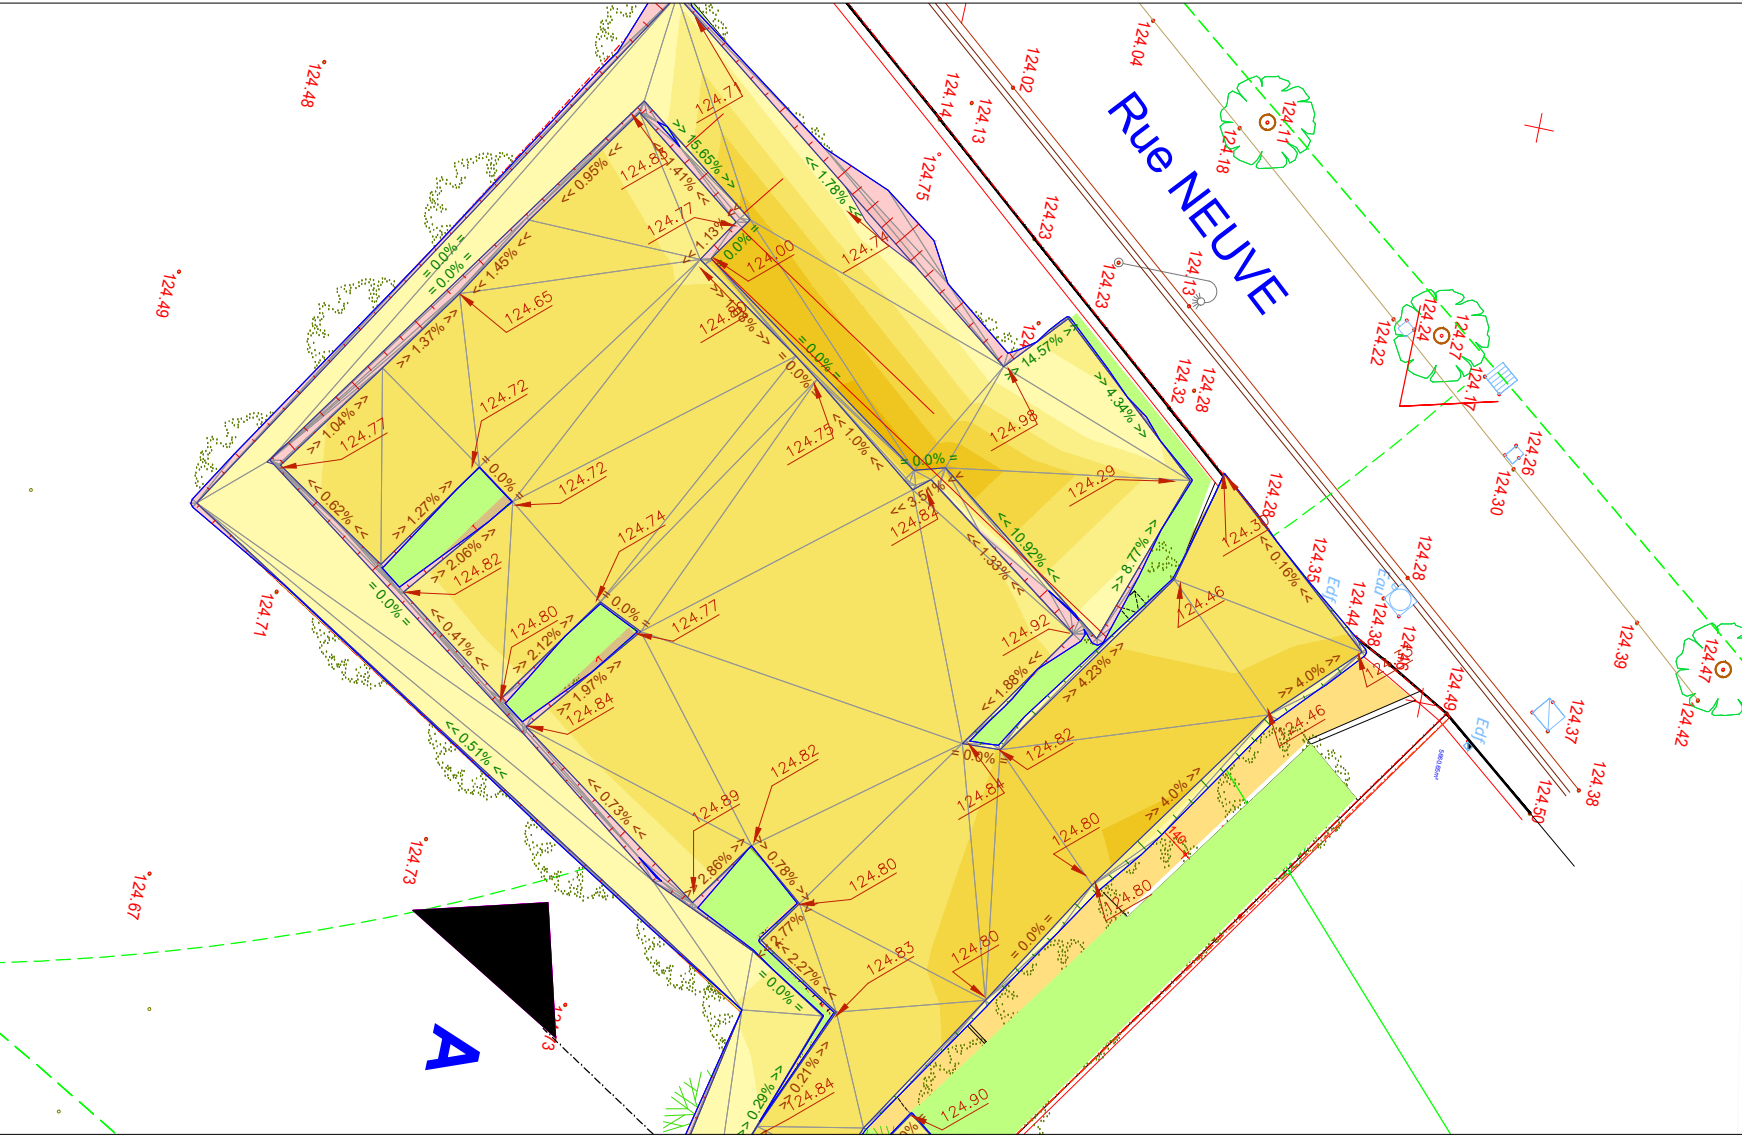

VILLE D AUREILLE

Création ensemble Immobilier de
18 villas individuelles rue Neuve Grande Terre

DOSSIER DE CONSULTATION
DES ENTREPRISES

Lot n° - VRD

MAÎTRE D'OUVRAGE	837BIS ALLEE DE PARIS 83500 LA SEYNE SUR MER
ARCHITECTE	
CHAUVET VERNET	
BE STRUCTURES	
BUREAU DE CONTROLE	
BET TPING	51 chemin de la Cadiere 69700 BEAUVALLON
BE FLUIDES	

25/05/26	MAJ suivant plan terrassement villa bon sol	GT	SB	SB
15/05/26	Création	GT	SB	SB
DATE	MODIFICATIONS	DESSIN	VERIF	APPROB
1/200				

Lot VRD		PLAN DES TERRASSEMENT VOIRIE ET ESPACES VERTS		DATE	PHASE
VRD03				25/05/26	DCE
AFFAIRE	PLAN	TYPE DE FICHIER	AUTEUR	IND A	ECHELLE 1/200