

Ø-x Canalisation PVC CR16 (section-pente x mm/m)
Caniveau L300 P350/440 (raccordement Ø315 PVC)
Caniveau L200 P240

x Canalisation PVC CR16 Ø200 (pente x mm/m)
Canalisation PVC CR16 Ø160

EAU POTABLE

Canalisation principale fonte
Canalisation de branchement PEHD
Canalisation de branchement apres compteur PEHD

BASSE TENSION

Câble de réseau
Câble de branchement 4x35mm² sous fourreau TPCØ75

ECLAIRAGE

Câble U1000R2V sous fourreau TPCØ63
Infrastructure 1 x fourreau TPCØ63

TELECOMMUNICATIONS ET IRVE

Infrastructure réseau 3 x fourreaux PVCØ42/45
Infrastructure branchement 2 x fourreaux PVCØ25/28

VOIR PLAN DETAIL DE L'ACCES SUD-OUEST
PC2g

Emprise zone Voie Principale
Surface 673m²
Emprise zone Cheminements piétons de la copropriété
ESPACES EXTERIEURS COMMUNS
VOIE VEHICULES IMERMEABLES / POMPIERS
ESPACES VERTS PRIVATISES
PLACES DE STATIONNEMENT ECO VEGETALISEES
P PLACES PRIVATISEES
VOIE PIETON / POMPIER / PISTE CYCLABLE


VUE PC6c

COUPE TYPE RESEAUX

VOIE ECHELLE
PIETON
PISTE CYCLABLE
3,00

LOTISSEMENT

LOTISSEMENT

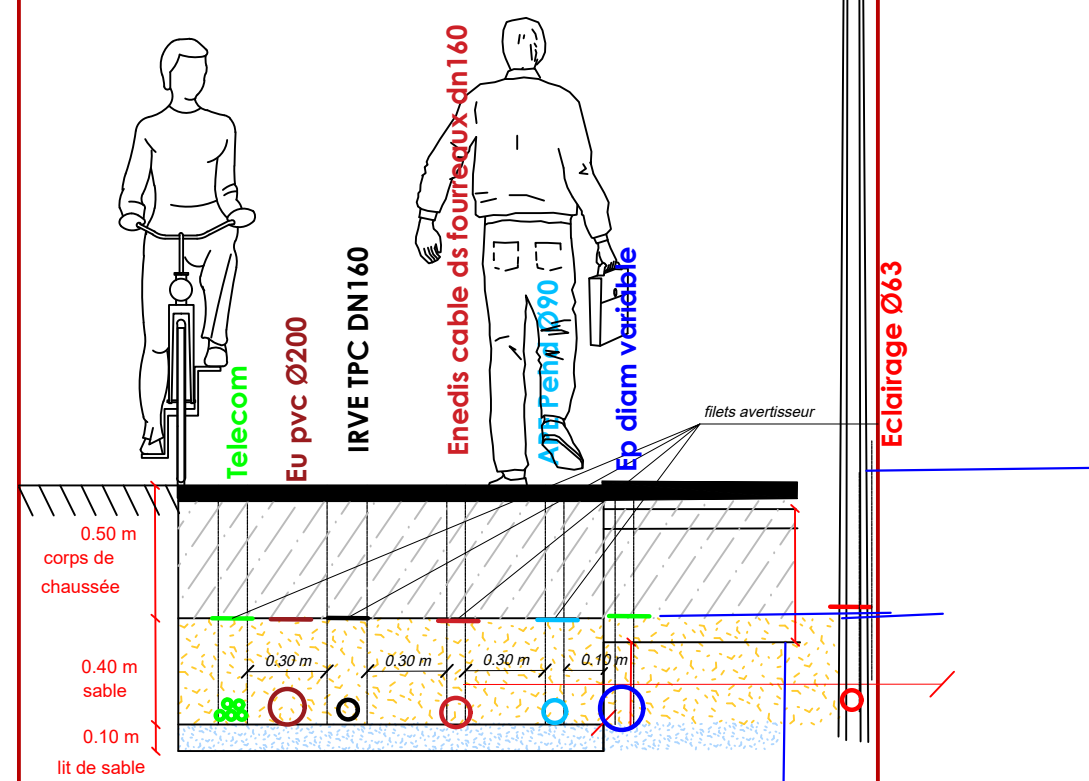

EMPRISE
VOIE PRINCIPALE

VILLE D AUREILLE

Création ensemble Immobilier de
18 villas individuelles rue Neuve Grande Terre

DOSSIER DE CONSULTATION
DES ENTREPRISES

Lot n°- VRD

MAITRE D'OUVRAGE SCCV GRANDE TERRE		837BIS ALLEE DE PARIS 83500 LA SEYNE SUR MER	
ARCHITECTE CHAUVET VERNET			
BE STRUCTURES			
BUREAU DE CONTROLE			
BE VRD BET TPING		51 chemin de la Cadiere 69700 BEAUVALLON	
BE FLUIDES			

I					
H					
G					
F					
E					
D					
C					
B					
A					
0	13/05/26	Création	GT	SB	SB
IND.	DATE	MODIFICATIONS	DESSIN	VERIF	APPROB

Lot VRD		VRD 04 Plan emprise voie principale et coupes reseaux		DATE 13/05/26	PHASE DCE
1/200					
IND	DATE	MODIFICATIONS	DESSIN	VERIF	APPROB

AFFAIRE 20250456	PLAN	TYPE DE FICHIER	AUTEUR GT	IND 0	ECHELLE 1/200
---------------------	------	-----------------	--------------	----------	------------------