


EAU POTABLE

- Canalisation principale fonte
- Canalisation de branchement PEHD
- Canalisation de branchement apres compteur PEHD
- Fosse de comptage collectif
- Alvéole de comptage individuel dans mur technique
- A Coffret de comptage arrosage
- P Regard de programmation arrosage
- G Départ de goutte-à-goutte
- E Enveloppe pour alvéole de comptage individuel à fournir au Lot Gros Oeuvre
- V Ventouse automatique
- bouche a clé
- PI Poteau incendie 60m3/H
- VI Vidange dans EP
- Canalisation arrosage pehd Øvariable

ID-OUEST

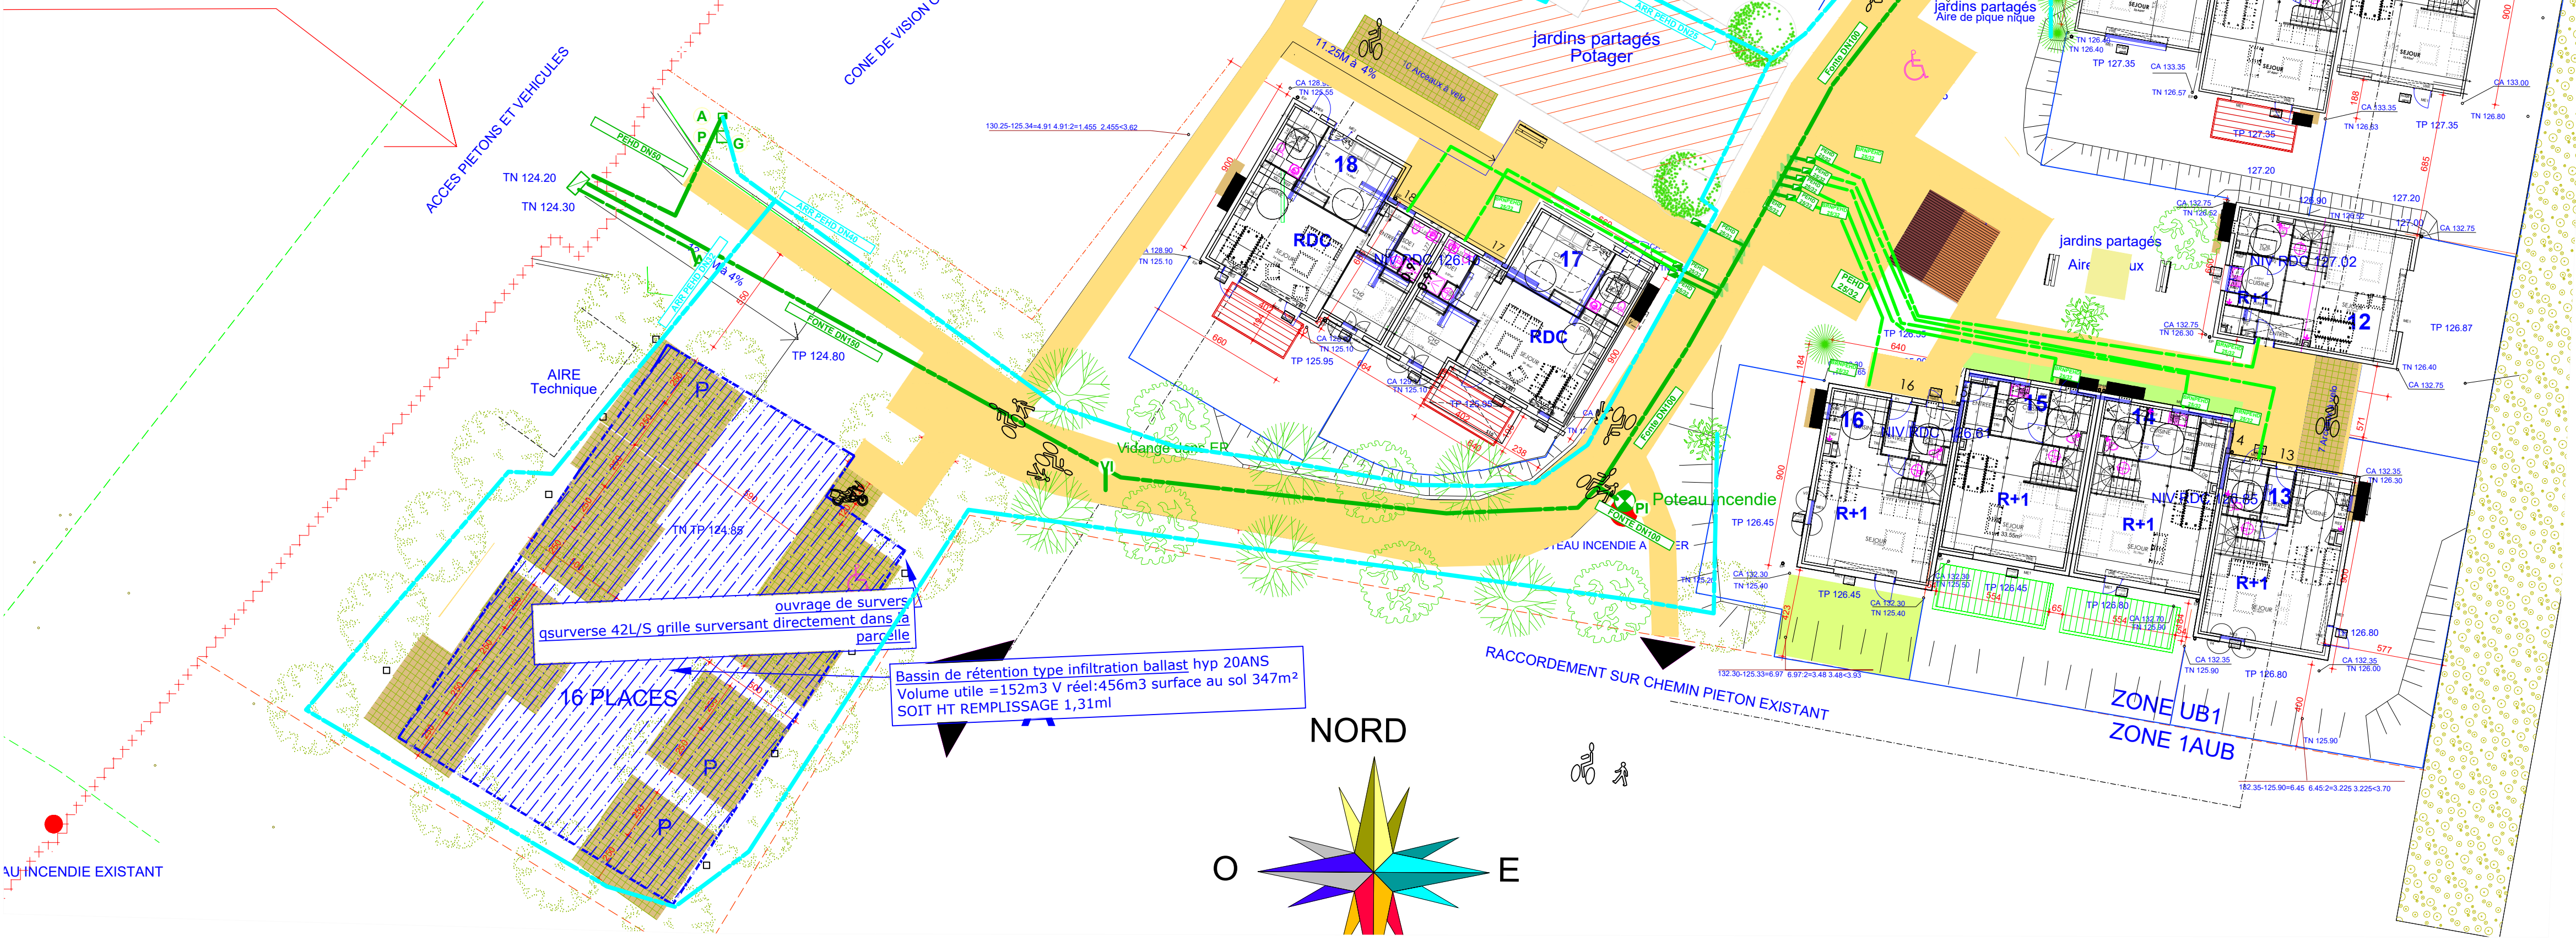

VILLE D AUREILLE
Création ensemble Immobilier de
18 villas individuelles rue Neuve Grande Terre
DOSSIER DE CONSULTATION
DES ENTREPRISES

Lot n° - VRD

MAITRE D'OUVRAGE	837BIS ALLEE DE PARIS 83500 LA SEYNE SUR MER
ARCHITECTE	
CHAUVET VERNET	
BE STRUCTURES	
BUREAU DE CONTROLE	
BET TPING	51 chemin de la Cadiere 68700 BEAUVALLON
BE FLUIDES	

25/05/26	MAJ AVEC ARROSAGE	GT	SB	SB
15/05/26	Création	GT	SB	SB
DATE	MODIFICATIONS	DESSIN	VERIF	APPROB
1/200				

Lot VRD VRD07 PLAN DES RESEAUX PRESSIONS				DATE	PHASE
				25/05/26	DCE
AFFAIRE	PLAN	TYPE DE FICHIER	AUTEUR	IND	ECHELLE
				A	1/200