


- ESPACES EXTERIEURS COMMUNS
- VOIE VEHICULES IMPERMEABLES / POMPIERS TYPE ENROBES
- ESPACES VERTS PRIVATISES
- PLACES DE STATIONNEMENT ECO VEGETALISEES
P PLACES PRIVATISEES
- CHEMINEMENT DOUX / POMPIER TYPE STABILISE
- CLOTURE H= 1.40m à MAILLES 15X15cm

VOIRIE

- Muret soutènement
- Bordure T2
- Bordure acier ou plastiques
- Bordure P1

XX.XX *
Cote de niveau terrain existant conservé
XX.XX
Cote de niveau terrain aménagé

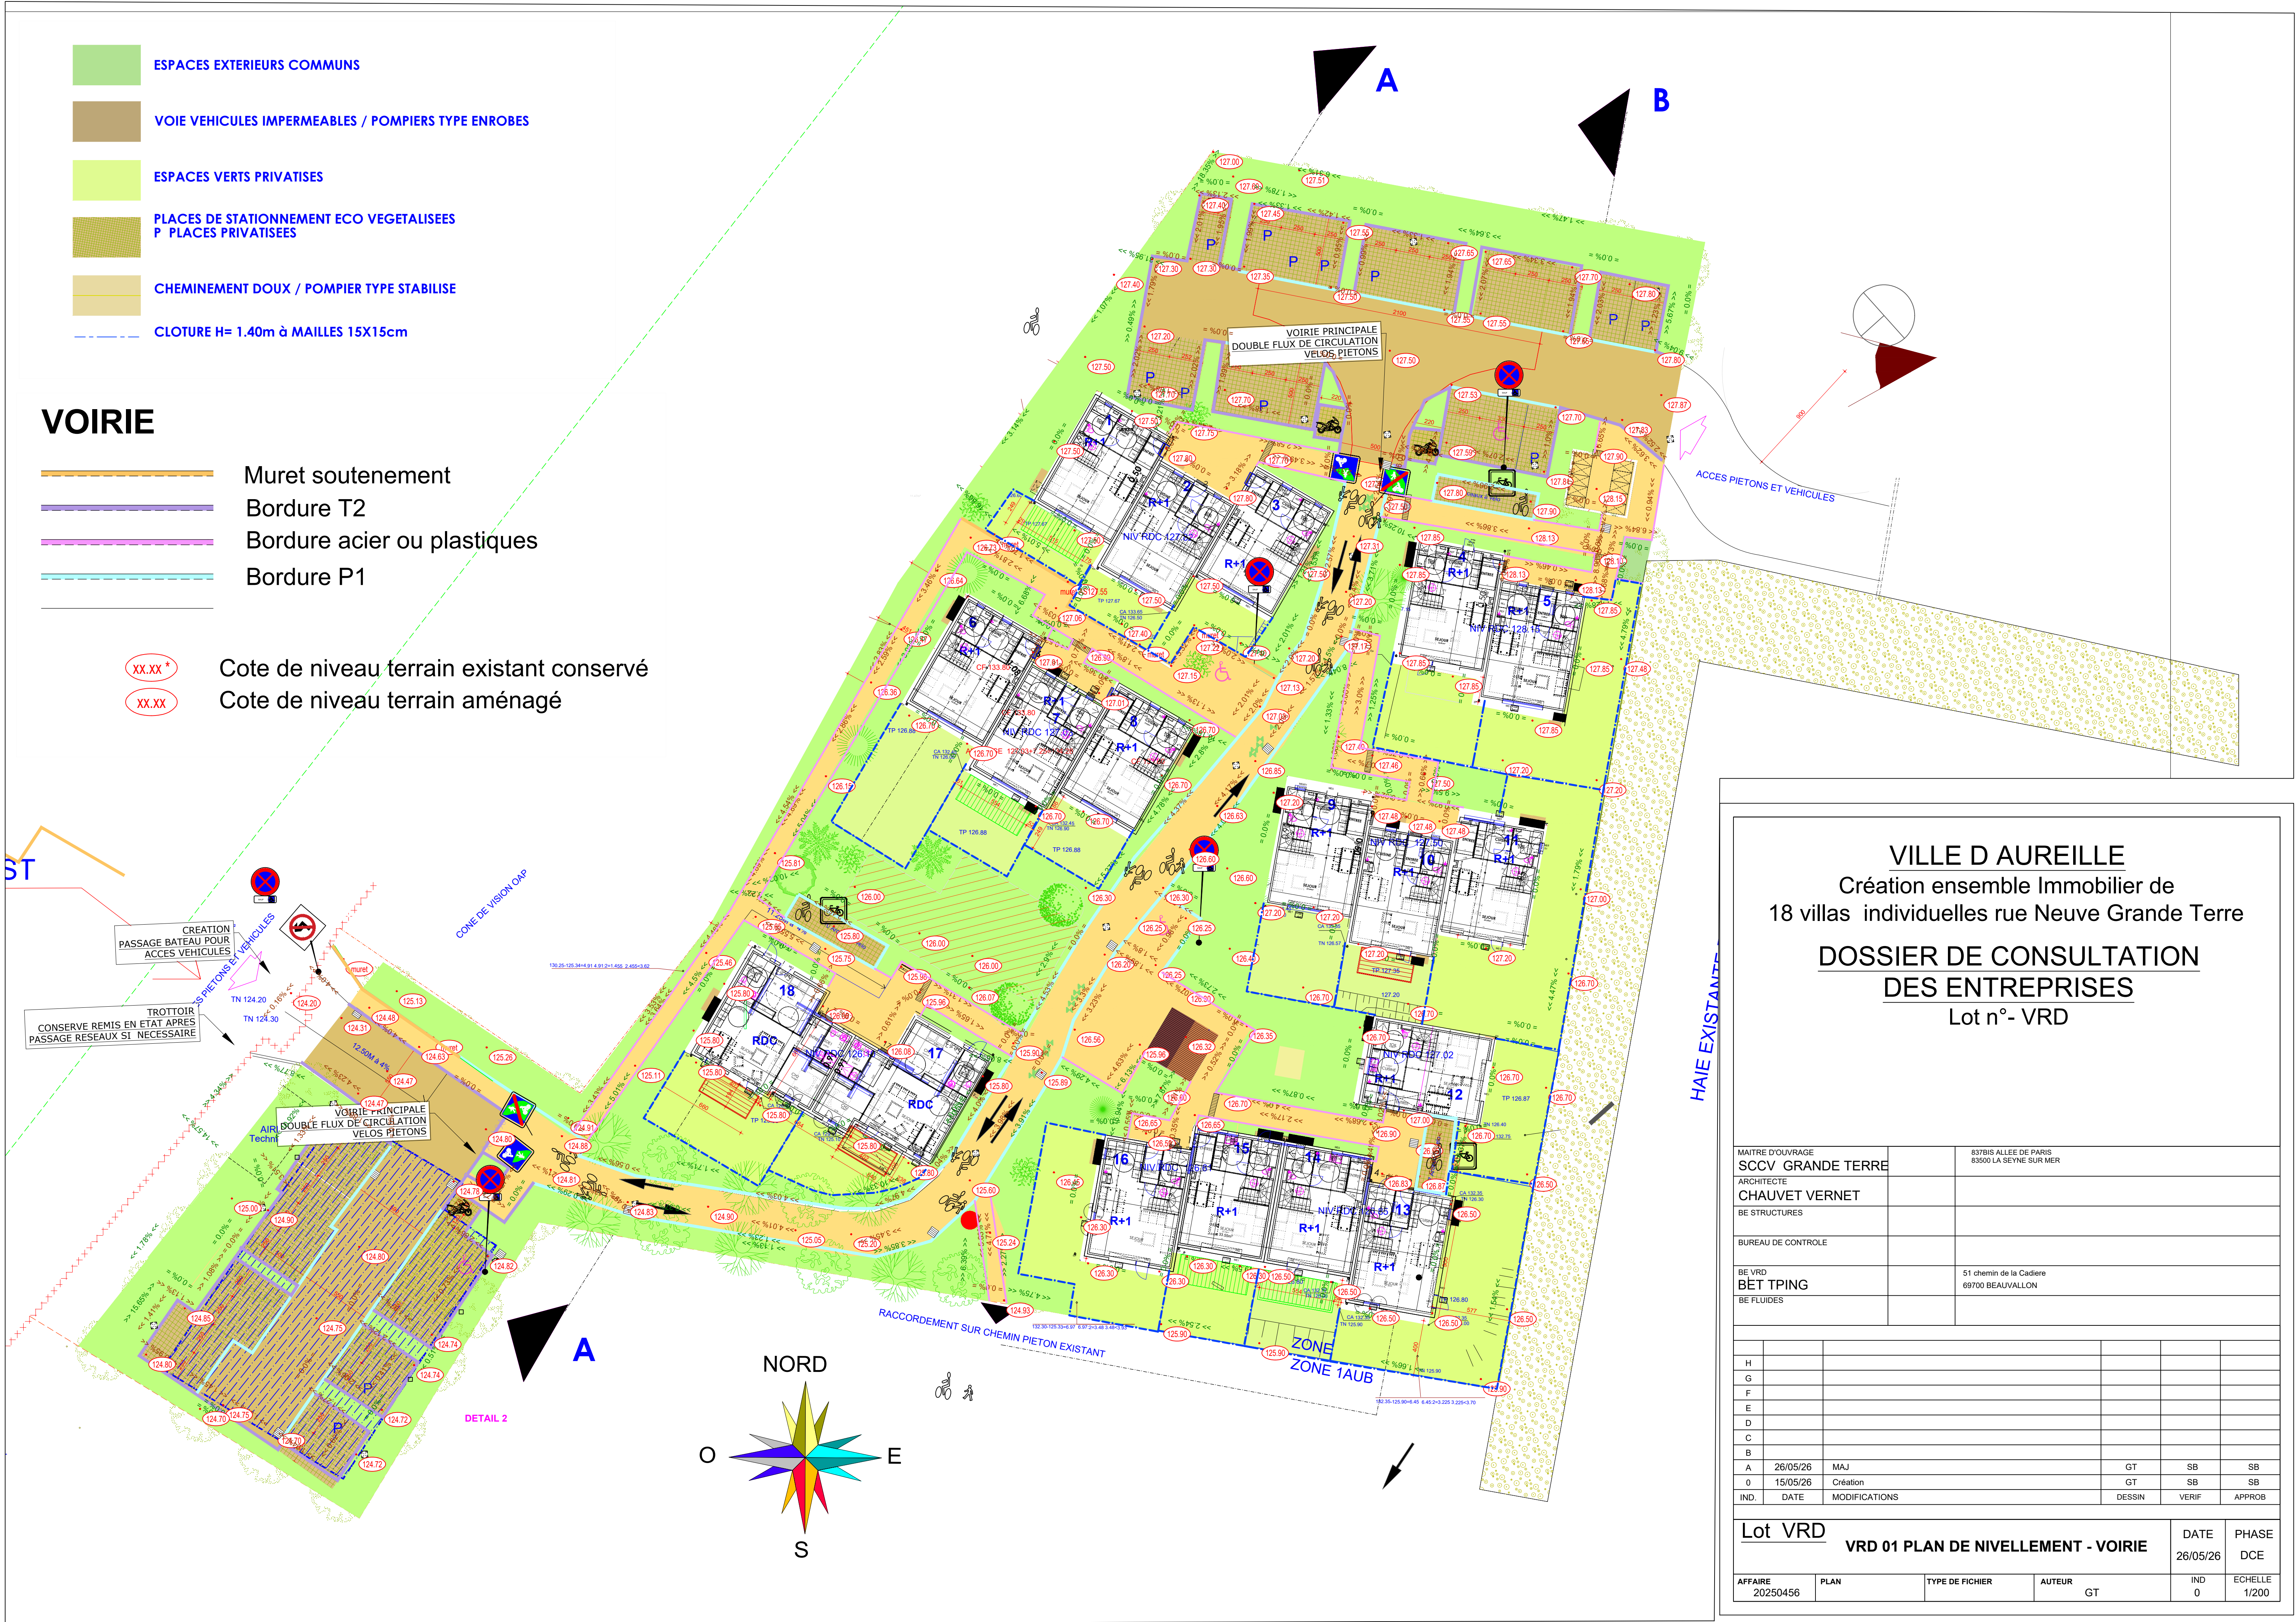

VILLE D AUREILLE
Création ensemble Immobilier de
18 villas individuelles rue Neuve Grande Terre
DOSSIER DE CONSULTATION
DES ENTREPRISES
Lot n°- VRD

MAITRE D'OUVRAGE SCCV GRANDE TERRE		83701S ALLEE DE PARIS 83500 LA SEYNE SUR MER			
ARCHITECTE CHAUVET VERNET					
BE STRUCTURES					
BUREAU DE CONTROLE					
BE VRD BET TPING		51 chemin de la Cadriere 69700 BEAUVALLON			
BE FLUIDES					
H					
G					
F					
E					
D					
C					
B					
A	26/05/26	MAJ	GT	SB	SB
O	15/05/26	Création	GT	SB	SB
IND.	DATE	MODIFICATIONS	DESSIN	VERIF	APPROB
Lot VRD			VRD 01 PLAN DE NIVELLEMENT - VOIRIE		DATE 26/05/26
					PHASE DCE
AFFAIRE 20250456		PLAN	TYPE DE FICHIER	AUTEUR GT	IND 0
					ECHELLE 1/200