


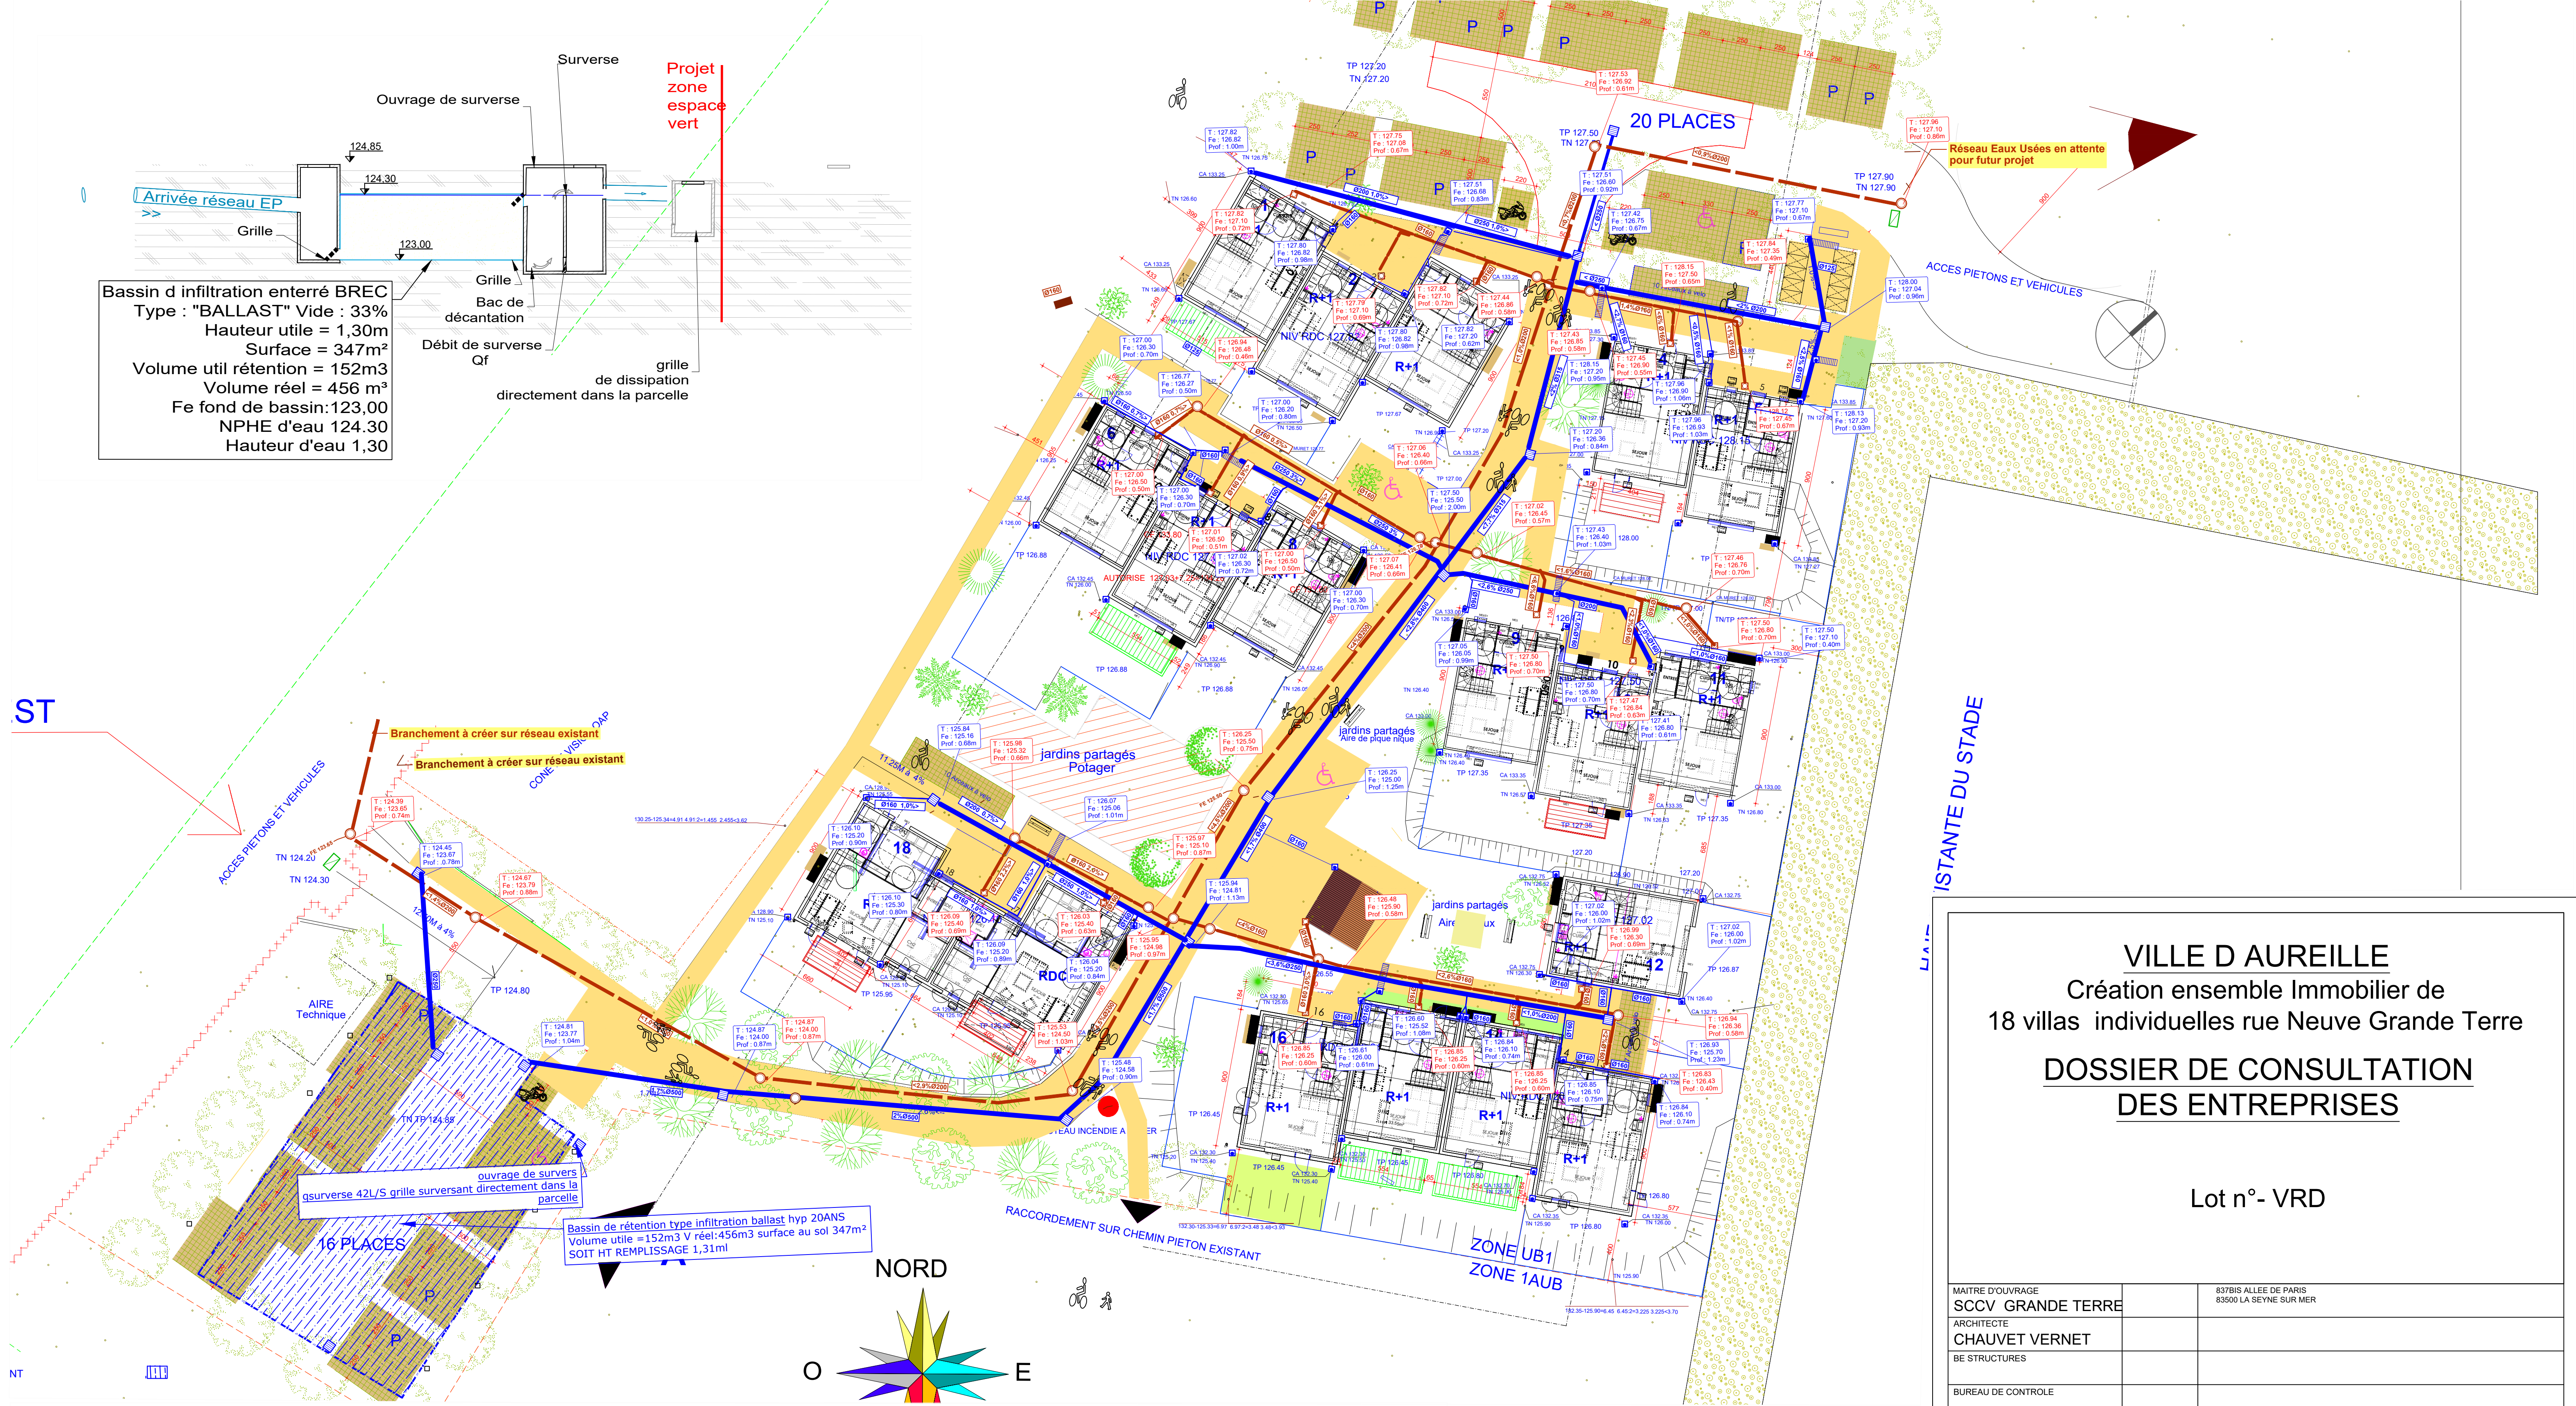

VILLE D AUREILLE  
Création ensemble Immobilier de  
18 villas individuelles rue Neuve Grande Terre  
DOSSIER DE CONSULTATION  
DES ENTREPRISES

Lot n° - VRD

|                    |                                                 |
|--------------------|-------------------------------------------------|
| MAÎTRE D'OUVRAGE   | 837BIS ALLÉE DE PARIS<br>83500 LA SEYNE SUR MER |
| ARCHITECTE         |                                                 |
| CHAUVET VERNET     |                                                 |
| BE STRUCTURES      |                                                 |
| BUREAU DE CONTRÔLE |                                                 |
| BET TPING          | 51 chemin de la Cadière<br>69700 BEAUVALLON     |
| BE FLUIDES         |                                                 |

EAUX PLUVIALES

- Canalisation PVC CR16 (section-pente x mm/m)
- Caniveau L300 P350/440 (raccordement Ø315 PVC)
- Caniveau L200 P240
- Regard de visite
- Regard à grille (raccordement Ø250 PVC)
- Regard à double grille
- Regard à grille 50x50
- Regard de branchement drain 50x50 (raccordement Ø250 PVC)
- Regard de pied de chute 30x30 avec tampon prédécoupé (racc.Ø160 PVC)
- Tabouret de branchement DN250 (raccordement Ø160 PVC)
- Regard de branchement 30x30 (raccordement Ø160 PVC)
- Bassin infiltration sous parking

EAUX USEES

- Canalisation PVC CR16 Ø200 (pente x mm/m)
- Canalisation PVC CR16 Ø160
- Regard de visite DN1000 TAMPON 400KN REXEL
- Tabouret de branchement DN315
- Tabouret de branchement DN250

|                                                                         |      |                 |        |          |         |
|-------------------------------------------------------------------------|------|-----------------|--------|----------|---------|
| <div>Lot VRD</div> <div>VRD02</div> <div>PLAN DES RESEAUX HUMIDES</div> |      |                 |        | DATE     | PHASE   |
|                                                                         |      |                 |        | 15/05/26 | DCE     |
| AFFAIRE                                                                 | PLAN | TYPE DE FICHIER | AUTEUR | IND      | ECHELLE |
|                                                                         |      |                 |        | 0        | 1/200   |