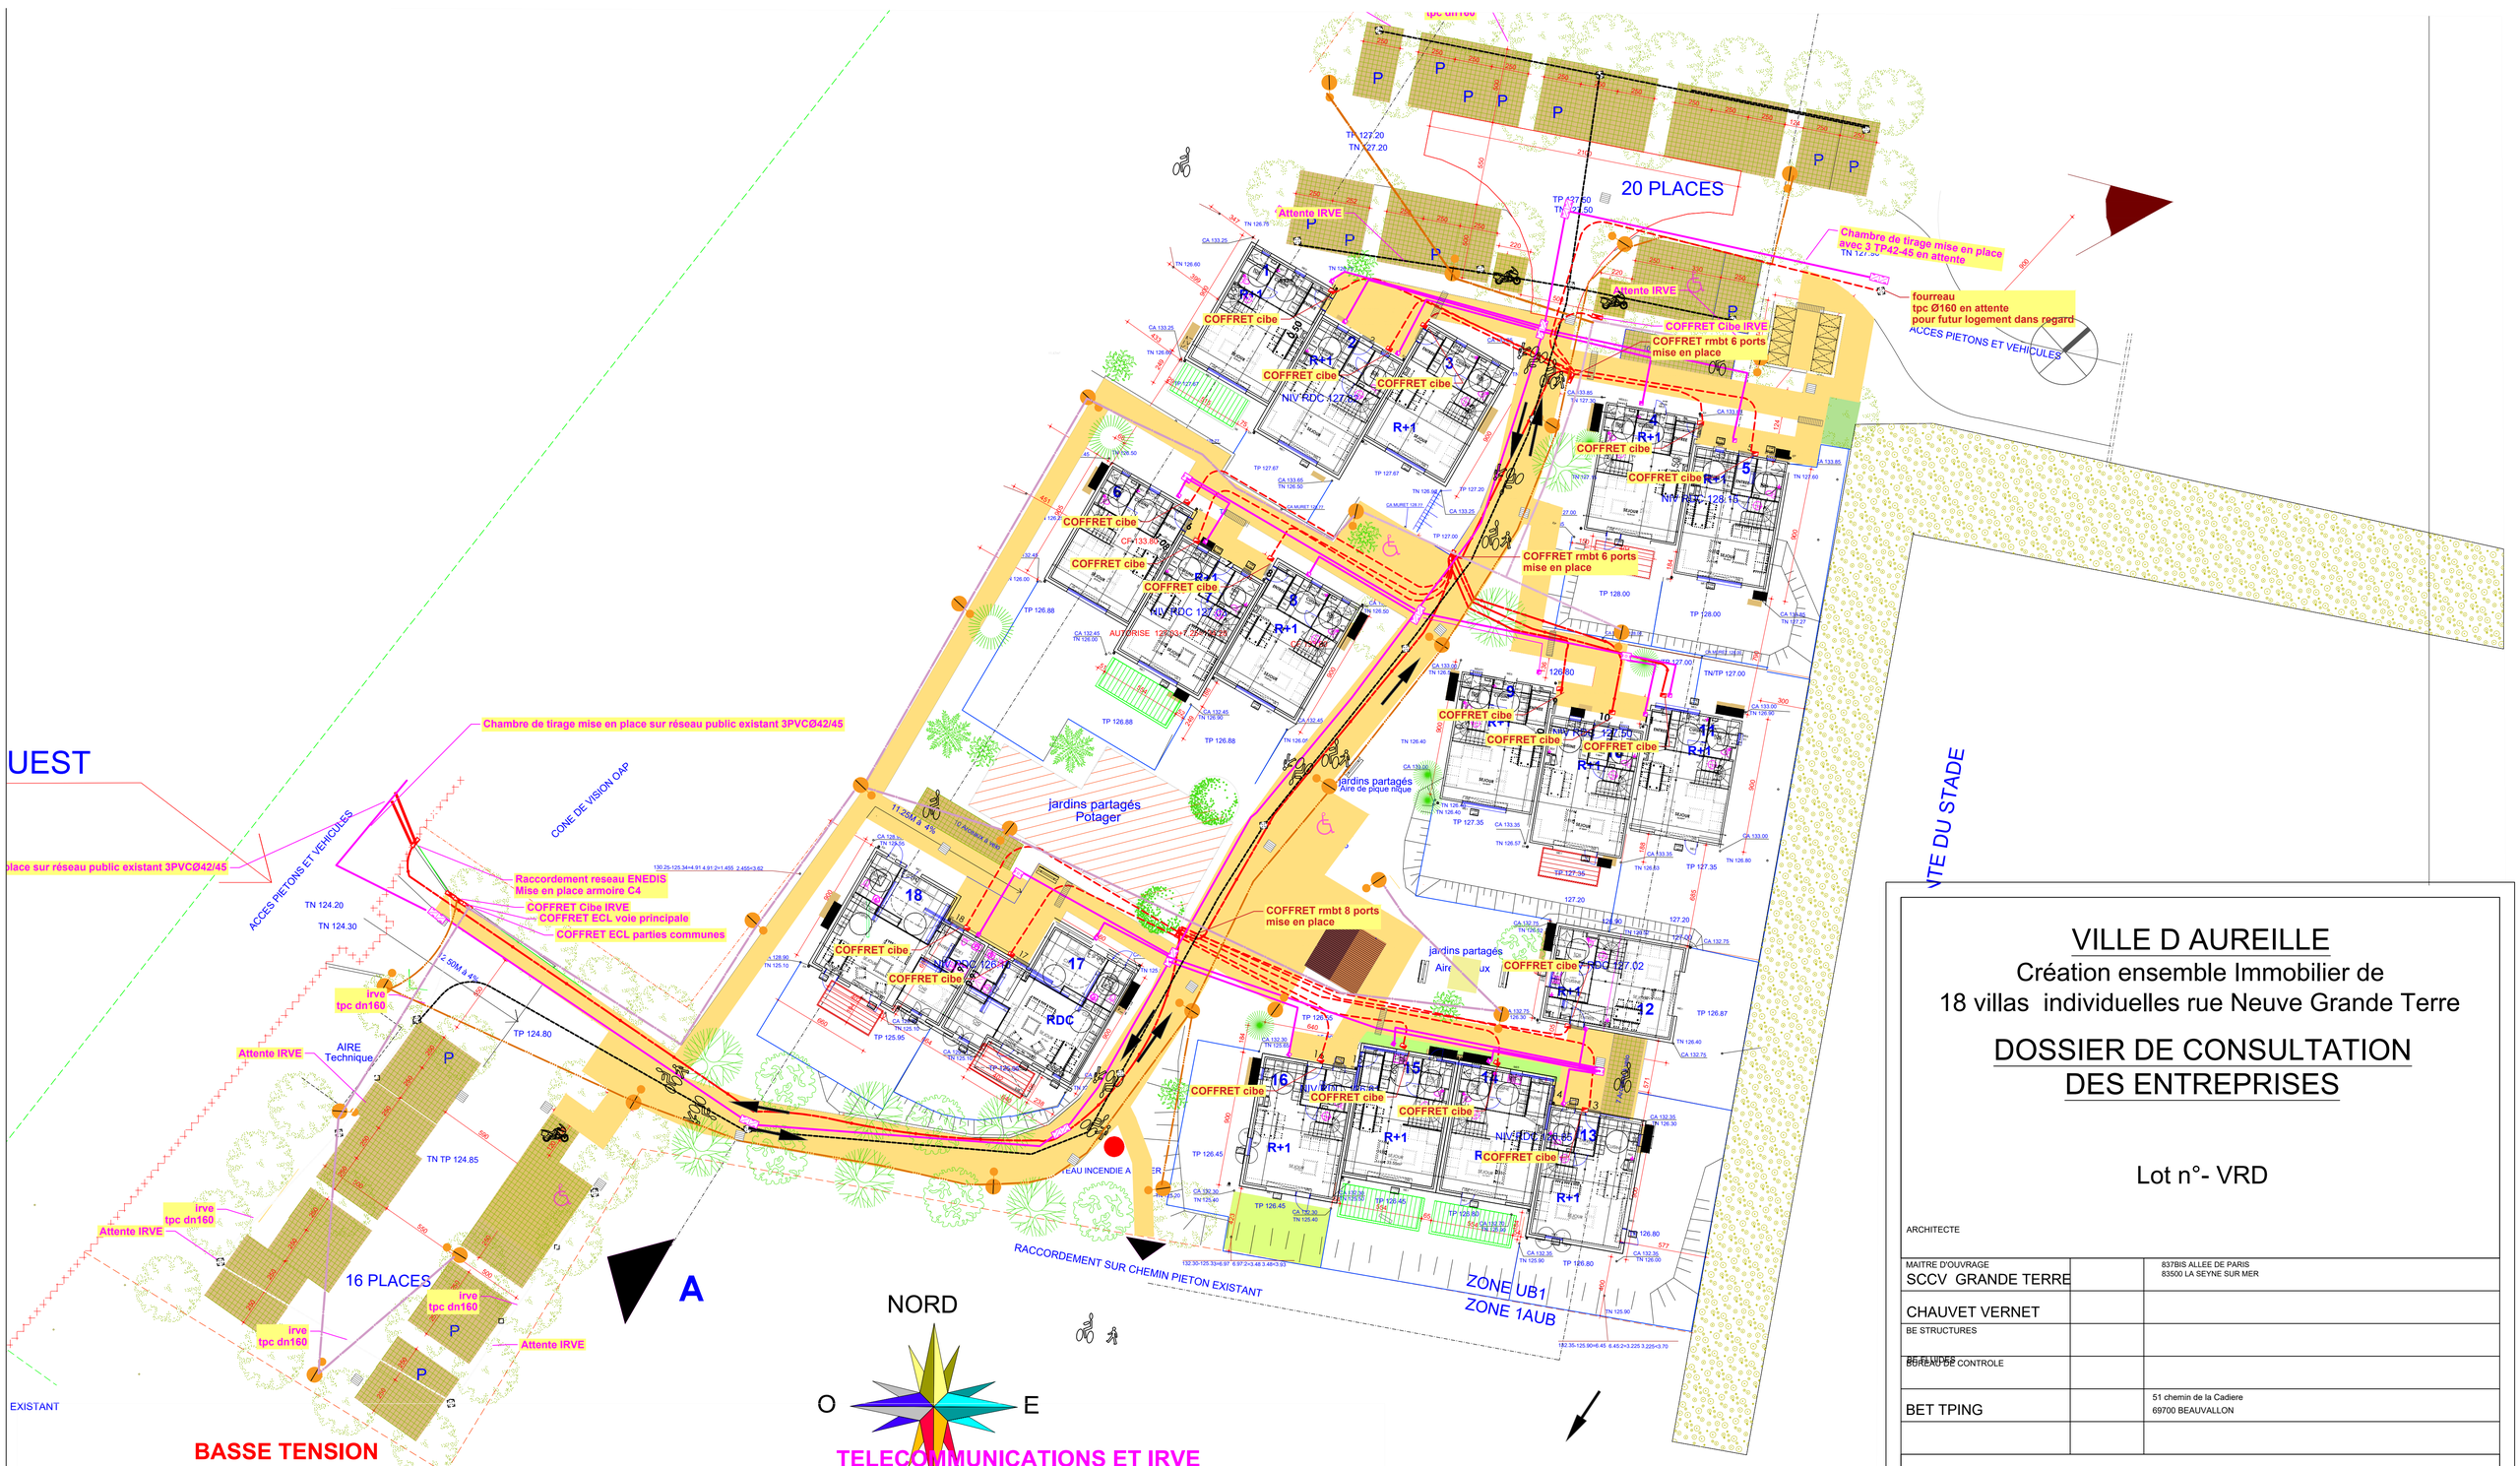


BASSE TENSION

- Câble de réseau
- Câble de branchement 4x35mm² sous fourreau TPCØ75
- Coffret REMBT
- Coffret C400/P200
- Coffret de comptage individuel

ECLAIRAGE

- Câble U1000R2V sous fourreau TPCØ75 partie voies principale
- Infrastructure 1 x fourreau TPCØ63 parties communes
- Luminaire
- Regard de tirage 40x40
- P — Entourage pour protection candélabre

TELECOMMUNICATIONS ET IRVE

- Infrastructure réseau 3 x fourreaux PVCØ42/45 (distribution générale + raccordements répartiteurs dans murs techniques)
- Infrastructure branchement 2 x fourreaux PVCØ25/28
- Chambre de tirage type L2C
- Chambre de tirage type L1T
- Coffret d'adduction individuel
- Regard 30x30 IRVE
- Infrastructure IRVE atttente GC 1dn160 en tpc
- R — Répartiteur dans coffret mur technique

VILLE D AUREILLE

Création ensemble Immobilier de 18 villas individuelles rue Neuve Grande Terre

DOSSIER DE CONSULTATION DES ENTREPRISES

Lot n°- VRD

ARCHITECTE

MAITRE D'OUVRAGE SCCV GRANDE TERRE		837BIS ALLEE DE PARIS 83500 LA SEYNE SUR MER
CHAUVET VERNET		
BE STRUCTURES		
BE FLUIDES BUREAU DE CONTROLE		
BET TPING		51 chemin de la Cadiere 69700 BEAUVALLON

DATE	MODIFICATIONS	DESSIN	VERIF	APPROB
25/05/26	MAJ CIBE IRVE ET DEPLACEMENT 2 RMBT	GT	SB	SB
15/05/26	Création	GT	SB	SB

AFFAIRE: Lot VRD

VRD03 **PLAN DES RESEAUX SECS**

DATE	PHASE
25/05/26	DCE

PLAN	TYPE DE FICHIER	AUTEUR	IND	ECHELLE
20250456		GT	0	1/250